


JOB PORTFOLIO


-SIMPLY DAS

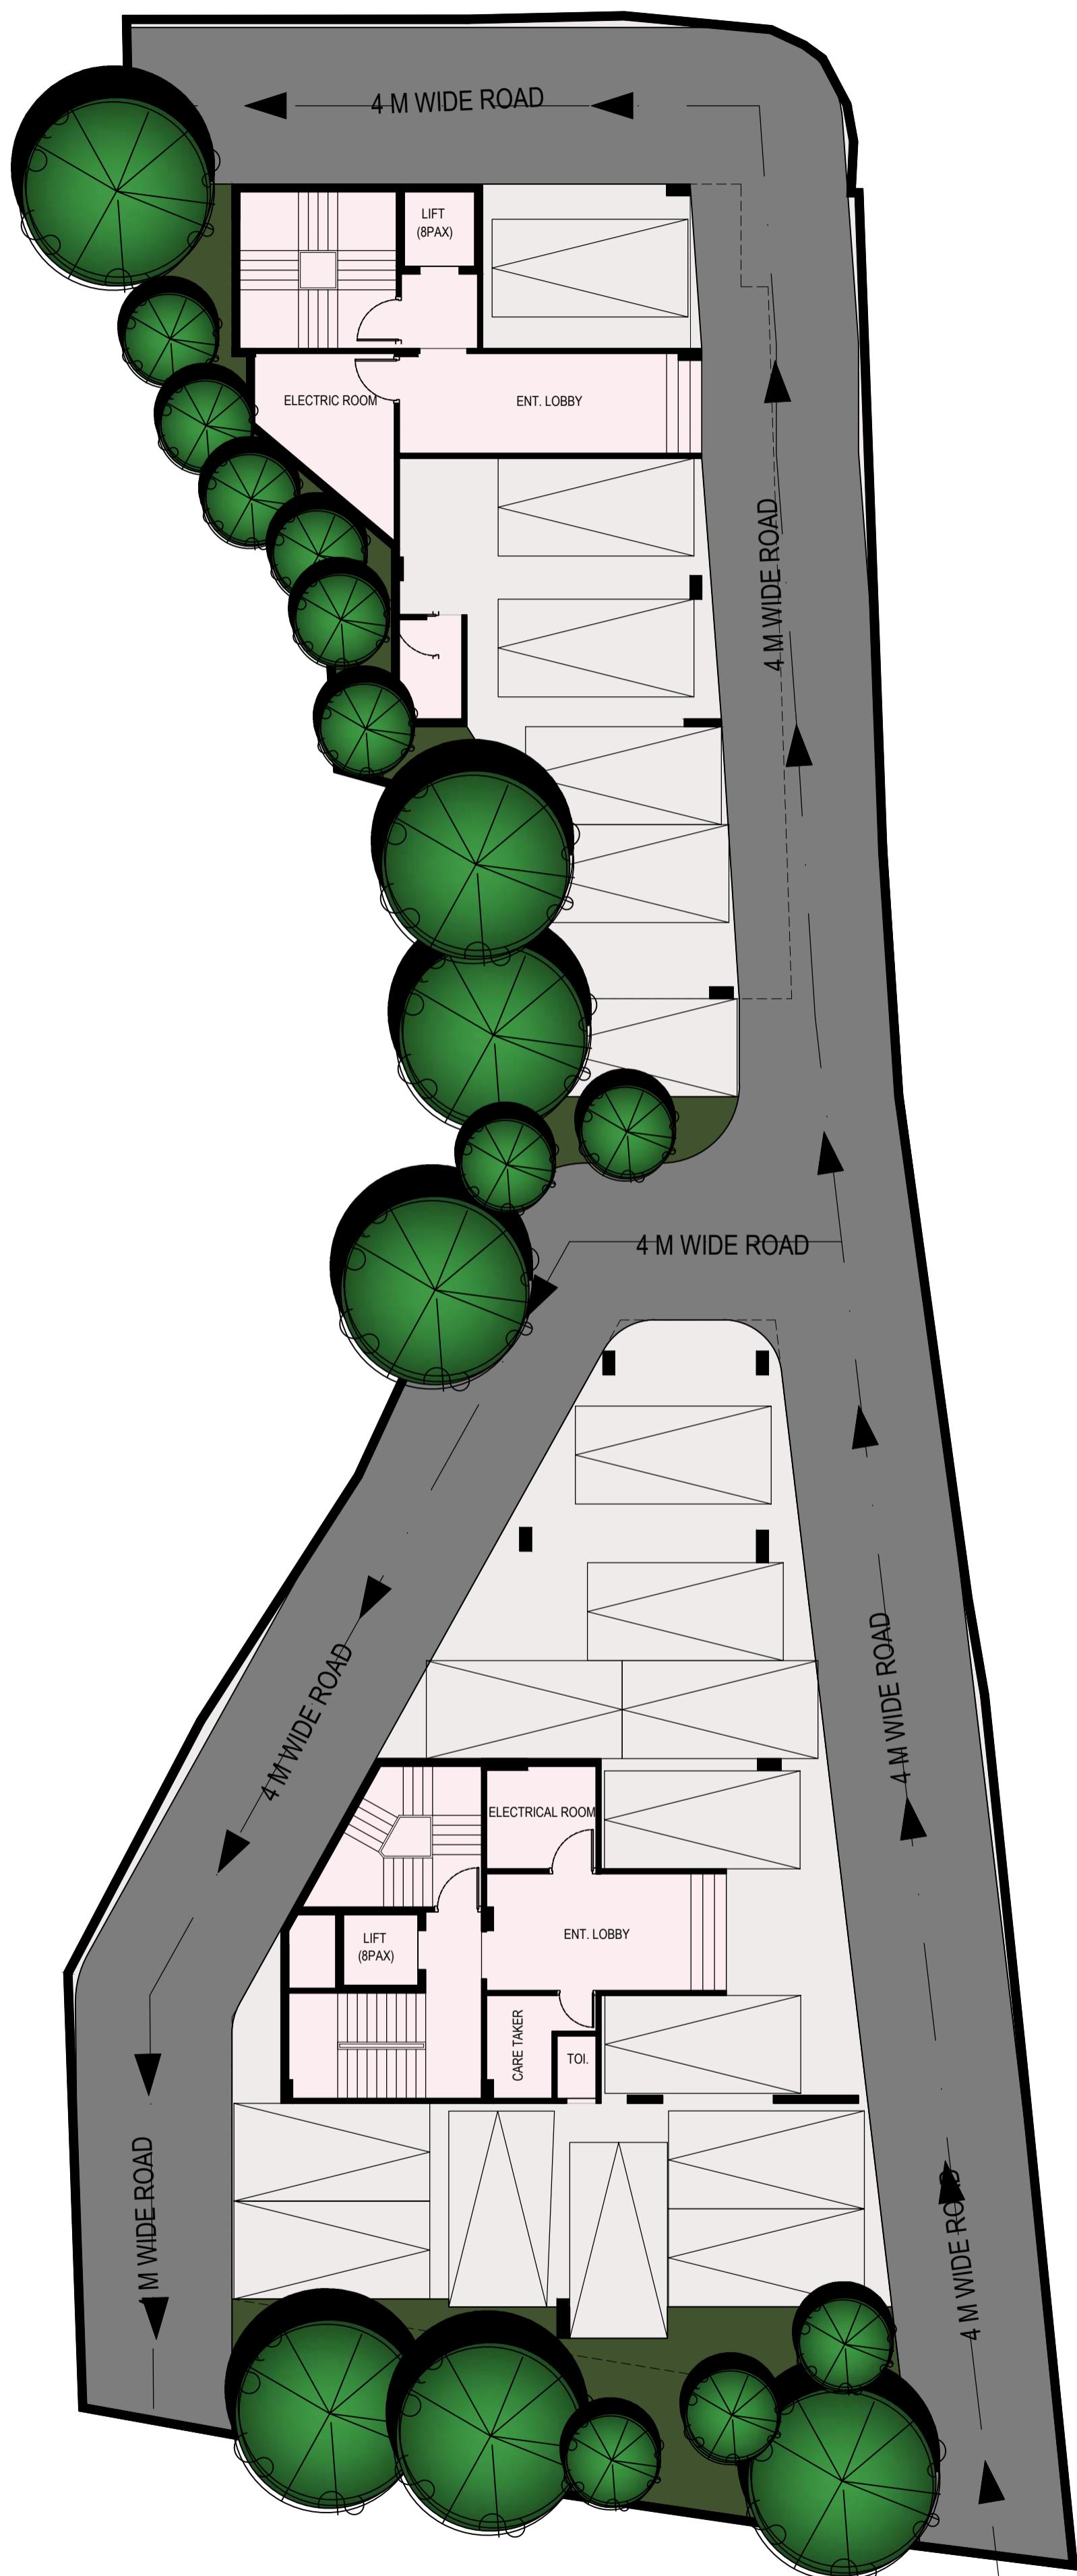

FLOOR PLAN - GROUND FLOOR PLAN
RAJA SANTOSH ROAD PROJECT, NEW- ALIPORE



ARCHITECTS
M
INTERIORS

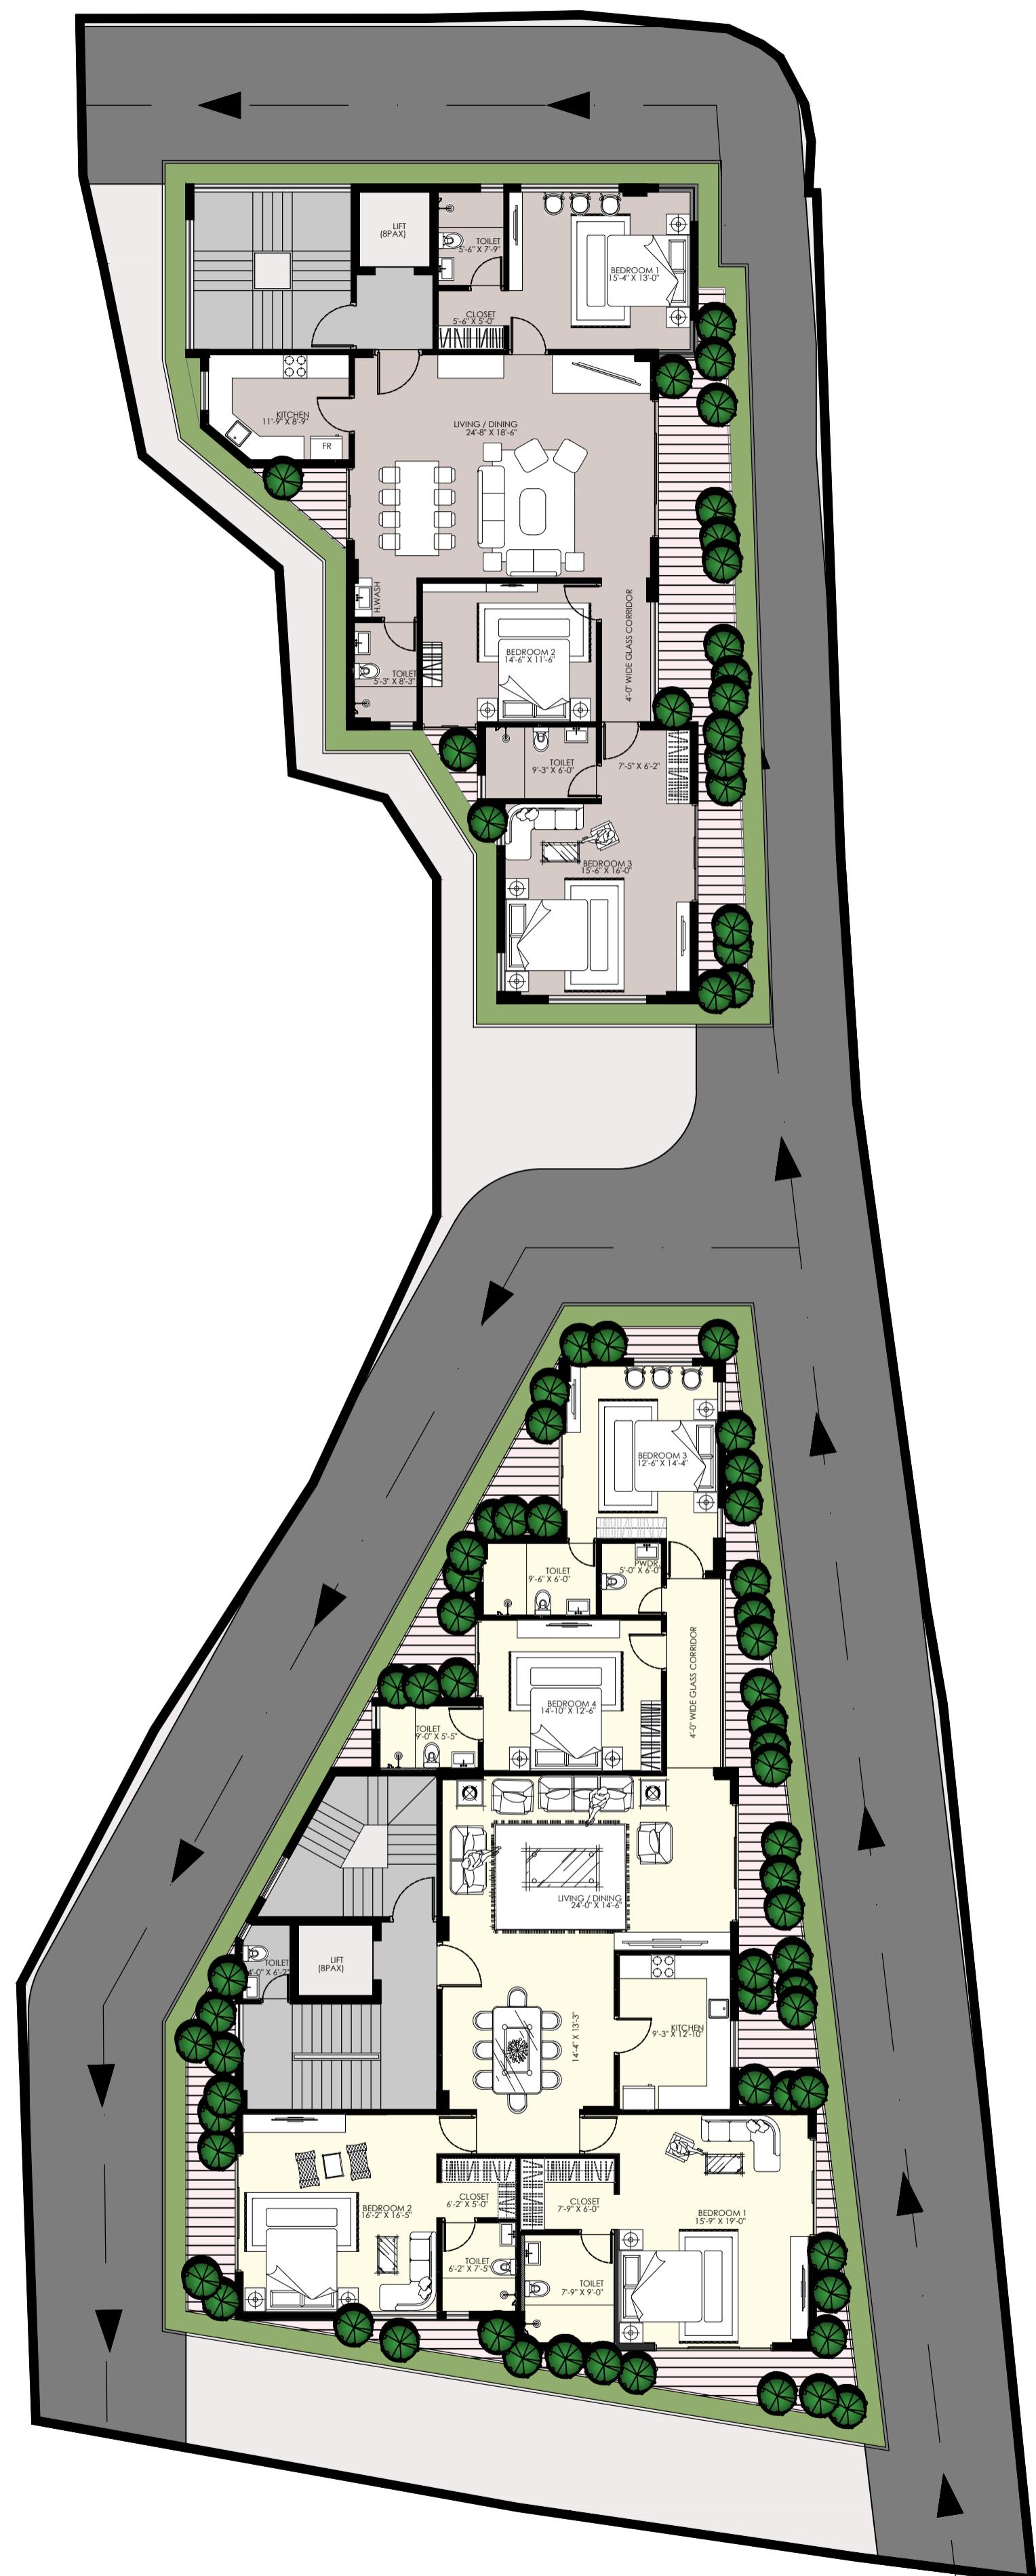


3 BHK TYP. 1-

4 BHK TYP. 1-

FLOOR PLAN - 1ST TO 3RD FLOOR PLAN
RAJA SANTOSH ROAD PROJECT, NEW- ALIPORE




ARCHITECTS
M
INTERIORS

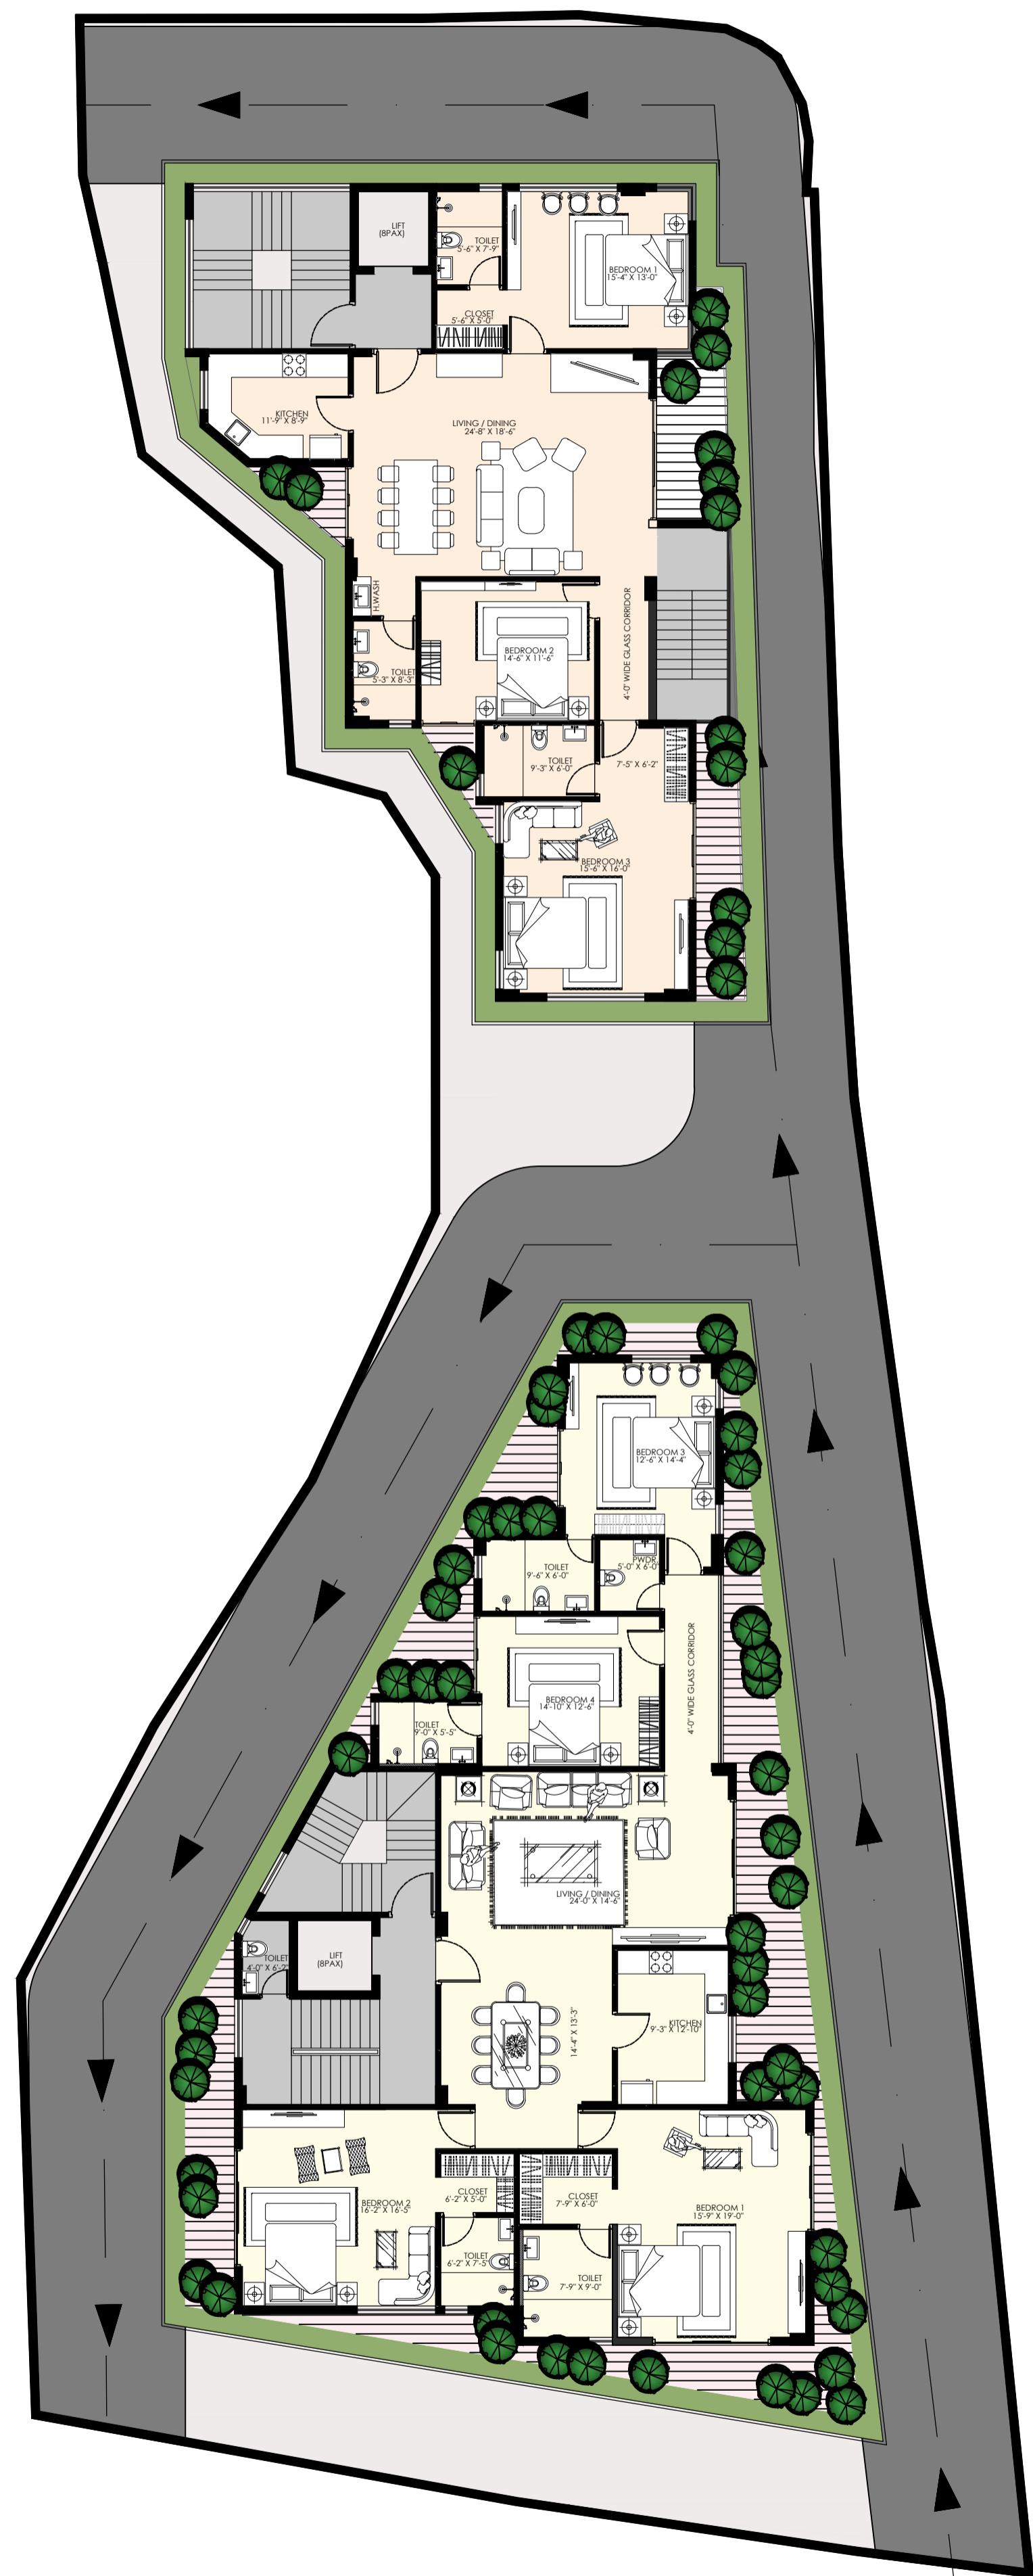


3 BHK DUPLEX-

4 BHK TYP. 1-

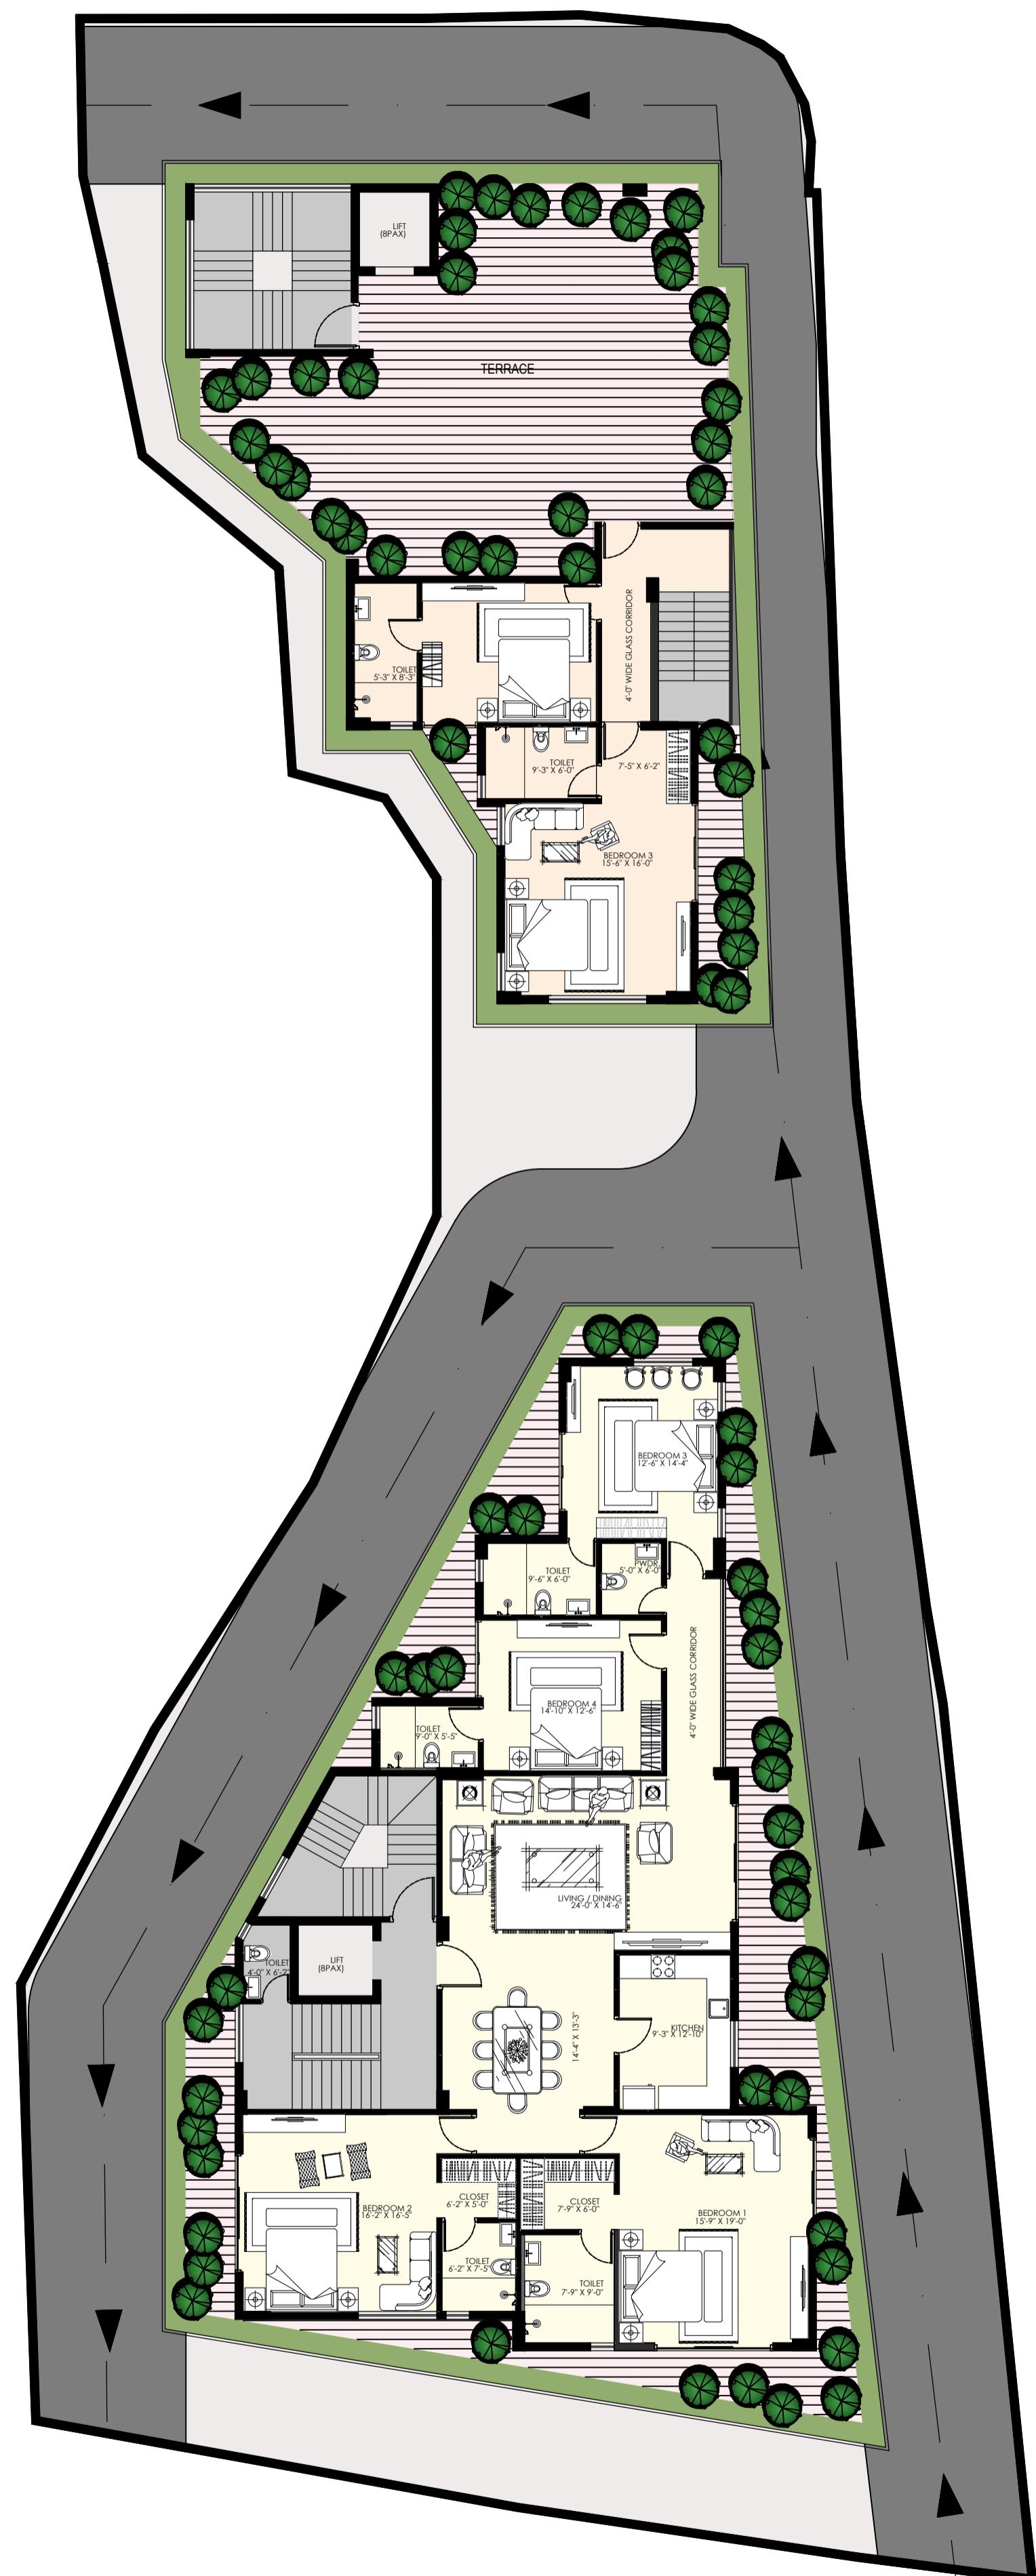

5TH FLOOR PLAN

3 BHK DUPLEX-
4 BHK TYP. 1-

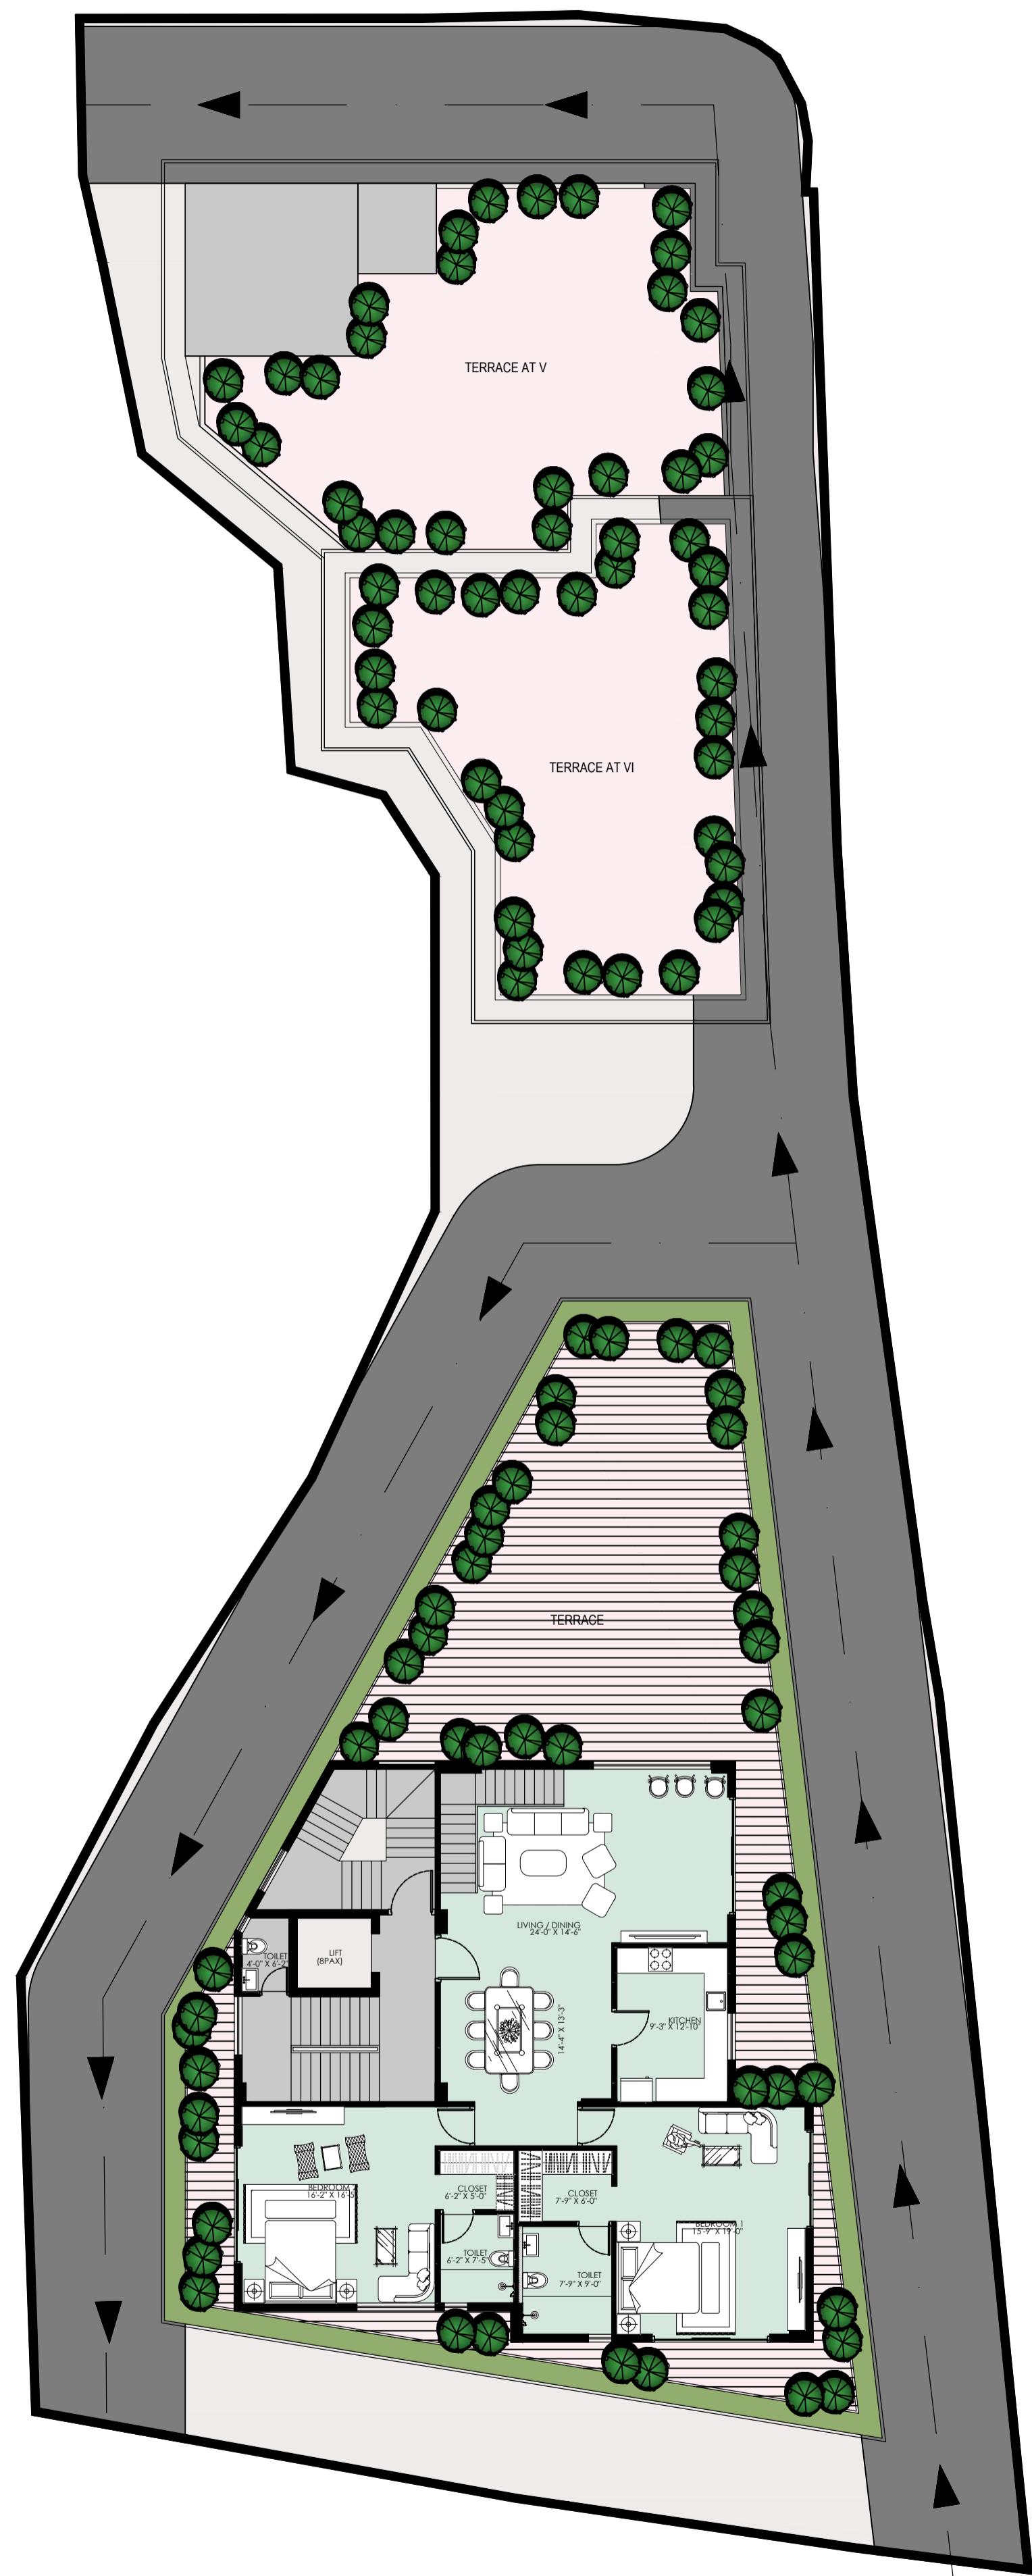


6TH FLOOR PLAN

2 BHK DUPLEX-

FLOOR PLAN - 6TH FLOOR PLAN
RAJA SANTOSH ROAD PROJECT, NEW- ALIPORE



ARCHITECTS
M
INTERIORS

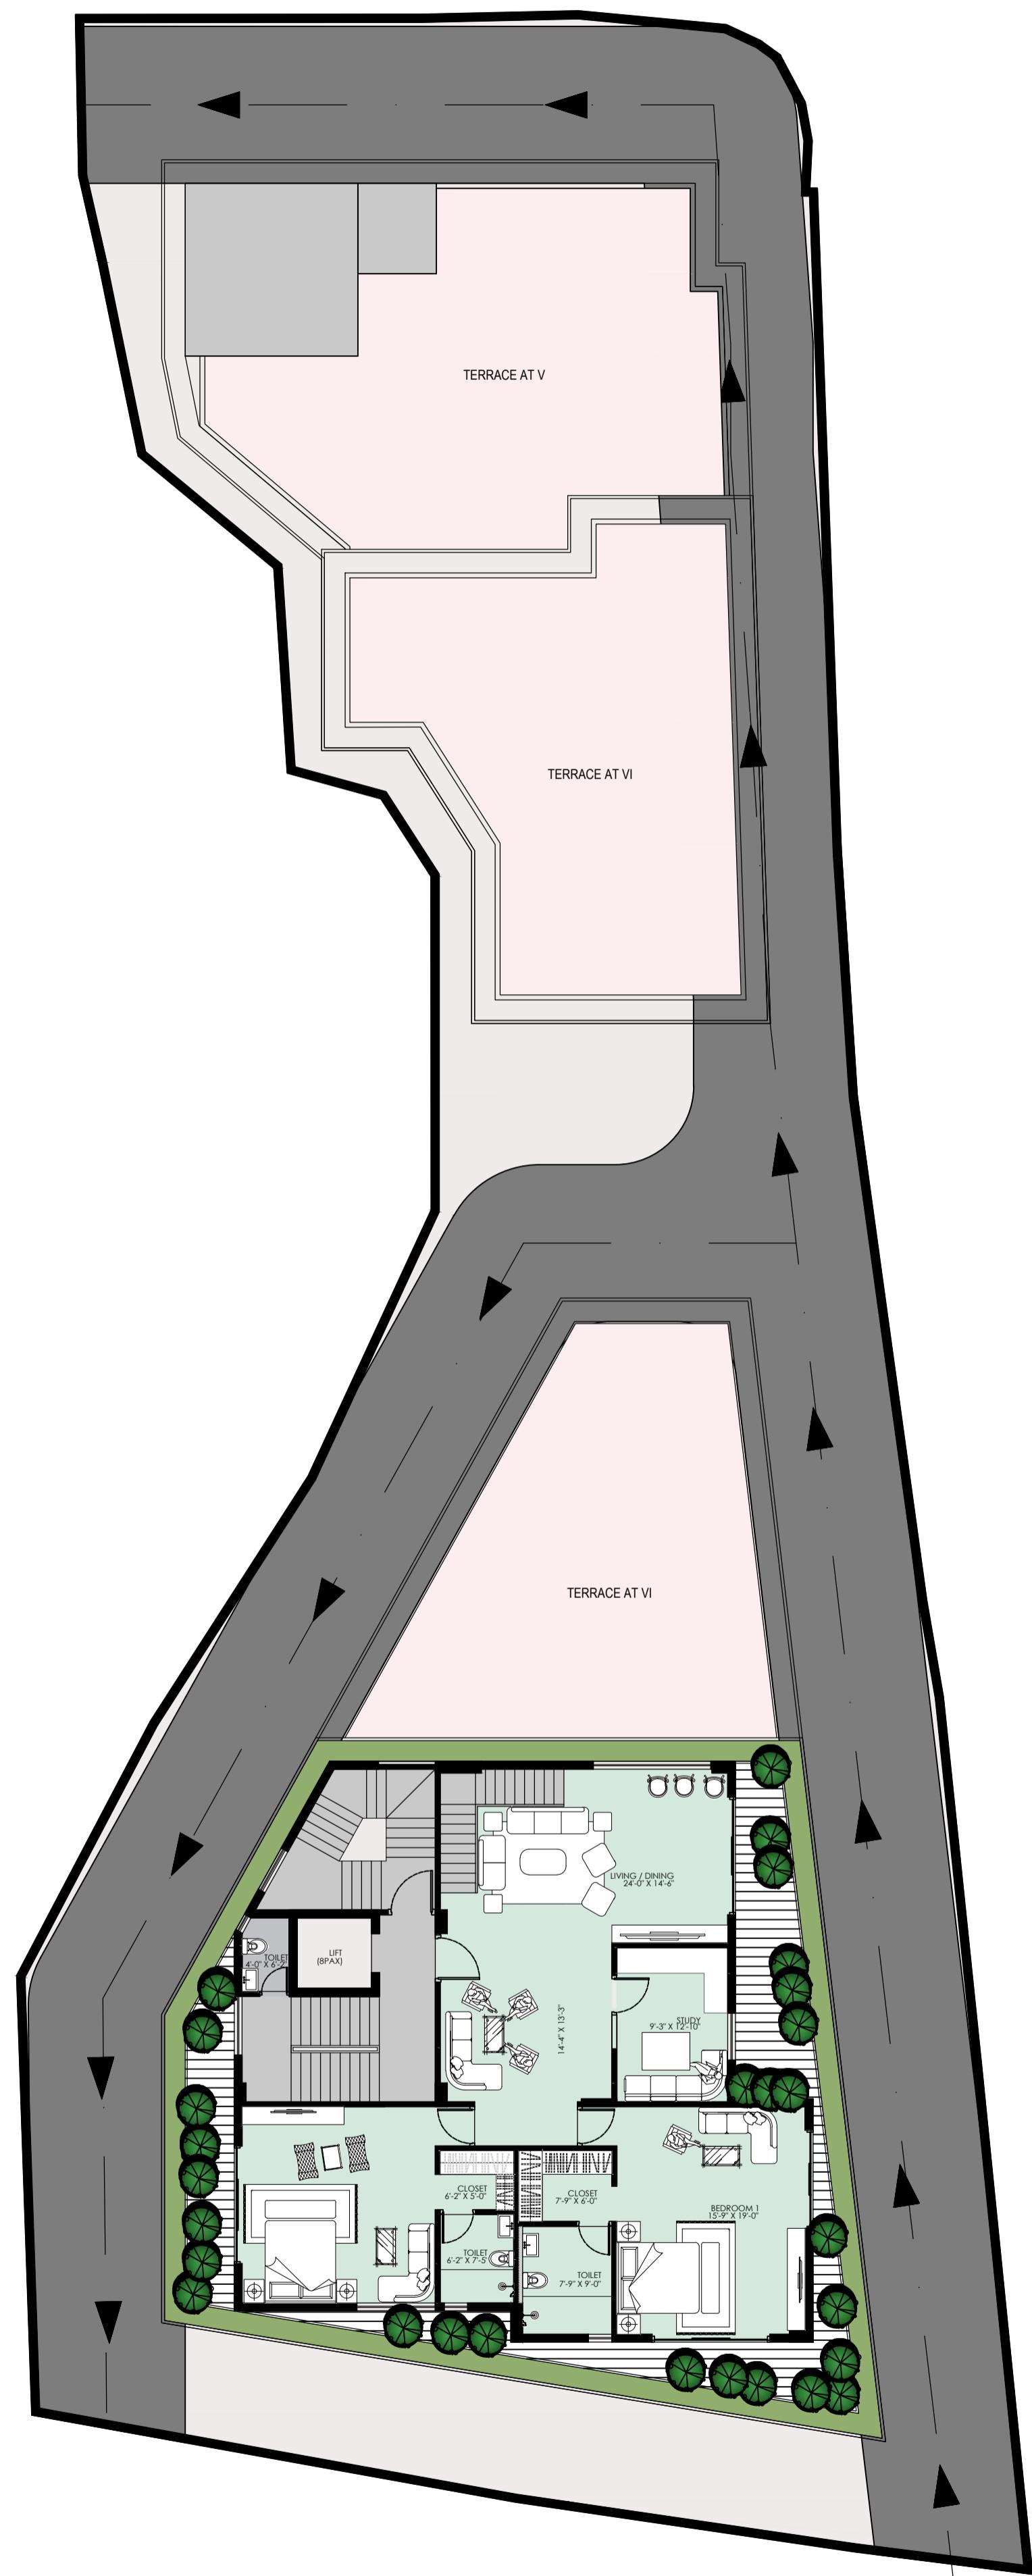

7TH FLOOR PLAN

2 BHK DUPLEX-

FLOOR PLAN - 7TH FLOOR PLAN
RAJA SANTOSH ROAD PROJECT, NEW- ALIPORE



ARCHITECTS
M
INTERIORS

GROUND FLOOR PLAN



PROPOSED COMMERCIAL MALL, GUWAHATI



FIRST FLOOR PLAN



PROPOSED COMMERCIAL MALL, GUWAHATI

SECOND & THIRD FLOOR PLAN



PROPOSED COMMERCIAL MALL, GUWAHATI

FOURTH FLOOR PLAN






PROPOSED COMMERCIAL MALL, GUWAHATI

FIFTH FLOOR PLAN




PROPOSED COMMERCIAL MALL, GUWAHATI

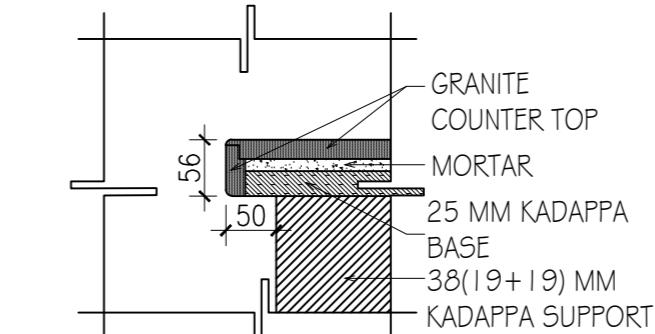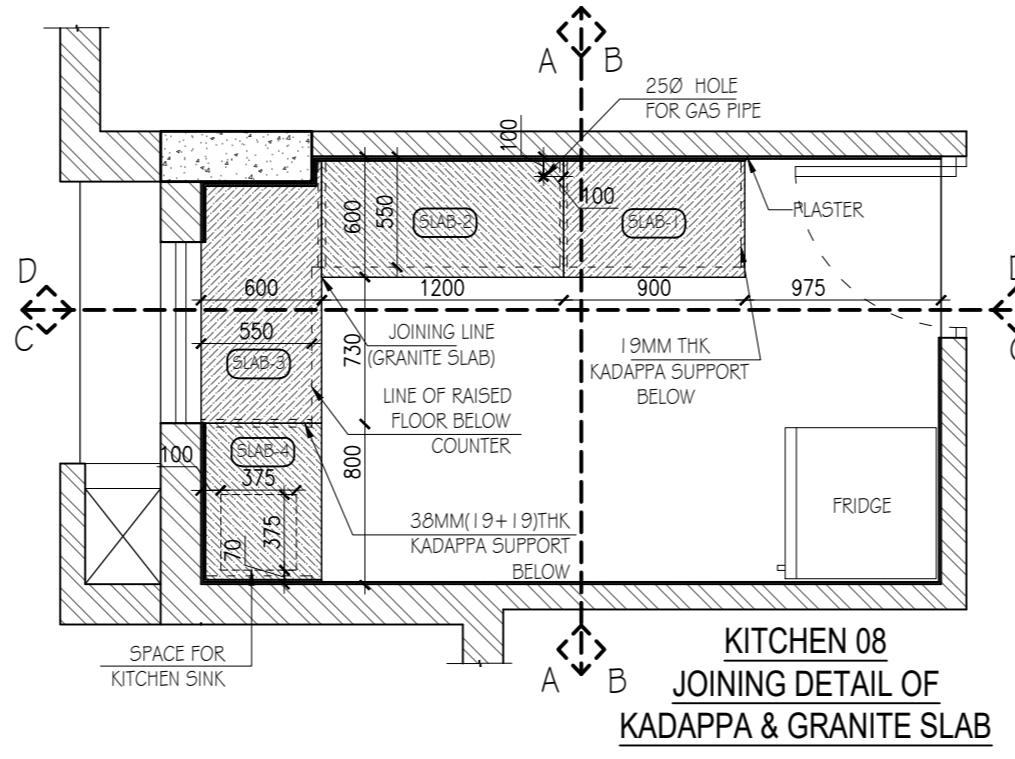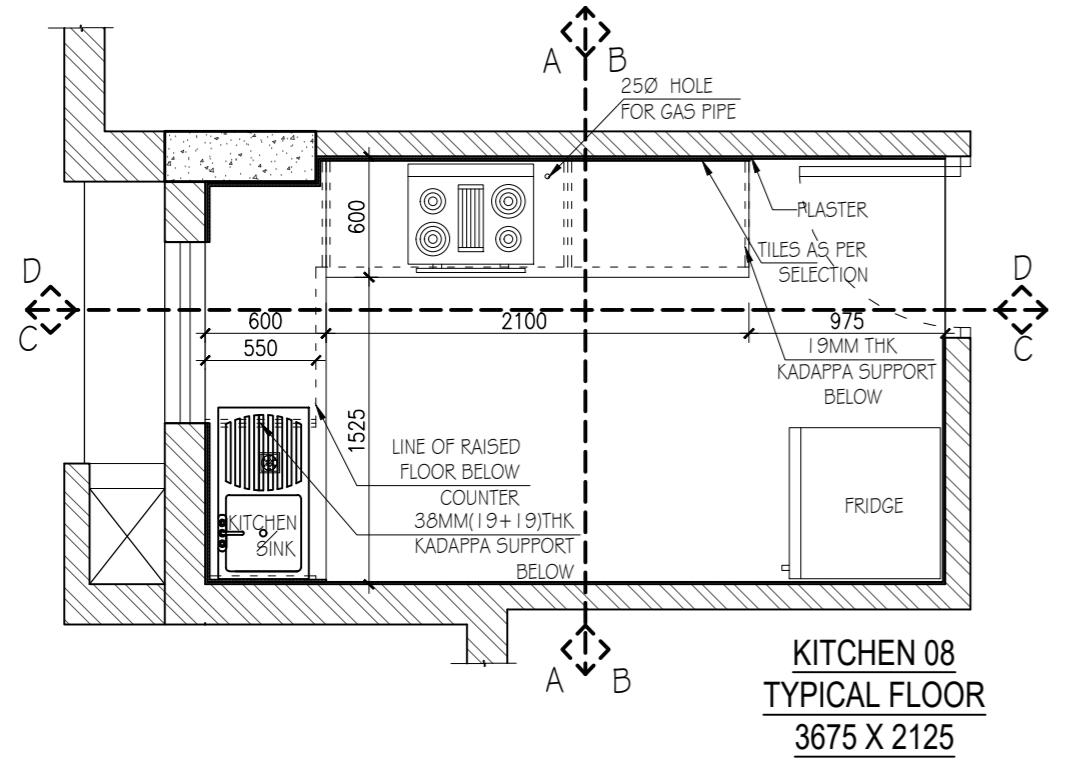


DETAIL AT X


SCALE-1:5

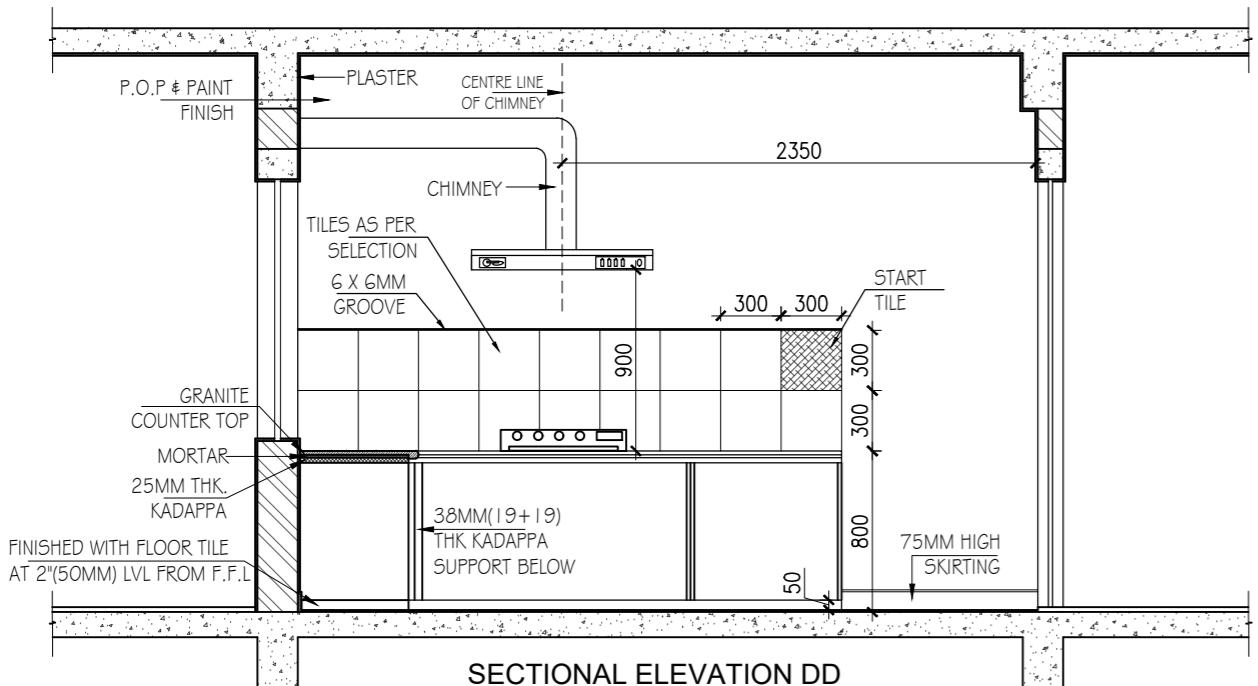


SECTIONAL ELEVATION DD

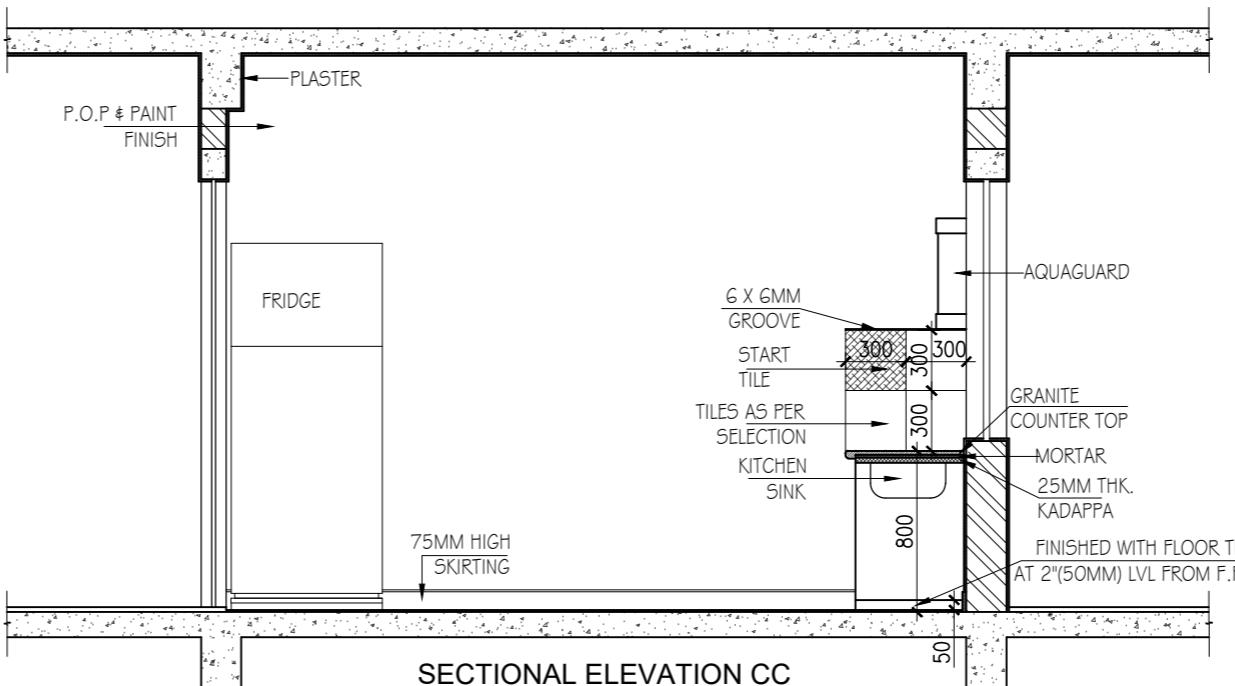


SECTIONAL ELEVATION CC

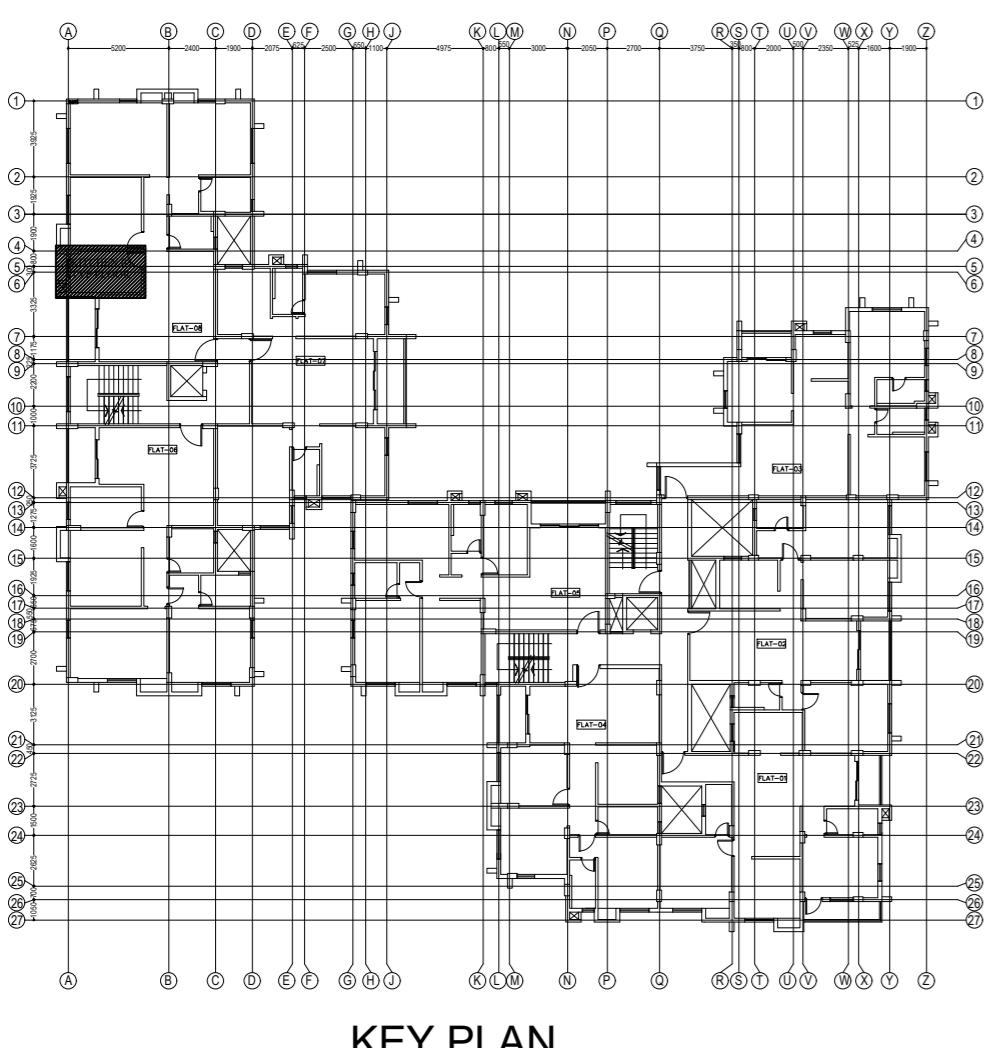

KEY PLAN







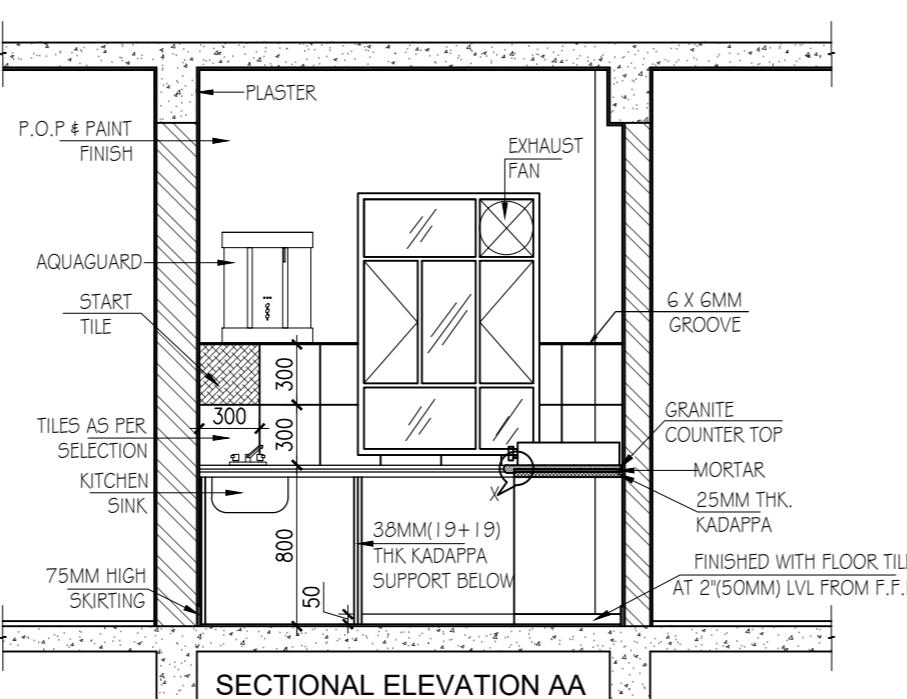


SECTIONAL ELEVATION AA

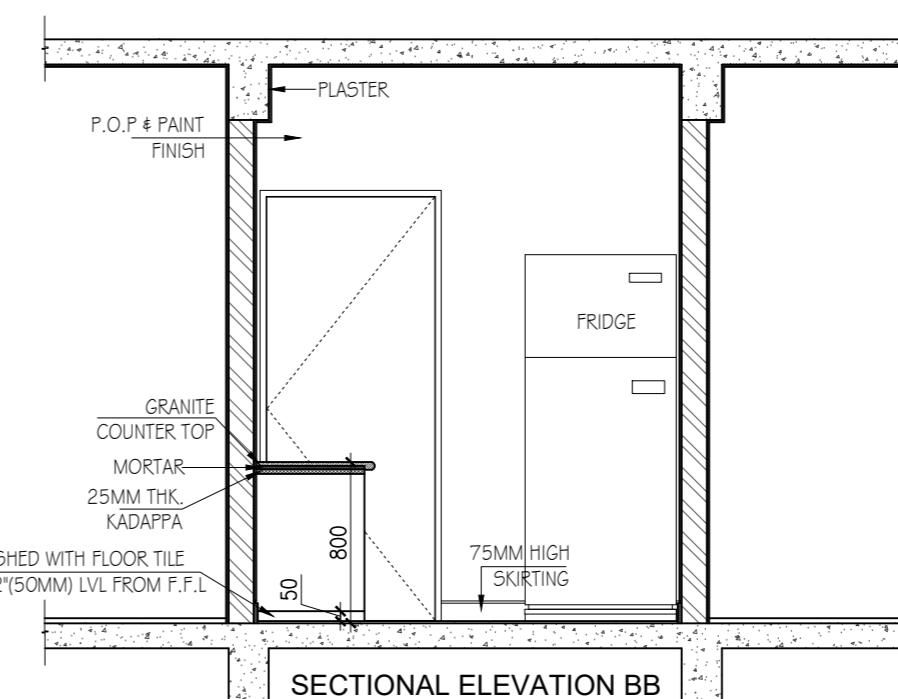


SECTIONAL ELEVATION BE


| DATE | DRAWN BY | CHECKED BY | DESCRIPTION OF THE REVISIONS |
|---|----------|---|---------------------------------------|
| | | | |
| | | | |
| | | | |
| | | | |
| | | | |
| STRUCTURAL SPA CONSULTANTS, 34, Rammohan Dutta Road, 2nd floor kol 20 | | | |
| PROJECT: PROPOSED G+IV STORIED RESIDENTIAL HOUSING COMPLEX FOR KOYLA VIHAR, PHASE-III, AT MOUZA-MONDALGANTHI, J.L. NO- 06, DAG NO- 273,274,275,276 & 277; KHTIAN NO-190/1 & 992, TOUZI NO - 172, WARD NO- 12, P.S.- BAGUIATI, DIST- 24 PGS(N), UNDER RAJARHAT GOPALPUR MUNICIPALITY. | | | |
| CLIENT: SPACE GROUP | | | |
| PROJECT ARCHITECTS:  Maheswari & Associates An ISO 9001 : 2008 CERTIFIED ORGANISATION 37A Baker Road, 2nd Floor, Alipore, Kolkata-700027 +91-33-24490323 / 65228584 Website: www.architectm.com MUMBAI-KOLKATA-GUWAHATI-SILIGURI | | | |
| PURPOSE OF RELEASE GOOD FOR CONSTRUCTION | | | |
| STAGE: WORKING | | | |
| DIRECTION: | | SCALE: 1:25 <small>UNLESS OTHERWISE SPECIFIED</small> | Current Revision: R0 |
| Start Date: | | Issue Date: | Last saved Date: |
| 5-05-13 | | 03.12.19 | - |
| Project Code: | | KOL-KV | |
| ldng/Block: | | BLOCK AB | |
| loor: | | TYPICAL FLOOR | |
| rawing title: | | KITCHEN DETAIL | |
| RG NO. | | MA/AR/KOYLA VIHAR/DETAILS/KITCHEN-01 | |
| <small>THIS DRAWING IS THE SOLE PROPERTY OF MAHESWARI & ASSOCIATES. IT'S USE FOR ANY PURPOSE OTHER THAN THAT MENTIONED IS TO BE DONE ONLY AFTER PRIOR APPROVAL.</small> | | | |

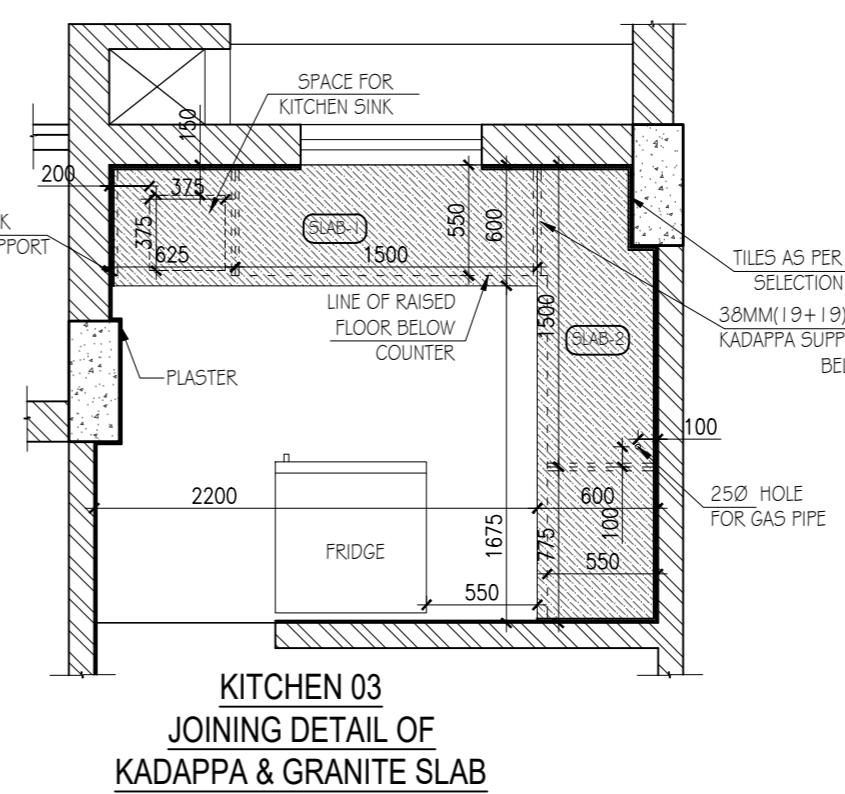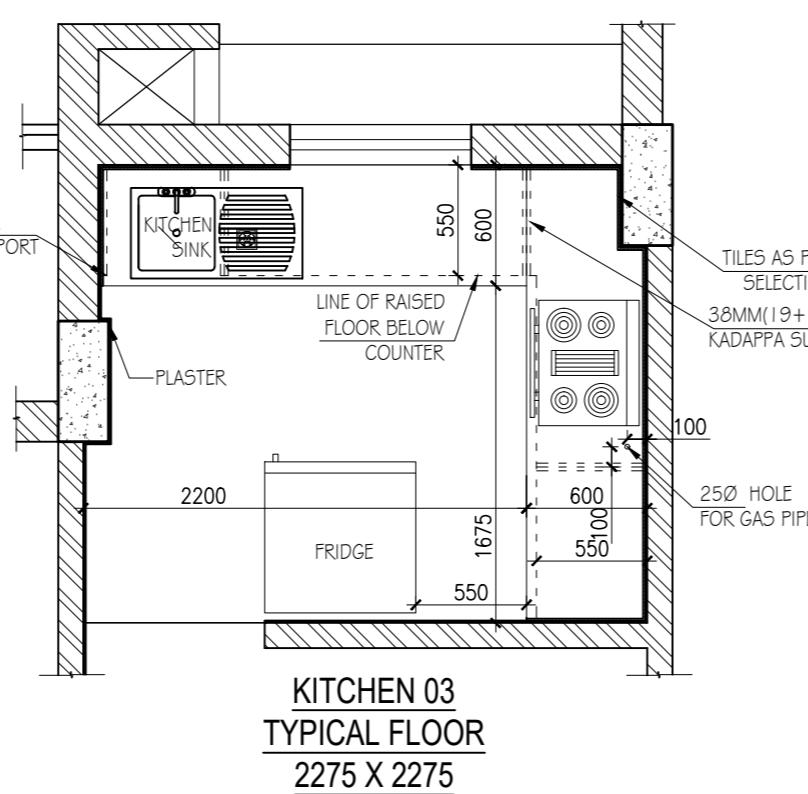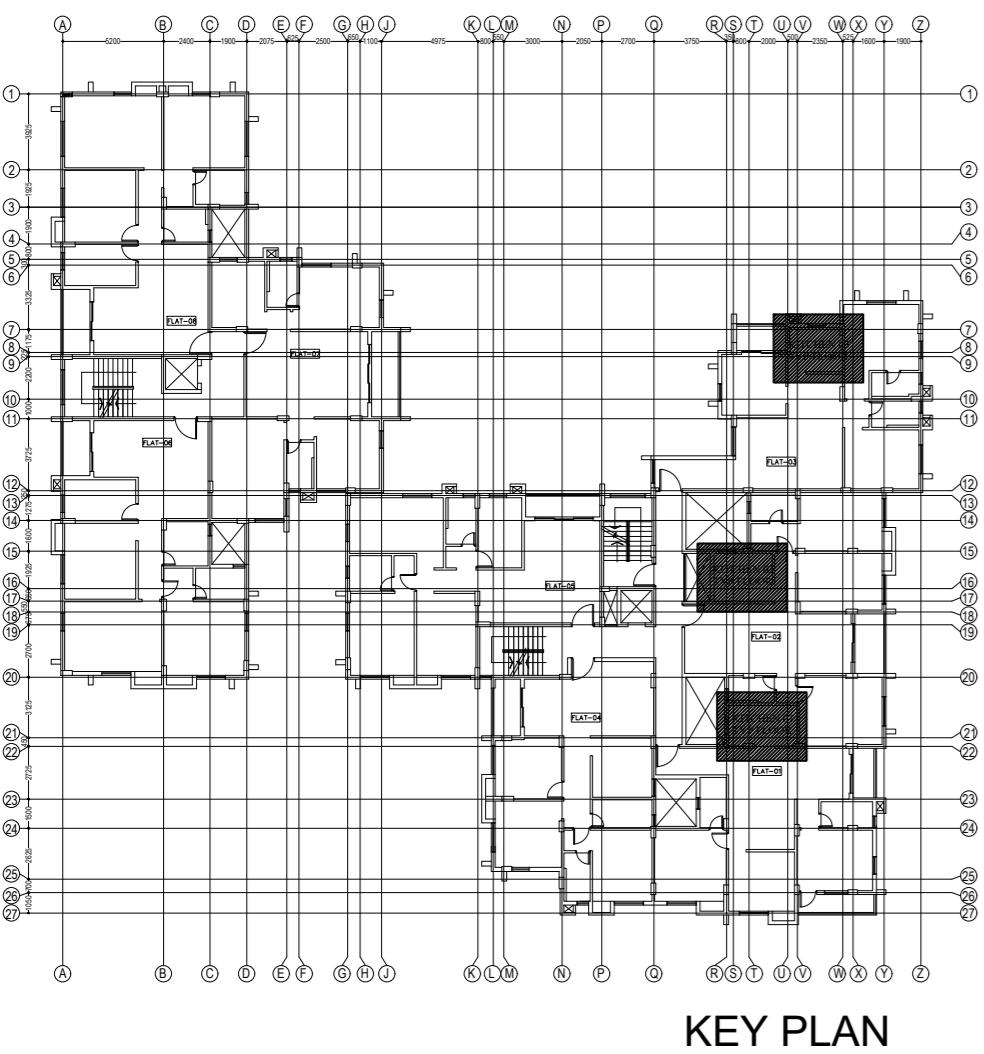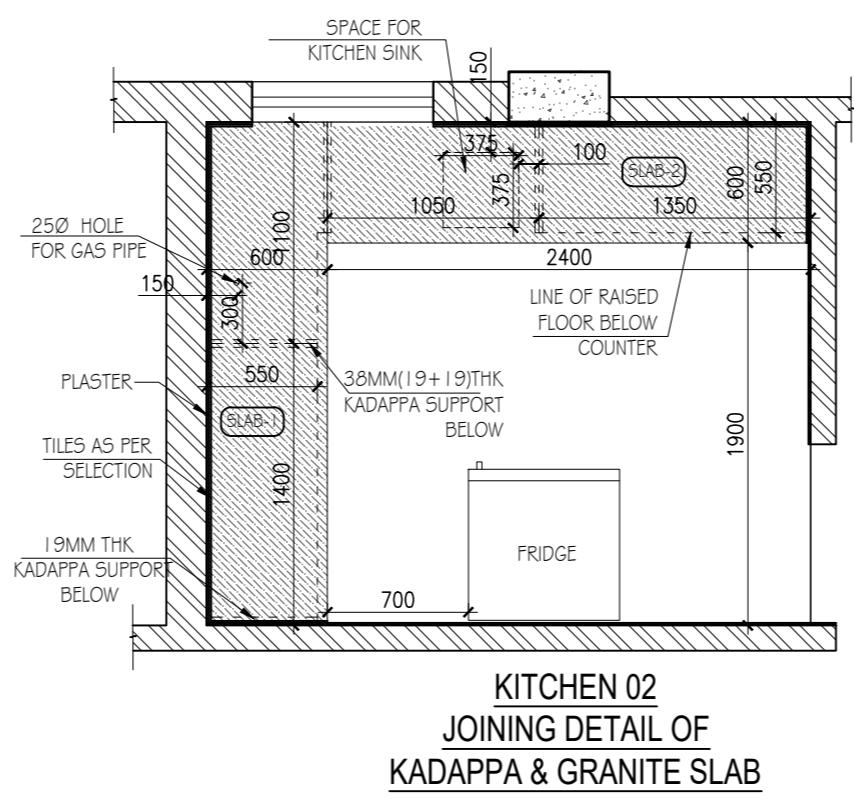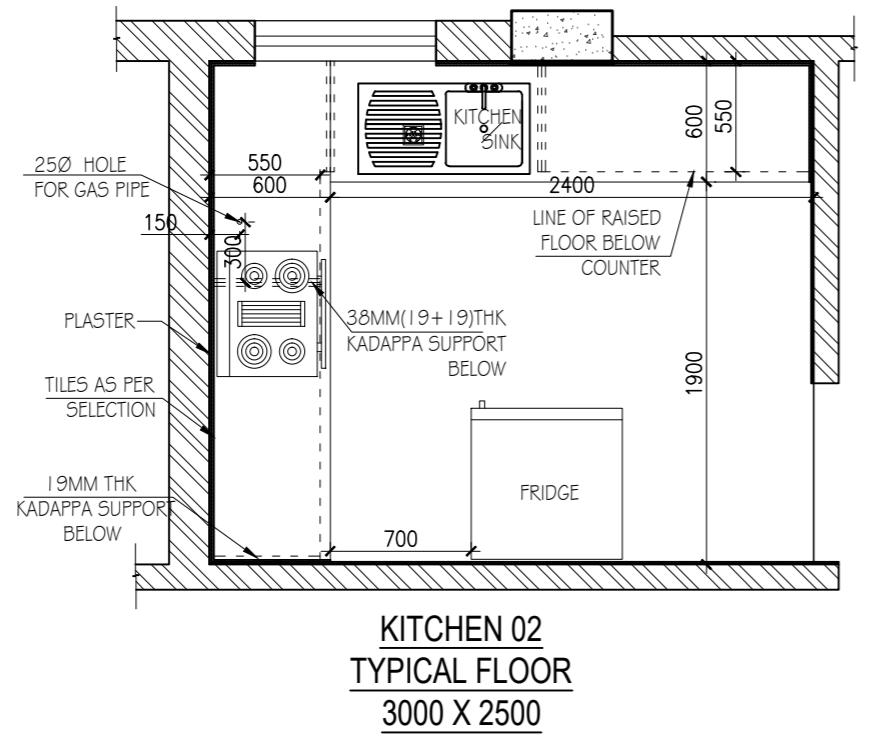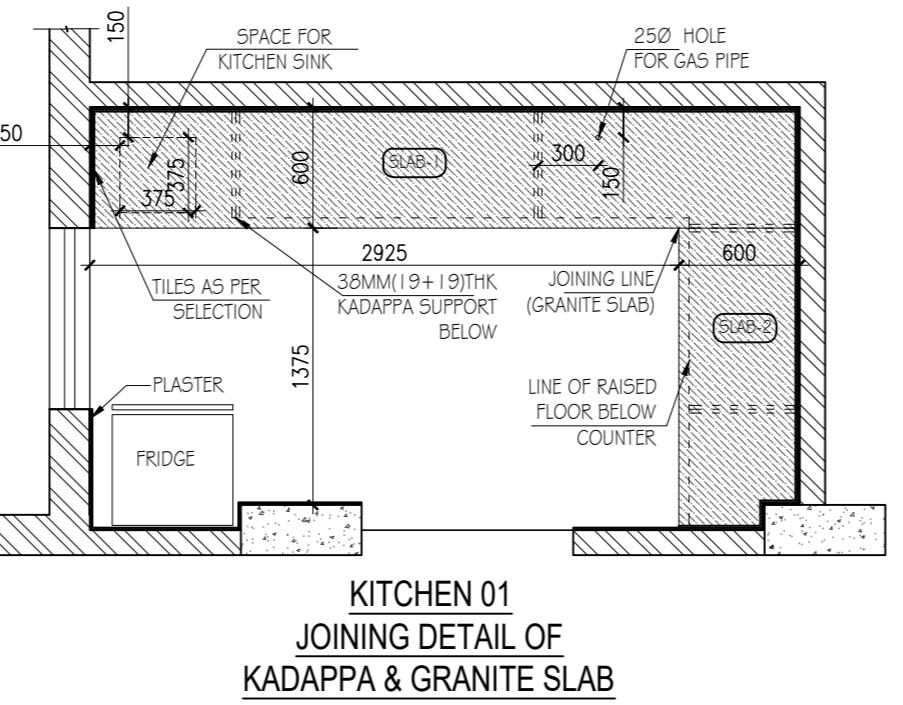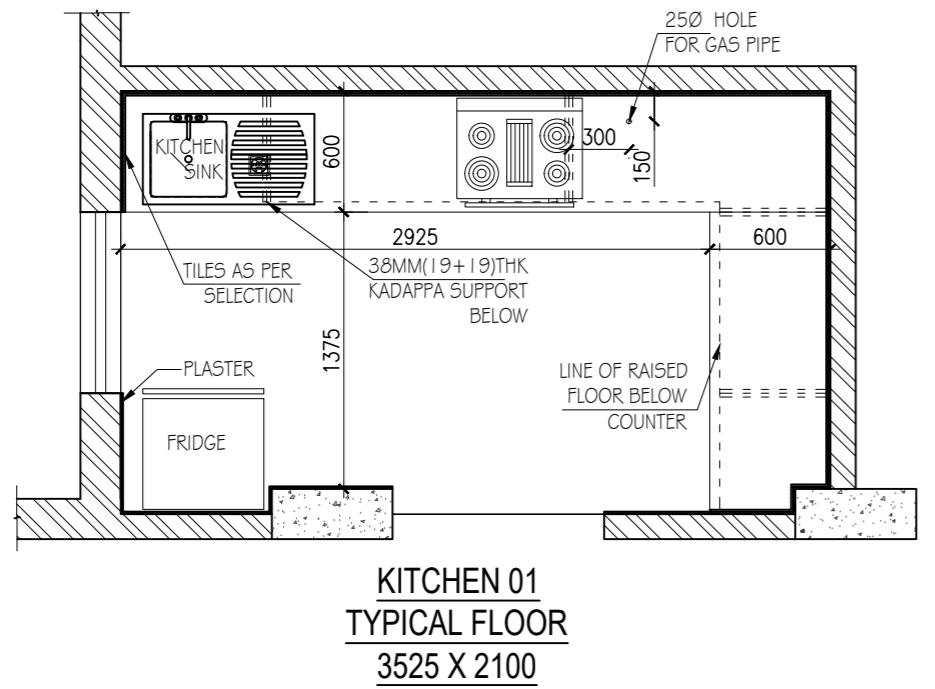


| DATE | DRAWN BY | CHECKED BY | DESCRIPTION OF THE REVISIONS |
|---|---|--------------------------|------------------------------|
| | | | |
| | | | |
| | | | |
| | | | |
| STRUCTURAL SPA CONSULTANTS, 34, Rammohan Dutta Road, 2nd floor kol 20 | | | |
| PROJECT: PROPOSED G+IV STORIED RESIDENTIAL HOUSING COMPLEX FOR KOYLA VIHAR, PHASE-III, AT MOUZA-MONDALGANTHI, J.L. NO- 06, DAG NO- 273,274,275,276 & 277; KHTIAN NO-190/1 & 992, TOUZI NO - 172, WARD NO- 12, P.S. - BAGIATI, DIST- 24 PGS(N), UNDER RAJARHAT GOPALPUR MUNICIPALITY. | | | |
| CLIENT: SPACE GROUP | | | |
| PROJECT ARCHITECTS: | | | |
| Maheswari & Associates  An ISO 9001 : 2008 CERTIFIED ORGANISATION 37A Baker Road, 2nd Floor, Alipore, Kolkata-700027 +91-33-24490323 / 65228584 Website: www.architectcm.com MUMBAI-KOLKATA-GUWAHATI-SILIGURI | | | |
| PURPOSE OF RELEASE | | | |
| GOOD FOR CONSTRUCTION | | | |
| STAGE: | WORKING | | |
| DIRECTION: | SCALE: 1:25 UNLESS OTHERWISE SPECIFIED | Current Revision: | R0 |
| Start Date: | Issue Date: | Last saved Date: | |
| 15-05-13 | 05.12.19 | - | |
| Project Code: | KOL-KV | | |
| Bldng/Block: | BLOCK AB | | |
| Floor: | TYPICAL FLOOR | | |
| Drawing title: | KITCHEN DETAIL (01,02, 03) | | |
| DRG NO. | MA/AR/KOYLA VIHAR/DETAILS/KITCHEN-06 | | |
| THIS DRAWING IS THE SOLE PROPERTY OF MAHESWARI & ASSOCIATES. ITS USE FOR ANY PURPOSE OTHER THAN THAT MENTIONED IS TO BE DONE ONLY AFTER PRIOR APPROVAL. | | | |

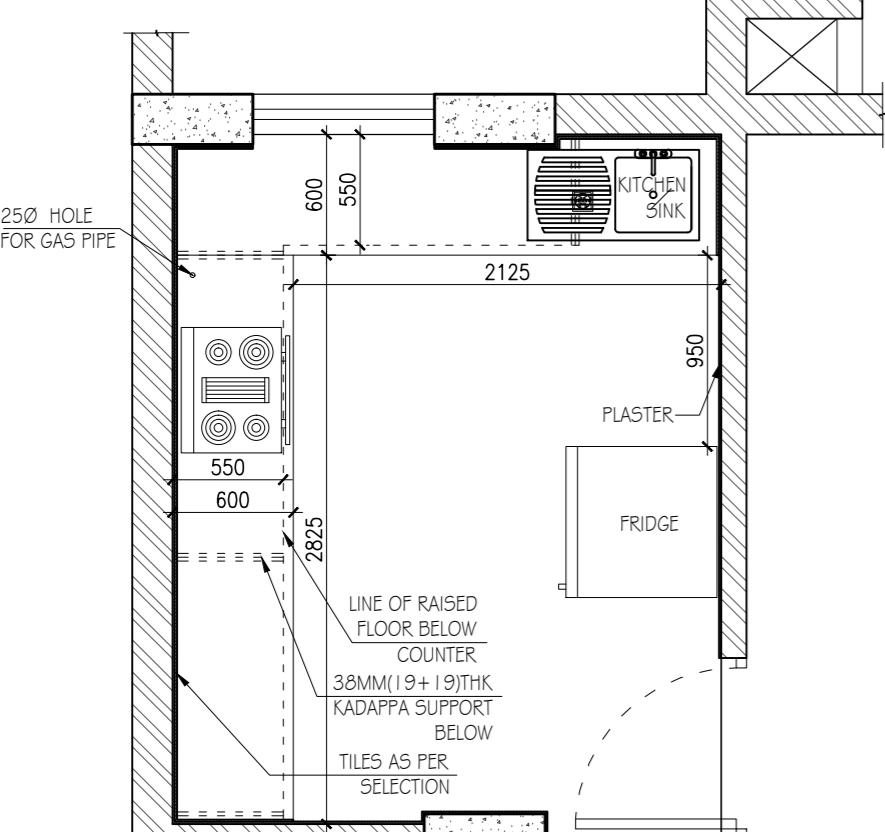


KITCHEN 07
TYPICAL FLOOR
2725 X 3375

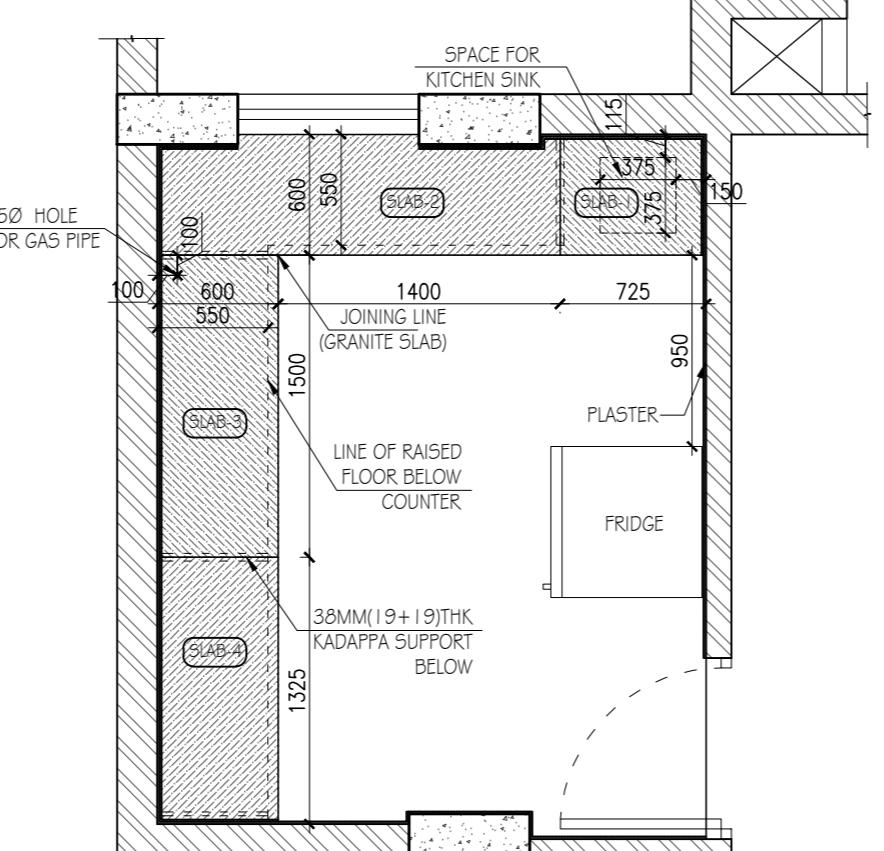


KITCHEN 07
JOINING DETAIL OF
KADAPPA & GRANITE SLAB

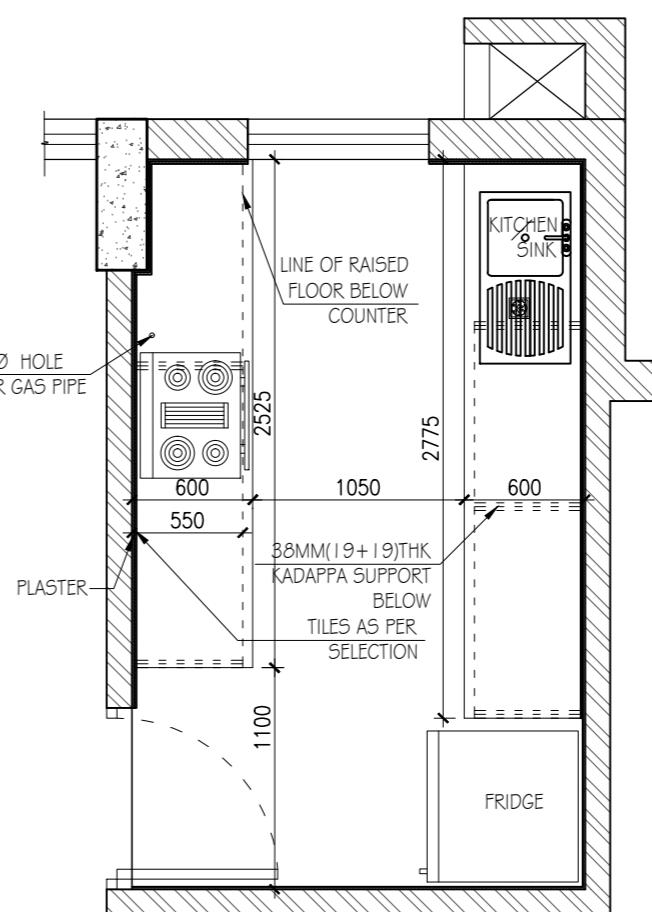


KITCHEN 05
TYPICAL FLOOR
2250 X 3625

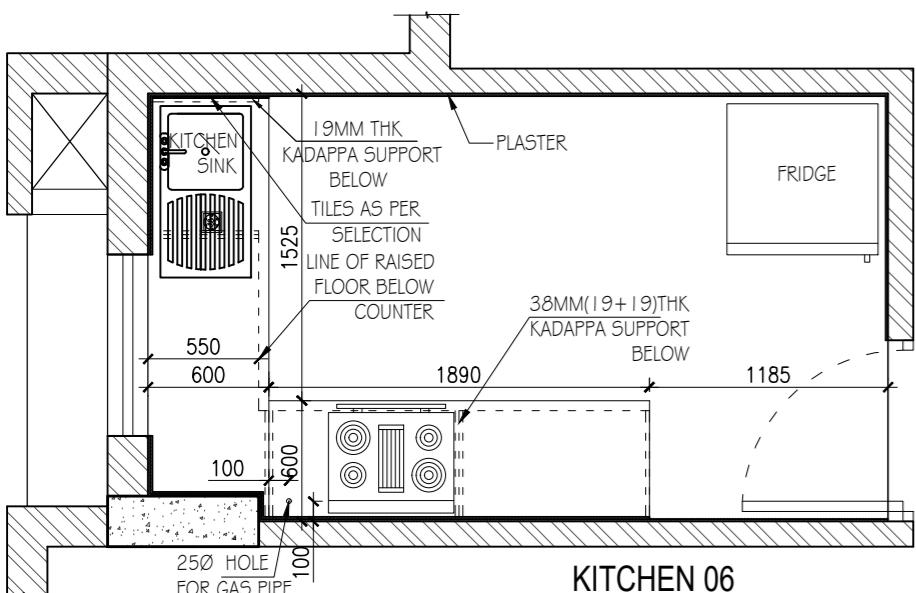


KITCHEN 06
TYPICAL FLOOR
3675 X 2125

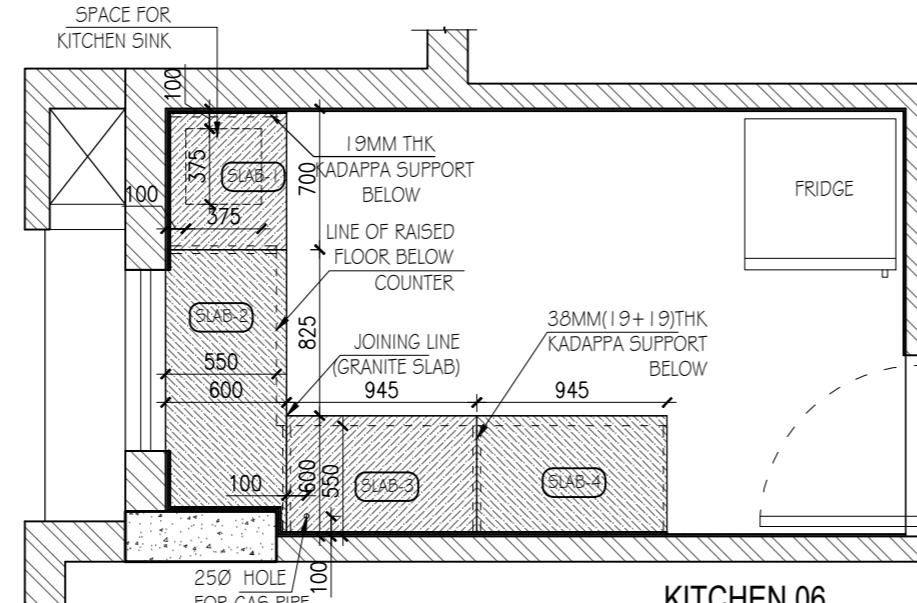


KITCHEN 06
JOINING DETAIL OF
KADAPPA & GRANITE SLAB

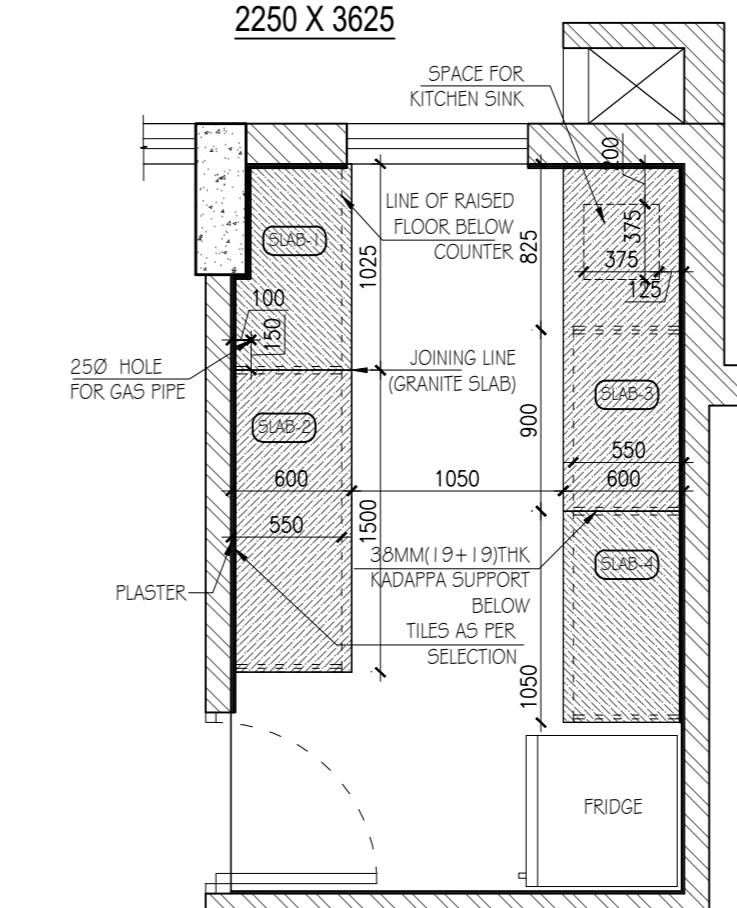

KITCHEN 05
JOINING DETAIL OF
KADAPPA & GRANITE SI A






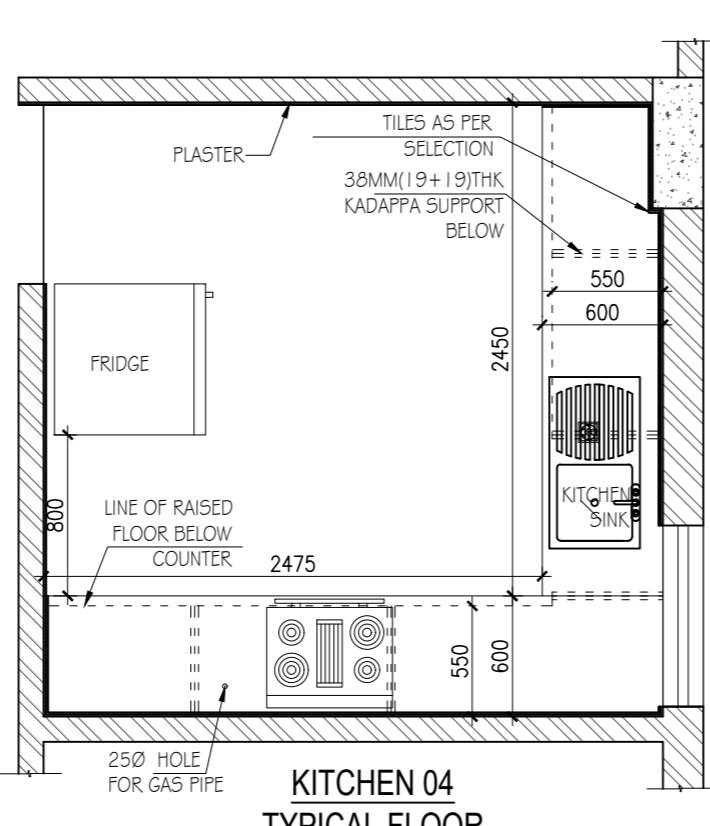


KITCHEN 04
TYPICAL FLOOR
3075 X 3050

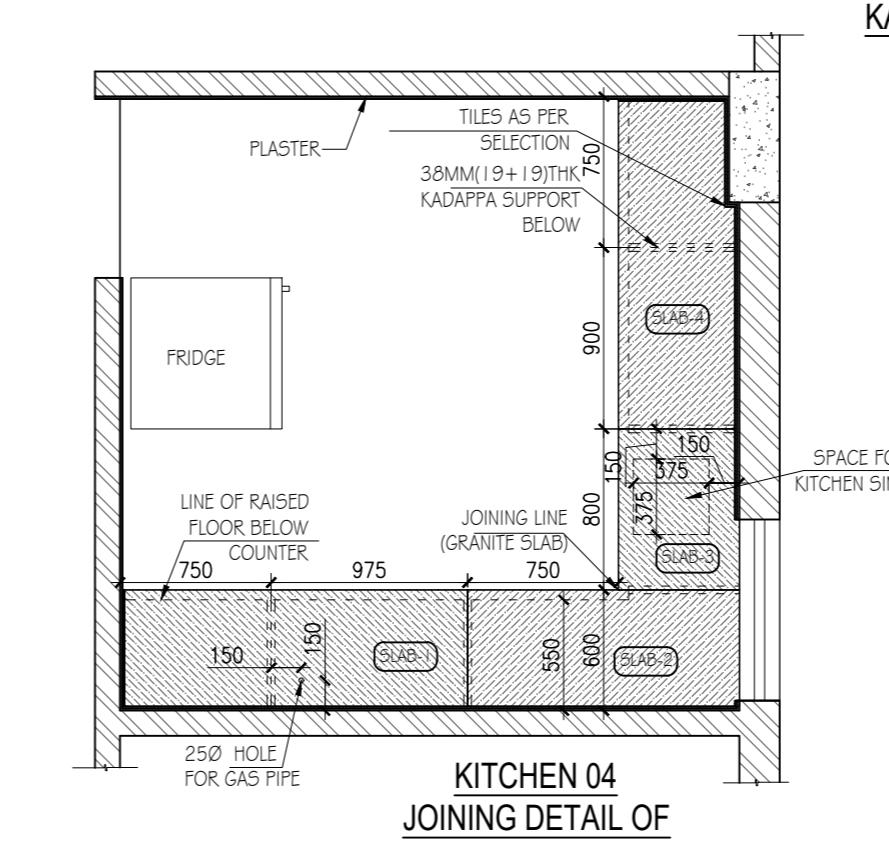

KITCHEN 04
JOINING DETAIL OF
KADAPPA & GRANITE SLA

| DATE | DRAWN BY | CHECKED BY | DESCRIPTION OF THE REVISIONS |
|---|---|---|---------------------------------------|
| | | | |
| | | | |
| | | | |
| | | | |
| | | | |
| | | | |
| STRUCTURAL SPA CONSULTANTS, 34, Rammohan Dutta Road, 2nd floor kol 20 | | | |
| PROJECT: PROPOSED G+IV STORIED RESIDENTIAL HOUSING COMPLEX FOR KOYLA VIHAR, PHASE-III, AT MOUZA-MONDALGANTHI, J.L. NO- 06, DAG NO- 273,274,275,276 & 277; KHTIAN NO-190/1 & 992, TOUZI NO - 172, WARD NO- 12, P.S.- BAGUIATI, DIST- 24 PGS(N), UNDER RAJARHAT GOPALPUR MUNICIPALITY. | | | |
| CLIENT: SPACE GROUP | | | |
| PROJECT ARCHITECTS:  Maheswari & Associates An ISO 9001 : 2008 CERTIFIED ORGANISATION 37A Baker Road, 2nd Floor, Alipore, Kolkata-700027 +91-33-24490323 / 65228584 Website: www.architectm.com MUMBAI-KOLKATA-GUWAHATI-SILIGURI | | | |
| PURPOSE OF RELEASE GOOD FOR CONSTRUCTION | | | |
| STAGE: | | WORKING | |
| DIRECTION: | | SCALE: 1:25 UNLESS OTHERWISE SPECIFIED | Current Revision: R0 |
| Start Date: | | Issue Date: | Last saved Date: |
| 15-05-13 | | 03.12.19 | - |
| Project Code: | | KOL-KV | |
| Bldng/Block: | | BLOCK AB | |
| Floor: | | TYPICAL FLOOR | |
| Drawing title: | KITCHEN DETAIL | | |
| DRG NO. | MA/AR/KOYLA VIHAR/DETAILS/KITCHEN-02 | | |
| THIS DRAWING IS THE SOLE PROPERTY OF MAHESWARI & ASSOCIATES. IT'S USE FOR ANY PURPOSE OTHER THAN THAT MENTIONED IS TO BE DONE ONLY AFTER PRIOR APPROVAL. | | | |

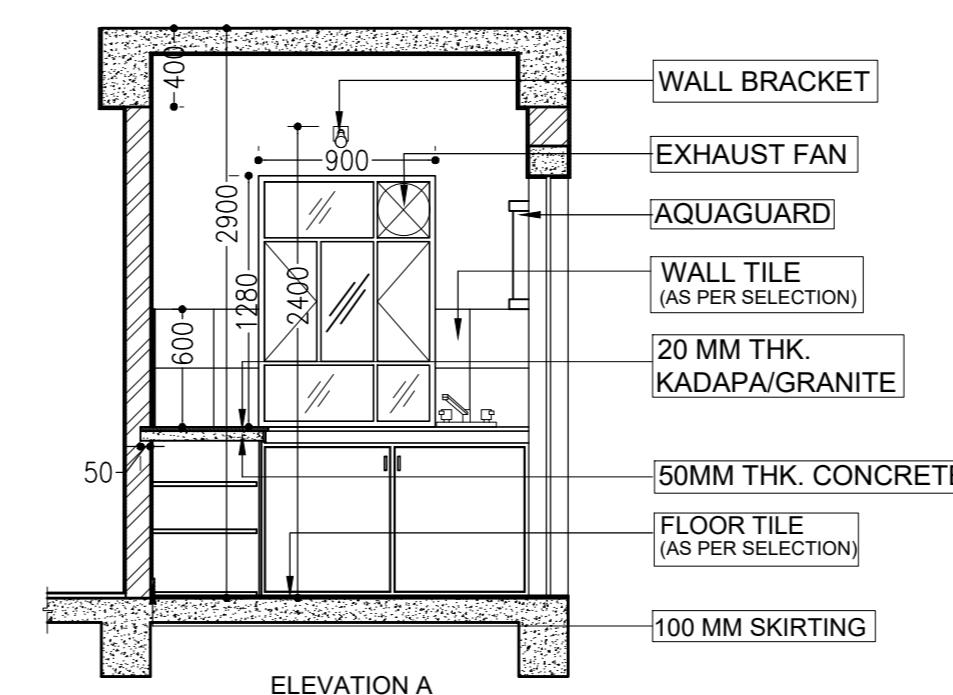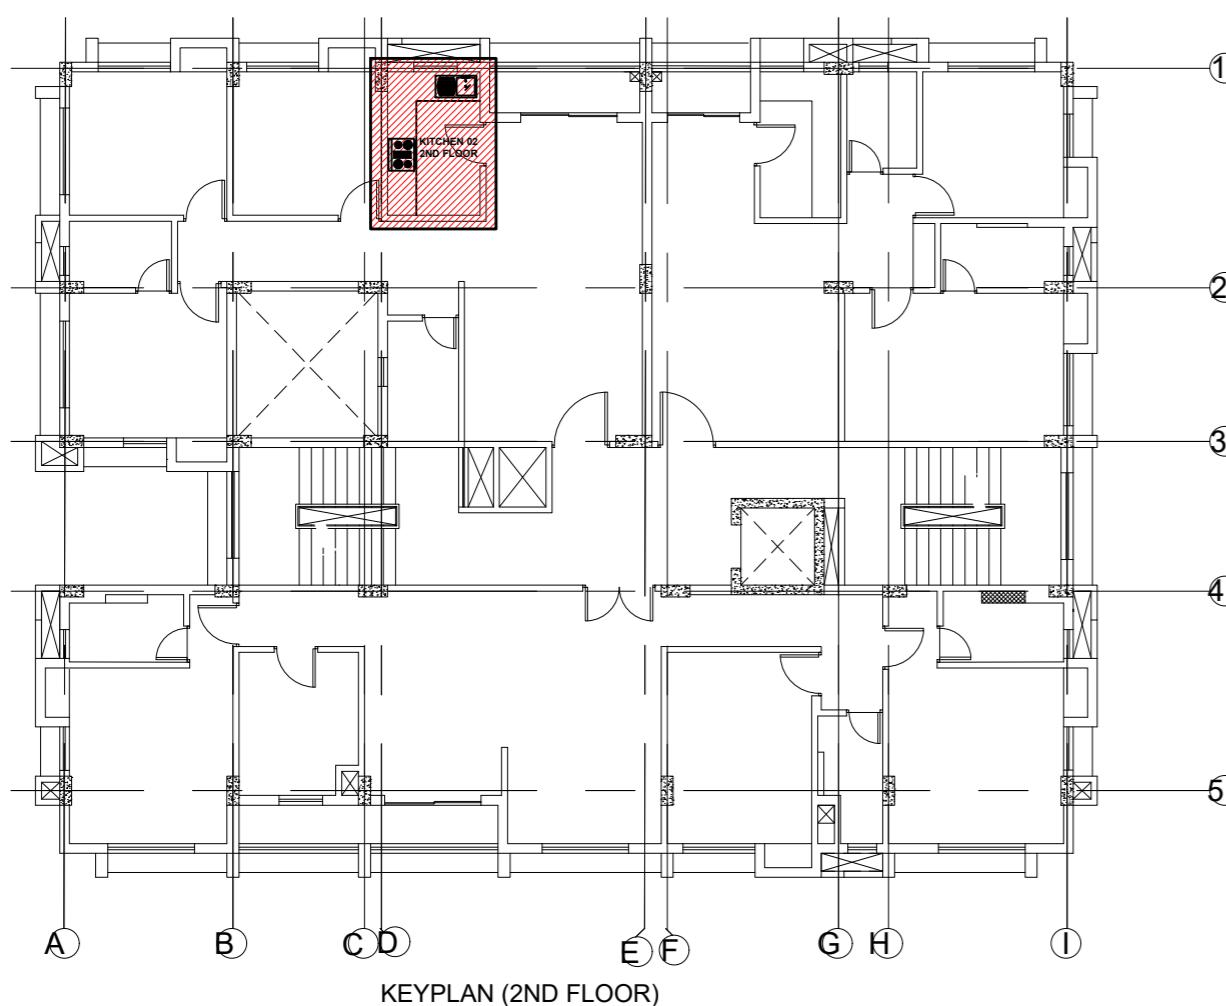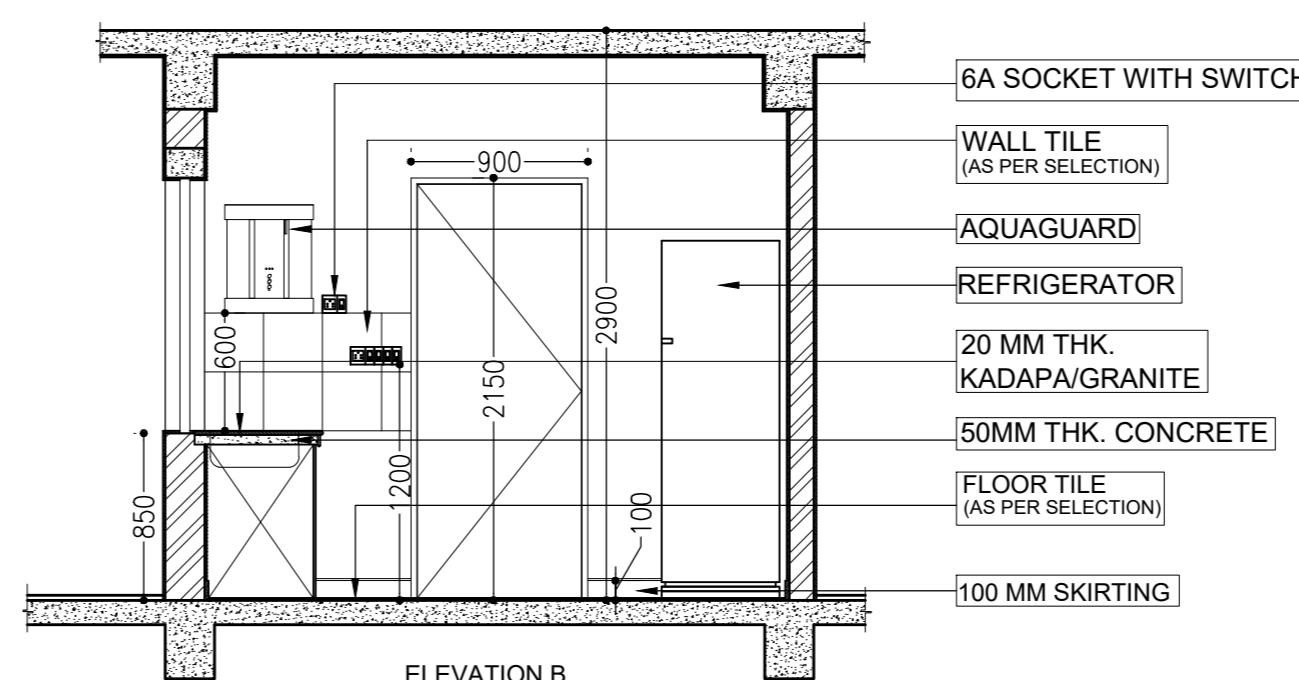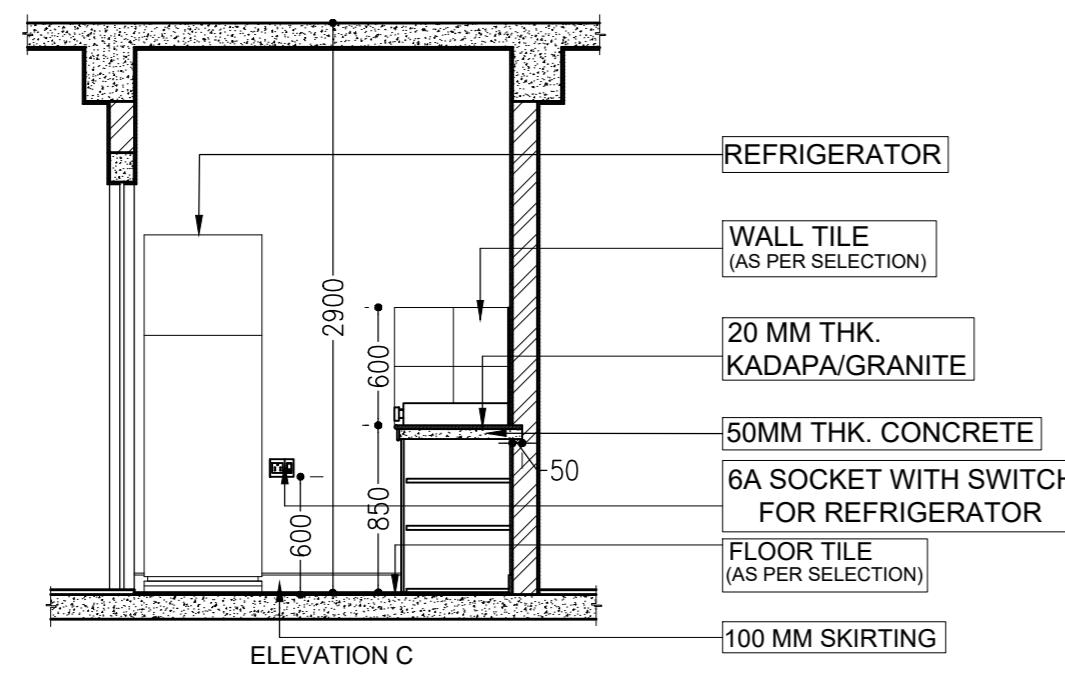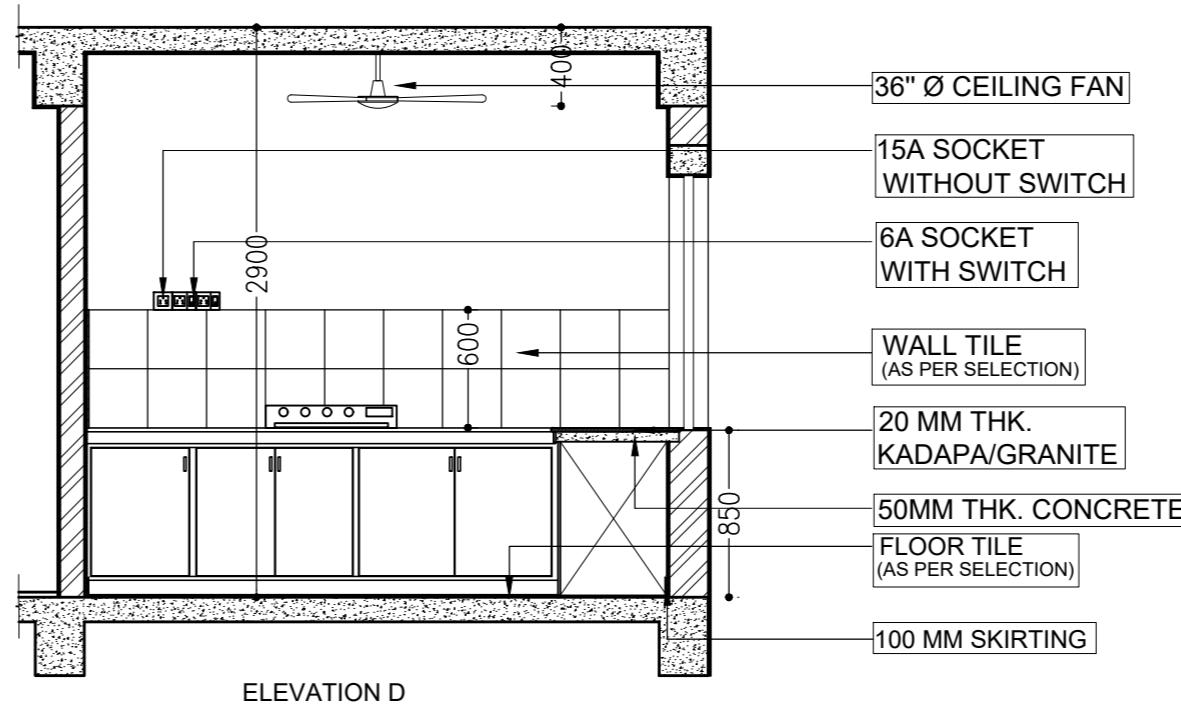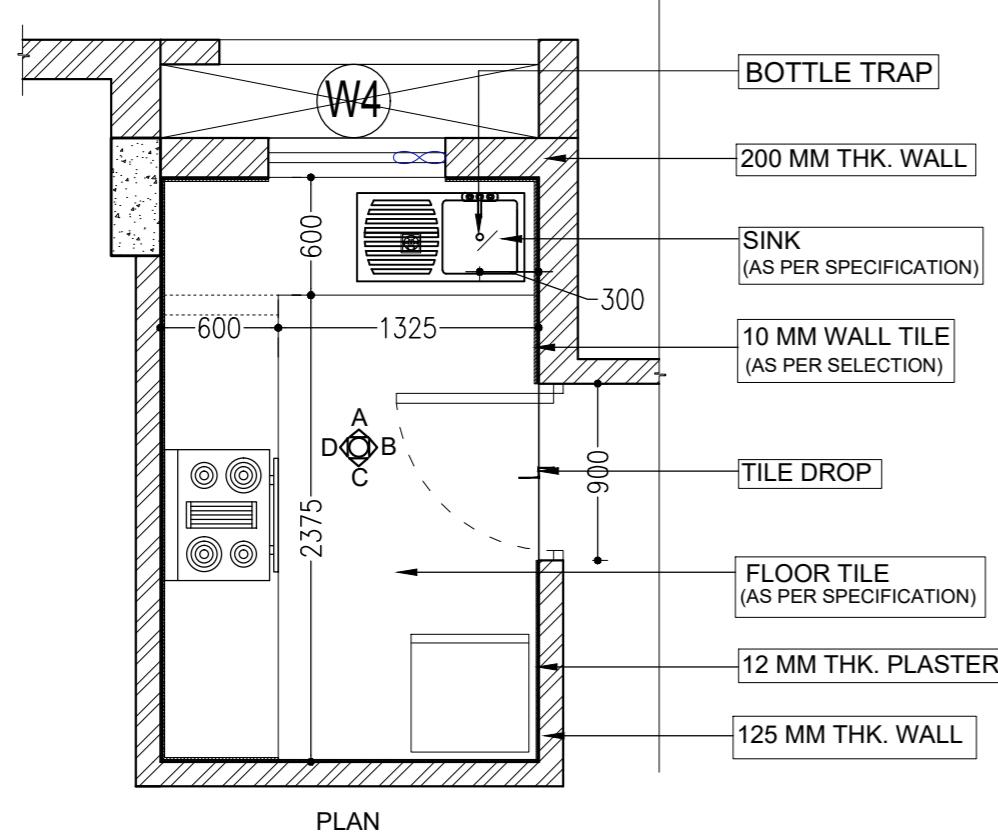

SIGNATURE OF ARCHITECT

REVISIONS

| DATE | DRAWN BY | CHECKED BY | DESCRIPTION OF THE REVISIONS |
|------|----------|------------|------------------------------|
| | | | |
| | | | |
| | | | |
| | | | |

STRUCTURAL
SPA CONSULTANTS,
34, Rammohan Dutta Road, 2nd floor kol 20

PROJECT:
**PROPOSED G+IV STORIED RESIDENTIAL
HOUSING COMPLEX FOR KOYLA VIHAR,**
PHASE-III, AT MOUZA-MONDALGANTHI, J.L. NO- 06, DAG
NO- 273,274,275,276 & 277; KHATIAN NO-190/1 & 992, TOUZI
NO - 172, WARD NO- 12, P.S.- BAGUIATI, DIST- 24 PGS(N),
UNDER RAJARHAT GOPALPUR MUNICIPALITY.

CLIENT:
SPACE GROUP

PROJECT ARCHITECTS:



Maheswari & Associates


An ISO 9001 : 2008 CERTIFIED ORGANISATION
37A Baker Road, 2nd Floor, Alipore, Kolkata-700027
+91-33-24490323 / 65228584
Website: www.architectcm.com
MUMBAI-KOLKATA-GUWAHATI-SILIGURI

PURPOSE OF RELEASE


GOOD FOR CONSTRUCTION

| STAGE: | | |
|----------------|--|--------------------------------|
| DIRECTION: | SCALE: 1:25 UNLESS OTHERWISE SPECIFIED | Current Revision: R0 |
| Start Date: | Issue Date: | Last saved Date: |
| 15-05-20 | | |
| Project Code: | KOL-KV | |
| Bldg/Block: | BLOCK D | |
| Floor: | 2ND FLOOR | |
| Drawing title: | KITCHEN DETAIL | |
| DRG NO. | MA/AR/KOYLA VIHAR/DETAILS/KITCHEN-01 | |


THIS DRAWING IS THE SOLE PROPERTY OF MAHESWARI & ASSOCIATES. ITS USE FOR ANY
PURPOSE OTHER THAN THAT MENTIONED IS TO BE DONE ONLY AFTER PRIOR APPROVAL.

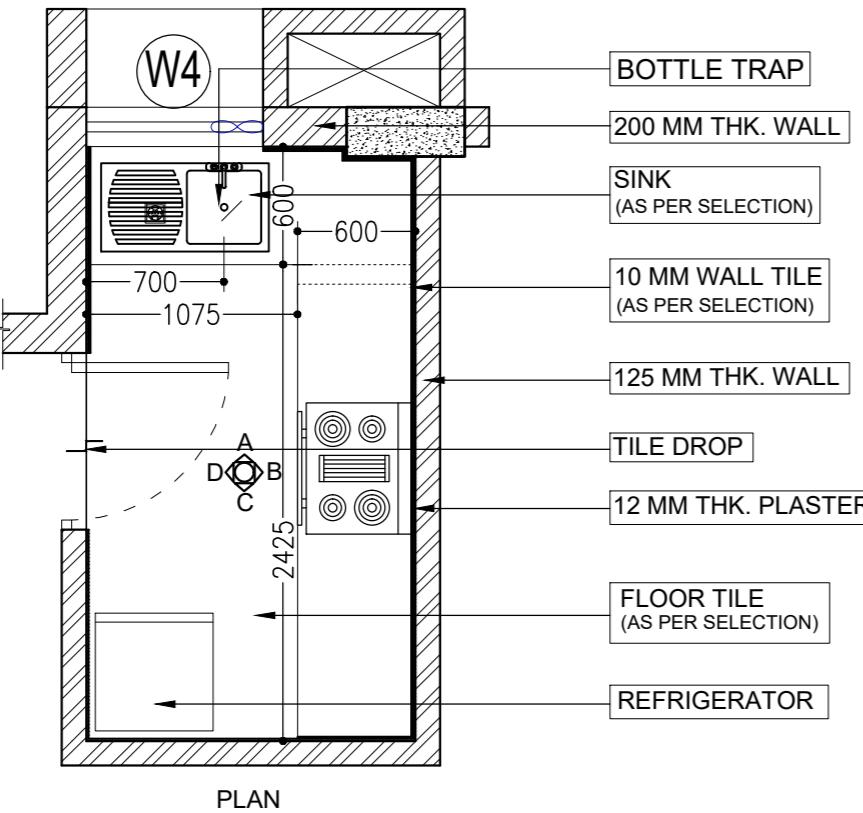


PLA

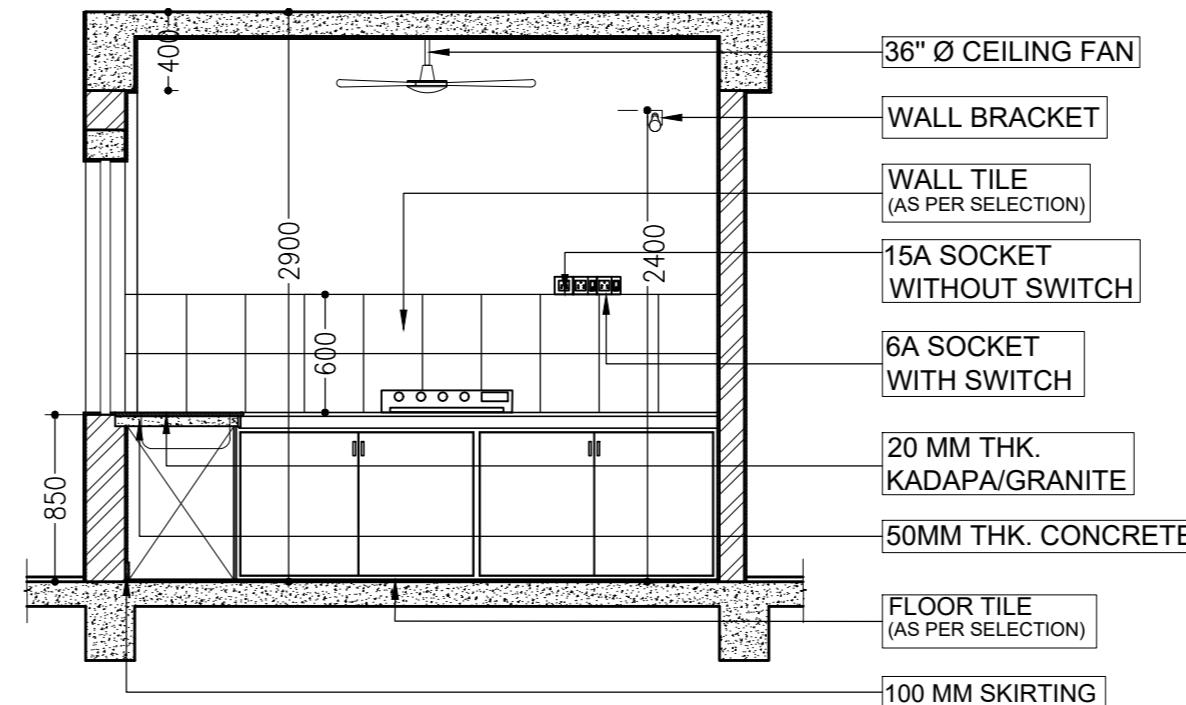


ELEVATION B

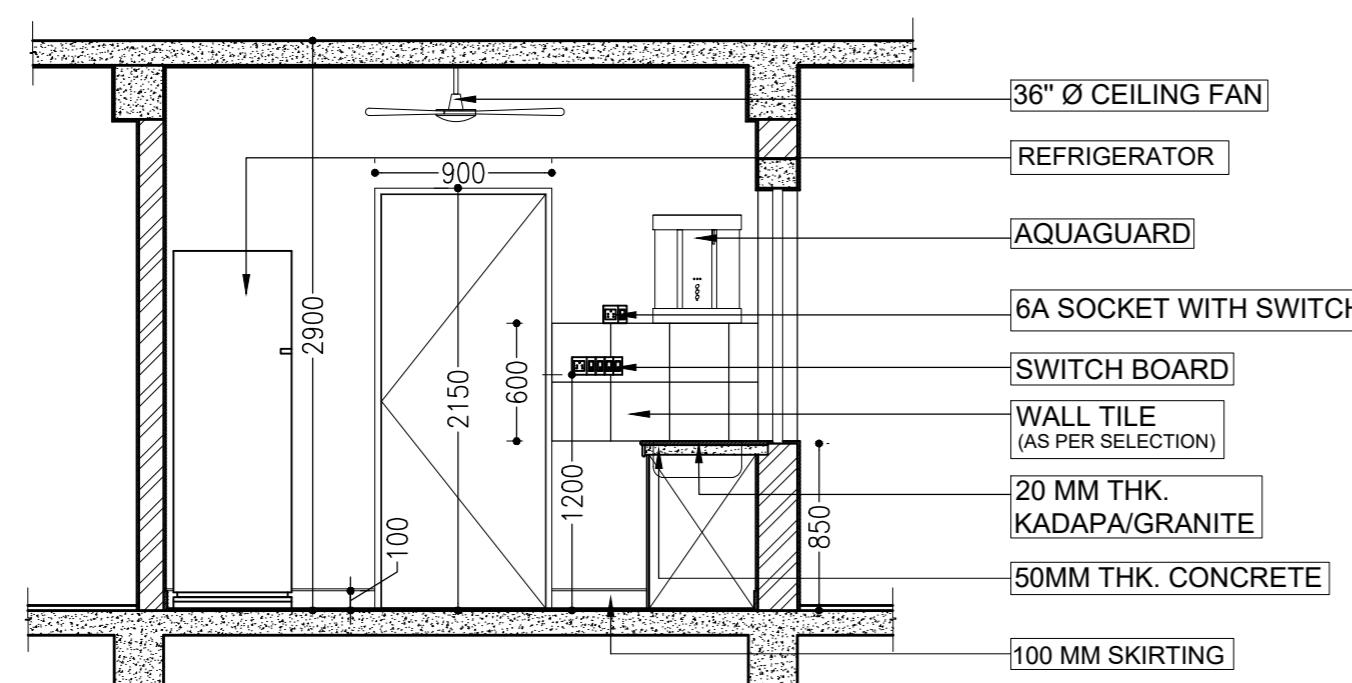


ELEVATION D

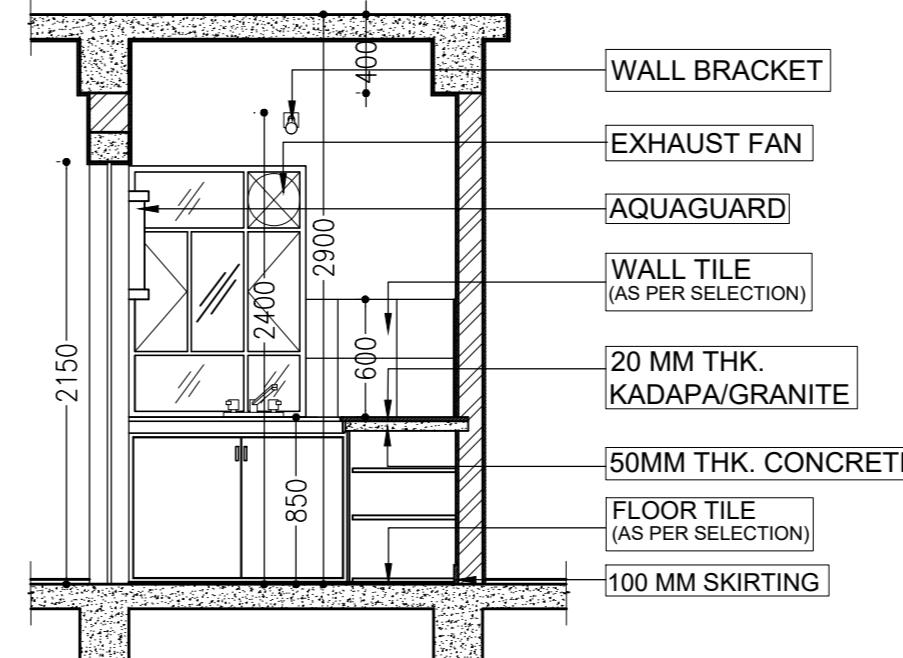

ELEVATION A

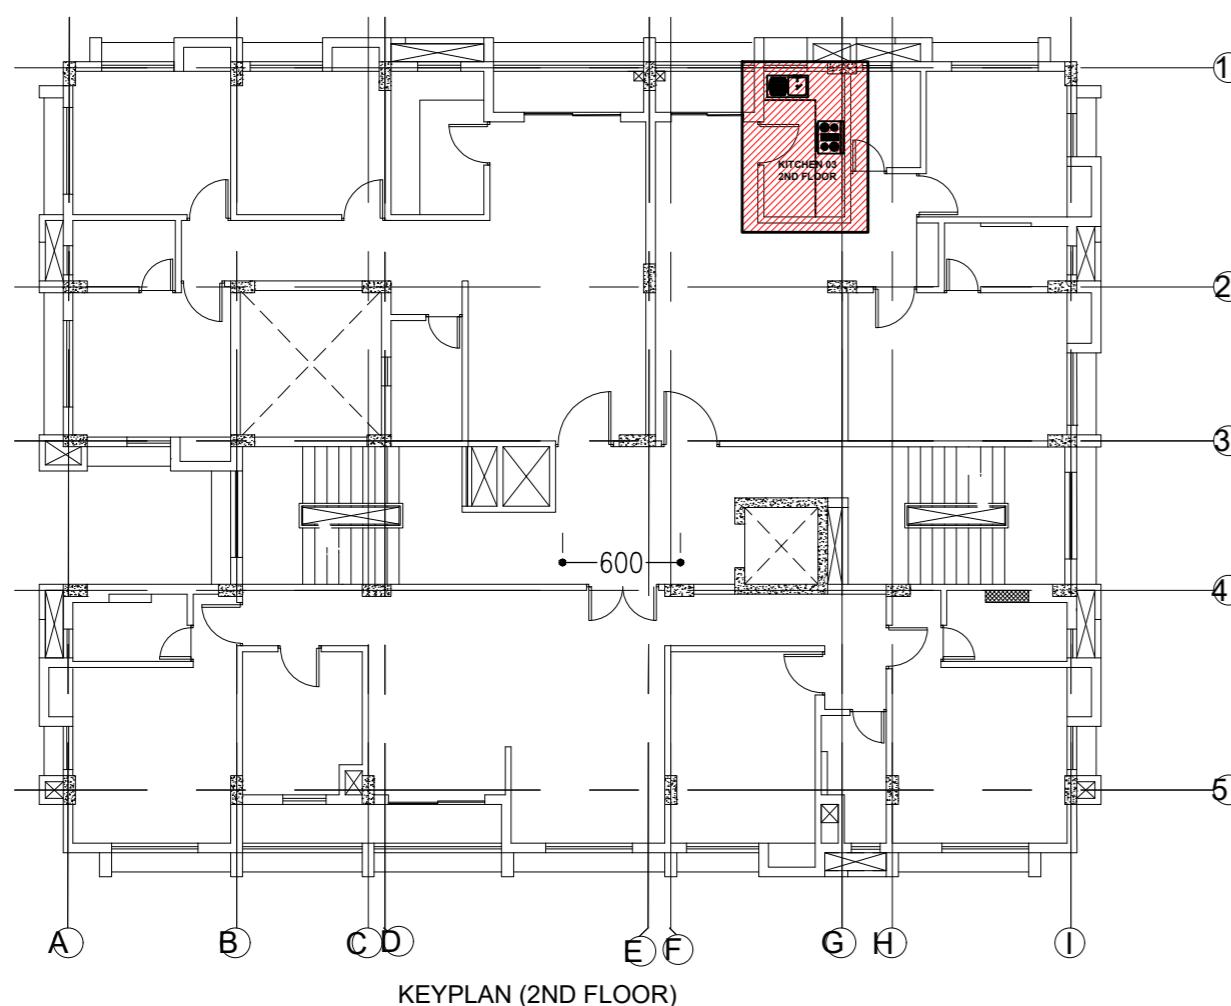

KEYPLAN (2ND FLOOR)

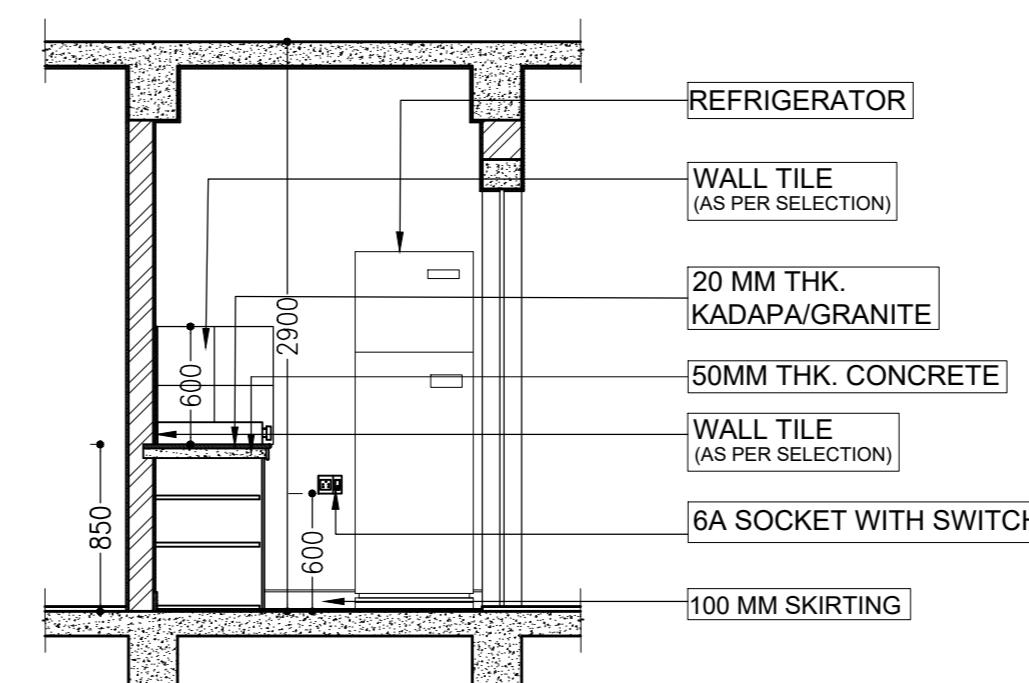

ELEVATION

SIGNATURE OF ARCHITECT

REVISIONS

| DATE | DRAWN BY | CHECKED BY | DESCRIPTION OF THE REVISIONS |
|------|----------|------------|------------------------------|
| | | | |
| | | | |
| | | | |
| | | | |
| | | | |

**STRUCTURAL
SPA CONSULTANTS,
34, Rammohan Dutta Road, 2nd floor kol 20**

PROJECT:

**PROPOSED G+IV STORIED RESIDENTIAL
HOUSING COMPLEX FOR KOYLA VIHAR,
PHASE-III, AT MOUZA-MONDALGANTHI, J.L. NO- 06, DAG
NO- 273,274,275,276 & 277; KHTIAN NO-190/1 & 992, TOUZI
NO - 172, WARD NO- 12, P.S.- BAGUIATI, DIST- 24 PGS(N),
UNDER RAJARHAT GOPALPUR MUNICIPALITY**

CLIENT:
SPACE GROUP

PROJECT ARCHITECTS:










Maheswari & Associates
An ISO 9001 : 2008 CERTIFIED ORGANISATION
37A Baker Road, 2nd Floor, Alipore, Kolkata-700027
+91-33-24490323 / 65228584
Website: www.architectm.com
MUMBAI-KOLKATA-GUWAHATI-SILIGURI

RELEASE

GOOD FOR CO

| | | | |
|--|--|------------------|--------------------------------|
| STAGE: | WORKING | | |
| DIRECTION: | SCALE: 1:25 UNLESS OTHERWISE SPECIFIED | | Current Revision: R0 |
| Start Date: | Issue Date: | Last saved Date: | |
| 15-05-20 | | | |
| Project Code: | KOL-KV | | |
| Bldng/Block: | BLOCK D | | |
| Floor: | 2ND FLOOR | | |
| Drawing title: | KITCHEN DETAIL | | |
| DRG NO. | MA/AR/KOYLA VIHAR/DETAILS/KITCHEN-02 | | |
| THIS DRAWING IS THE SOLE PROPERTY OF MAHESWARI & ASSOCIATES. IT'S USE FOR ANY PURPOSE OTHER THAN THAT MENTIONED IS TO BE DONE ONLY AFTER PRIOR APPROVAL. | | | |

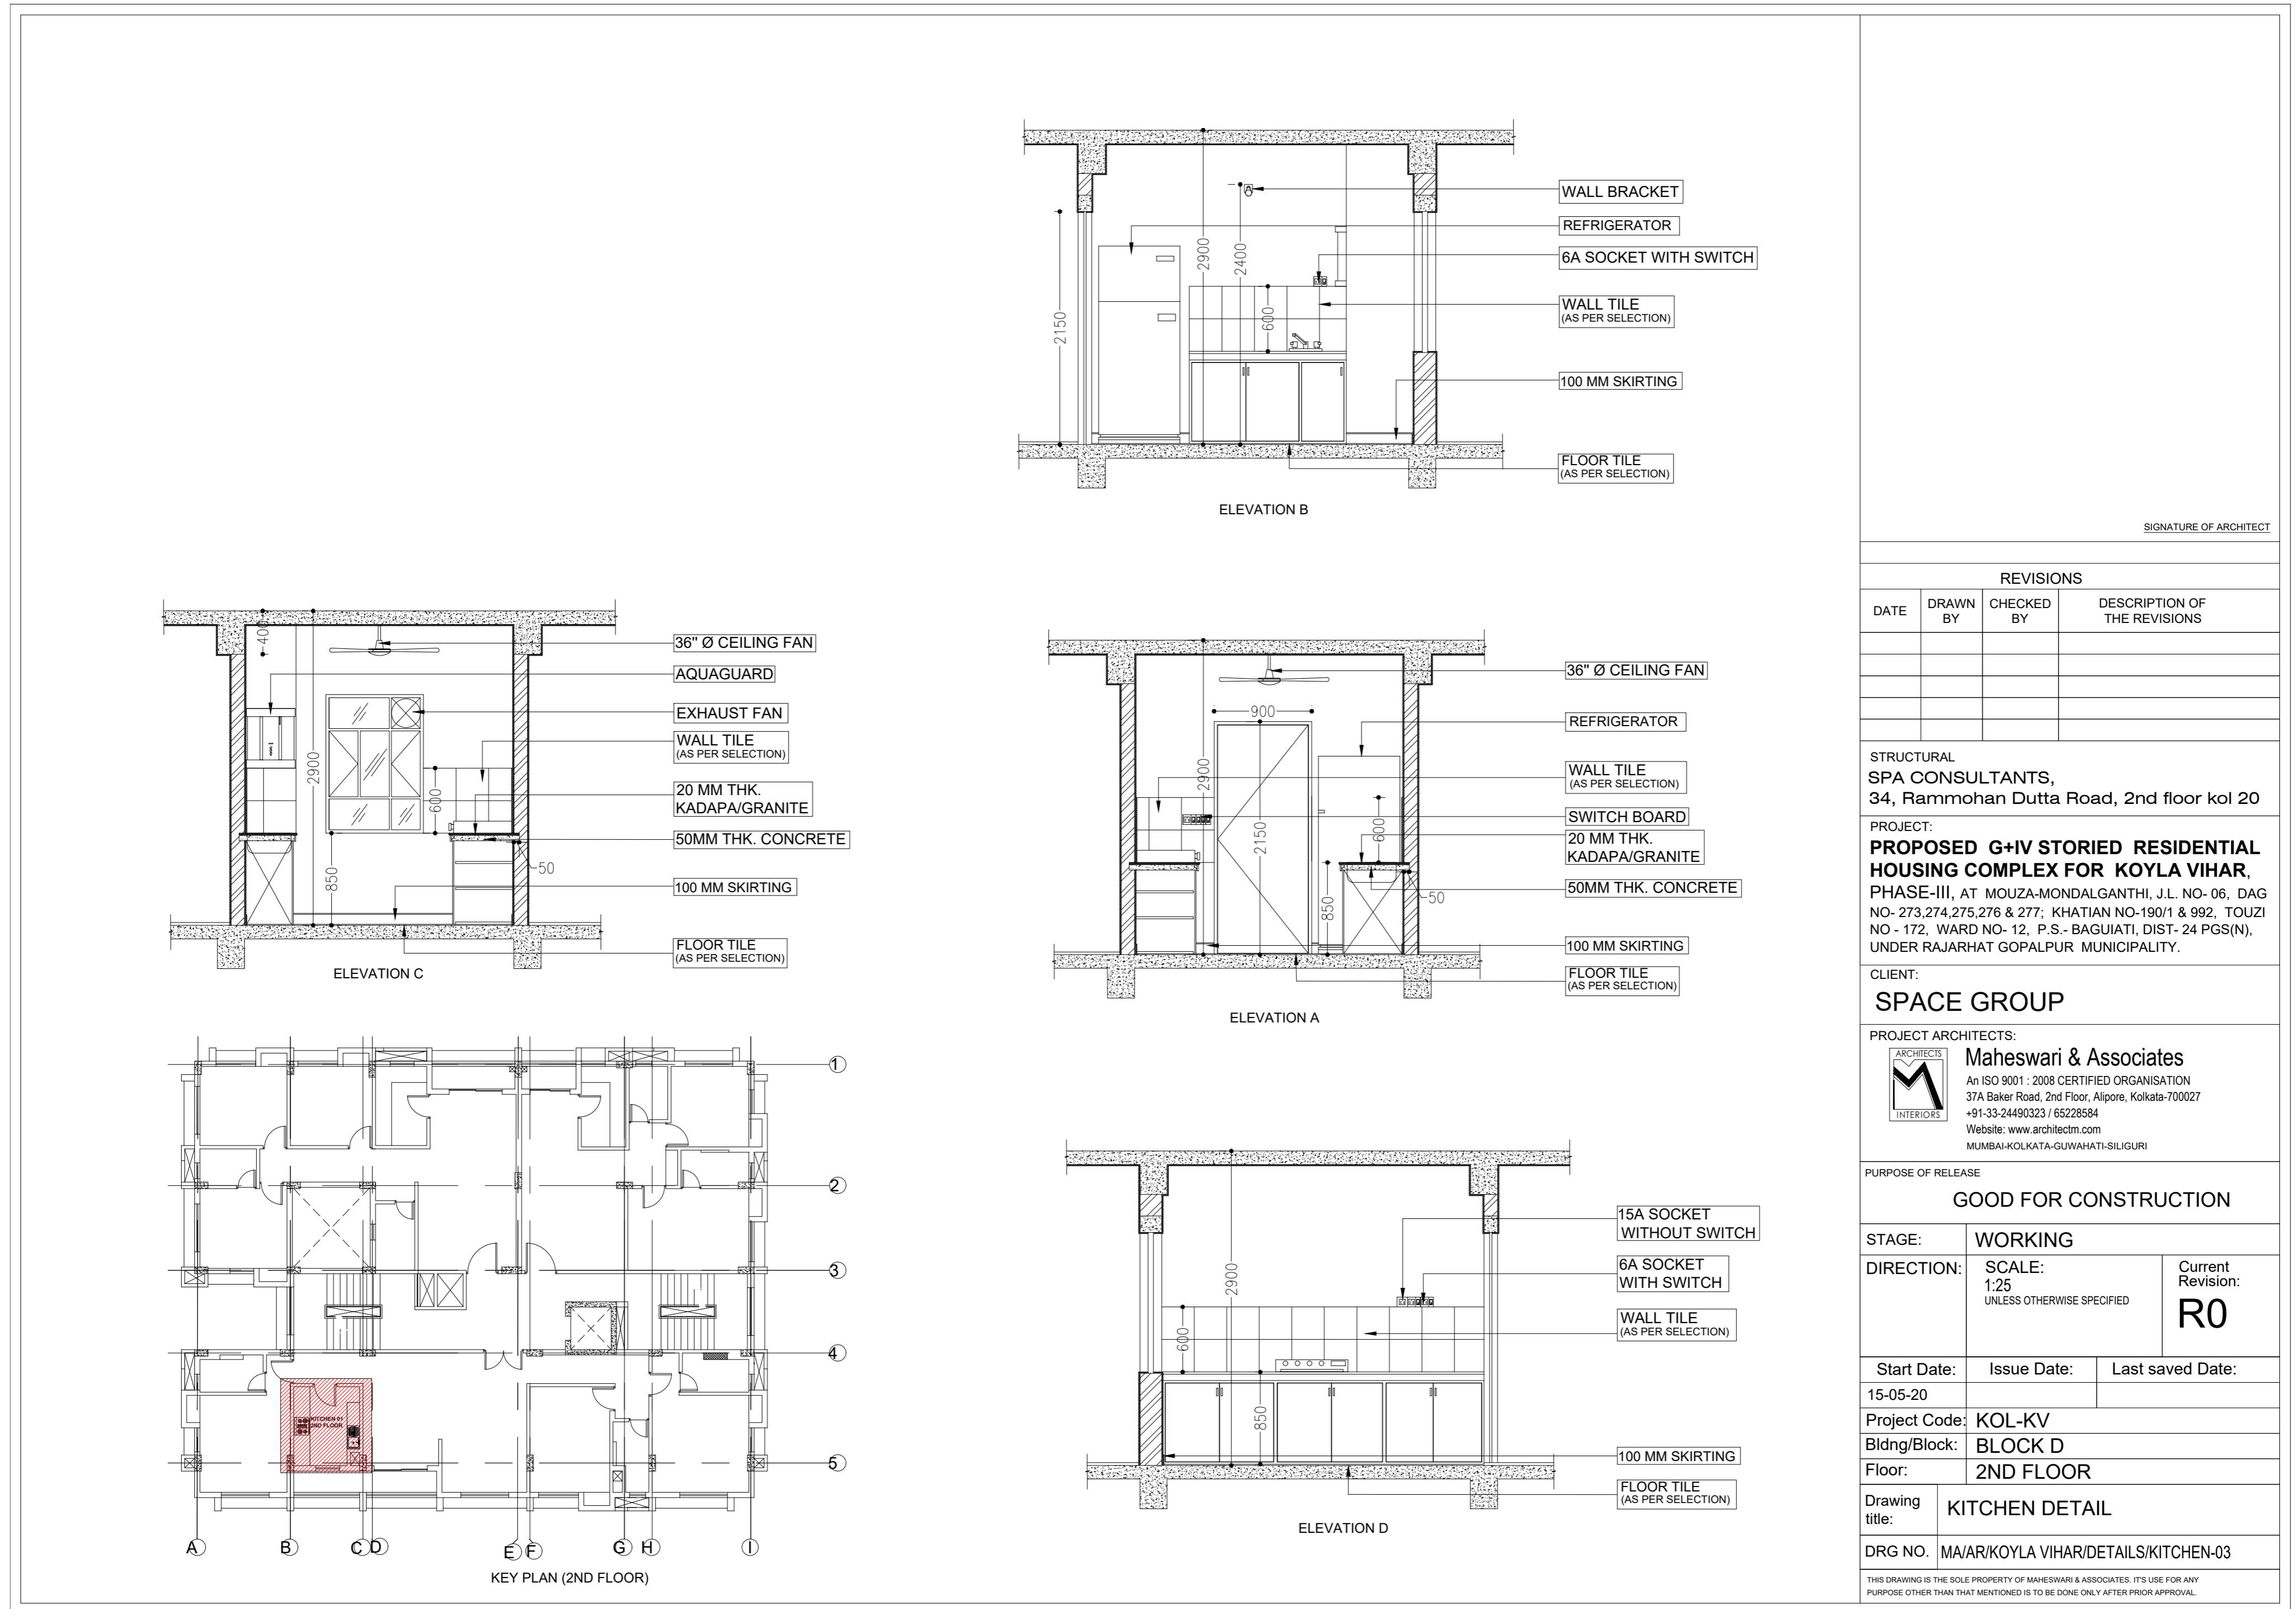

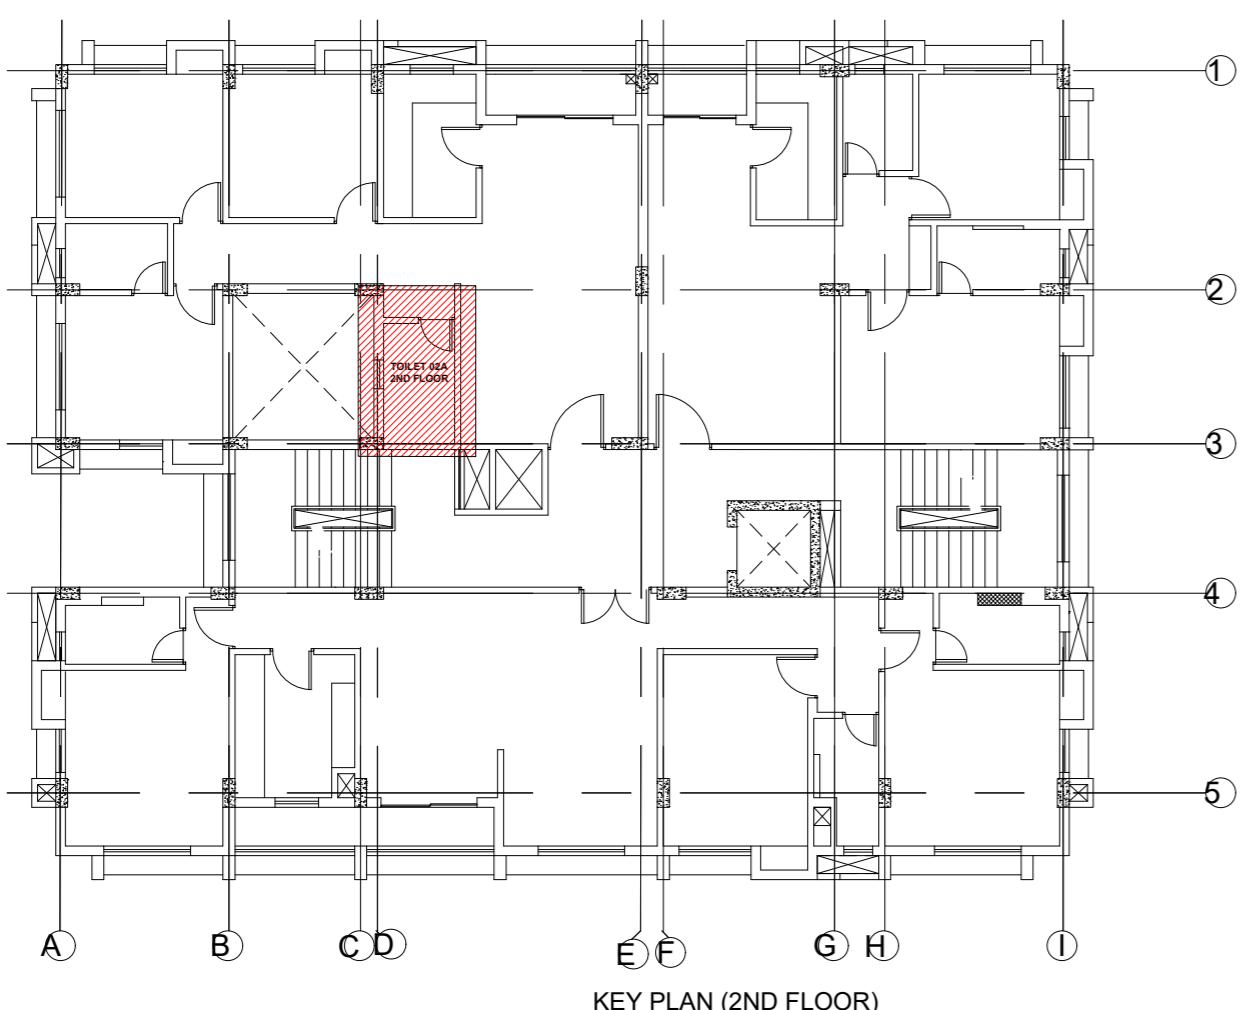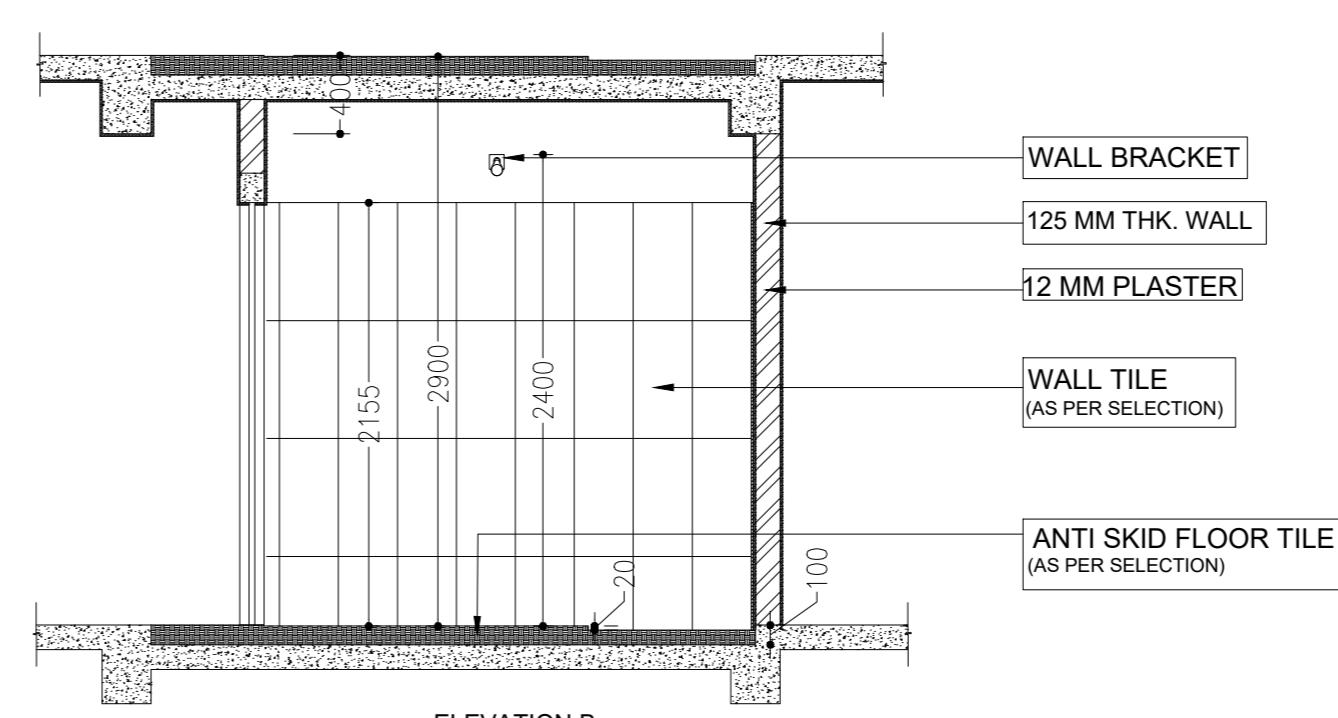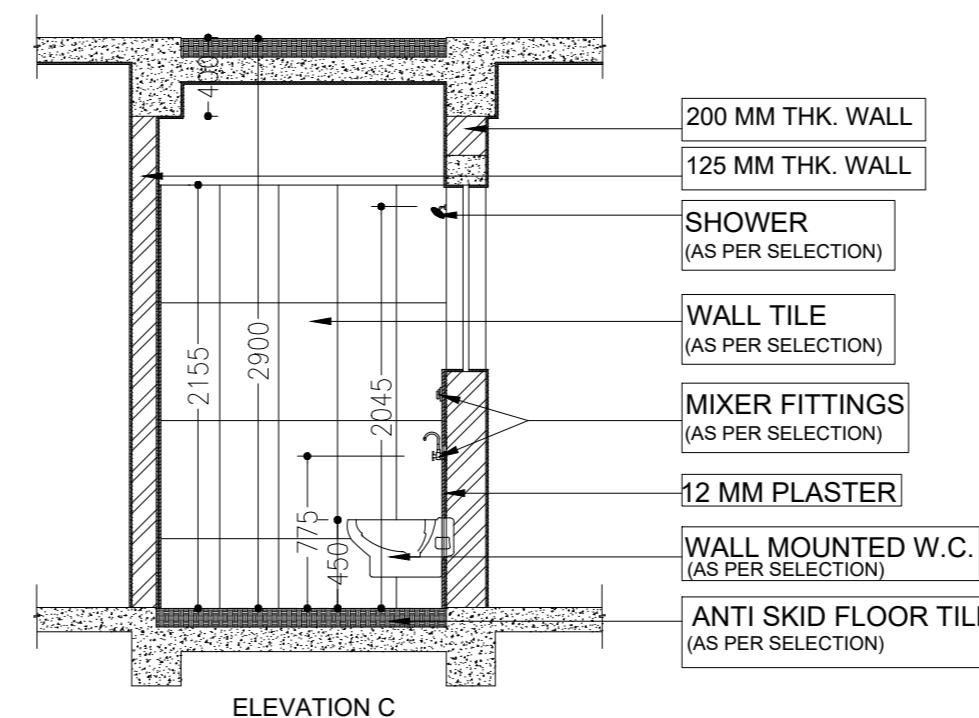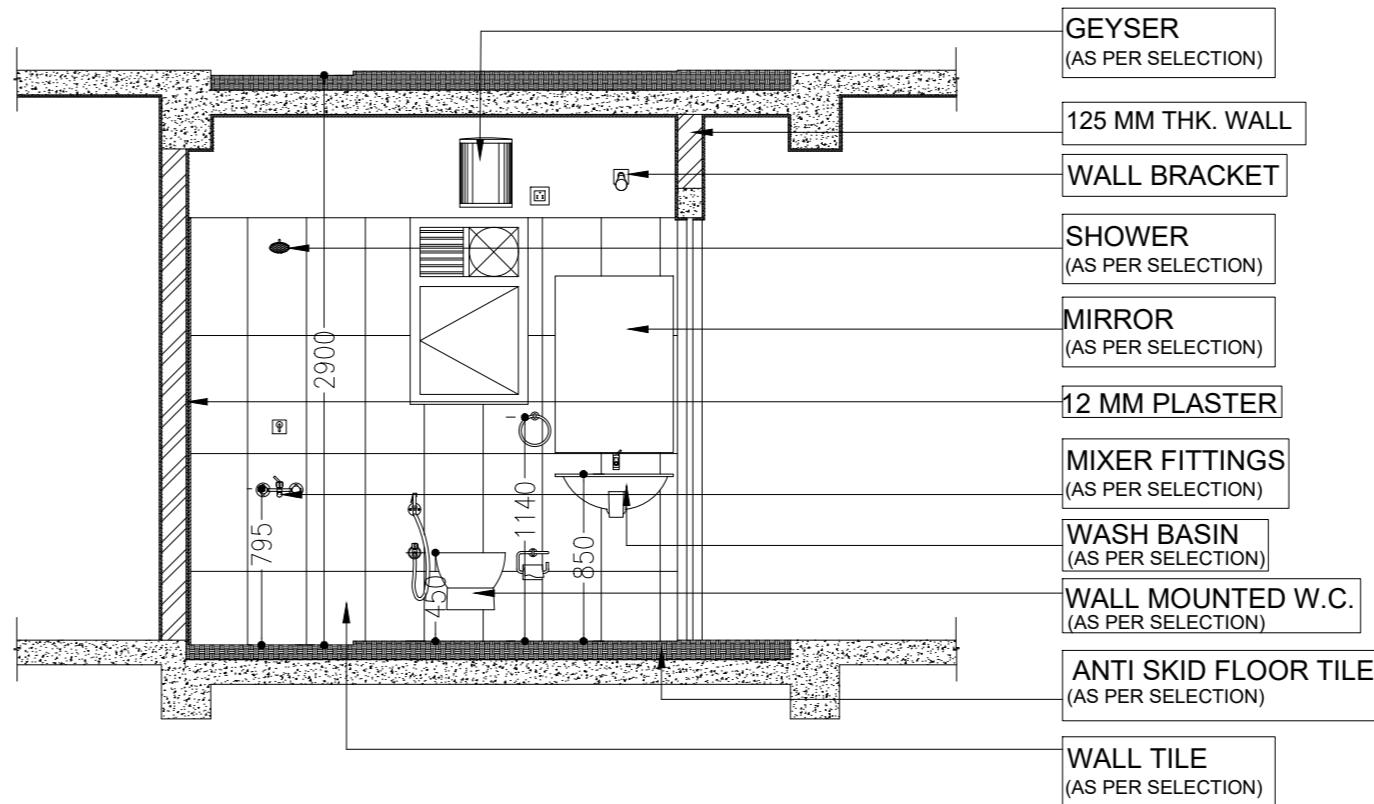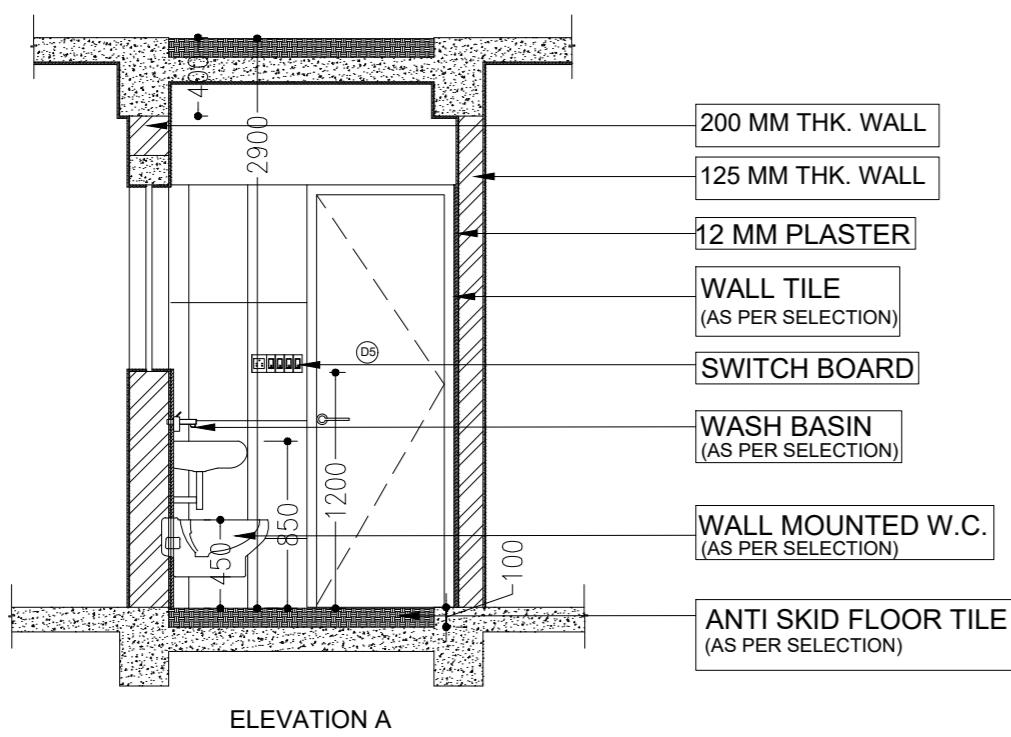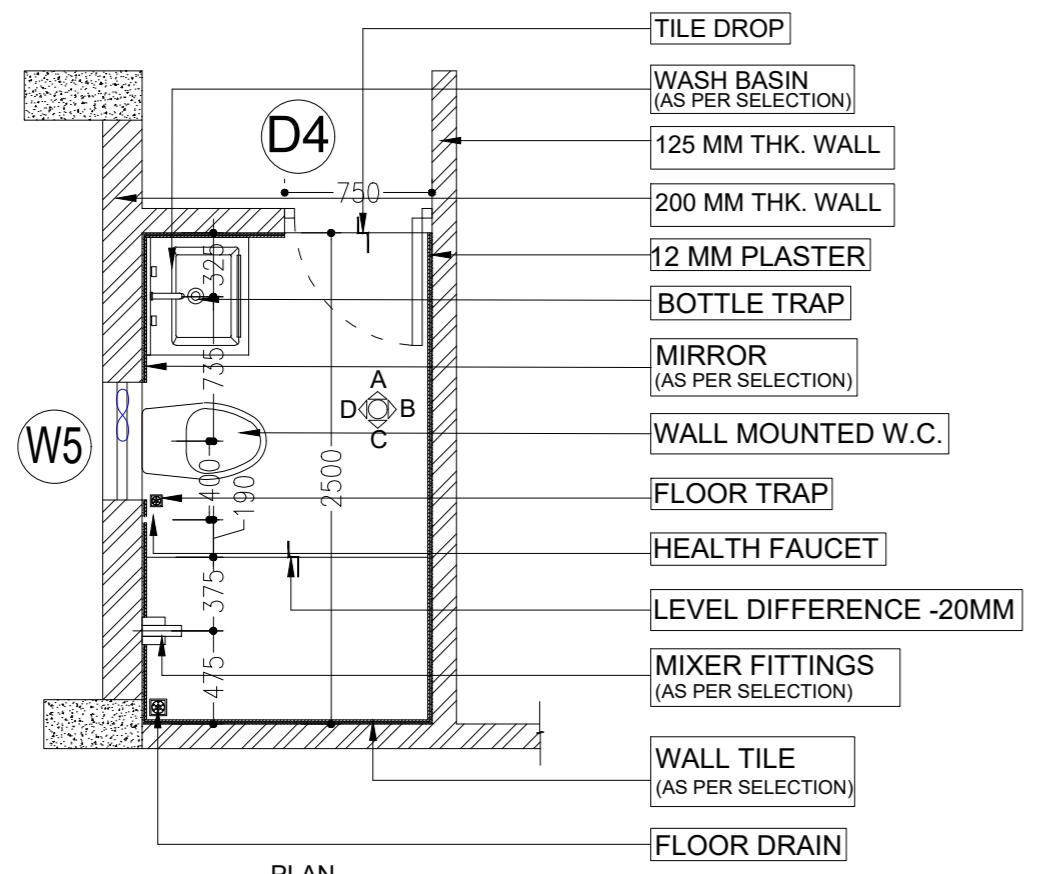

SIGNATURE OF ARCHITECT

REVISIONS

| DATE | DRAWN BY | CHECKED BY | DESCRIPTION OF THE REVISIONS |
|------|----------|------------|------------------------------|
| | | | |
| | | | |
| | | | |
| | | | |
| | | | |

STRUCTURAL
SPA CONSULTANTS,
34, Rammohan Dutta Road, 2nd floor kol 20

PROJECT:
PROPOSED G+IV STORIED RESIDENTIAL HOUSING COMPLEX FOR KOYLA VIHAR,
PHASE-III, AT MOUZA-MONDALGANTHI, J.L. NO- 06, DAG NO- 273,274,275,276 & 277; KHATIAN NO-190/1 & 992, TOUZI NO - 172, WARD NO- 12, P.S.- BAGUIATI, DIST- 24 PGS(N), UNDER RAJARHAT GOPALPUR MUNICIPALITY.

CLIENT:
SPACE GROUP

PROJECT ARCHITECTS:
Maheswari & Associates
An ISO 9001 : 2008 CERTIFIED ORGANISATION
37A Baker Road, 2nd Floor, Alipore, Kolkata-700027
+91-33-24490323 / 65228584
Website: www.architectcm.com
MUMBAI-KOLKATA-GUWAHATI-SILIGURI

PURPOSE OF RELEASE

GOOD FOR CONSTRUCTION

STAGE: **WORKING**

DIRECTION: **SCALE:** 1:25 UNLESS OTHERWISE SPECIFIED **Current Revision:** **R0**

Start Date: 15-05-20 Issue Date: Last saved Date:

Project Code: **KOL-KV**







Bldg/Block: **BLOCK D**

Floor: **2ND FLOOR**

Drawing title: **TOILET DETAIL**

DRG NO. **MA/AR/KOYLA VIHAR/DETAILS/TOILET-01**

THIS DRAWING IS THE SOLE PROPERTY OF MAHESWARI & ASSOCIATES. IT'S USE FOR ANY PURPOSE OTHER THAN THAT MENTIONED IS TO BE DONE ONLY AFTER PRIOR APPROVAL.

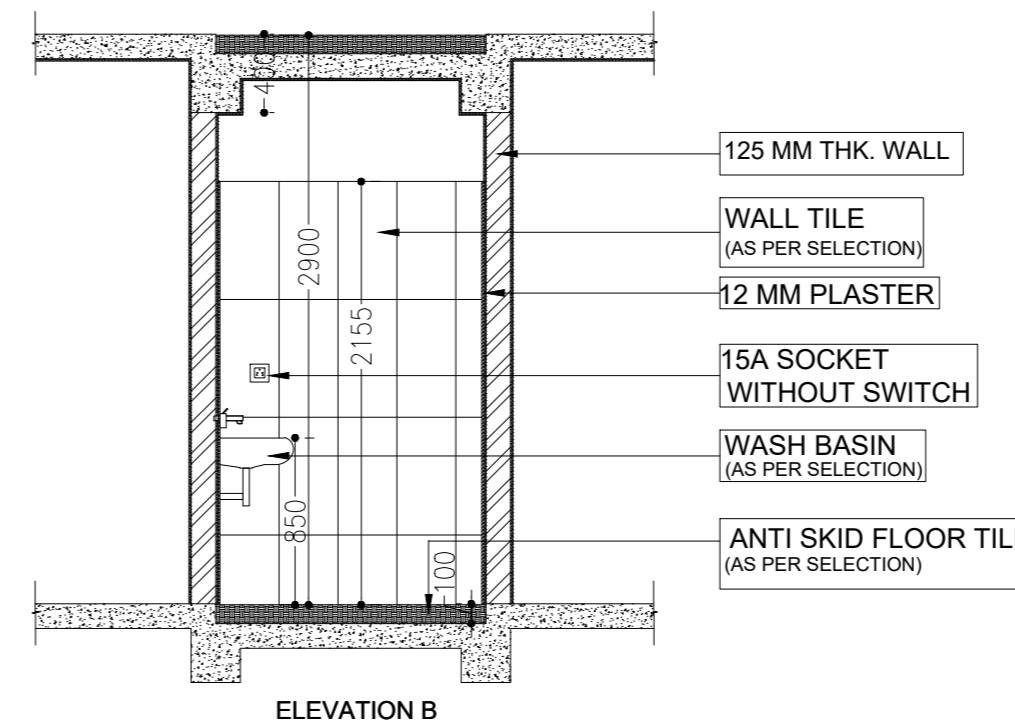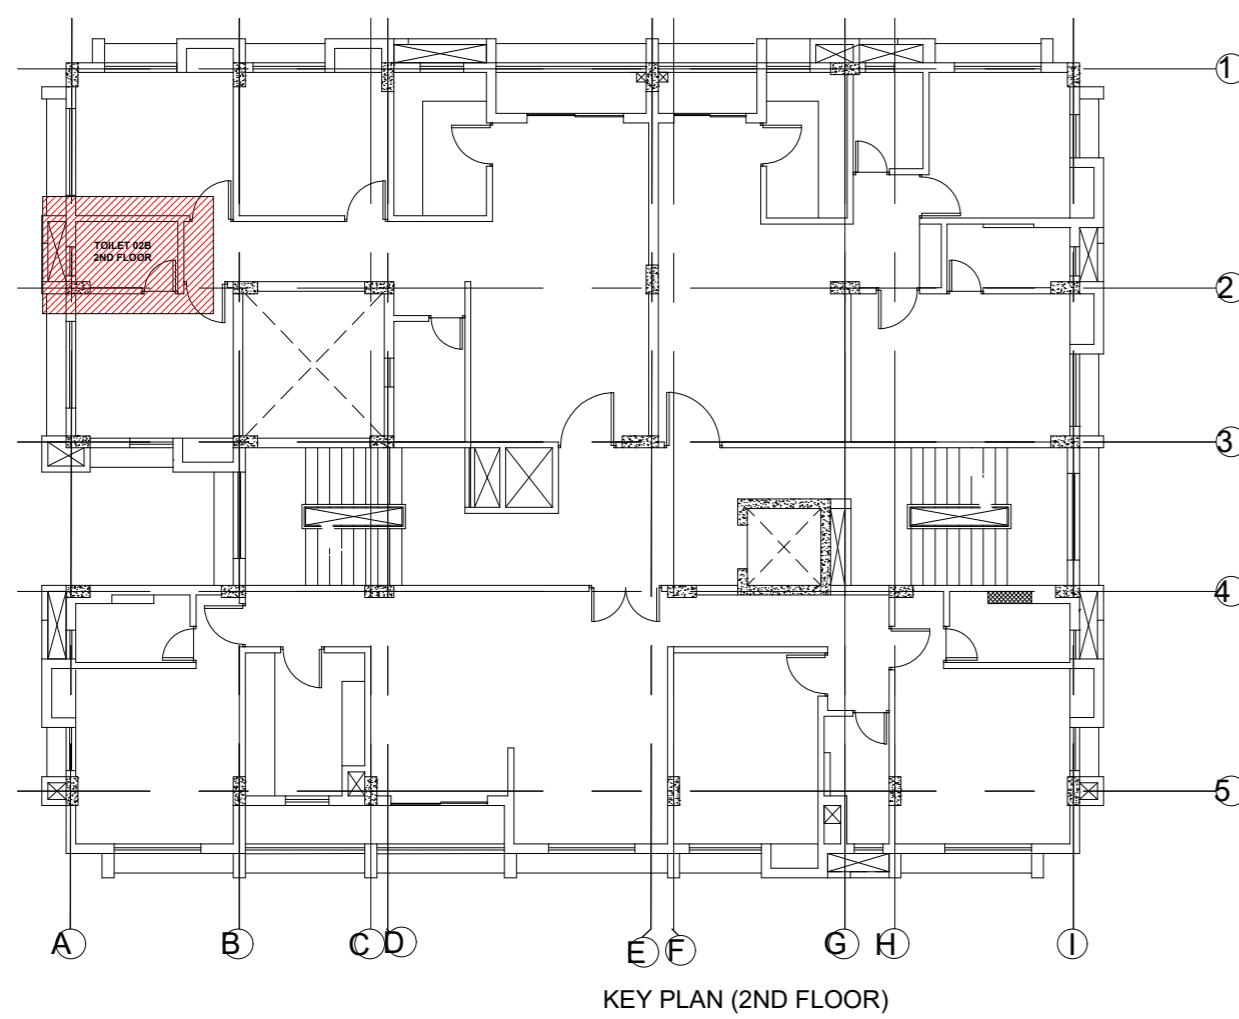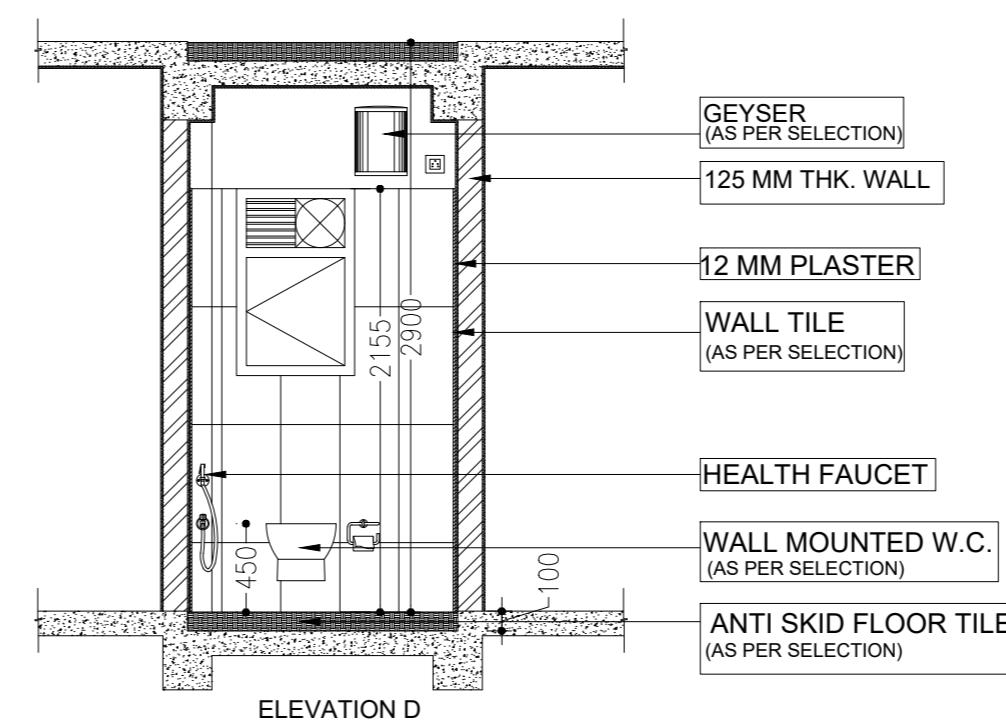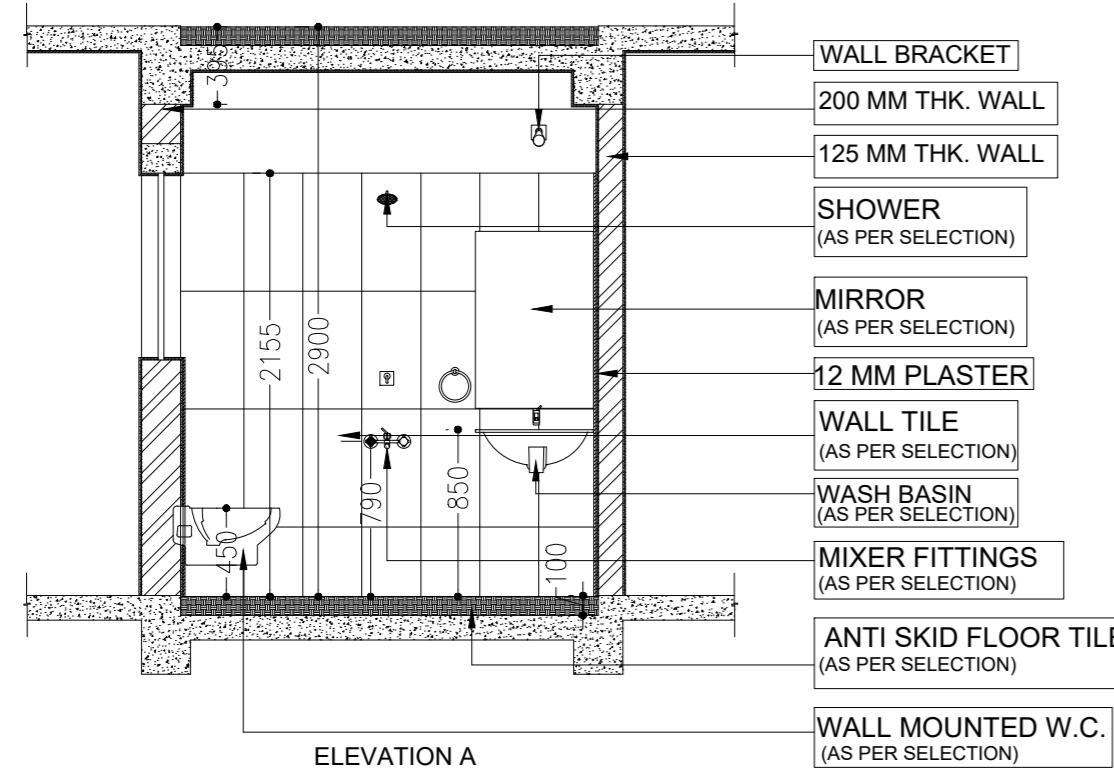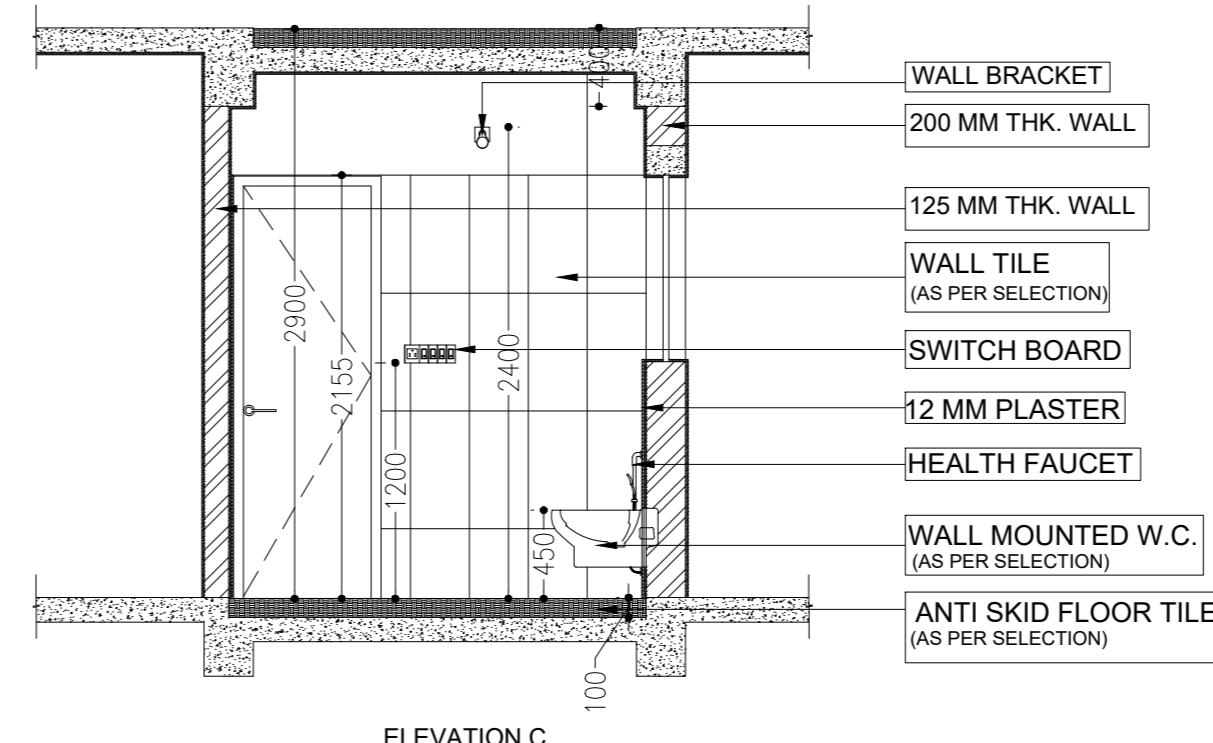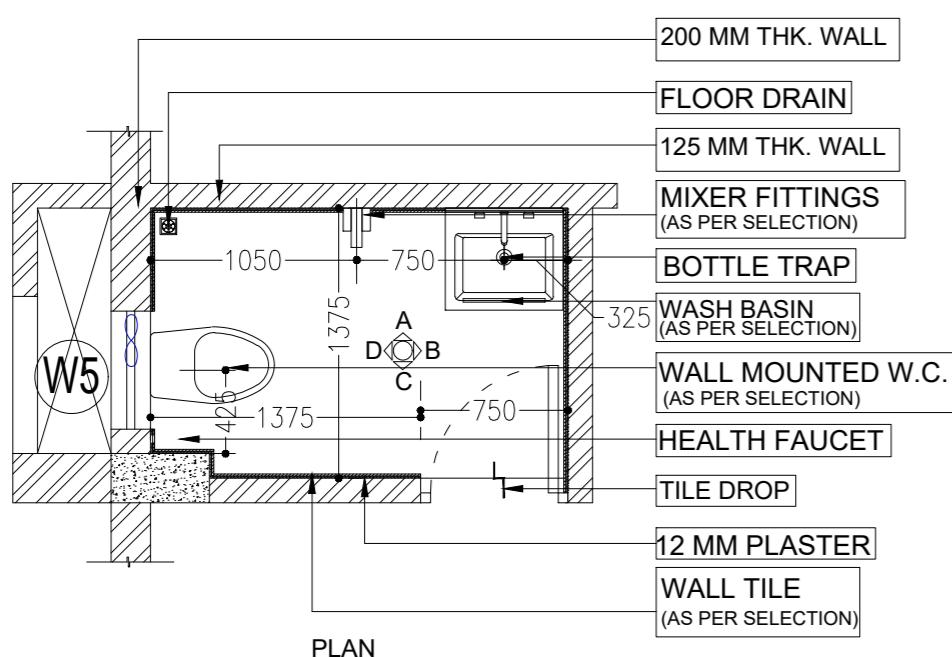

SIGNATURE OF ARCHITECT

REVISIONS

| DATE | DRAWN BY | CHECKED BY | DESCRIPTION OF THE REVISIONS |
|------|----------|------------|------------------------------|
| | | | |
| | | | |
| | | | |
| | | | |

STRUCTURAL
SPA CONSULTANTS,
34, Rammohan Dutta Road, 2nd floor kol 20

PROJECT:
PROPOSED G+IV STORIED RESIDENTIAL HOUSING COMPLEX FOR KOYLA VIHAR,
PHASE-III, AT MOUZA-MONDALGANTHI, J.L. NO- 06, DAG NO- 273,274,275,276 & 277; KHATIAN NO-190/1 & 992, TOUZI NO - 172, WARD NO- 12, P.S.- BAGUIATI, DIST- 24 PGS(N), UNDER RAJARHAT GOPALPUR MUNICIPALITY.

CLIENT:
SPACE GROUP

PROJECT ARCHITECTS:
Maheswari & Associates
An ISO 9001 : 2008 CERTIFIED ORGANISATION
37A Baker Road, 2nd Floor, Alipore, Kolkata-700027
+91-33-24490323 / 65228584
Website: www.architectcm.com
MUMBAI-KOLKATA-GUWAHATI-SILIGURI

PURPOSE OF RELEASE
GOOD FOR CONSTRUCTION

STAGE: **WORKING**

DIRECTION: **SCALE:** 1:25 UNLESS OTHERWISE SPECIFIED **Current Revision:** **R0**

Start Date: **15-05-20** Issue Date: Last saved Date:

Project Code: **KOL-KV**







Bldg/Block: **BLOCK D**

Floor: **2ND FLOOR**

Drawing title: **TOILET DETAIL**

DRG NO. **MA/AR/KOYLA VIHAR/DETAILS/TOILET-02**

THIS DRAWING IS THE SOLE PROPERTY OF MAHESWARI & ASSOCIATES. IT'S USE FOR ANY PURPOSE OTHER THAN THAT MENTIONED IS TO BE DONE ONLY AFTER PRIOR APPROVAL.

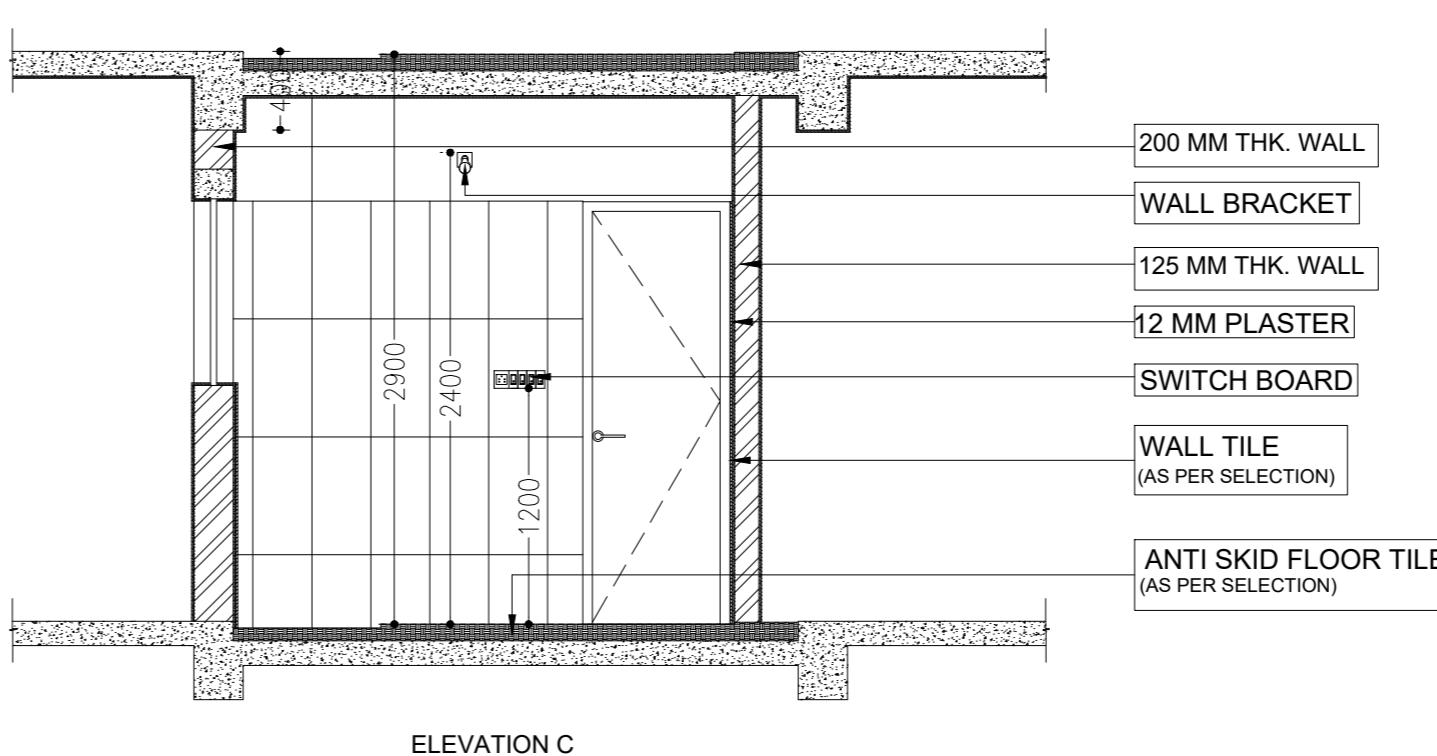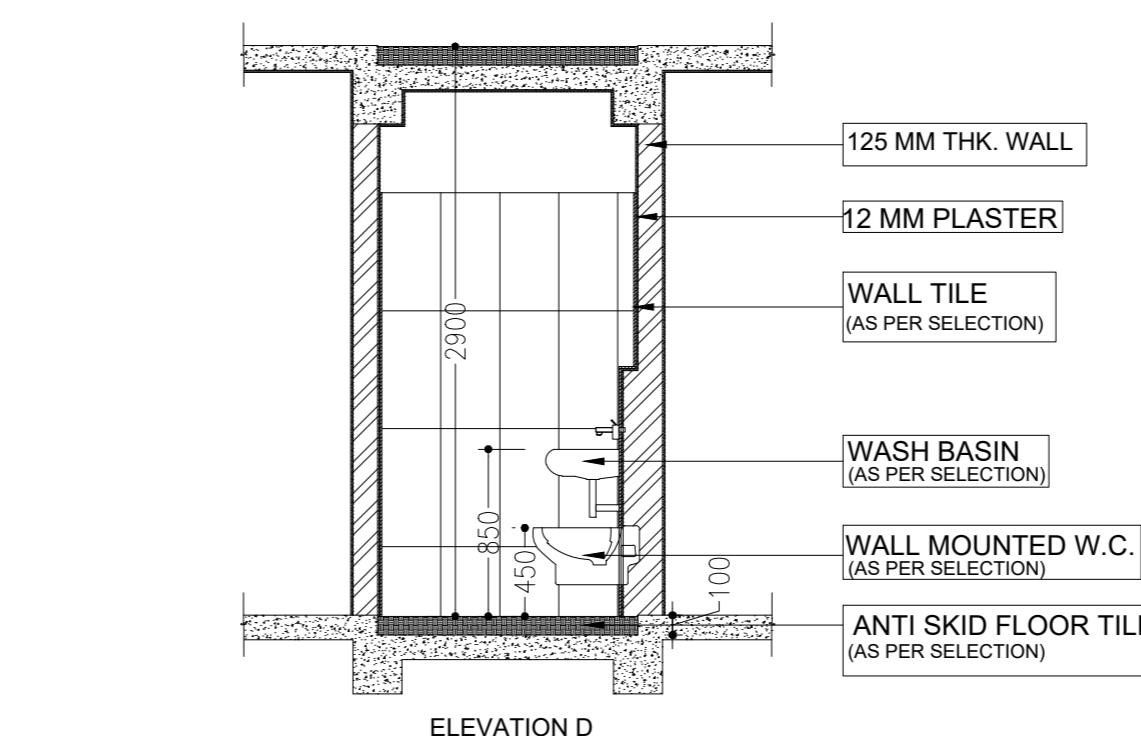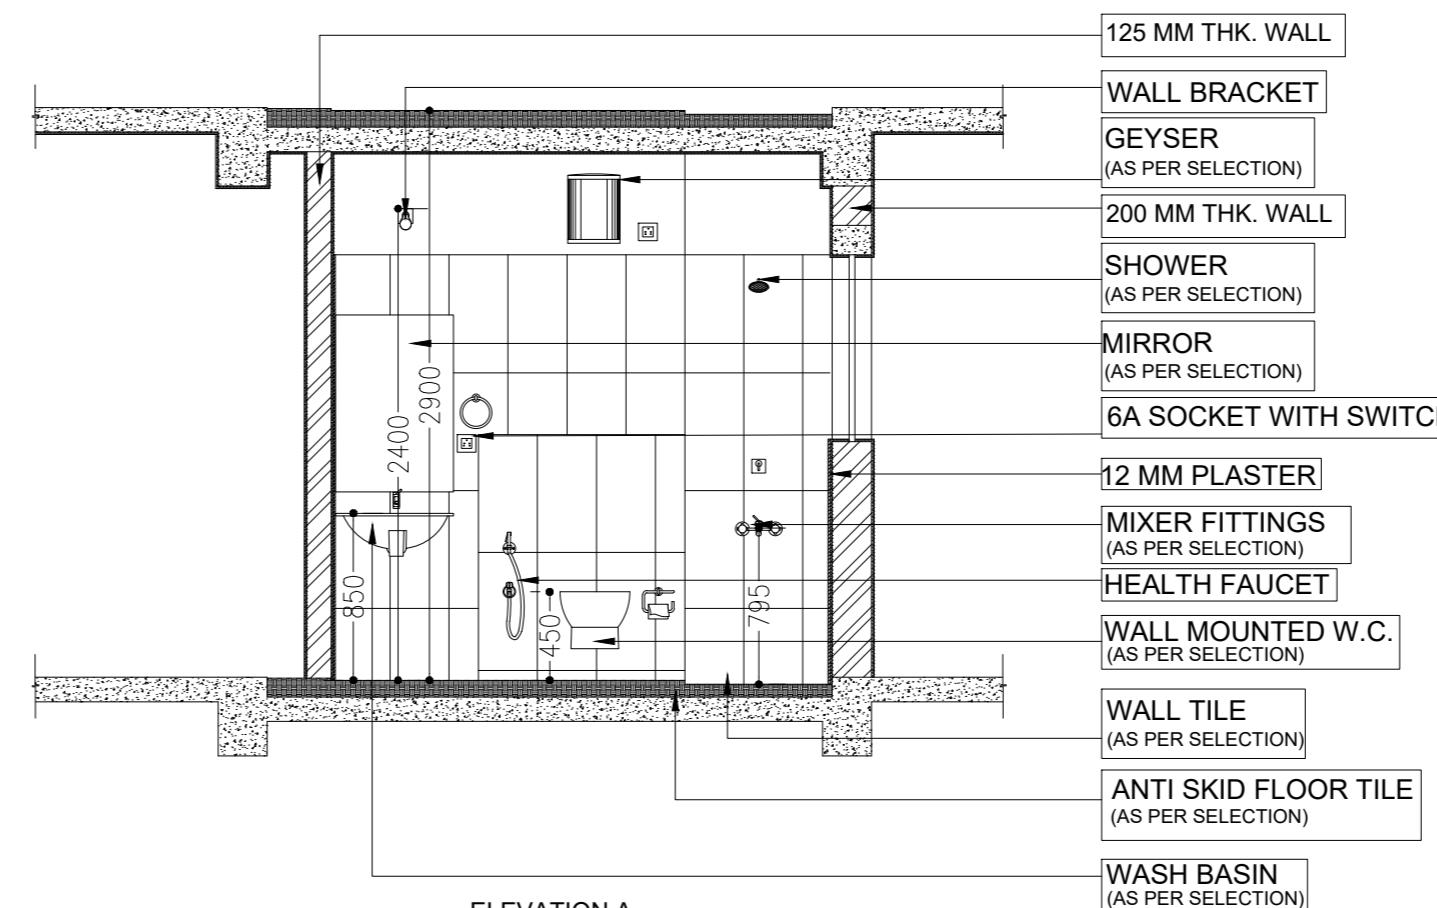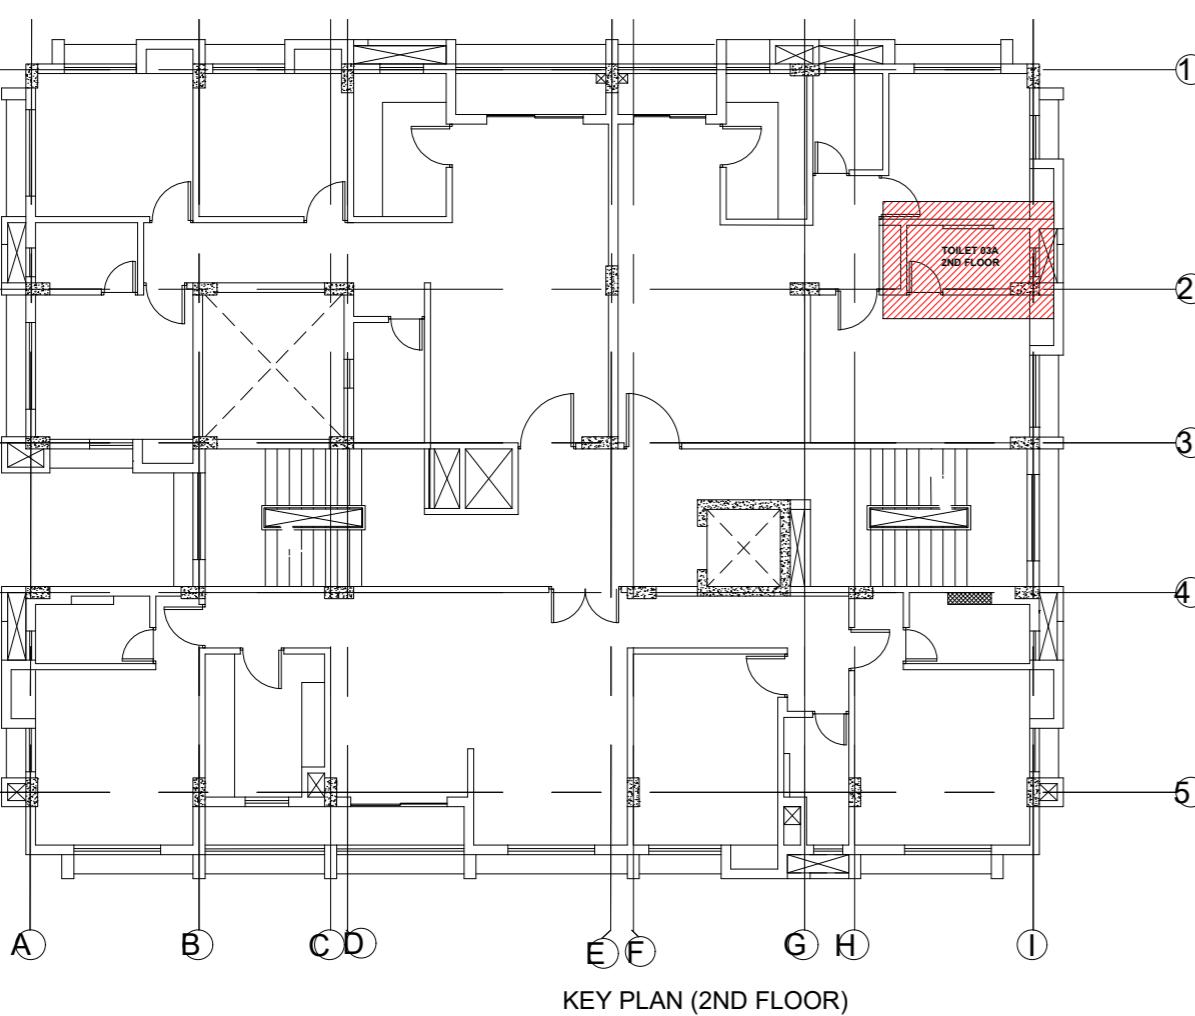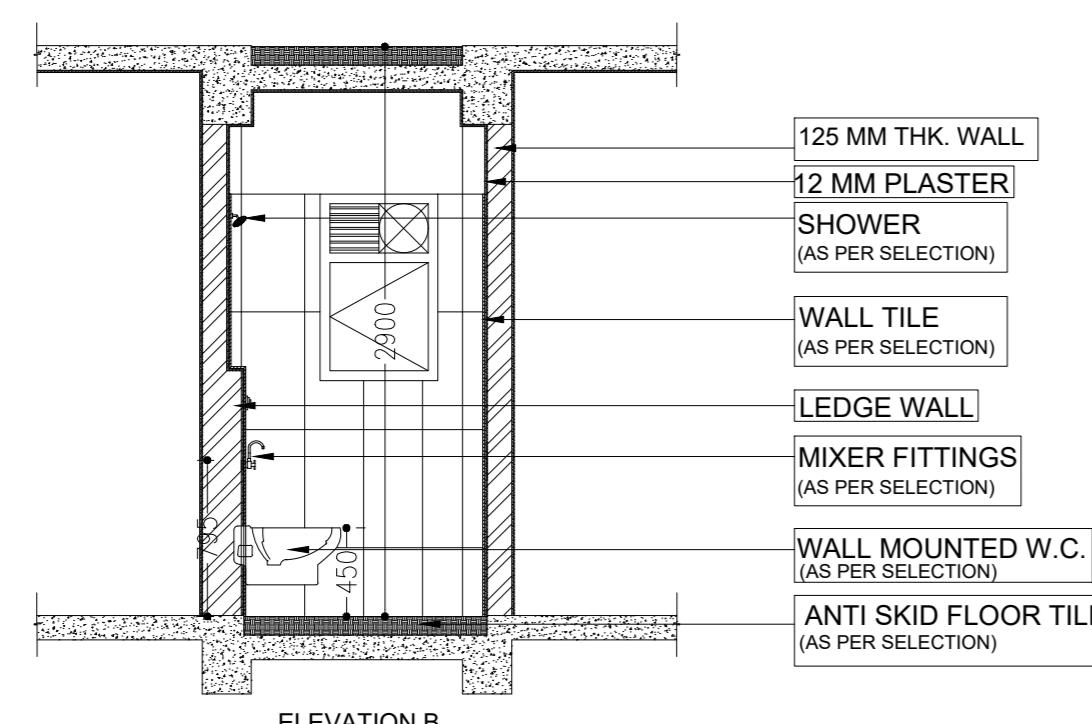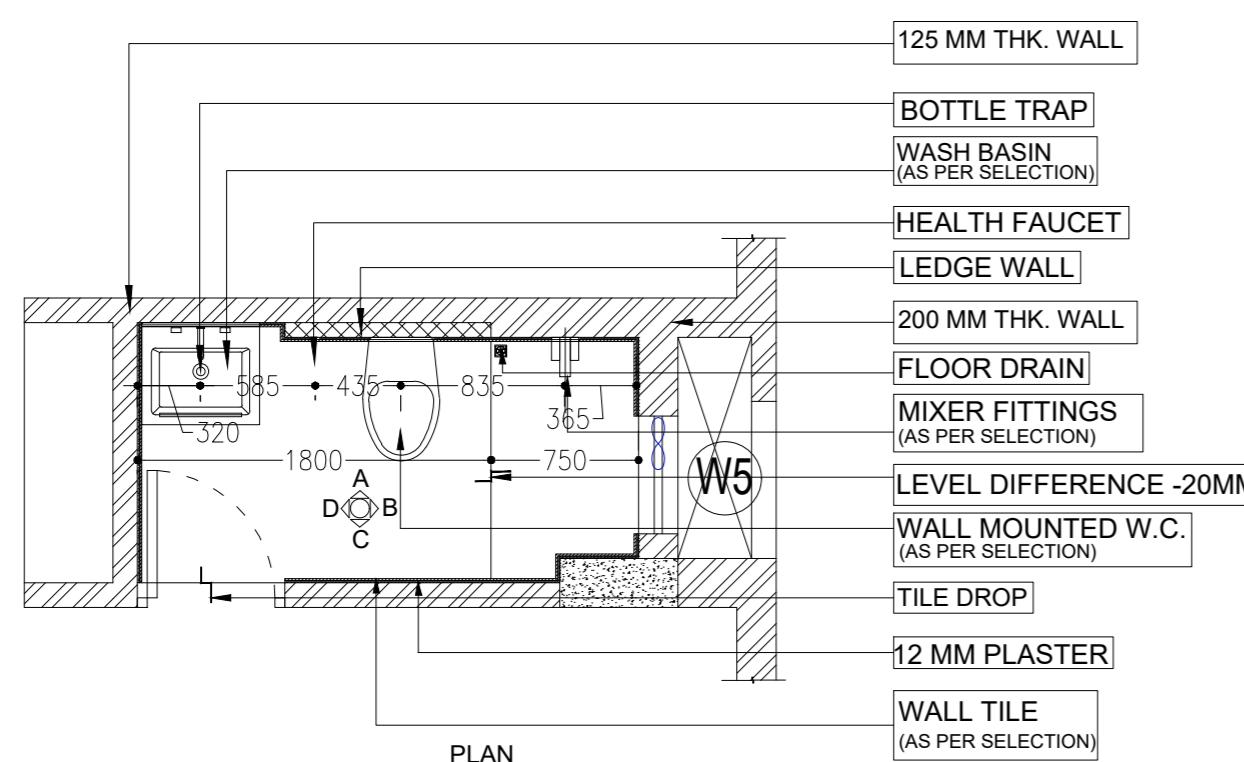

SIGNATURE OF ARCHITECT

REVISIONS

| DATE | DRAWN BY | CHECKED BY | DESCRIPTION OF THE REVISIONS |
|------|----------|------------|------------------------------|
| | | | |
| | | | |
| | | | |
| | | | |

STRUCTURAL
SPA CONSULTANTS,
34, Rammohan Dutta Road, 2nd floor kol 20

PROJECT:
PROPOSED G+IV STORIED RESIDENTIAL HOUSING COMPLEX FOR KOYLA VIHAR,
PHASE-III, AT MOUZA-MONDALGANTHI, J.L. NO- 06, DAG NO- 273,274,275,276 & 277; KHATIAN NO-190/1 & 992, TOUZI NO - 172, WARD NO- 12, P.S.- BAGUIATI, DIST- 24 PGS(N), UNDER RAJARHAT GOPALPUR MUNICIPALITY.

CLIENT:
SPACE GROUP

PROJECT ARCHITECTS:
Maheswari & Associates
An ISO 9001 : 2008 CERTIFIED ORGANISATION
37A Baker Road, 2nd Floor, Alipore, Kolkata-700027
+91-33-24490323 / 65228584
Website: www.architectcm.com
MUMBAI-KOLKATA-GUWAHATI-SILIGURI

PURPOSE OF RELEASE

GOOD FOR CONSTRUCTION

STAGE: WORKING

DIRECTION: SCALE: 1:25 UNLESS OTHERWISE SPECIFIED Current Revision: R0

Start Date: 15-05-20 Issue Date: Last saved Date:

Project Code: KOL-KV







Bldg/Block: BLOCK D

Floor: 2ND FLOOR


Drawing title: TOILET DETAIL

DRG NO. MA/AR/KOYLA VIHAR/DETAILS/TOILET-03


THIS DRAWING IS THE SOLE PROPERTY OF MAHESWARI & ASSOCIATES. IT'S USE FOR ANY PURPOSE OTHER THAN THAT MENTIONED IS TO BE DONE ONLY AFTER PRIOR APPROVAL.

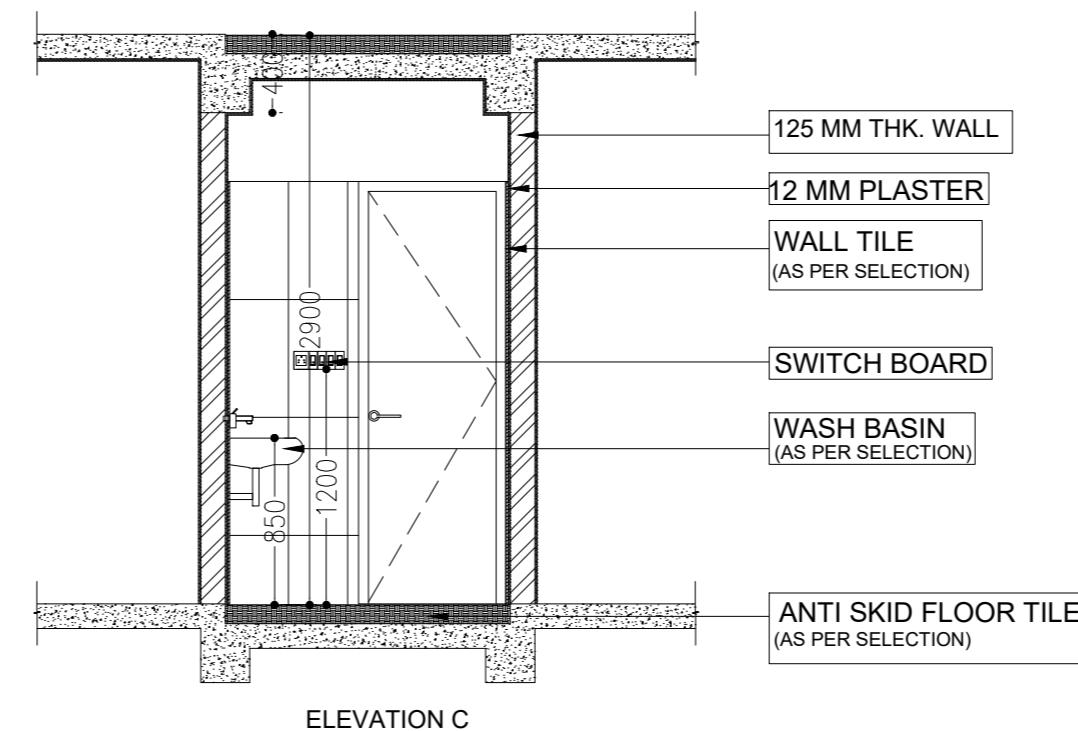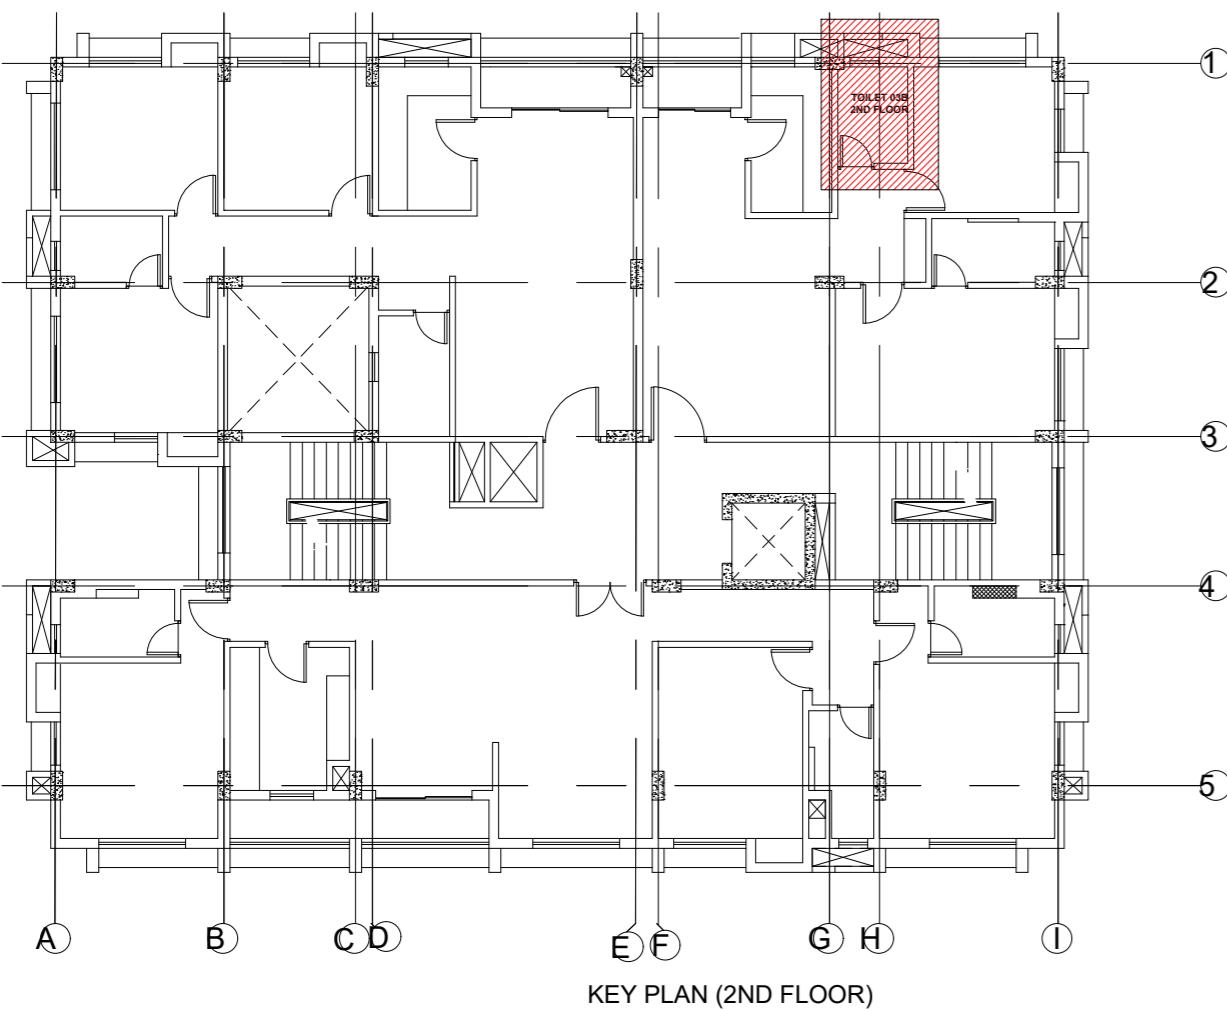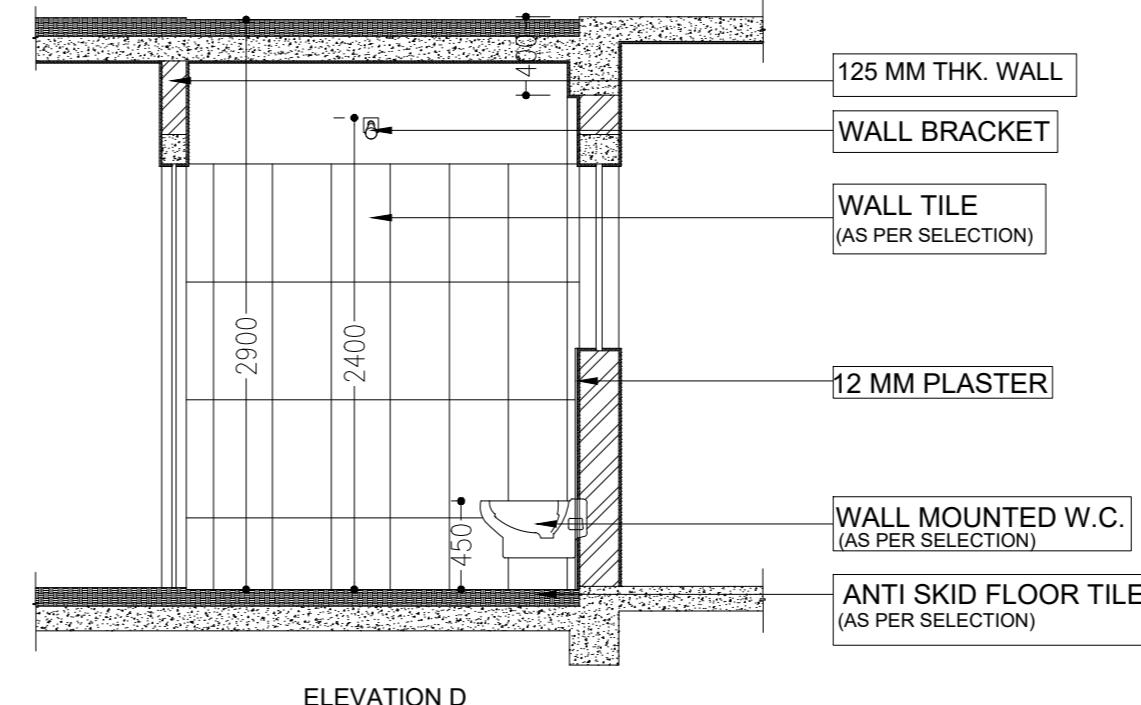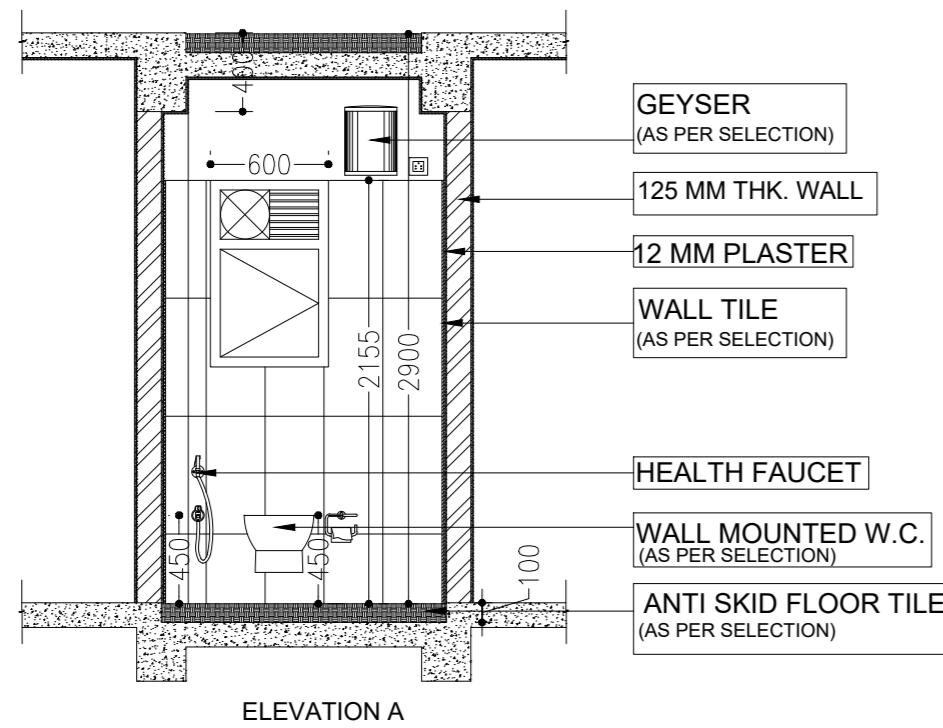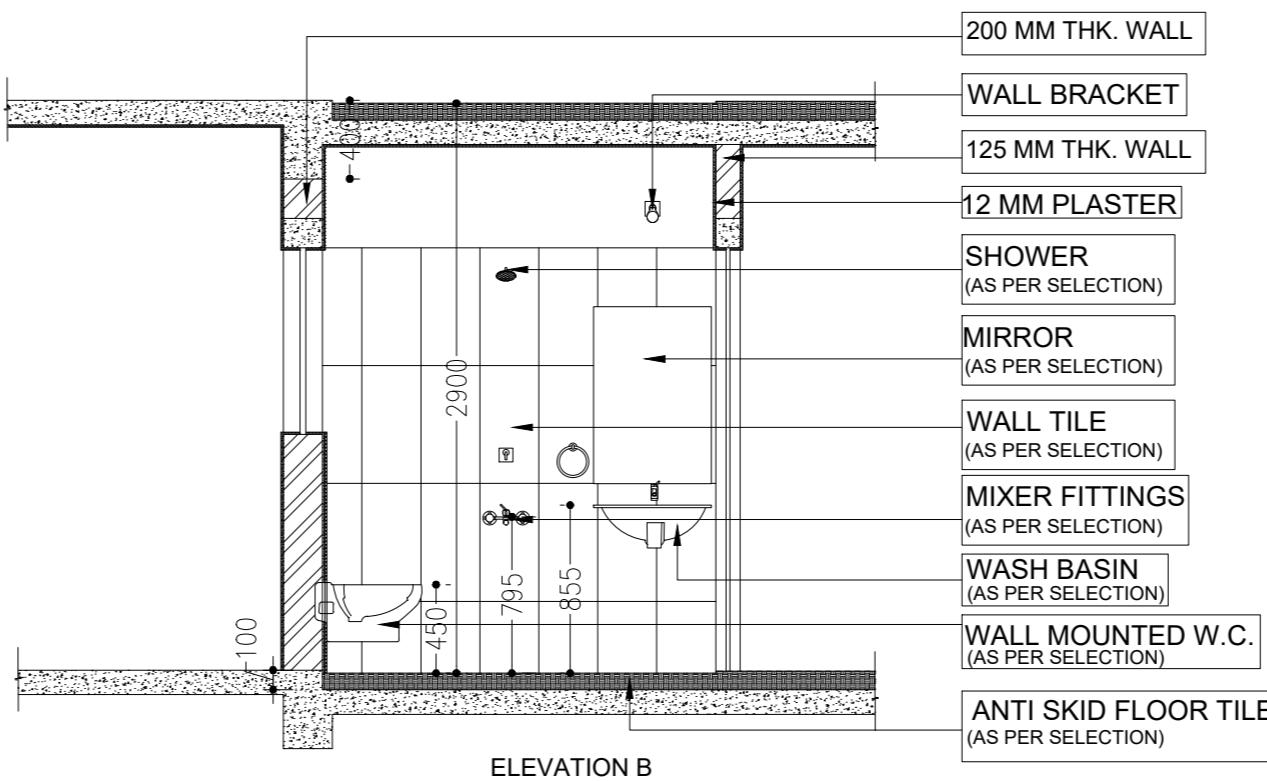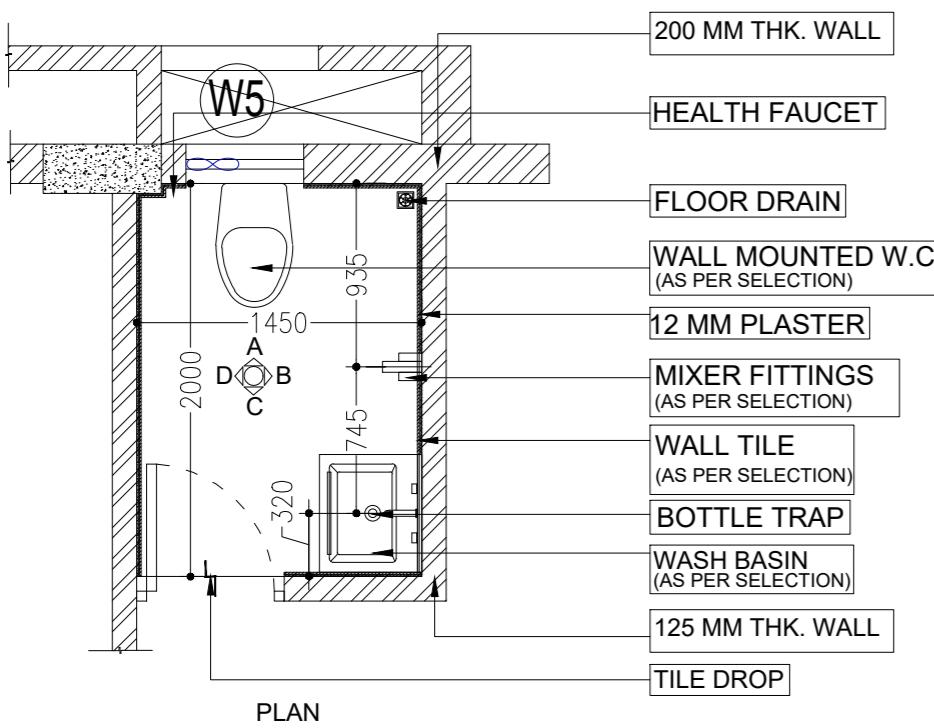


| DATE | DRAWN BY | CHECKED BY | DESCRIPTION OF THE REVISIONS |
|---|--|---|---------------------------------------|
| | | | |
| | | | |
| | | | |
| | | | |
| | | | |
| STRUCTURAL SPA CONSULTANTS, 34, Rammohan Dutta Road, 2nd floor kol 20 | | | |
| PROJECT: PROPOSED G+IV STORIED RESIDENTIAL HOUSING COMPLEX FOR KOYLA VIHAR, PHASE-III, AT MOUZA-MONDALGANTHI, J.L. NO- 06, DAG NO- 273,274,275,276 & 277; KHTIAN NO-190/1 & 992, TOUZI NO - 172, WARD NO- 12, P.S.- BAGUIATI, DIST- 24 PGS(N), UNDER RAJARHAT GOPALPUR MUNICIPALITY. | | | |
| CLIENT: SPACE GROUP | | | |
| PROJECT ARCHITECTS:  Maheswari & Associates An ISO 9001 : 2008 CERTIFIED ORGANISATION 37A Baker Road, 2nd Floor, Alipore, Kolkata-700027 +91-33-24490323 / 65228584 Website: www.architectm.com MUMBAI-KOLKATA-GUWAHATI-SILIGURI | | | |
| PURPOSE OF RELEASE GOOD FOR CONSTRUCTION | | | |
| STAGE: | | WORKING | |
| DIRECTION: | | SCALE: 1:25 UNLESS OTHERWISE SPECIFIED | Current Revision: R0 |
| Start Date: | | Issue Date: | Last saved Date: |
| 15-05-20 | | | |
| Project Code: | | KOL-KV | |
| Bldng/Block: | | BLOCK D | |
| Floor: | | 2ND FLOOR | |
| Drawing title: | TOILET DETAIL | | |
| DRG NO. | MA/AR/KOYLA VIHAR/DETAILS/TOILET-04 | | |

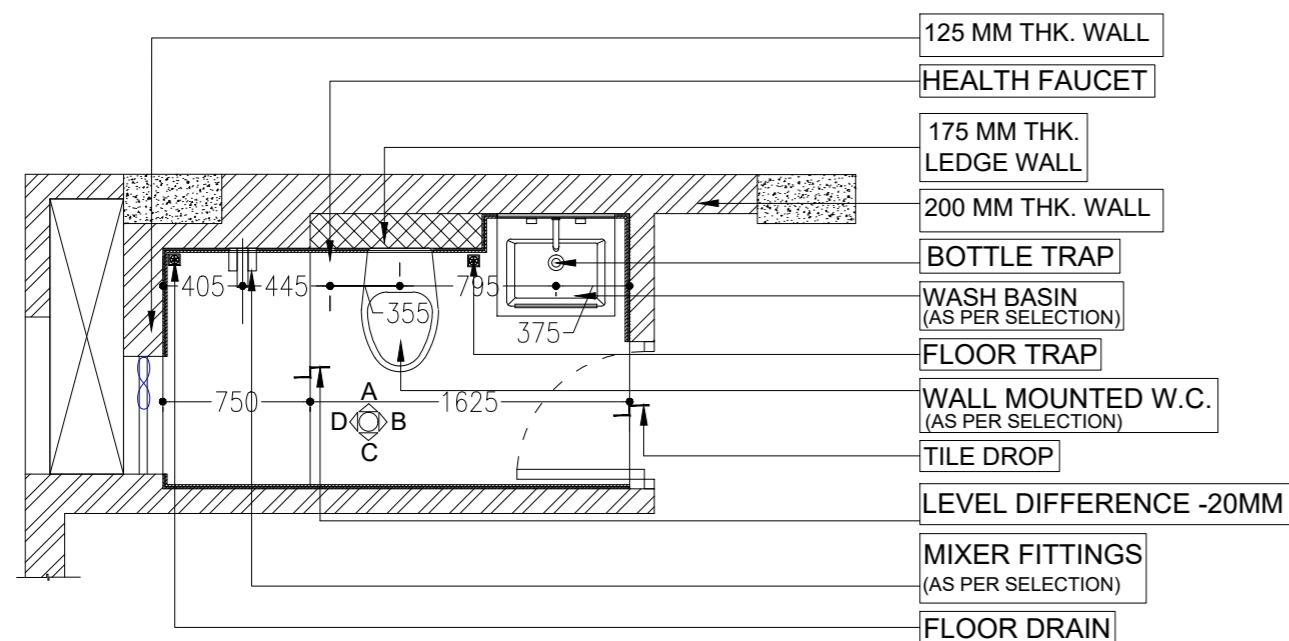


PLAN

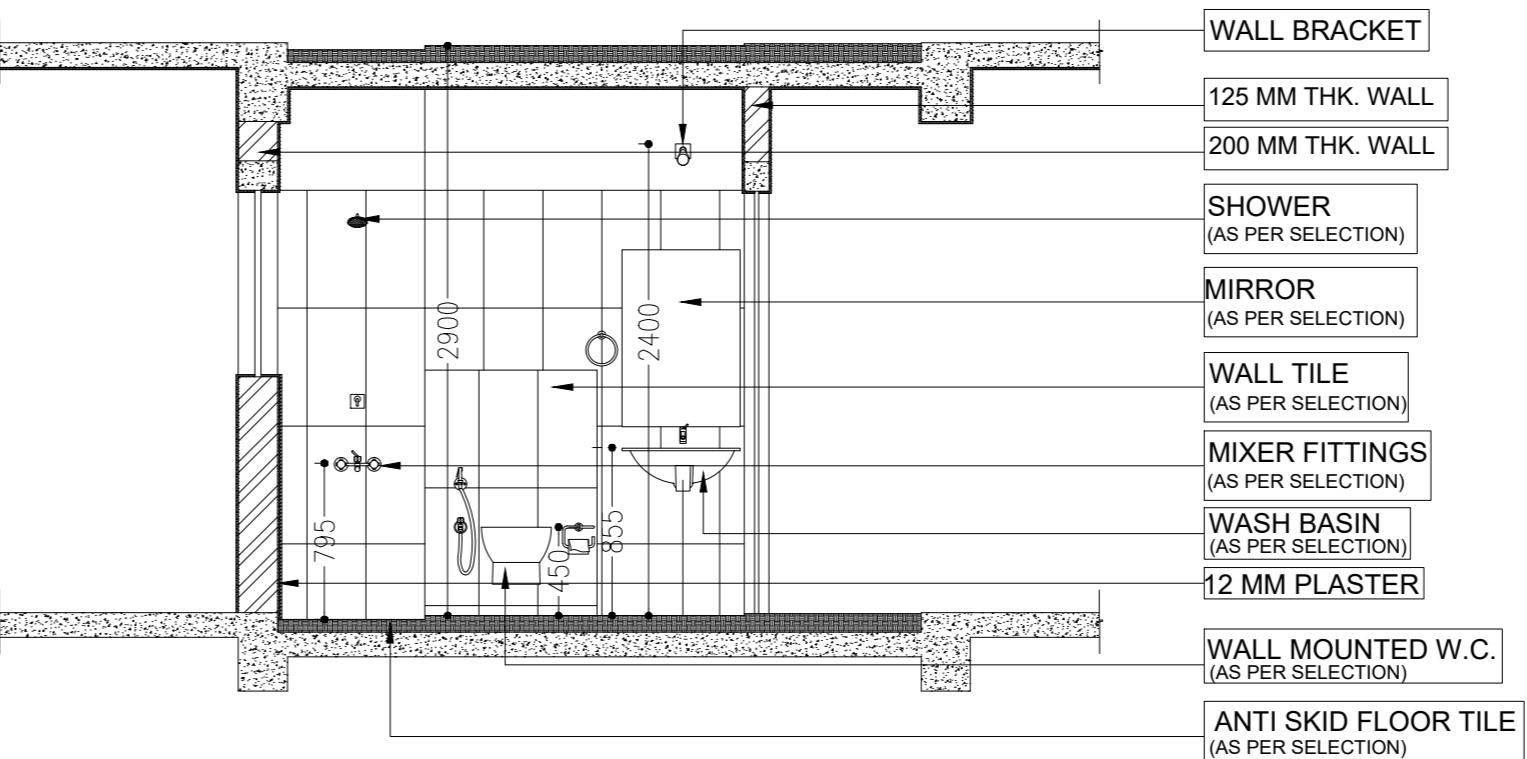


ELEVATION A

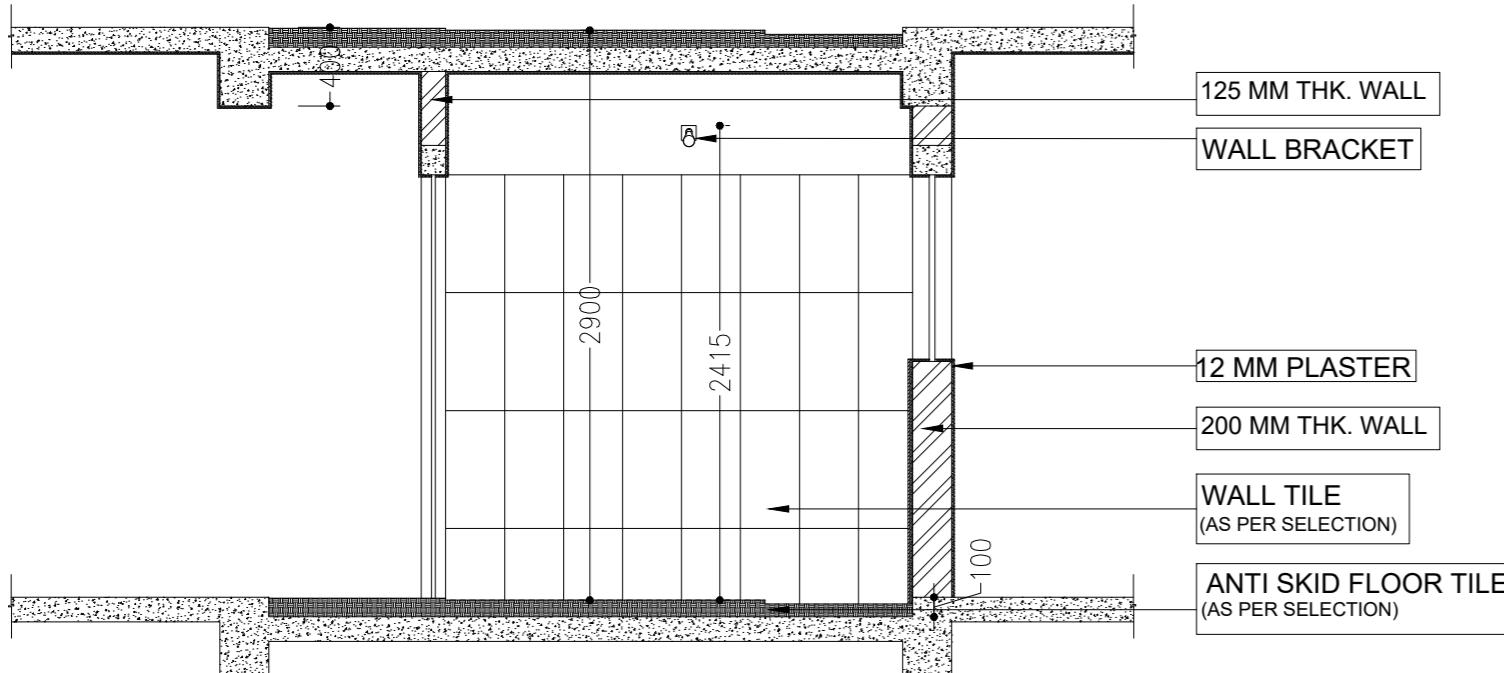


ELEVATION C

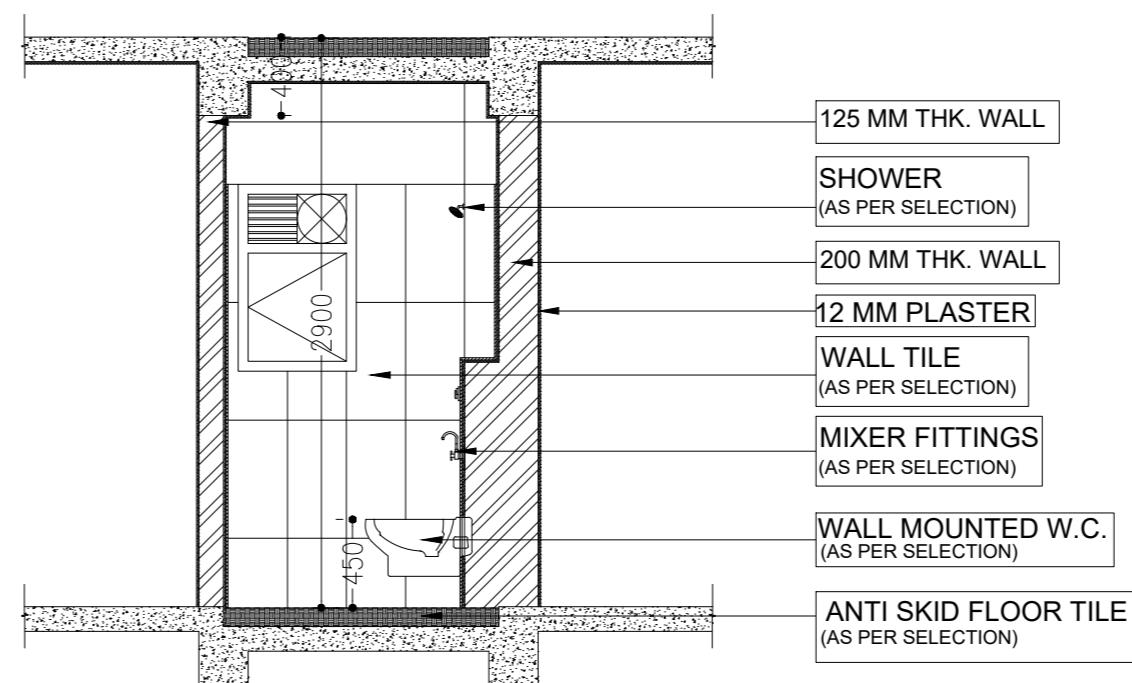

ELEVATION D

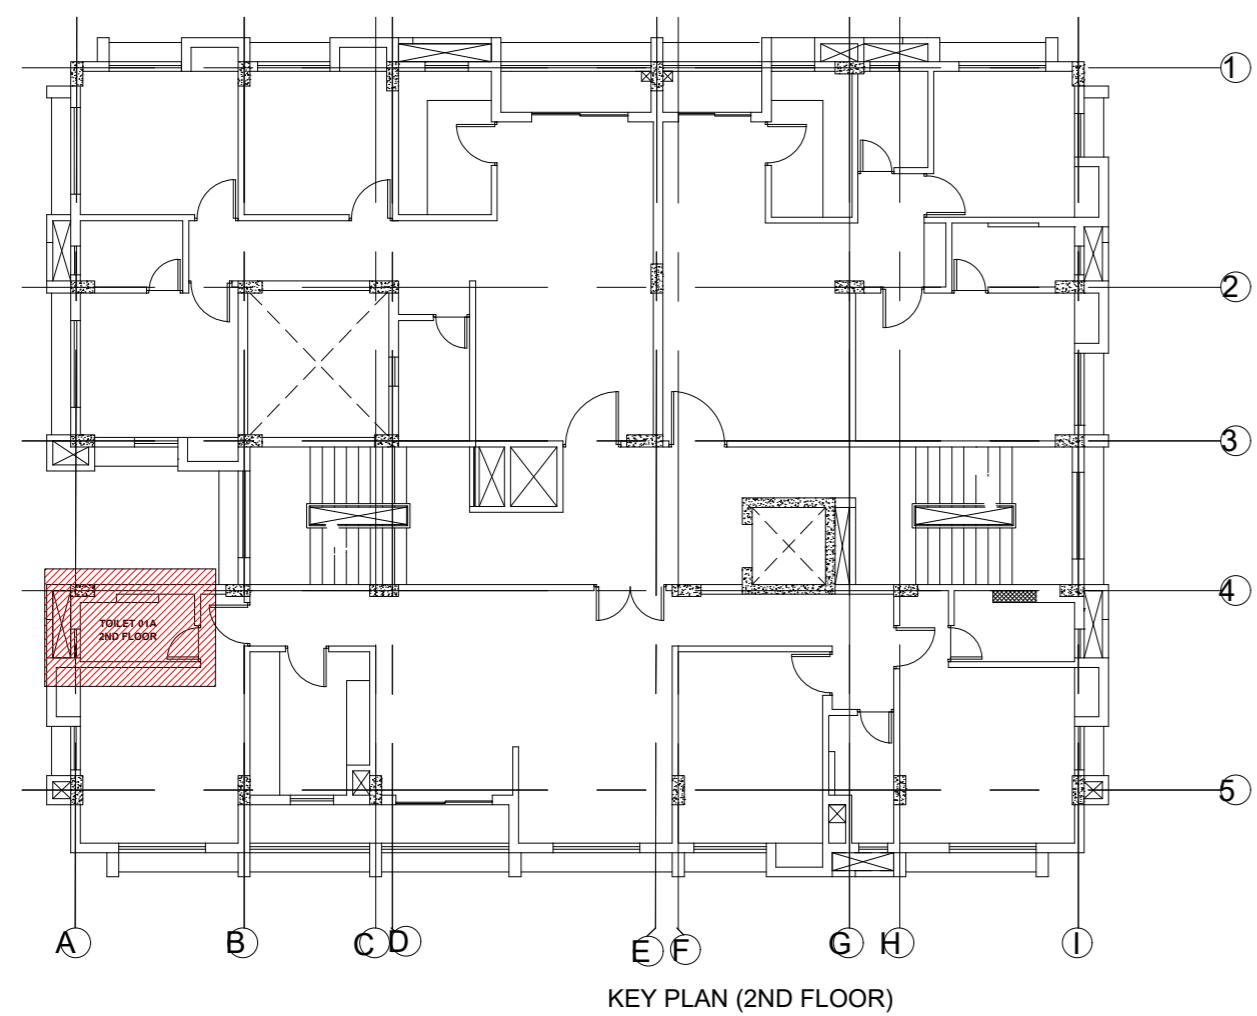


KEY PLAN (2ND FLOOR)

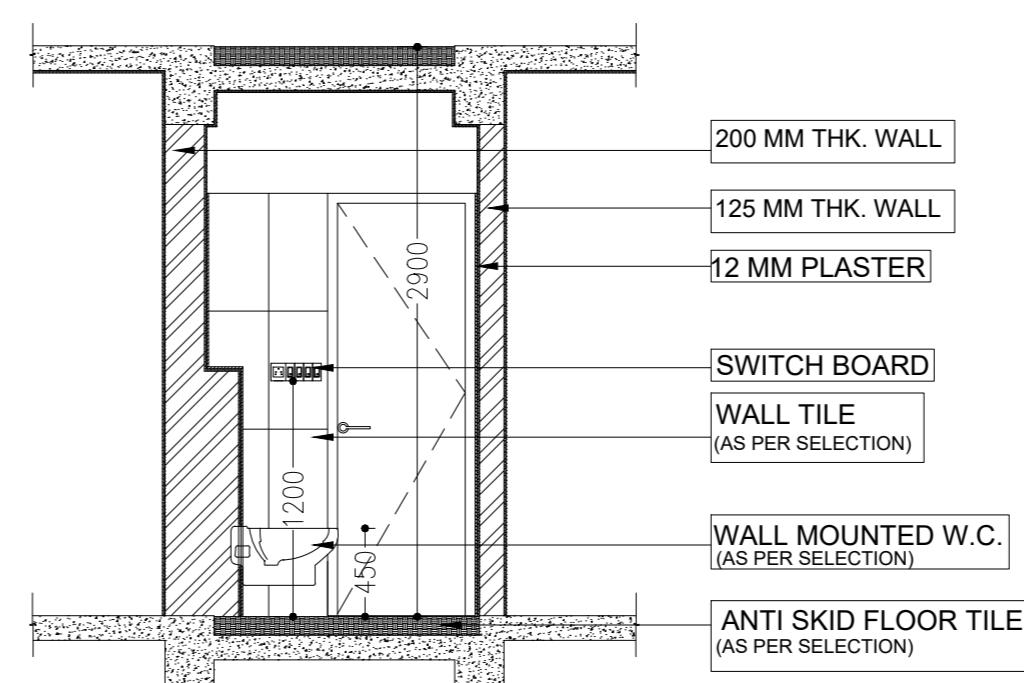


ELEVATION


| DATE | DRAWN BY | CHECKED BY | DESCRIPTION OF THE REVISIONS |
|--|--|-------------------|------------------------------|
| | | | |
| | | | |
| | | | |
| | | | |
| | | | |
| STRUCTURAL SPA CONSULTANTS, 34, Rammohan Dutta Road, 2nd floor kol 20 | | | |
| PROJECT: PROPOSED G+IV STORIED RESIDENTIAL HOUSING COMPLEX FOR KOYLA VIHAR, PHASE-III, AT MOUZA-MONDALGANTHI, J.L. NO- 06, DAG NO- 273,274,275,276 & 277; KHTIAN NO-190/1 & 992, TOUZI NO - 172, WARD NO- 12, P.S.- BAGUIATI, DIST- 24 PGS(N), UNDER RAJARHAT GOPALPUR MUNICIPALITY. | | | |
| CLIENT: SPACE GROUP | | | |
| PROJECT ARCHITECTS:  Maheswari & Associates An ISO 9001 : 2008 CERTIFIED ORGANISATION 37A Baker Road, 2nd Floor, Alipore, Kolkata-700027 +91-33-24490323 / 65228584 Website: www.architectm.com MUMBAI-KOLKATA-GUWAHATI-SILIGURI | | | |
| PURPOSE OF RELEASE GOOD FOR CONSTRUCTION | | | |
| STAGE: | WORKING | | |
| DIRECTION: | SCALE: 1:25 UNLESS OTHERWISE SPECIFIED | Current Revision: | R0 |
| Start Date: | Issue Date: | Last saved Date: | |
| 15-05-20 | | | |
| Project Code: | KOL-KV | | |
| Bldng/Block: | BLOCK D | | |
| Floor: | 2ND FLOOR | | |
| Drawing title: | TOILET DETAIL | | |
| DRG NO. | MA/AR/KOYLA VIHAR/DETAILS/TOILET-05 | | |
| THIS DRAWING IS THE SOLE PROPERTY OF MAHESWARI & ASSOCIATES. IT'S USE FOR ANY PURPOSE OTHER THAN THAT MENTIONED IS TO BE DONE ONLY AFTER PRIOR APPROVAL. | | | |

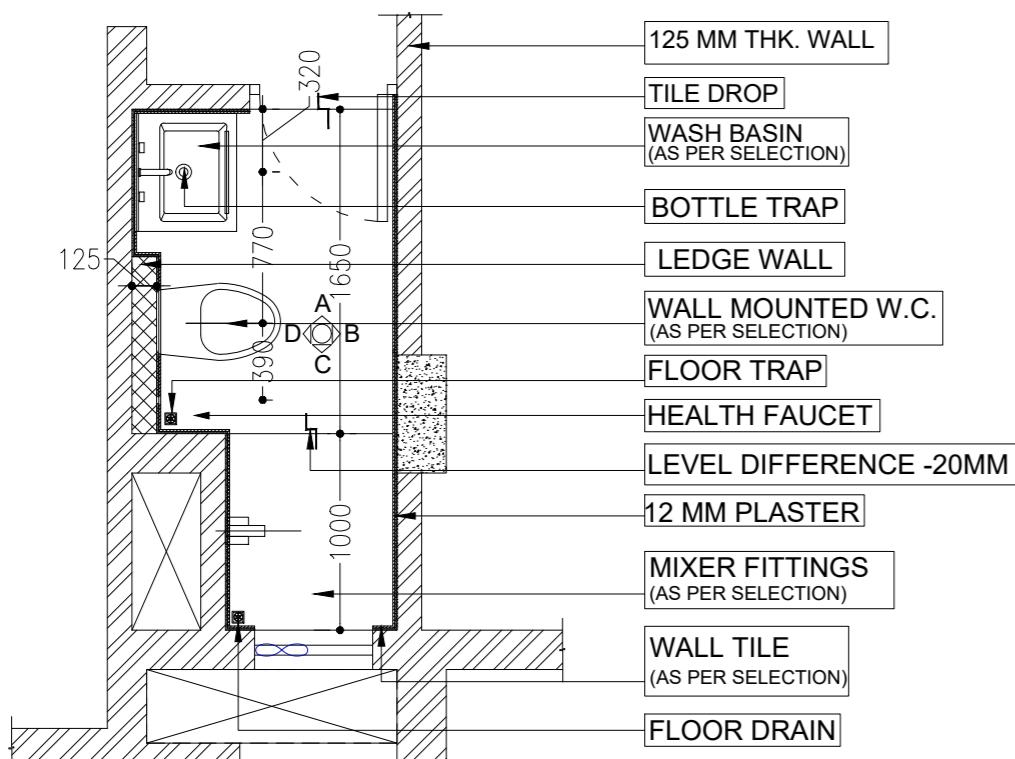


PLAN

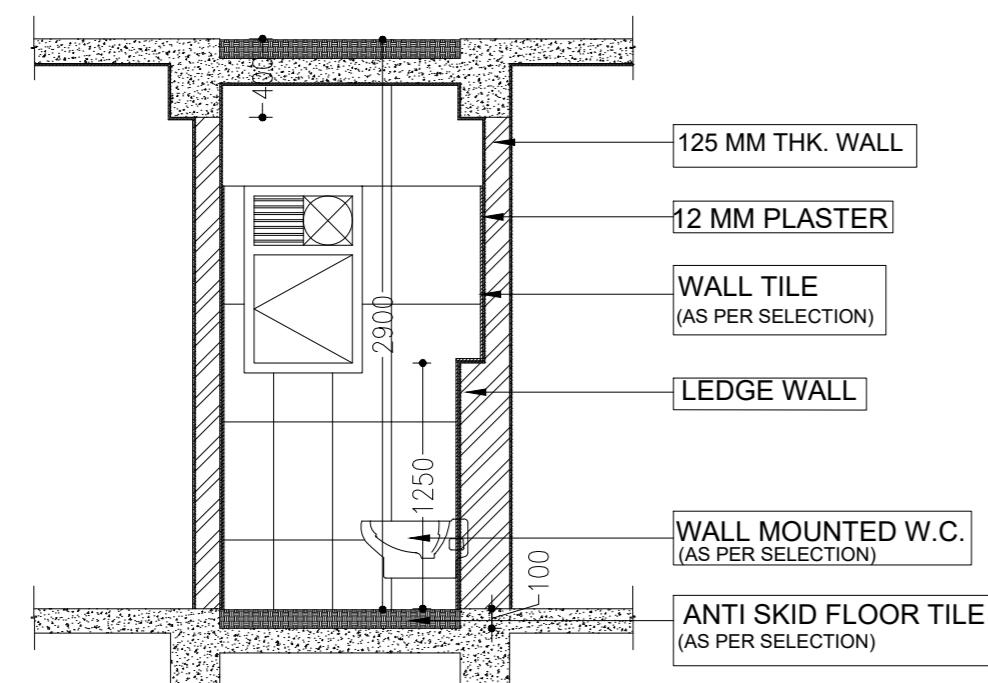


ELEVATION

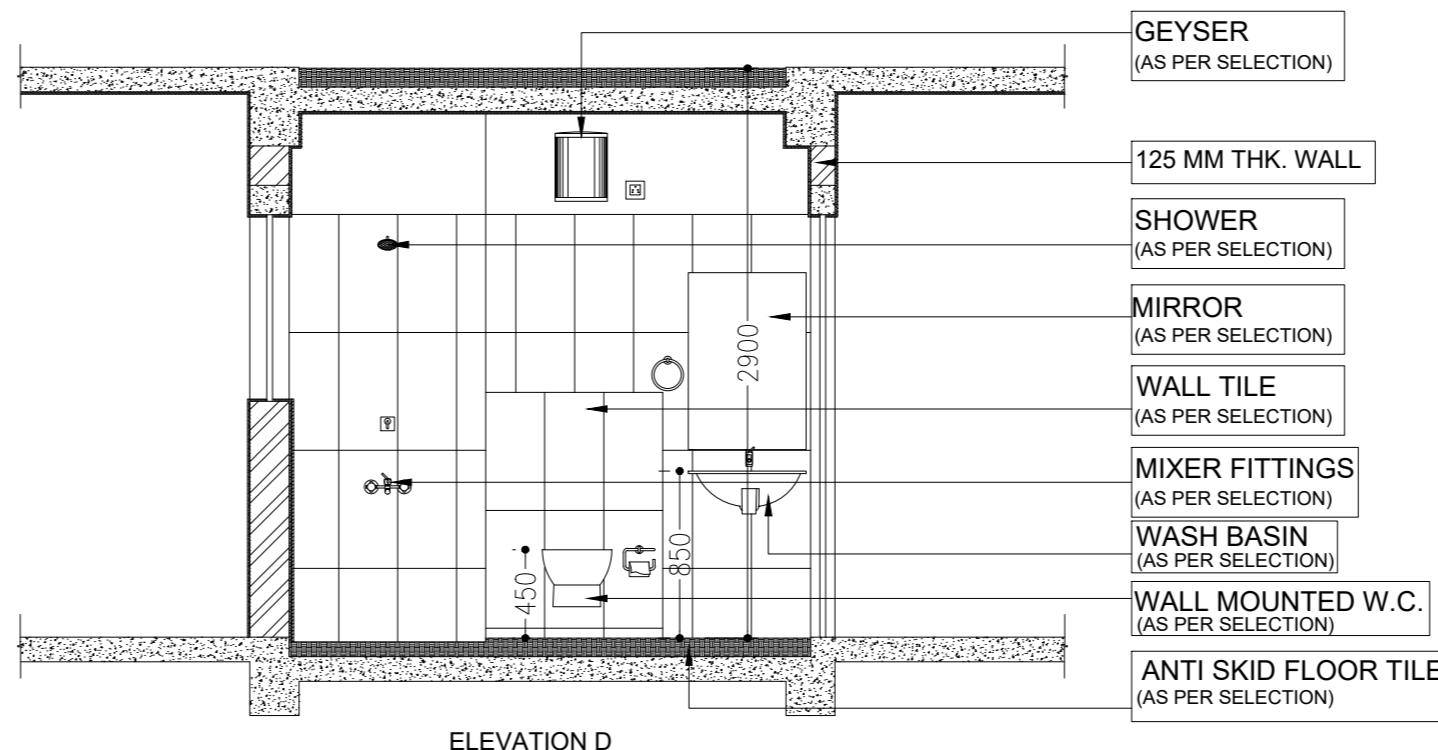


ELEVATION

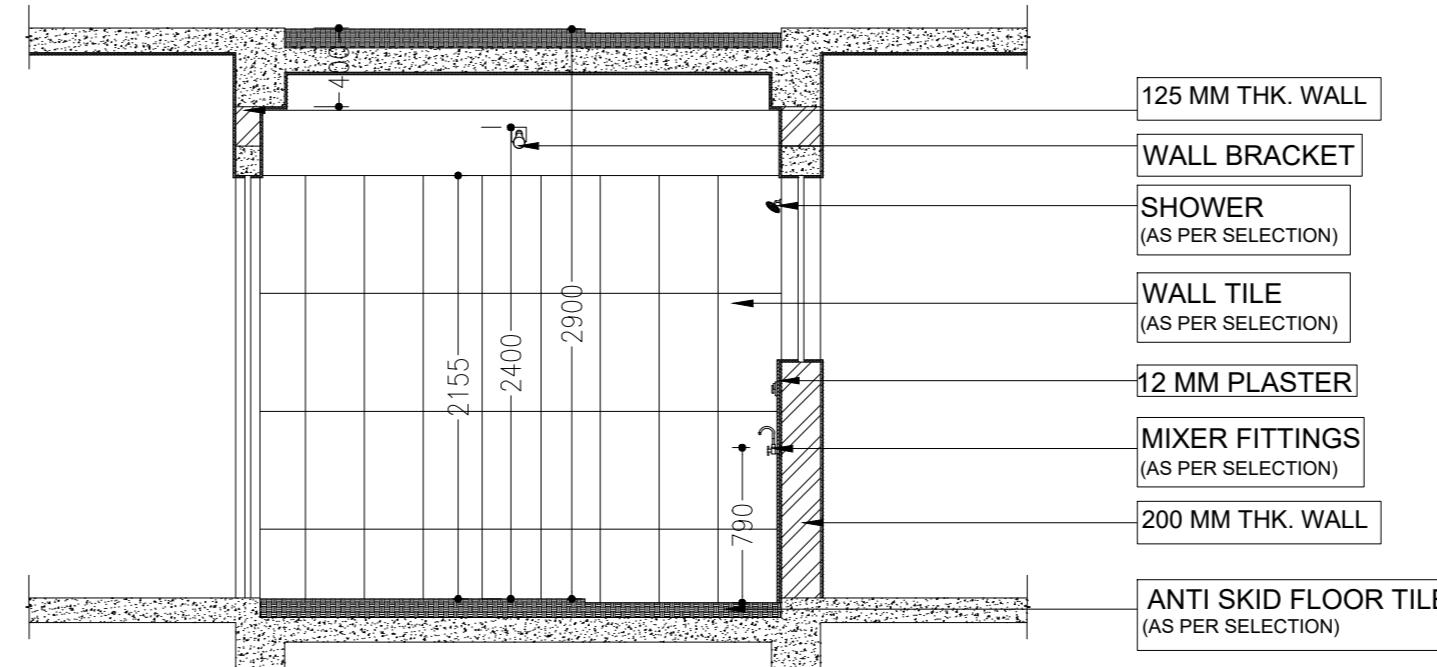

ELEVATION

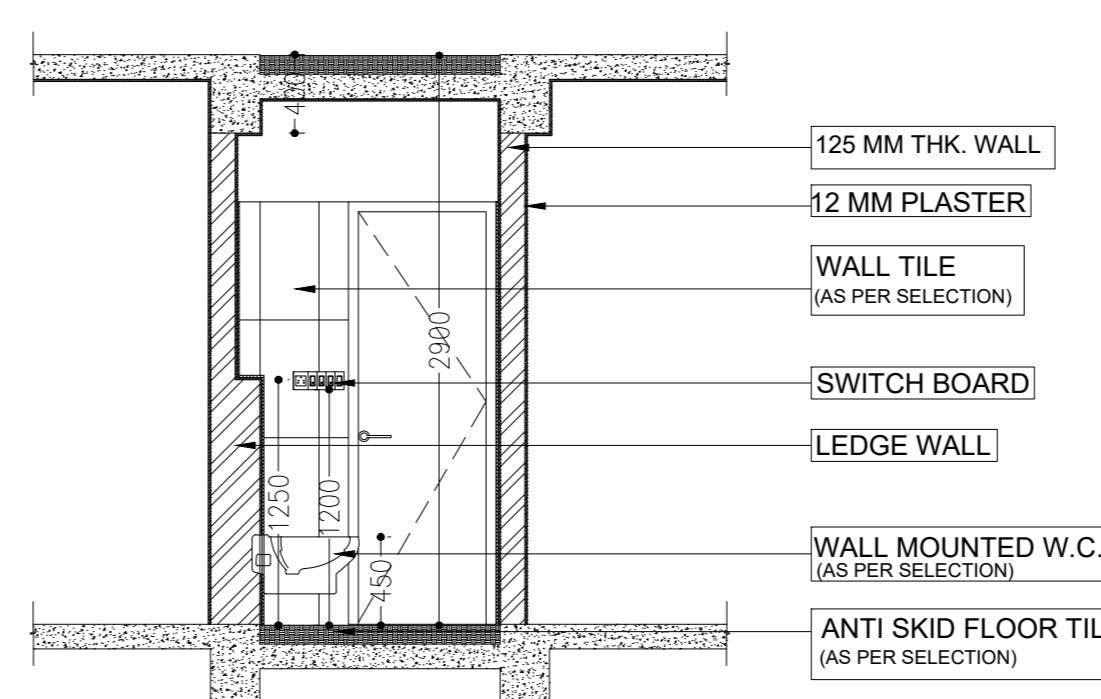


ELEVATION

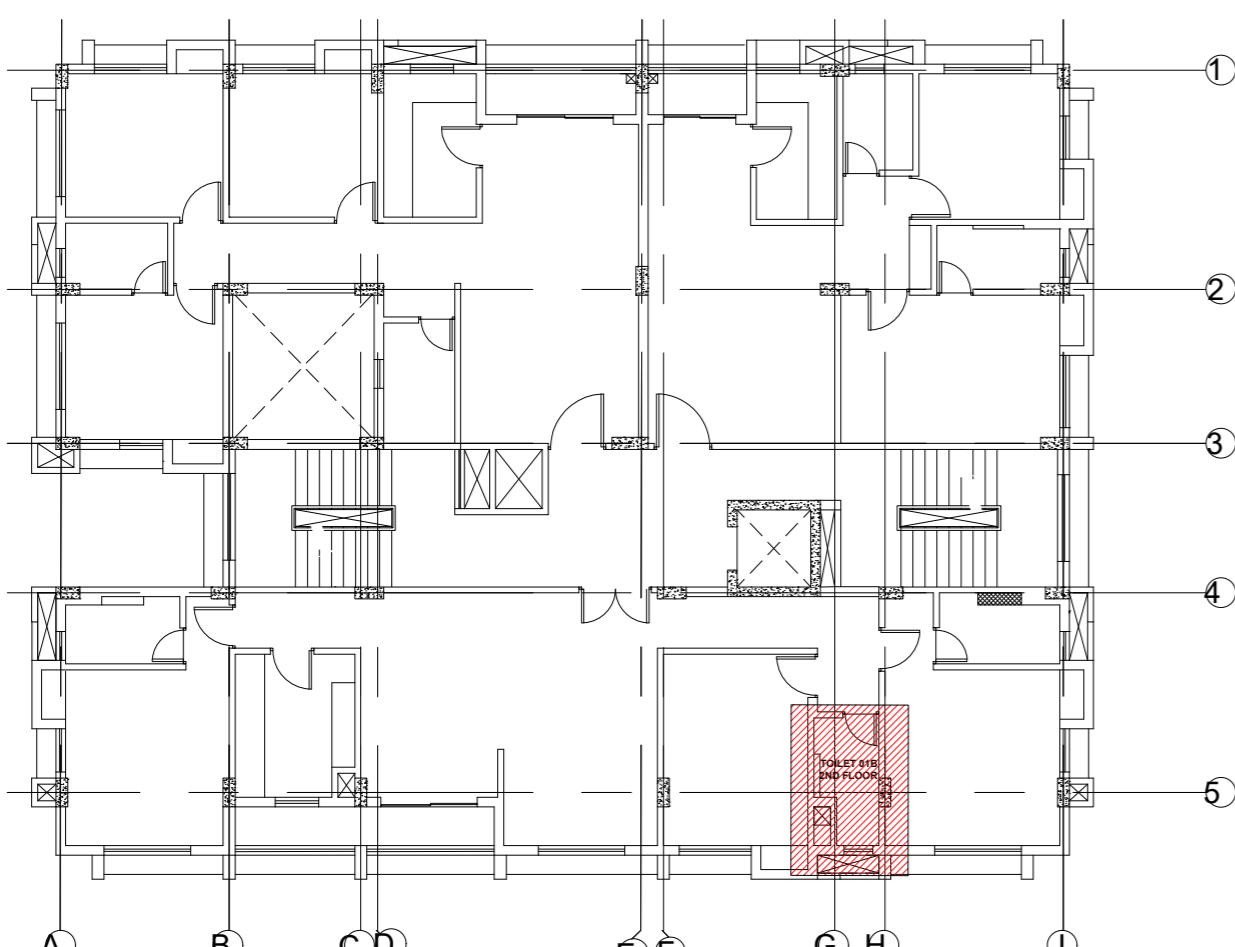


KEY PLAN (2ND FLOOR)


| DATE | DRAWN BY | CHECKED BY | DESCRIPTION OF THE REVISIONS |
|--|---|--------------------------|------------------------------|
| | | | |
| | | | |
| | | | |
| | | | |
| | | | |
| <p>STRUCTURAL SPA CONSULTANTS, 34, Rammohan Dutta Road, 2nd floor kol 20</p> | | | |
| <p>PROJECT: PROPOSED G+IV STORIED RESIDENTIAL HOUSING COMPLEX FOR KOYLA VIHAR, PHASE-III, AT MOUZA-MONDALGANTHI, J.L. NO- 06, DAG NO- 273,274,275,276 & 277; KHTIAN NO-190/1 & 992, TOUZI NO - 172, WARD NO- 12, P.S.- BAGUIATI, DIST- 24 PGS(N), UNDER RAJARHAT GOPALPUR MUNICIPALITY.</p> | | | |
| <p>CLIENT: SPACE GROUP</p> | | | |
| <p>PROJECT ARCHITECTS:</p>  <p>Maheswari & Associates An ISO 9001 : 2008 CERTIFIED ORGANISATION 37A Baker Road, 2nd Floor, Alipore, Kolkata-700027 +91-33-24490323 / 65228584 Website: www.architectm.com MUMBAI-KOLKATA-GUWAHATI-SILIGURI</p> | | | |
| <p>PURPOSE OF RELEASE</p> <p style="text-align: center;">GOOD FOR CONSTRUCTION</p> | | | |
| STAGE: | WORKING | | |
| DIRECTION: | SCALE: 1:25 UNLESS OTHERWISE SPECIFIED | Current Revision: | R0 |
| Start Date: | Issue Date: | Last saved Date: | |
| 15-05-20 | | | |
| Project Code: | KOL-KV | | |
| Bldng/Block: | BLOCK D | | |
| Floor: | 2ND FLOOR | | |
| Drawing title: | TOILET DETAIL | | |
| DRG NO. | MA/AR/KOYLA VIHAR/DETAILS/TOILET-06 | | |
| <p>THIS DRAWING IS THE SOLE PROPERTY OF MAHESWARI & ASSOCIATES. IT'S USE FOR ANY PURPOSE OTHER THAN THAT MENTIONED IS TO BE DONE ONLY AFTER PRIOR APPROVAL.</p> | | | |

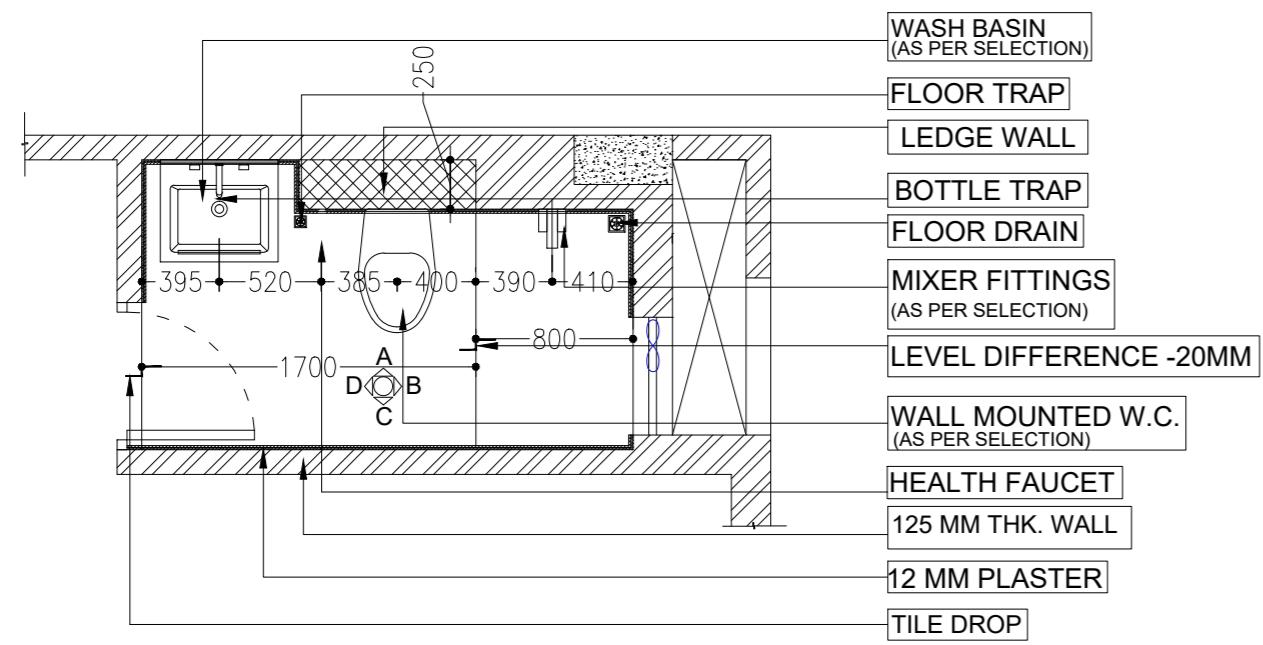


PLAN

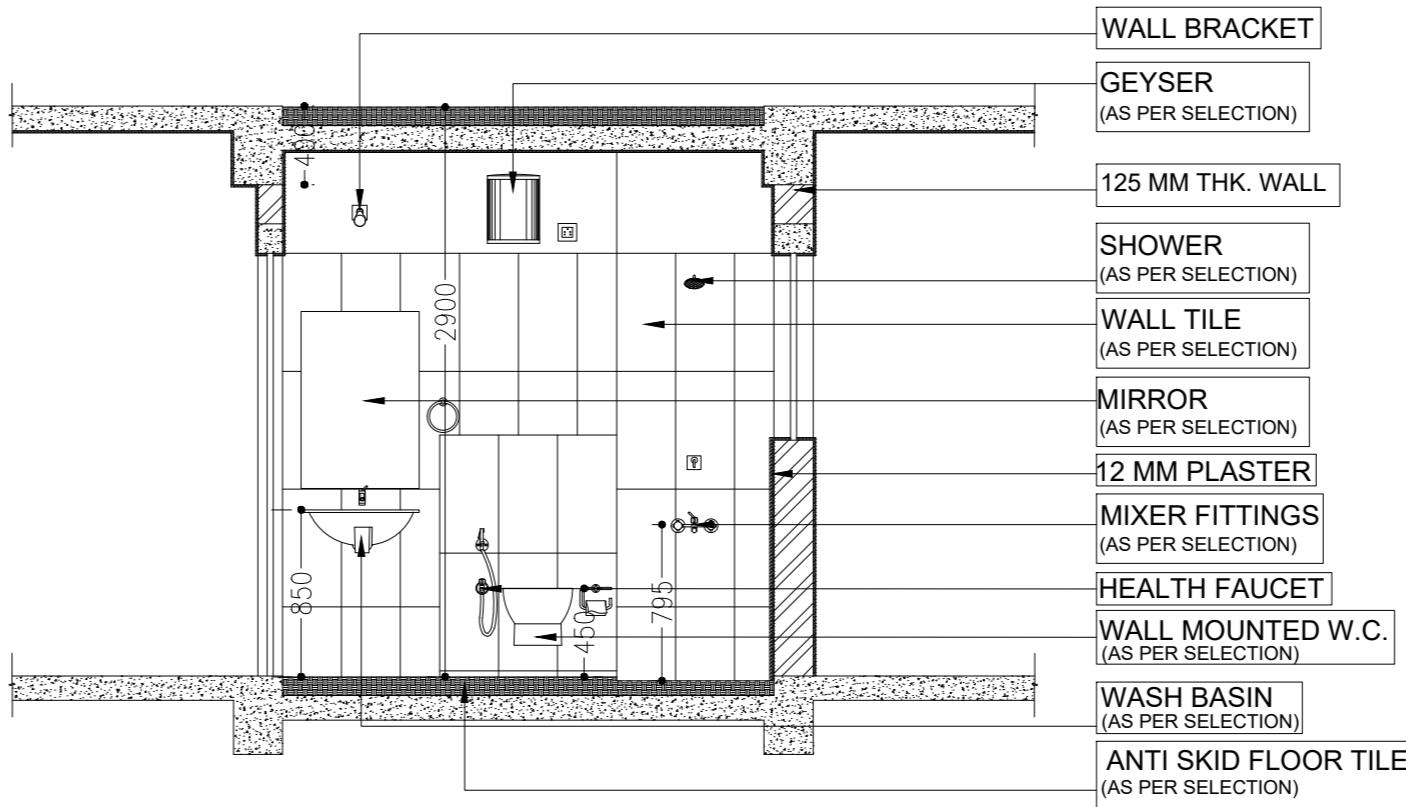


ELEVATION A

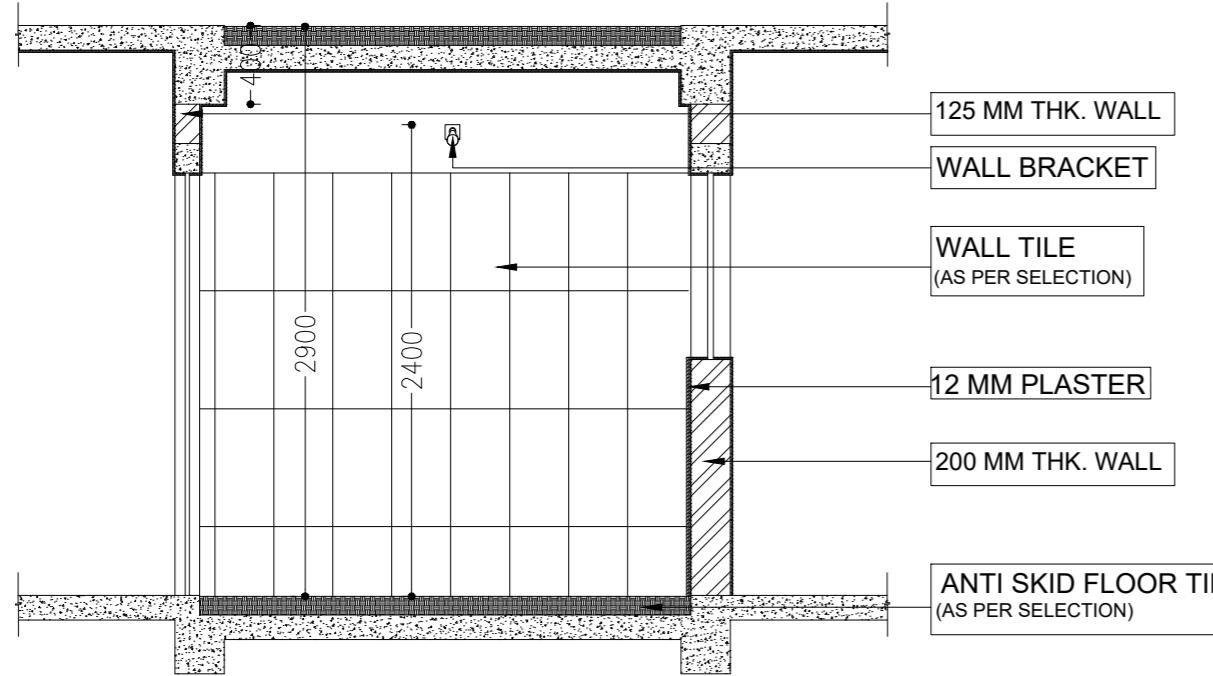


ELEVATION C

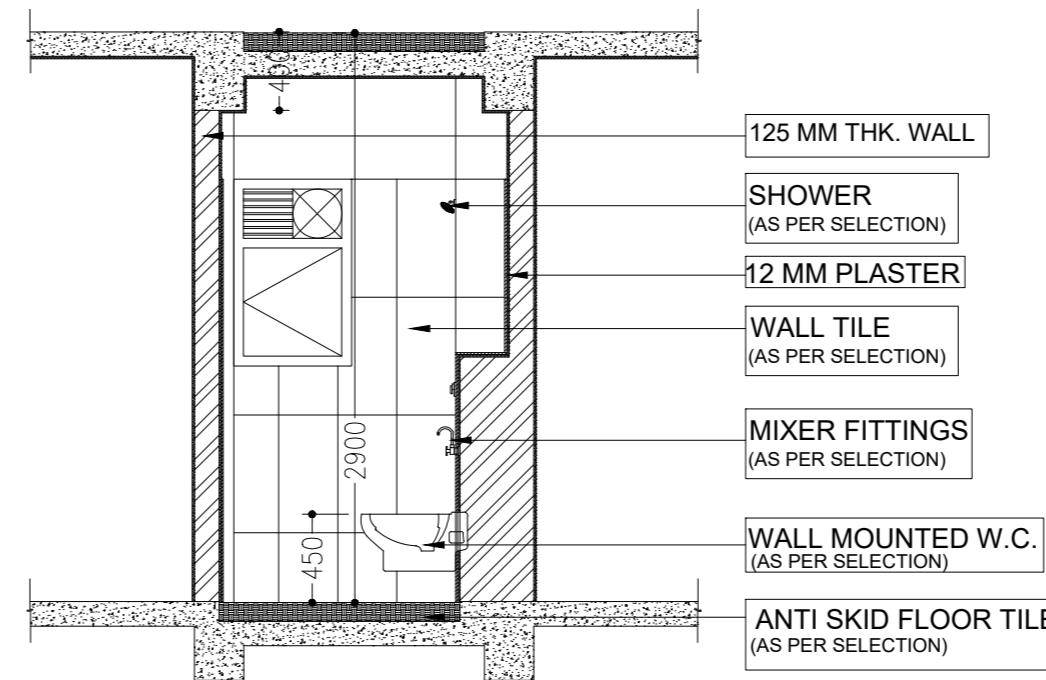


ELEVATION

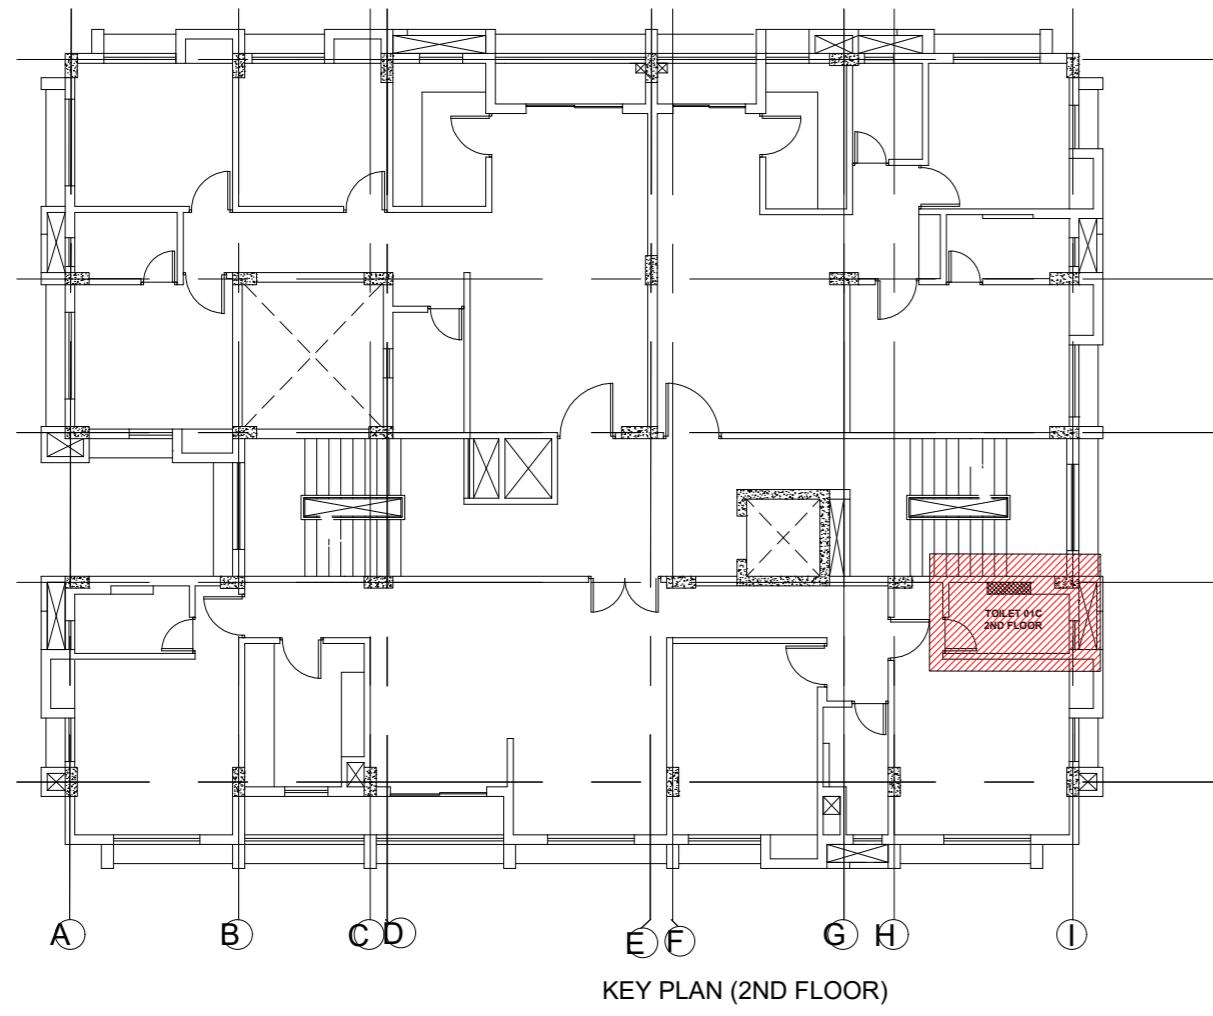


KEY PLAN (2ND FLOOR)

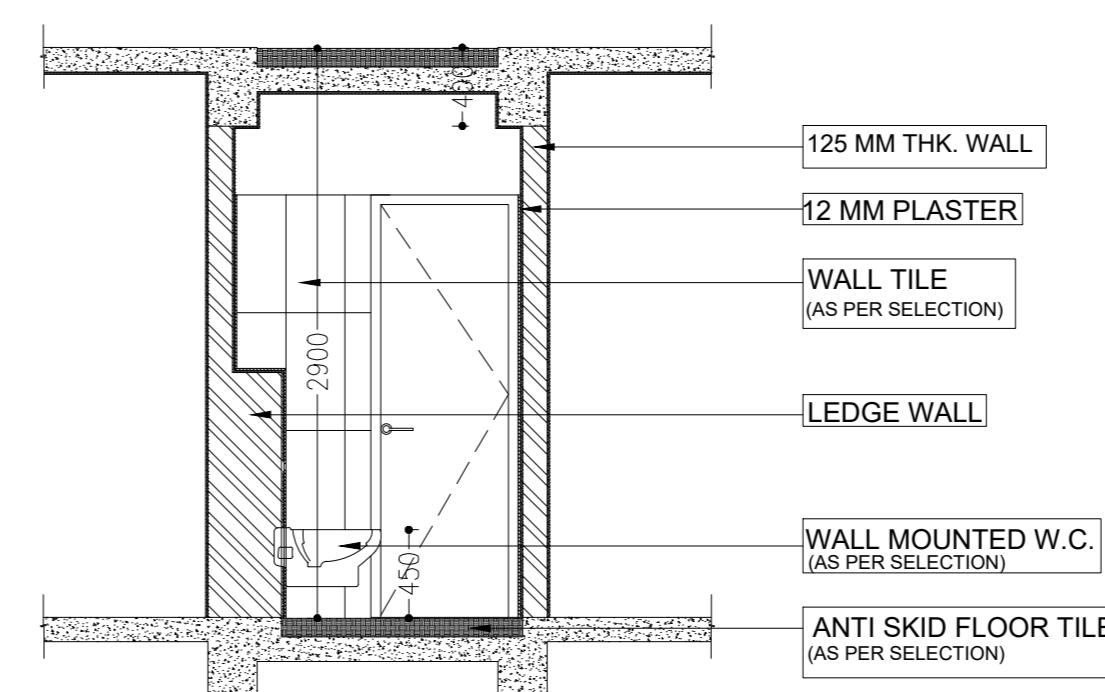

ELEVATION
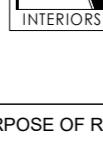
| DATE | DRAWN BY | CHECKED BY | DESCRIPTION OF THE REVISIONS |
|--|---|--|--|
| | | | |
| | | | |
| | | | |
| | | | |
| | | | |
| <p>STRUCTURAL SPA CONSULTANTS, 34, Rammohan Dutta Road, 2nd floor kol 20</p> | | | |
| <p>PROJECT: PROPOSED G+IV STORIED RESIDENTIAL HOUSING COMPLEX FOR KOYLA VIHAR, PHASE-III, AT MOUZA-MONDALGANTHI, J.L. NO- 06, DAG NO- 273,274,275,276 & 277; KHTIAN NO-190/1 & 992, TOUZI NO - 172, WARD NO- 12, P.S.- BAGUIATI, DIST- 24 PGS(N), UNDER RAJARHAT GOPALPUR MUNICIPALITY.</p> | | | |
| <p>CLIENT: SPACE GROUP</p> | | | |
| <p>PROJECT ARCHITECTS:</p>  <p>Maheswari & Associates An ISO 9001 : 2008 CERTIFIED ORGANISATION 37A Baker Road, 2nd Floor, Alipore, Kolkata-700027 +91-33-24490323 / 65228584 Website: www.architectm.com MUMBAI-KOLKATA-GUWAHATI-SILIGURI</p> | | | |
| <p>PURPOSE OF RELEASE</p> <p style="text-align: center;">GOOD FOR CONSTRUCTION</p> | | | |
| <p>STAGE:</p> | | <p>WORKING</p> | |
| <p>DIRECTION:</p> | | <p>SCALE: 1:25 UNLESS OTHERWISE SPECIFIED</p> | <p>Current Revision:</p> <p>R0</p> |
| <p>Start Date:</p> | | <p>Issue Date:</p> | <p>Last saved Date:</p> |
| <p>15-05-20</p> | | | |
| <p>Project Code:</p> | | <p>KOL-KV</p> | |
| <p>Bldng/Block:</p> | | <p>BLOCK D</p> | |
| <p>Floor:</p> | | <p>2ND FLOOR</p> | |
| <p>Drawing title:</p> | <p>TOILET DETAIL</p> | | |
| <p>DRG NO.</p> | <p>MA/AR/KOYLA VIHAR/DETAILS/TOILET-07</p> | | |
| <p>THIS DRAWING IS THE SOLE PROPERTY OF MAHESWARI & ASSOCIATES. IT'S USE FOR ANY PURPOSE OTHER THAN THAT MENTIONED IS TO BE DONE ONLY AFTER PRIOR APPROVAL.</p> | | | |

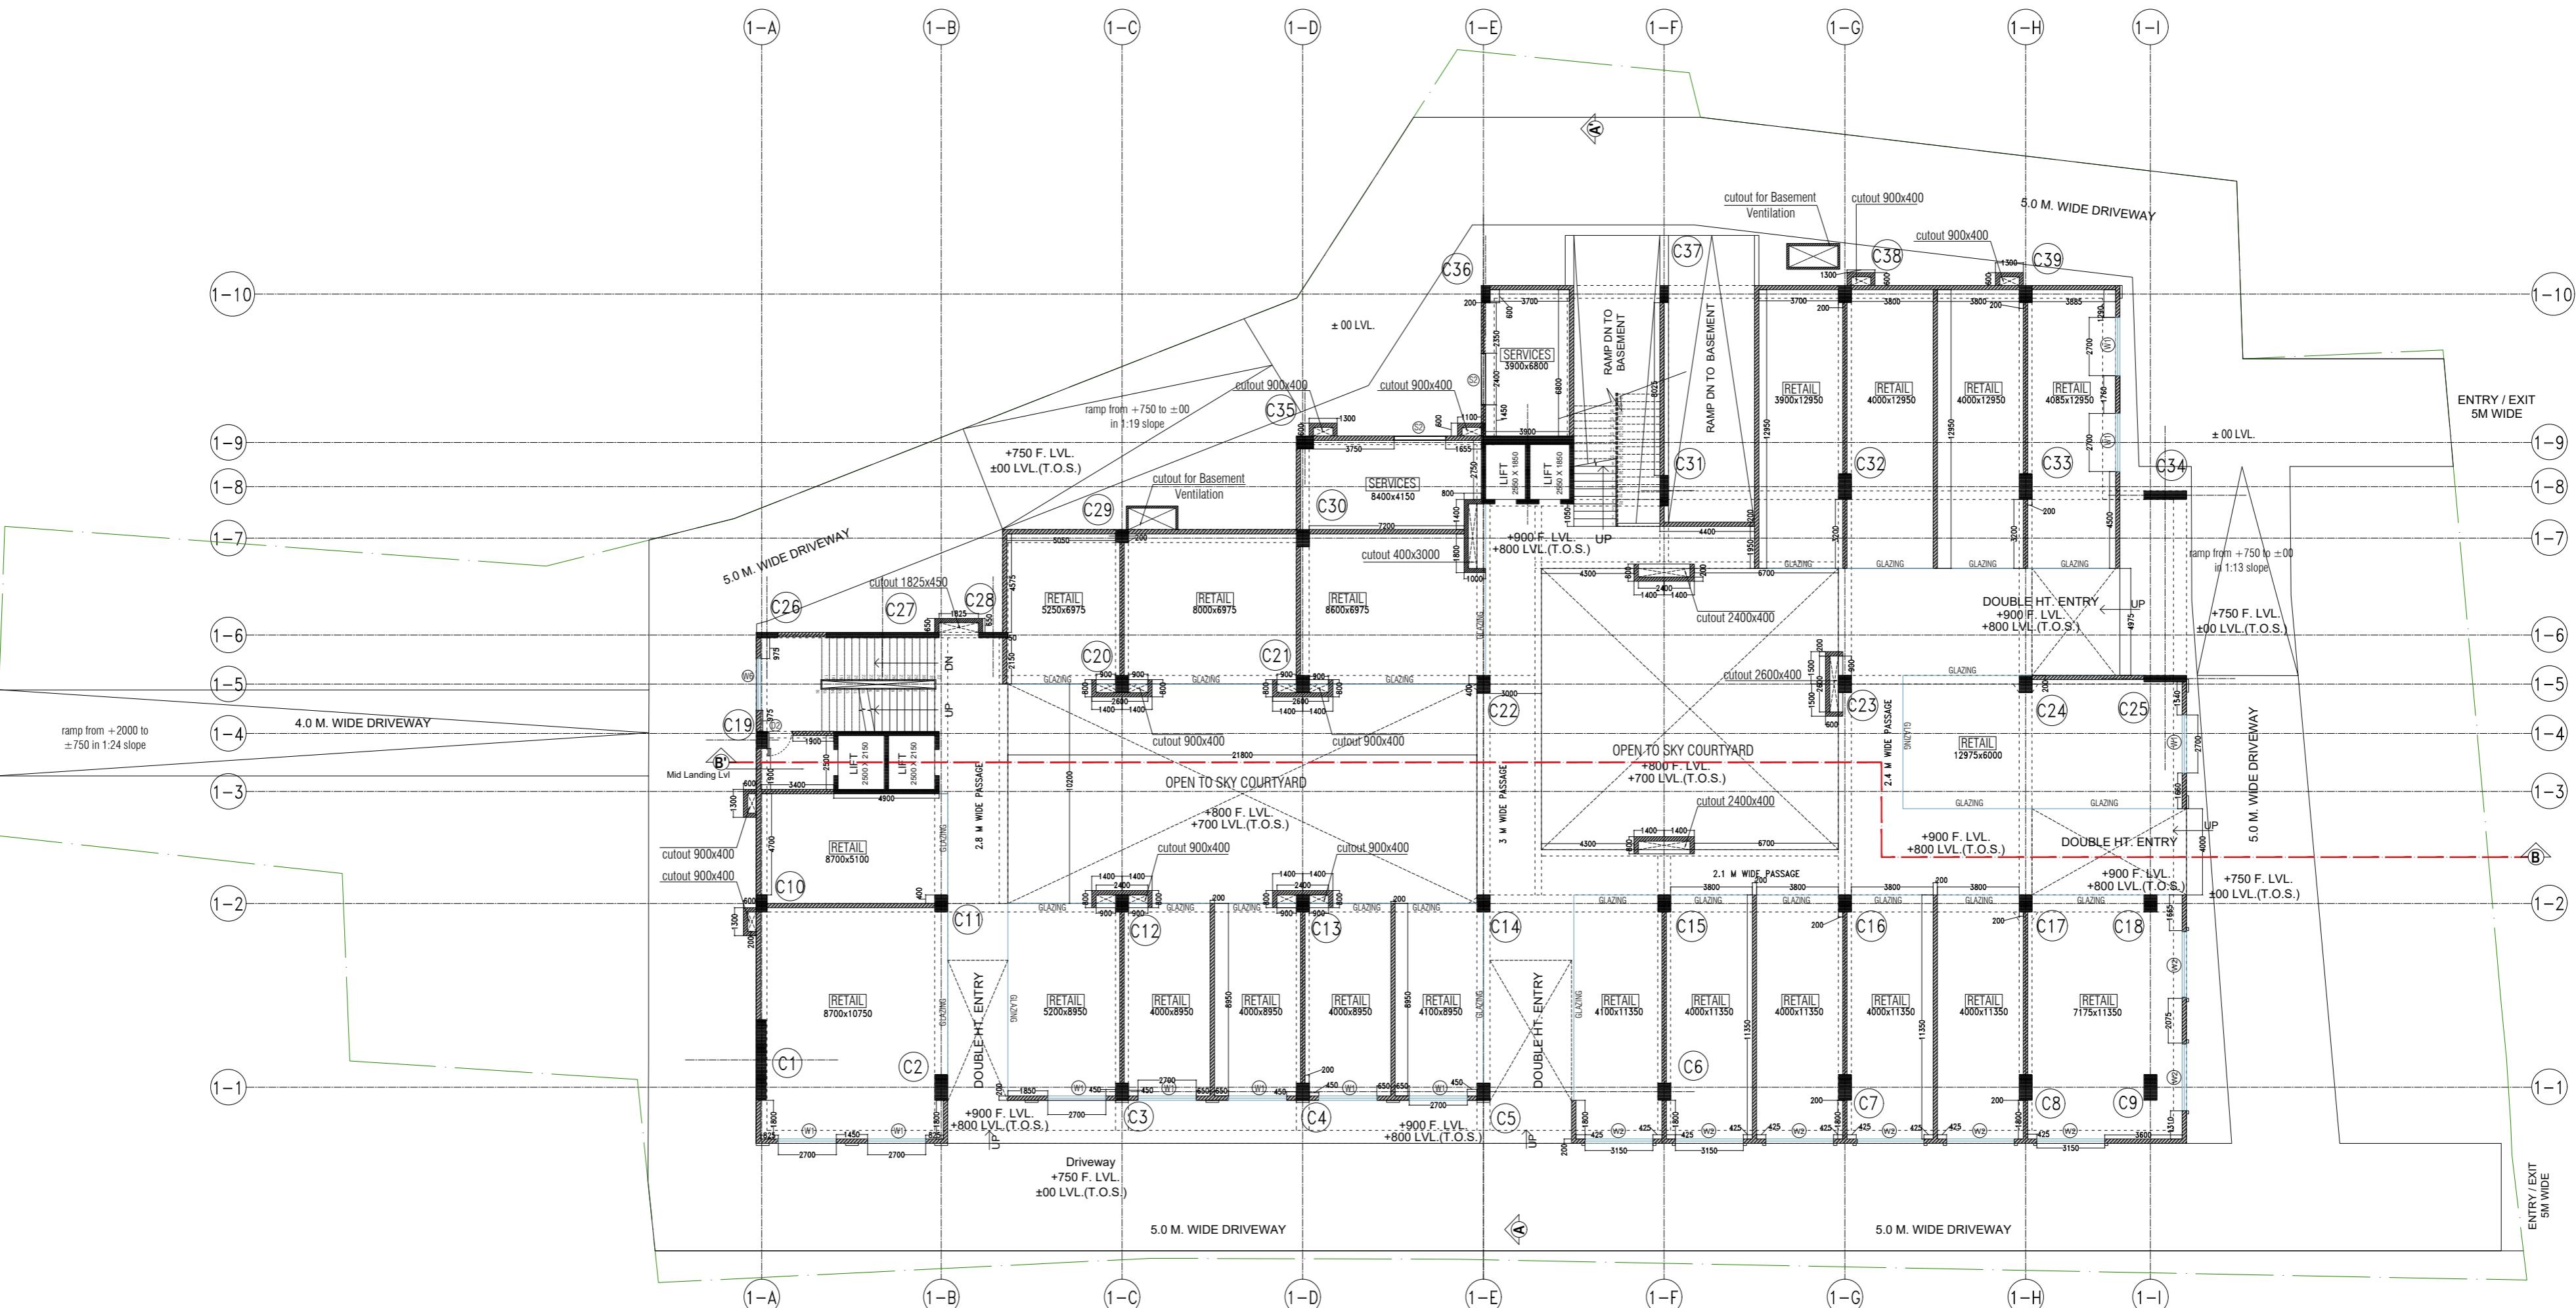

SCHEDULE OF DOORS & WINDOWS

| WINDOWS: | | | | | DOORS: | | | |
|----------|-------|-----------------|------|--------|--------|-------|--------|------|
| MKD. | WIDTH | HEIGHT | SILL | LINTEL | MKD | WIDTH | HEIGHT | SILL |
| W1 | 2700 | 6550 | | | | | | |
| W2 | 3150 | 6290 (ARCH TOP) | | | | | | |
| W3 | 1800 | 2800 | | | | | | |
| W4 | 3600 | 6600 | | | | | | |
| W5 | 3600 | 7500 (ARCH TOP) | | | | | | |

NOTE:
ALL BRICK WALLS ARE 200 MM THICK

For more information about the study, please contact Dr. Michael J. Hwang at (319) 356-4000 or email at mhwang@uiowa.edu.

- PROIE

SHIVADITYA GLOBAL

DRAWING PURPOSE

WORKING DRAWING


TITLE


GROUND FLOOR PLAN

CLIENT

ARCHITECT : Kamal Periwal

WARI & ASSOCIATES
KER ROAD, 2nd FLOOR
KOLKATA - 700 027
hitectm.com

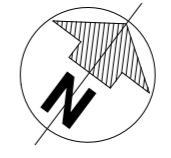

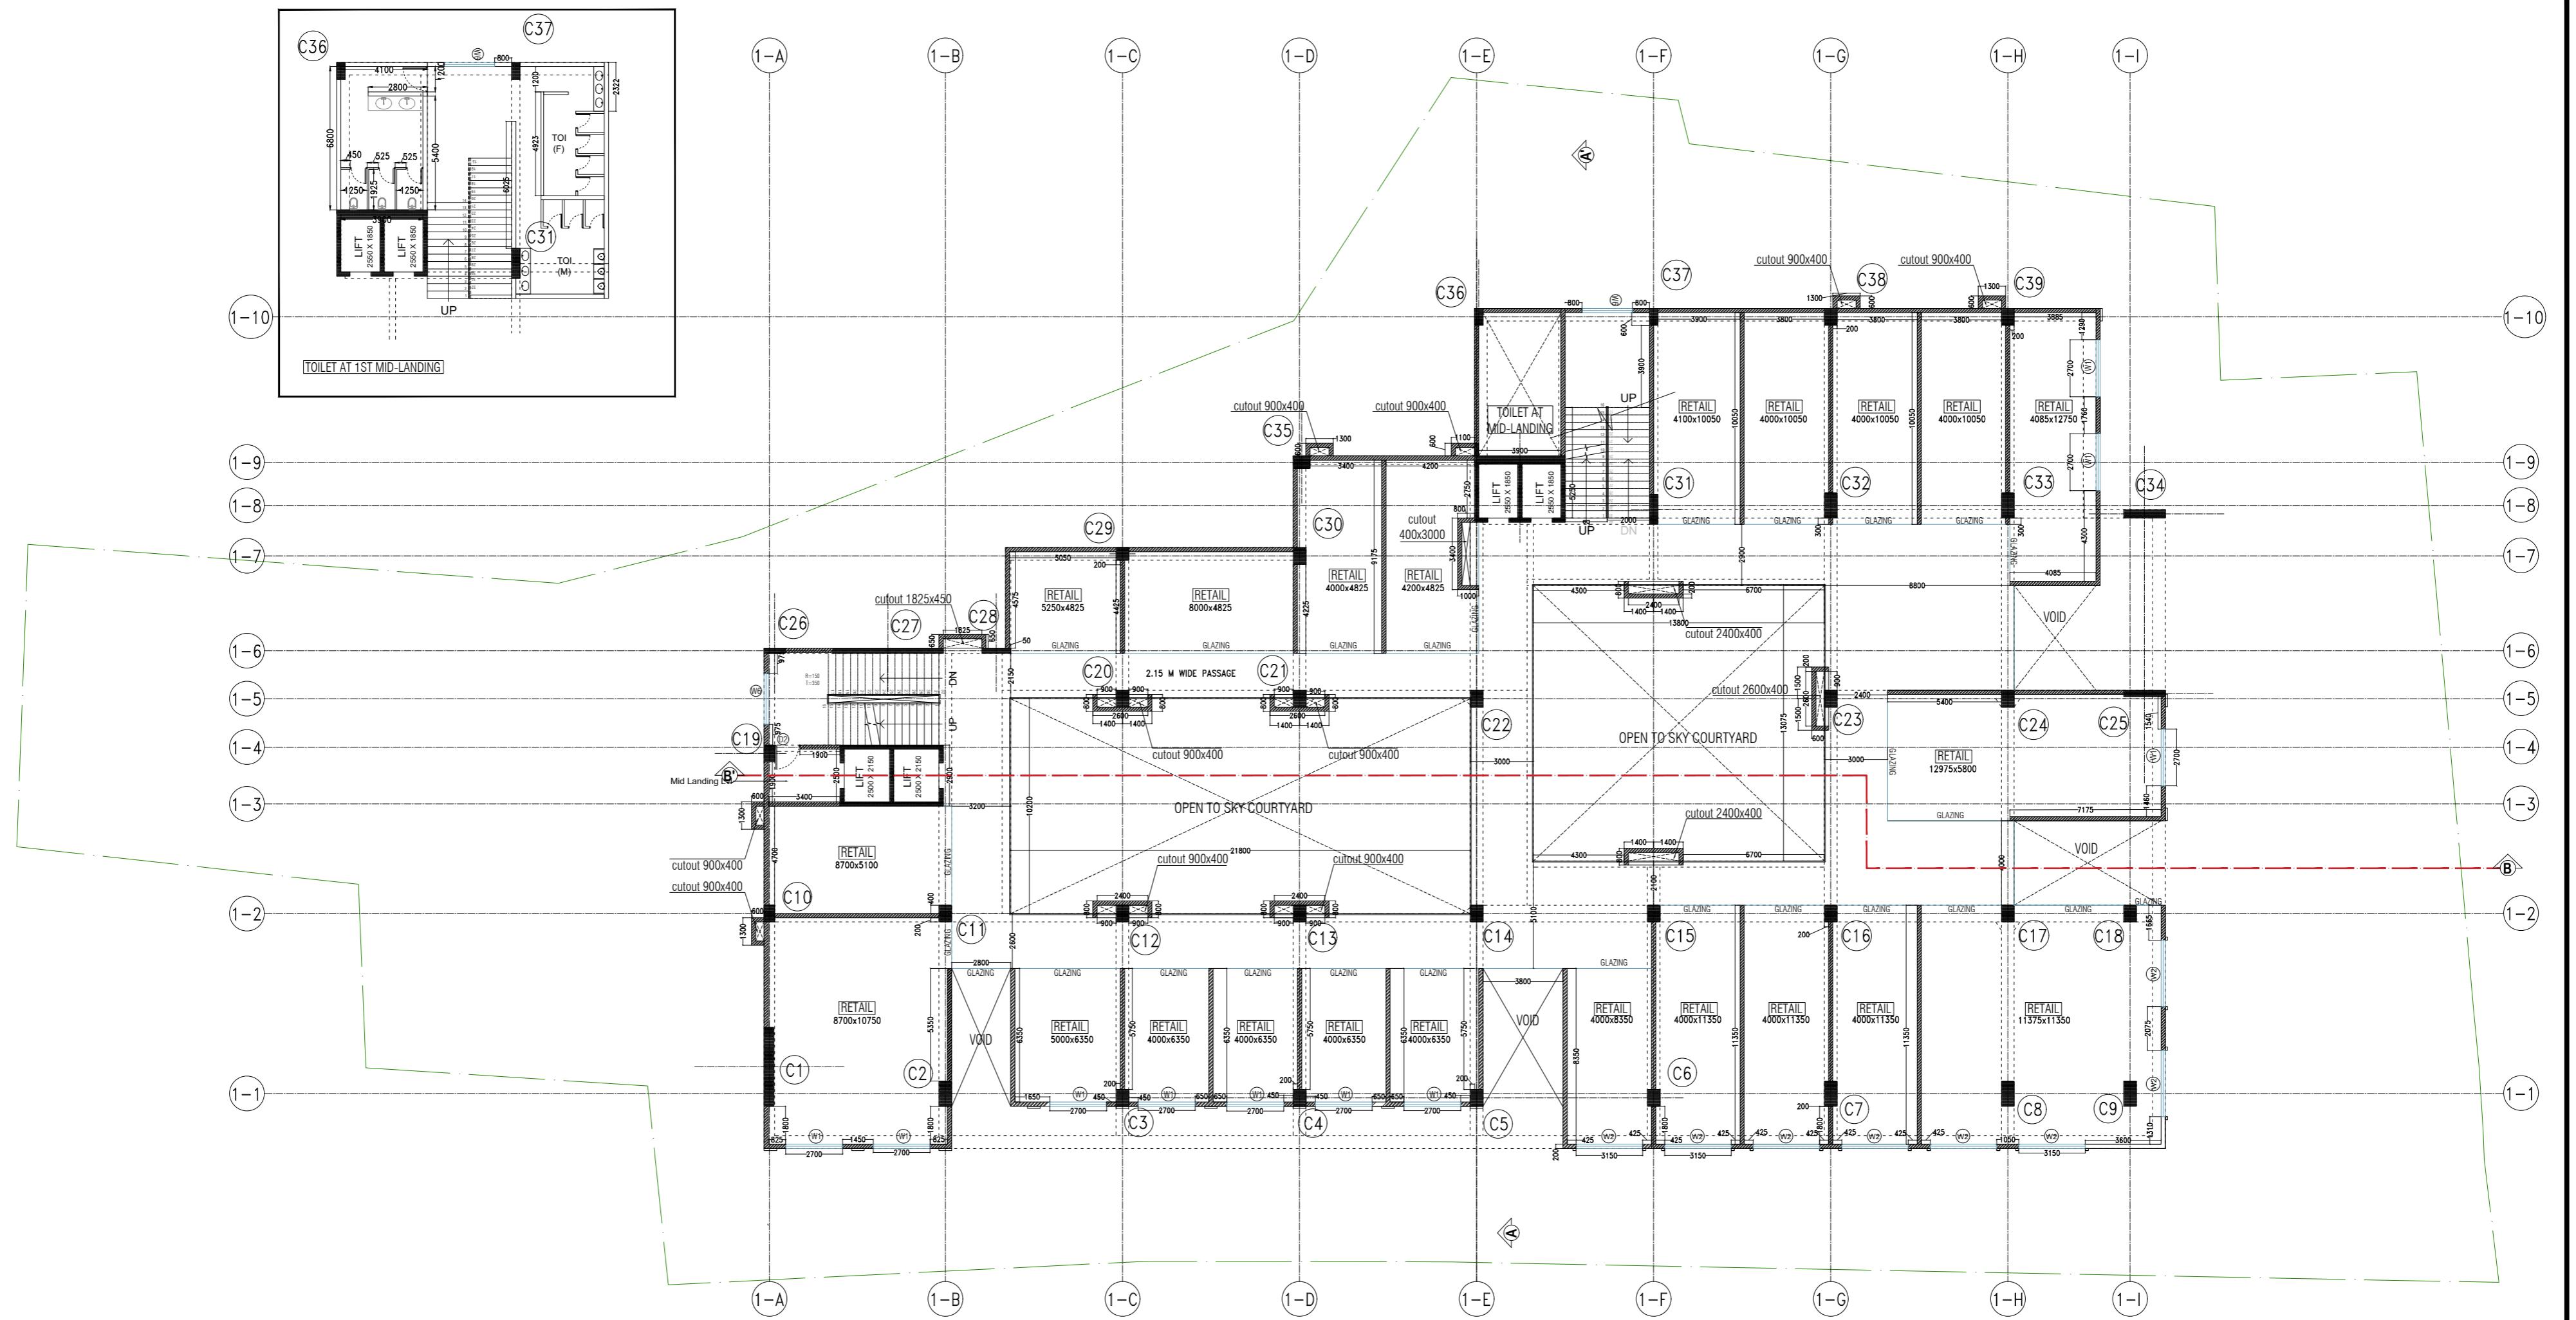

1ST FLOOR PLAN

BUA 18760 SQFT

SCHEDULE OF DOORS & WINDOWS

WINDOWS: DOORS:

| MKD. | WIDTH | HEIGHT | SILL | LINTEL | MKD | WIDTH | HEIGHT | SILL | LINTEL |
|------|-------|-----------------|------|--------|-----|-------|--------|------|--------|
| W1 | 2700 | 6550 | | | | | | | |
| W2 | 3150 | 6290 (ARCH TOP) | | | | | | | |
| W3 | 1800 | 2800 | | | | | | | |
| W4 | 3600 | 6600 | | | | | | | |
| W5 | 3600 | 7500 (ARCH TOP) | | | | | | | |

NOTE:
ALL BRICK WALLS ARE 200 MM THK

DRAWING PURPOSE :

WORKING DRAWING

TITLE :

FIRST FLOOR PLAN

CLIENT :

PROJECT :

SHIVADITYA GLOBAL

DRAWING STATUS :

ADVANCED COPY

ARCHITECT : Kamal Periwal

SCALE 1:150

ARCHITECTS MAHESWARI & ASSOCIATES


DATE


37A, BAKER ROAD, 2nd FLOOR
ALIPUR, KOLKATA - 700 027
www.architectm.com

DRAWN BY Simply Das

INTERIORS

DRG NO.

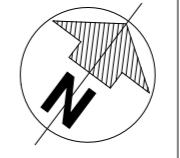

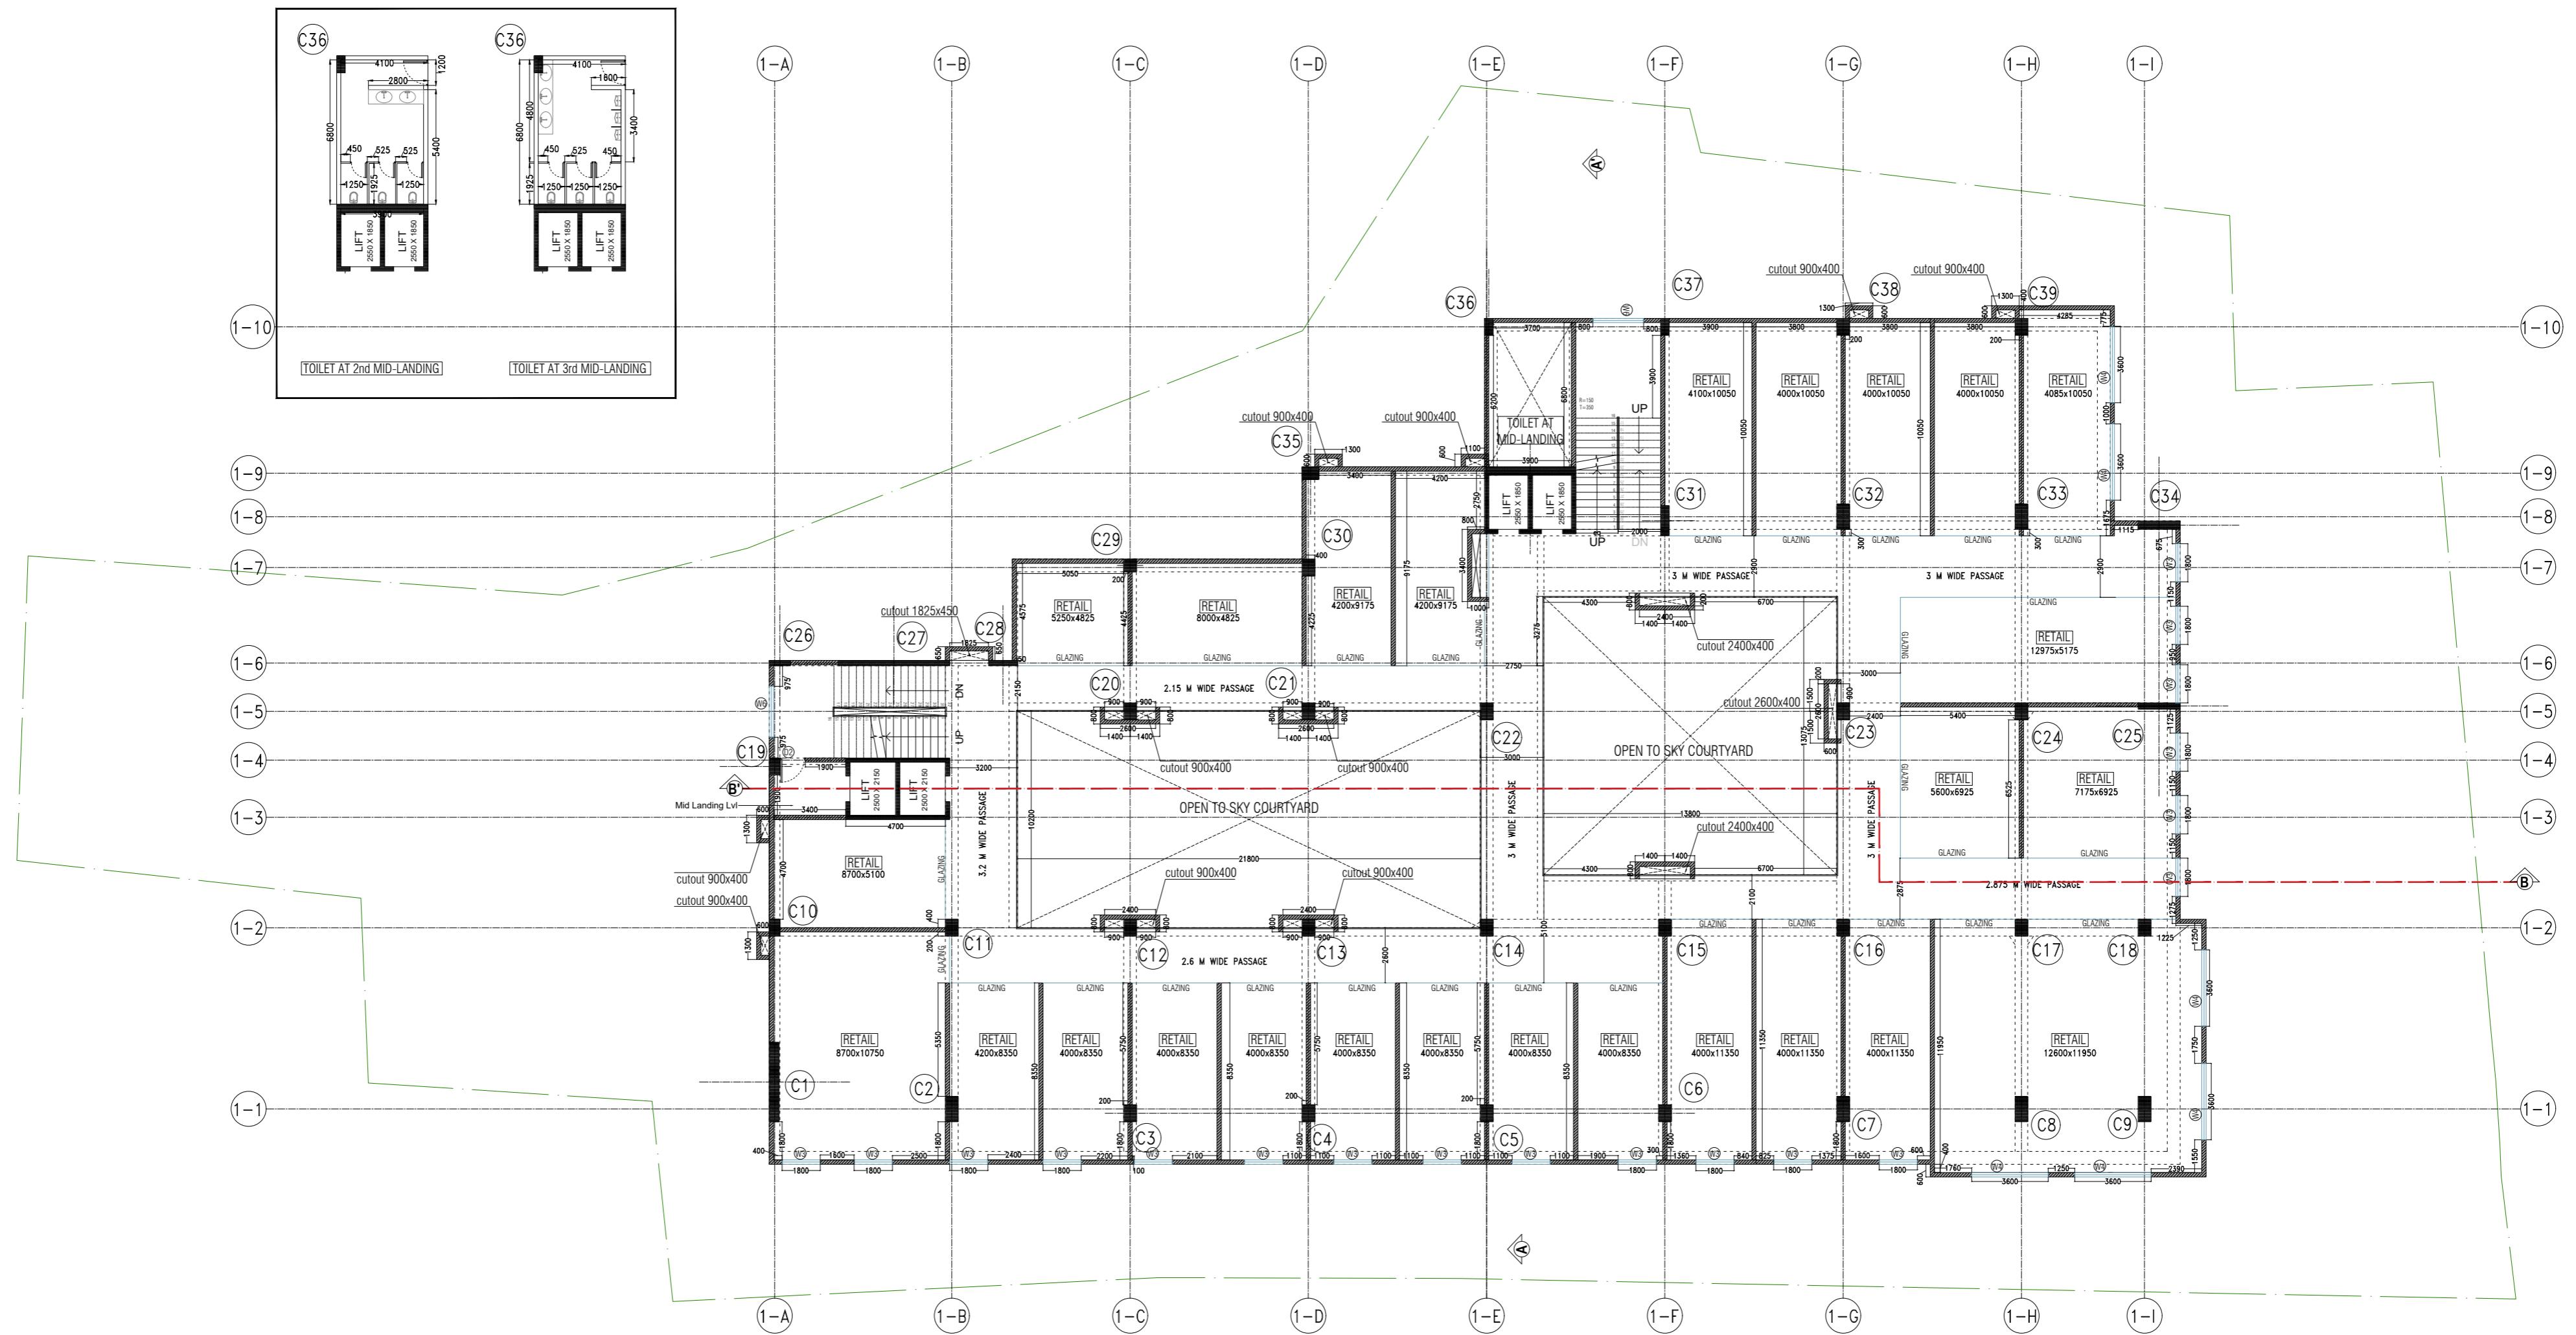

TYPICAL 2ND & 3RD FLOOR PLAN

BUA 19330 SQFT

SCHEDULE OF DOORS & WINDOWS

WINDOWS: DOORS:

| MKD. | WIDTH | HEIGHT | SILL | LINTEL | MKD | WIDTH | HEIGHT | SILL | LINTEL |
|------|-------|-----------------|------|--------|-----|-------|--------|------|--------|
| W1 | 2700 | 6550 | | | | | | | |
| W2 | 3150 | 6290 (ARCH TOP) | | | | | | | |
| W3 | 1800 | 2800 | | | | | | | |
| W4 | 3600 | 6600 | | | | | | | |
| W5 | 3600 | 7500 (ARCH TOP) | | | | | | | |

NOTE:
ALL BRICK WALLS ARE 200 MM THK

DRAWING PURPOSE :

WORKING DRAWING

TITLE :

SECOND FLOOR PLAN

CLIENT :

PROJECT :

SHIVADITYA GLOBAL

DRAWING STATUS :

ADVANCED COPY


ARCHITECT : Kamal Periw

SCALE 1:150

DATE


DRAWN BY Simply Das

DRG NO.

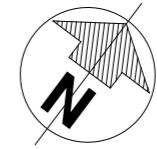

MAHESWARI & ASSOCIATES
37A, BAKER ROAD, 2nd FLOOR
ALIPUR, KOLKATA - 700 027
www.architectm.com

ARCHITECTS
INTERIORS

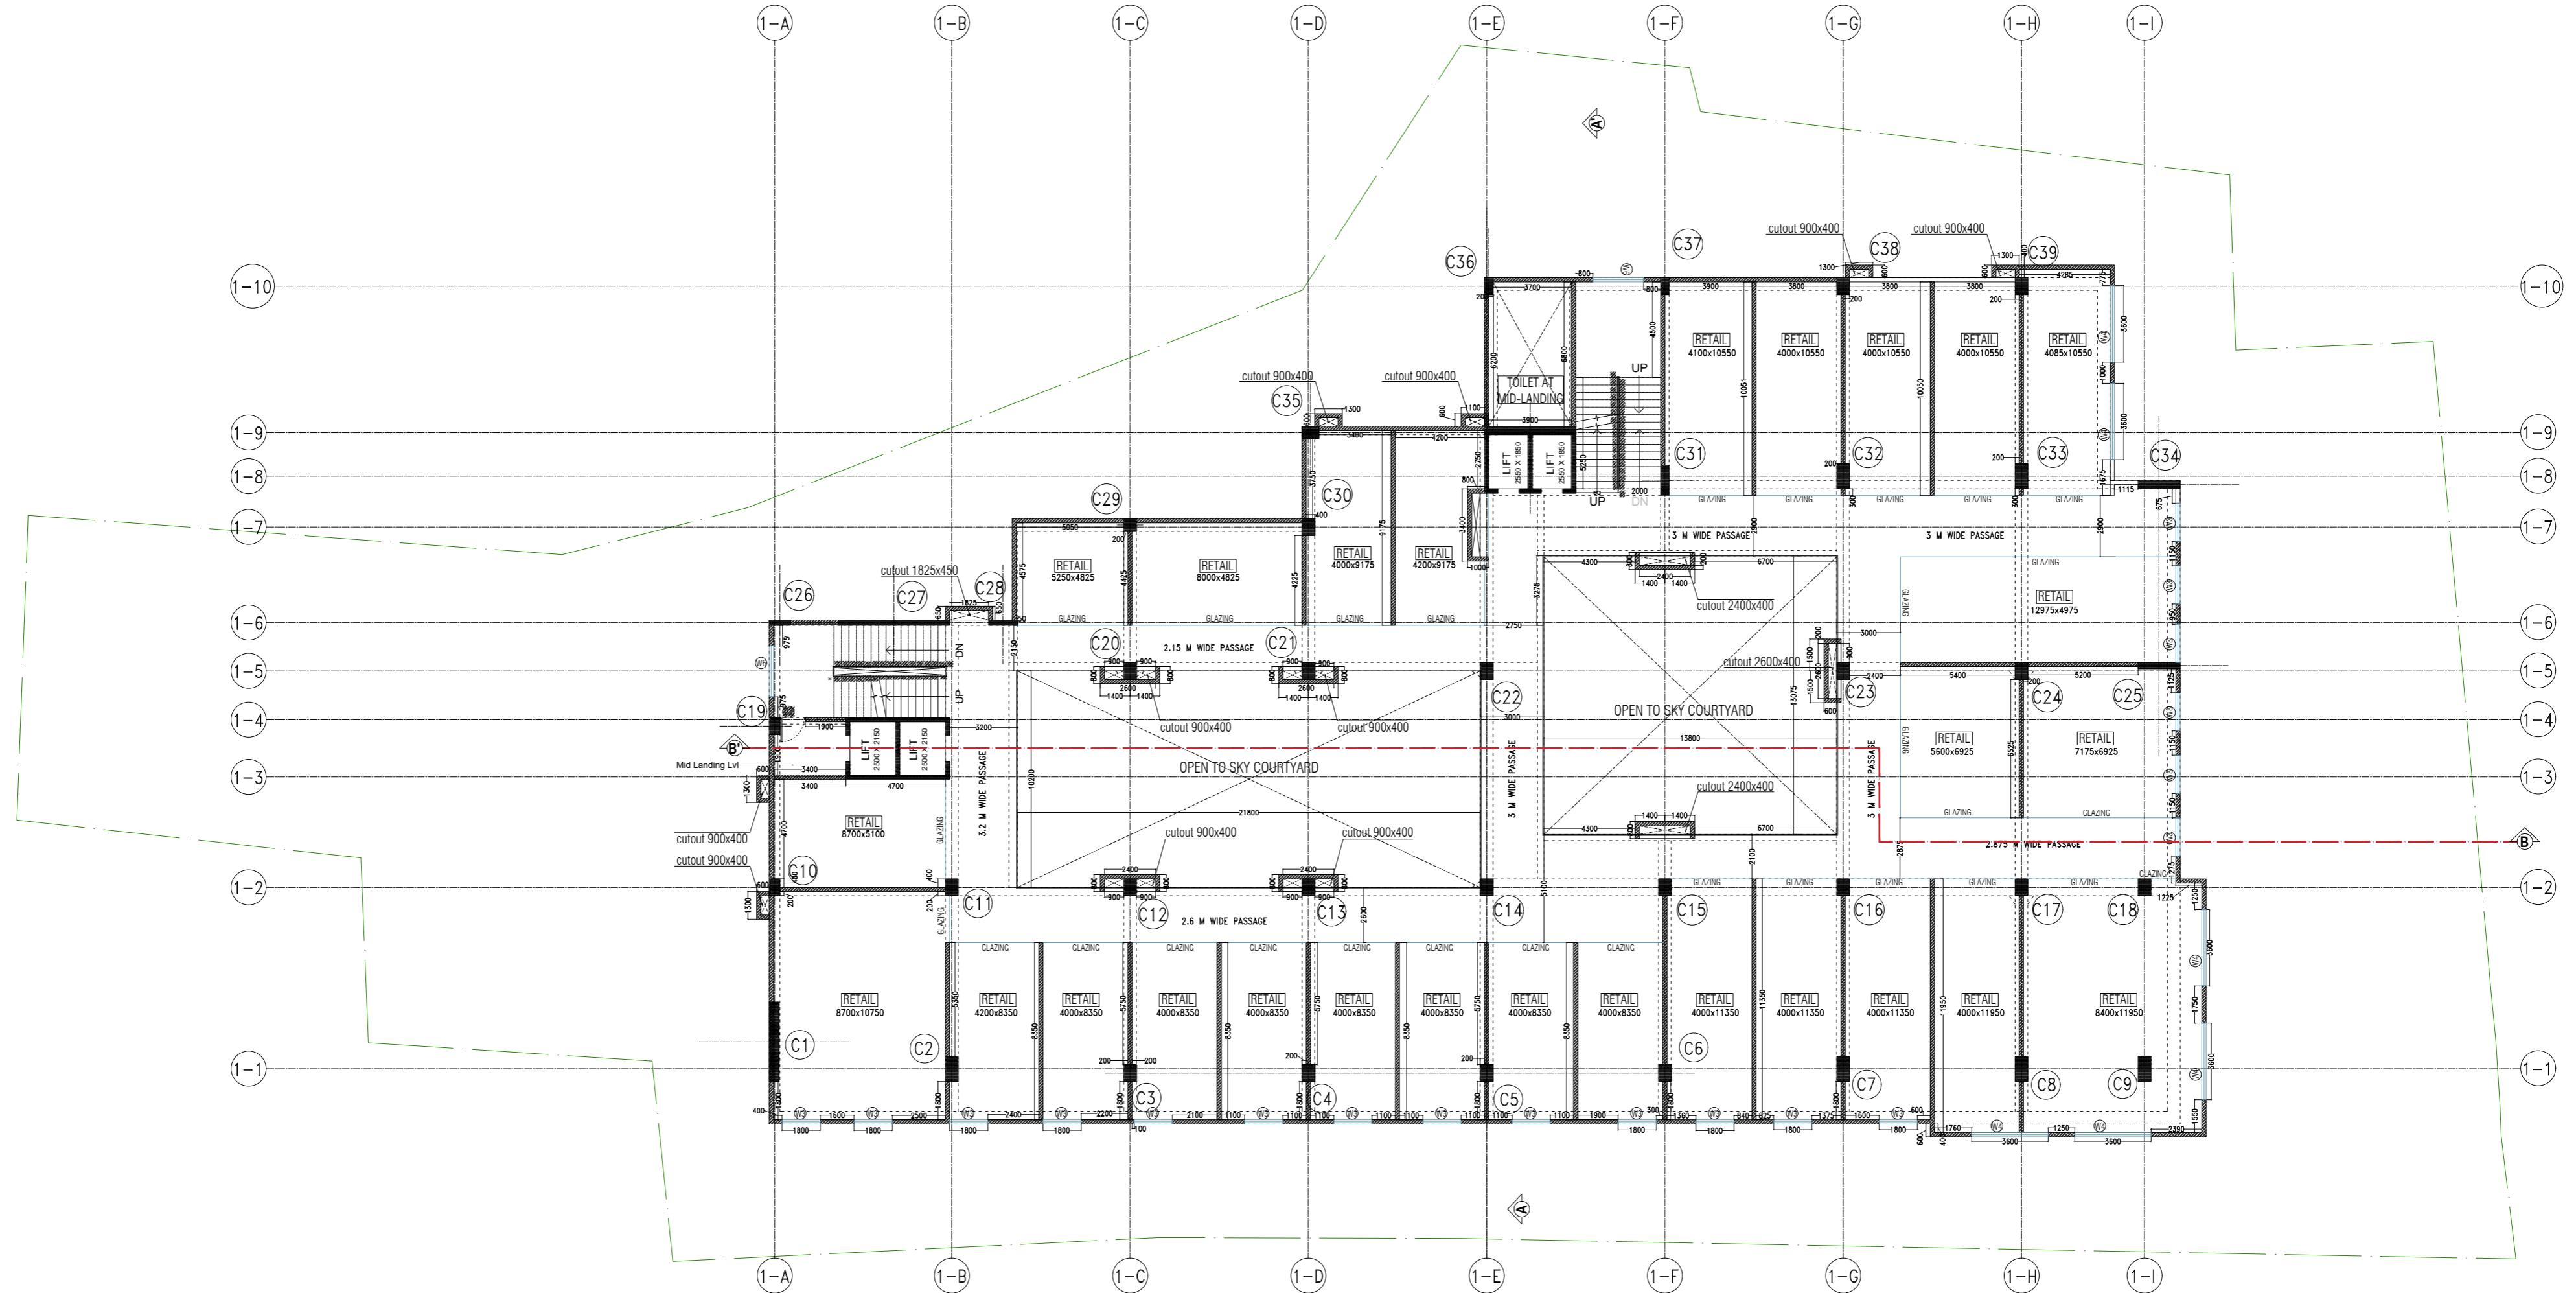

TYPICAL 2ND & 3RD FLOOR PLAN

BUA 19330 SQFT

SCHEDULE OF DOORS & WINDOWS

WINDOWS: DOORS:

| MKD. | WIDTH | HEIGHT | SILL | LINTEL | MKD | WIDTH | HEIGHT | SILL | LINTEL |
|------|-------|-----------------|------|--------|-----|-------|--------|------|--------|
| W1 | 2700 | 6550 | | | | | | | |
| W2 | 3150 | 6290 (ARCH TOP) | | | | | | | |
| W3 | 1800 | 2800 | | | | | | | |
| W4 | 3600 | 6600 | | | | | | | |
| W5 | 3600 | 7500 (ARCH TOP) | | | | | | | |

NOTE:
ALL BRICK WALLS ARE 200 MM THK

DRAWING PURPOSE :

WORKING DRAWING

TITLE :

THIRD FLOOR PLAN


CLIENT :

PROJECT :

SHIVADITYA GLOBAL

DRAWING STATUS :

ADVANCED COPY

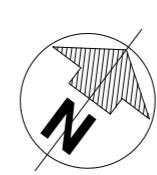


ARCHITECT : Kamal Periwal

ARCHITECTS
MAHESWARI & ASSOCIATES
37A, BAKER ROAD, 2nd FLOOR
ALIPUR, KOLKATA - 700 027
www.architectm.com

DRAWN BY Simply Das

DRG NO.

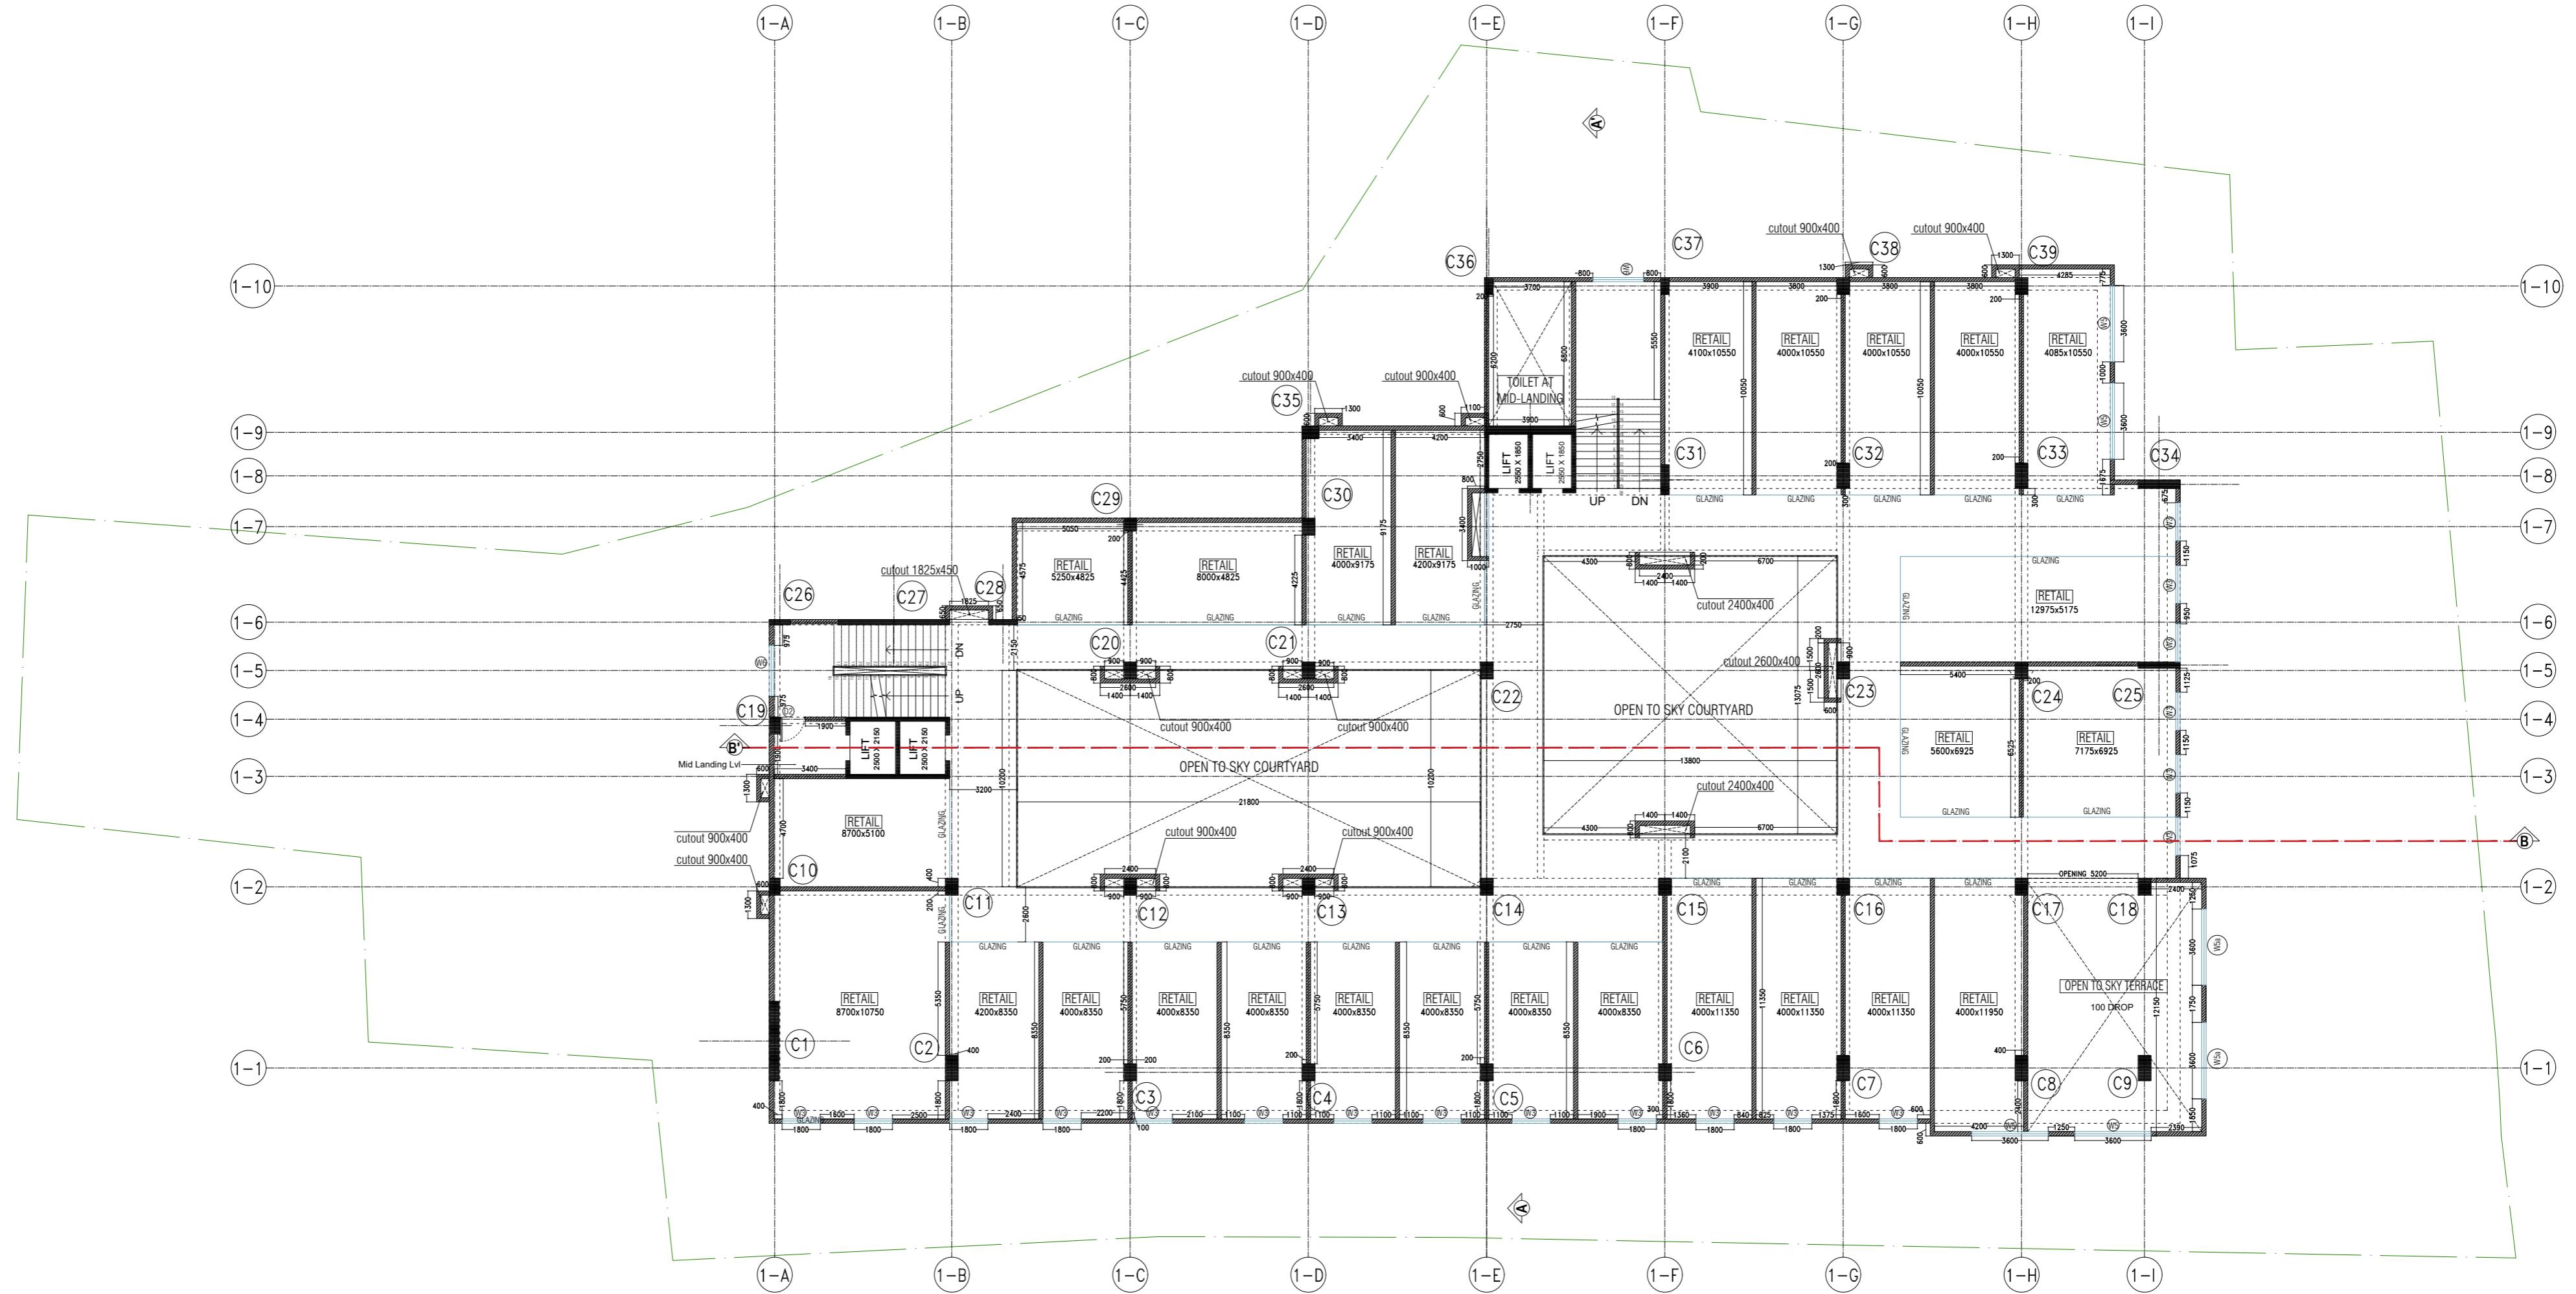

4TH FLOOR PLAN

BUA 17440 SQFT

SCHEDULE OF DOORS & WINDOWS

WINDOWS: DOORS:

| MKD. | WIDTH | HEIGHT | SILL | LINTEL | MKD | WIDTH | HEIGHT | SILL | LINTEL |
|------|-------|-----------------|------|--------|-----|-------|--------|------|--------|
| W1 | 2700 | 6550 | | | | | | | |
| W2 | 3150 | 6290 (ARCH TOP) | | | | | | | |
| W3 | 1800 | 2800 | | | | | | | |
| W4 | 3600 | 6600 | | | | | | | |
| W5 | 3600 | 7500 (ARCH TOP) | | | | | | | |

NOTE:
ALL BRICK WALLS ARE 200 MM THK

DRAWING PURPOSE :

WORKING DRAWING

TITLE :

FOURTH FLOOR PLAN

CLIENT :

PROJECT :

SHIVADITYA GLOBAL

DRAWING STATUS :

ADVANCED COPY

ARCHITECT : Kamal Periw

SCALE 1:150



MAHESWARI & ASSOCIATES
37A, BAKER ROAD, 2nd FLOOR
ALIPUR, KOLKATA - 700 027
www.architectm.com

DATE

INTERIORS

DRAWN BY Simply Das

DRG NO.

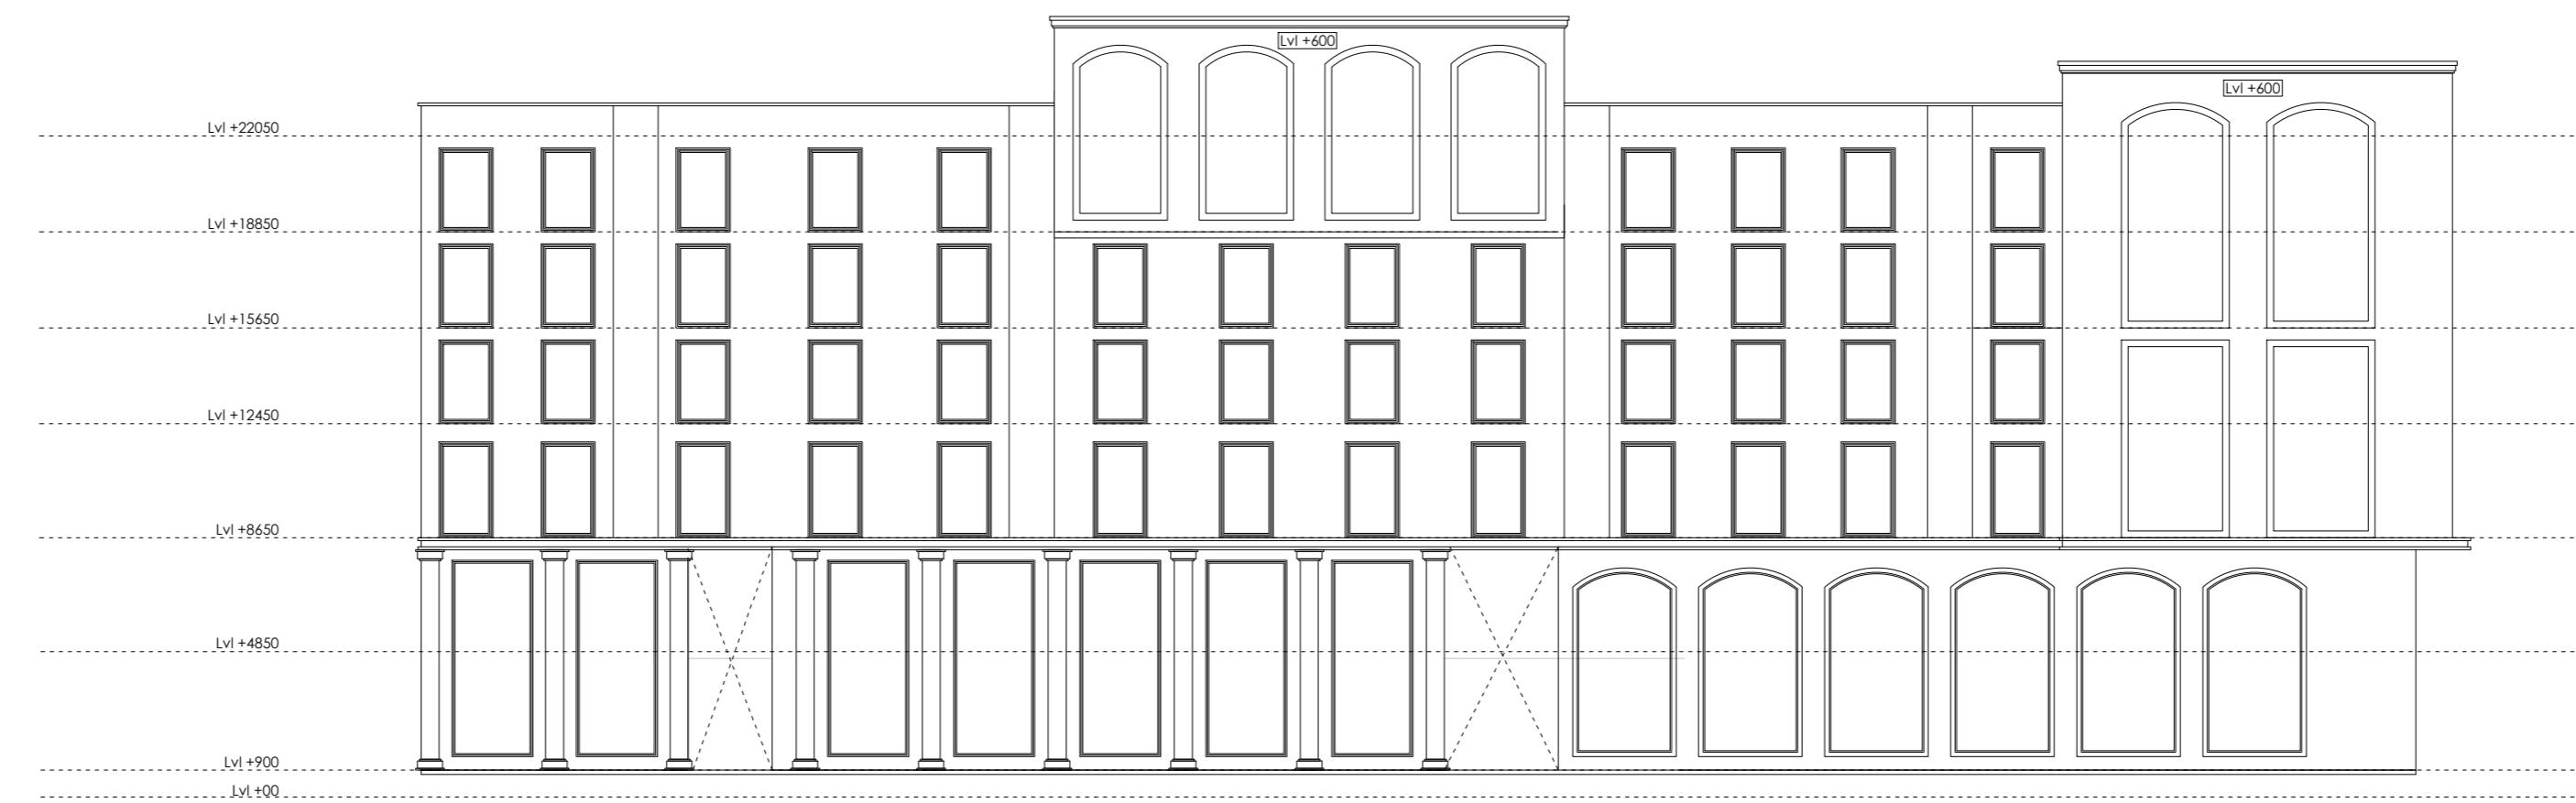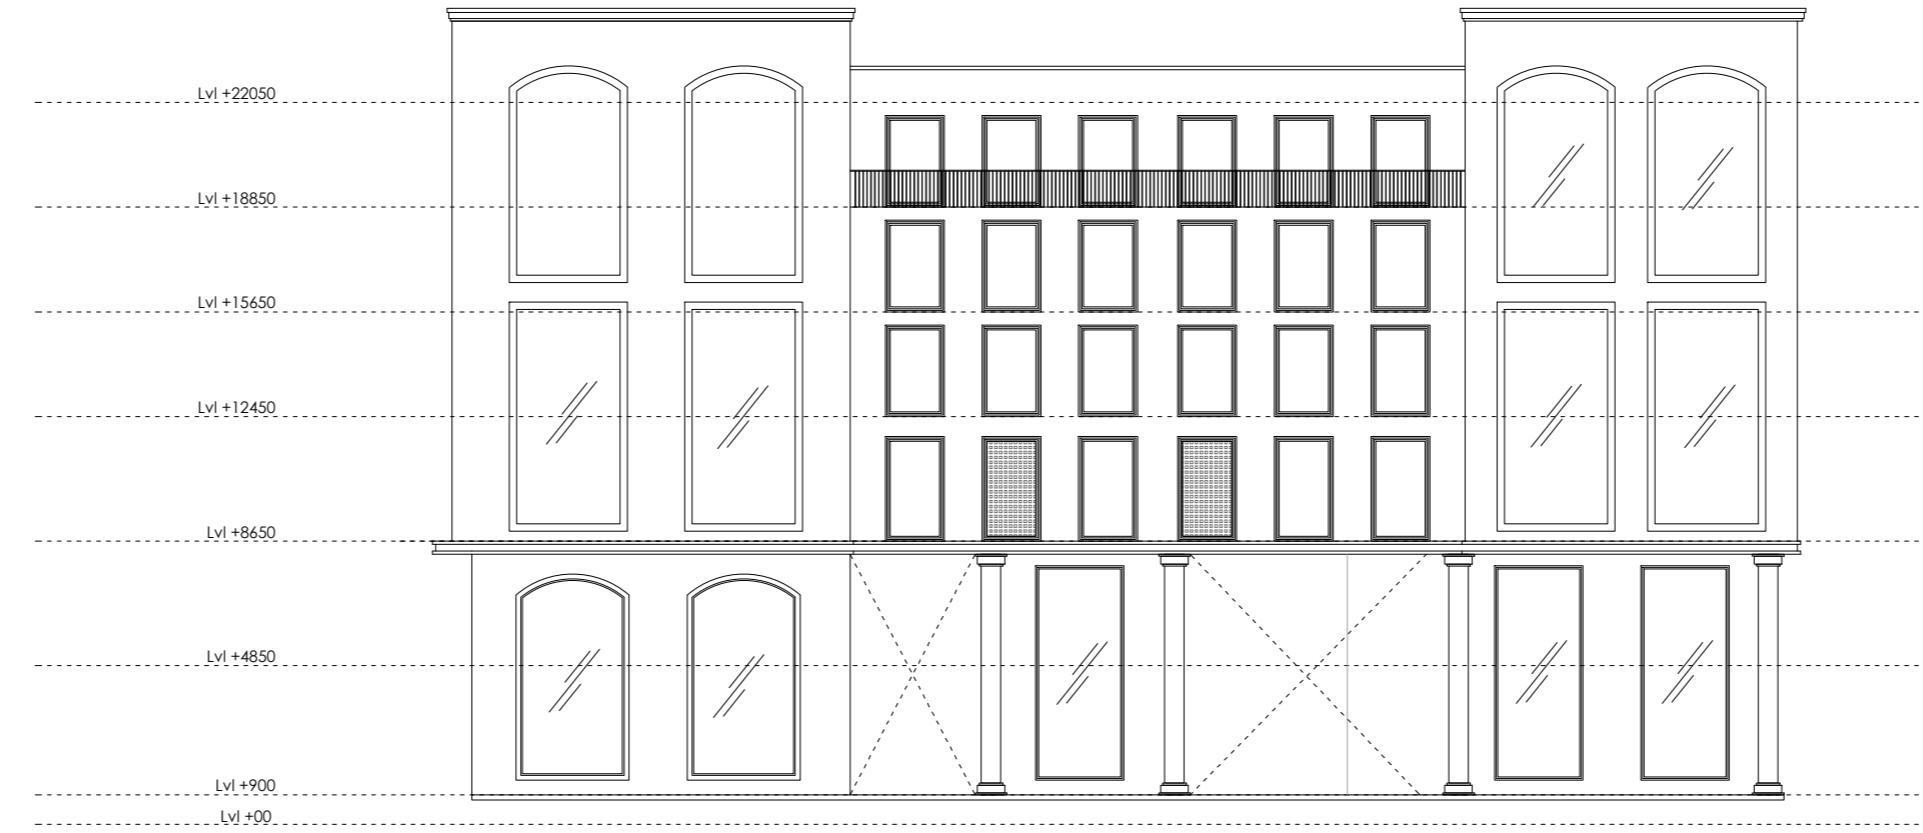

SCHEDULE OF DOORS & WINDOWS

WINDOWS: **DOORS:**

| MKD. | WIDTH | HEIGHT | SILL | LINTEL | MKD | WIDTH | HEIGHT | SILL | LINTEL |
|------|-------|-----------------|------|--------|-----|-------|--------|------|--------|
| W1 | 2700 | 6550 | | | | | | | |
| W2 | 3150 | 6290 (ARCH TOP) | | | | | | | |
| W3 | 1800 | 2800 | | | | | | | |
| W4 | 3600 | 6600 | | | | | | | |
| W5 | 3600 | 7500 (ARCH TOP) | | | | | | | |
| | | | | | | | | | |
| | | | | | | | | | |
| | | | | | | | | | |
| | | | | | | | | | |

NOTE:
ALL BRICK WALLS ARE 200 MM THK

DRAWING PURPOSE :

WORKING DRAWING

TITLE :

ELEVATIONS

PROJECT :


DRAWING STATUS :

SHIVADITYA GLOBAL

ADVANCED COPY



CLIENT :

ARCHITECT : Kamal Periwal

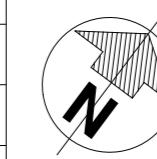

MAHESWARI & ASSOCIATES
37A, BAKER ROAD, 2nd FLOOR
ALIPUR, KOLKATA - 700 027
www.architectm.com

INTERIORS

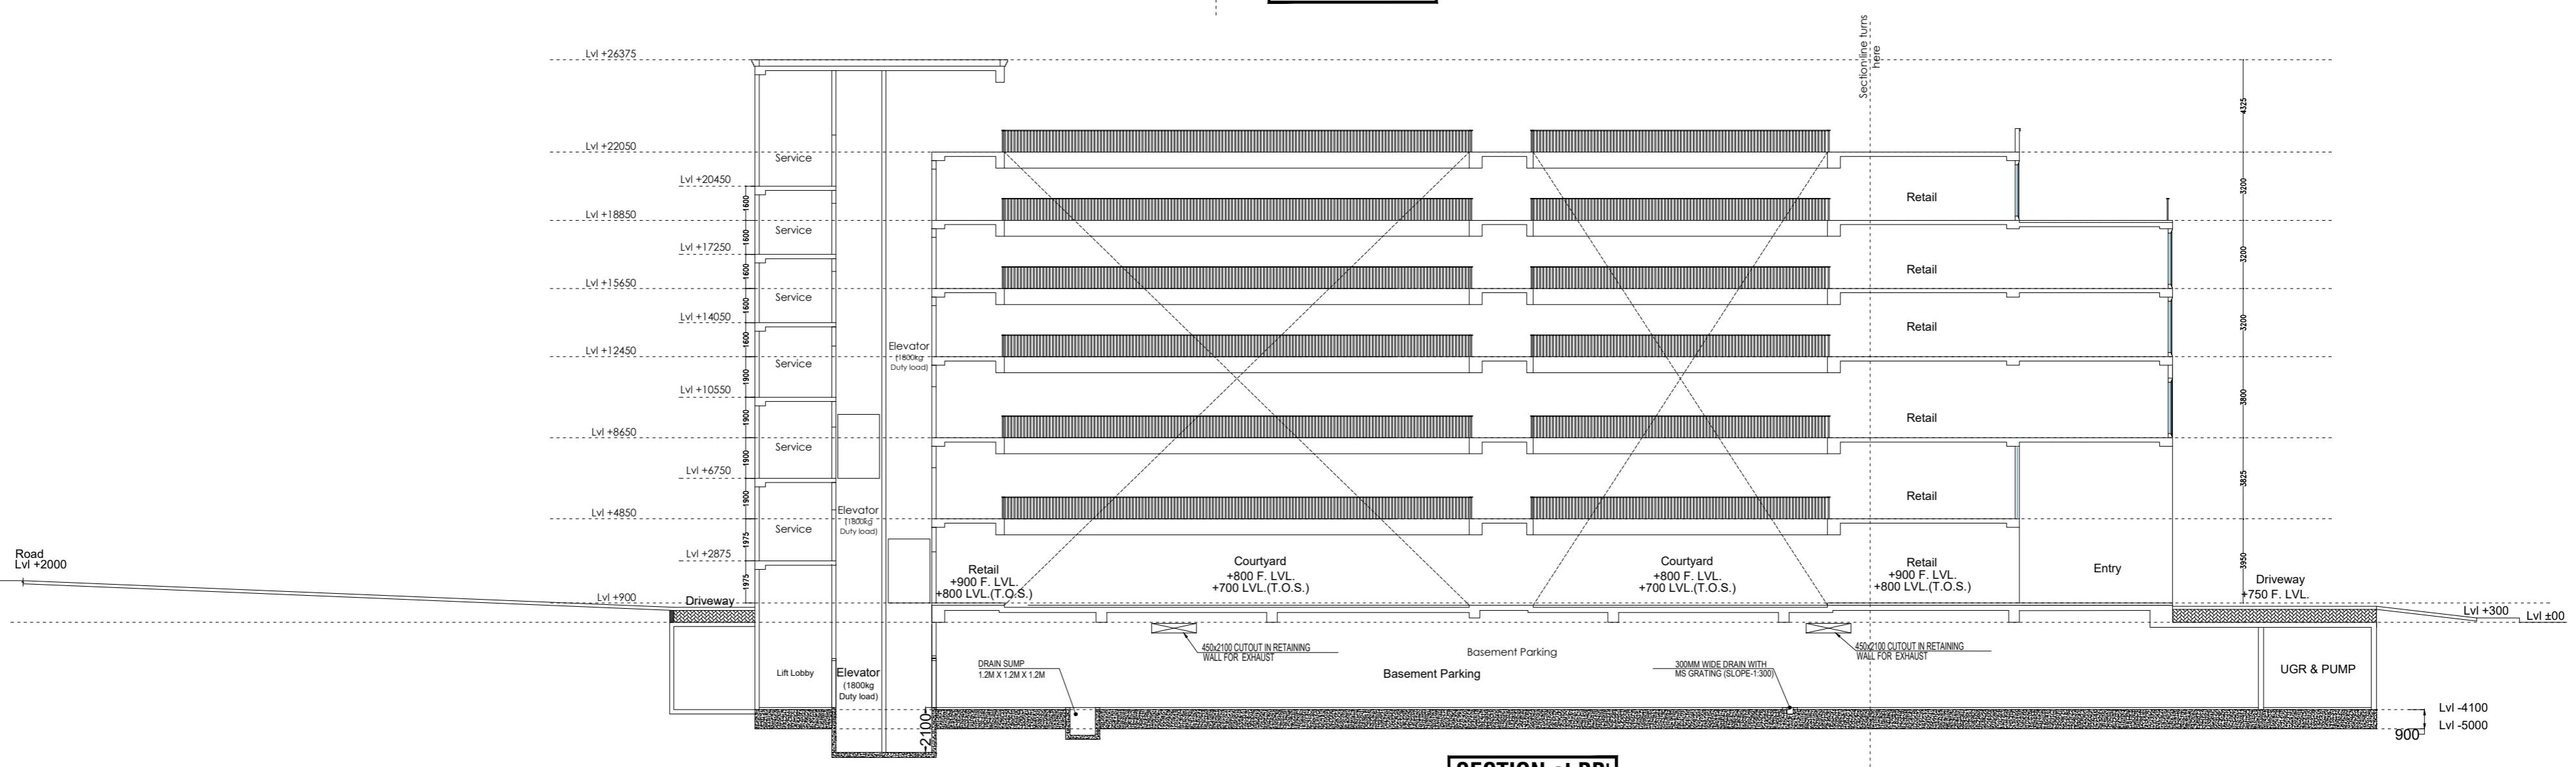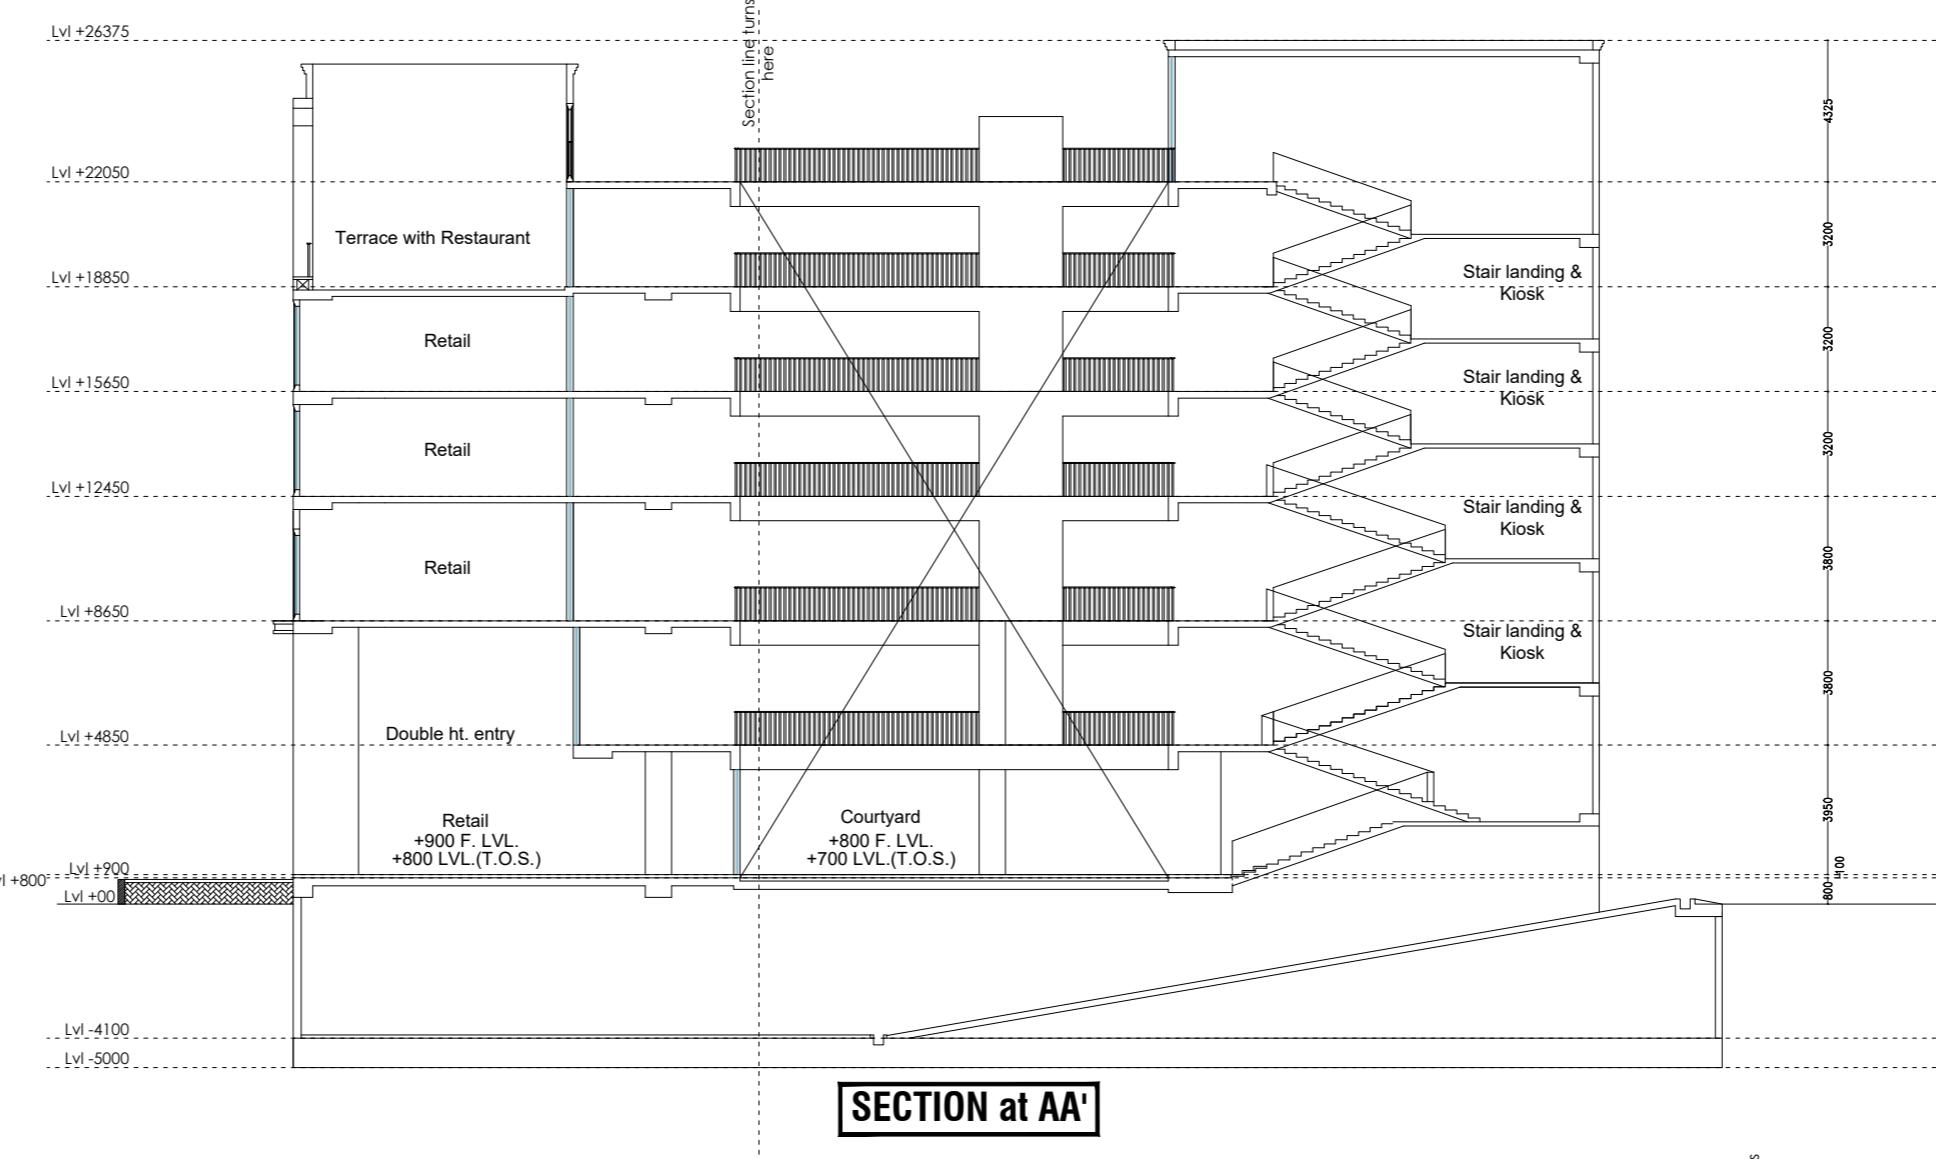

SCHEDULE OF DOORS & WINDOWS

WINDOWS: DOORS:

| MKD. | WIDTH | HEIGHT | SILL | LINTEL | MKD | WIDTH | HEIGHT | SILL | LINTEL |
|------|-------|-----------------|------|--------|-----|-------|--------|------|--------|
| W1 | 2700 | 6550 | | | | | | | |
| W2 | 3150 | 6290 (ARCH TOP) | | | | | | | |
| W3 | 1800 | 2800 | | | | | | | |
| W4 | 3600 | 6600 | | | | | | | |
| W5 | 3600 | 7500 (ARCH TOP) | | | | | | | |

NOTE:
ALL BRICK WALLS ARE 200 MM THK

DRAWING PURPOSE :

WORKING DRAWING

TITLE :

SECTIONS

CLIENT :


PROJECT :

DRAWING STATUS :

ARCHITECT : Kamal Periwal


SHIVADITYA GLOBAL

ADVANCED COPY

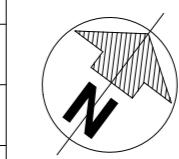

ARCHITECTS
MAHESWARI & ASSOCIATES
37A, BAKER ROAD, 2nd FLOOR
ALIPUR, KOLKATA - 700 027
www.architectm.com

INTERIORS

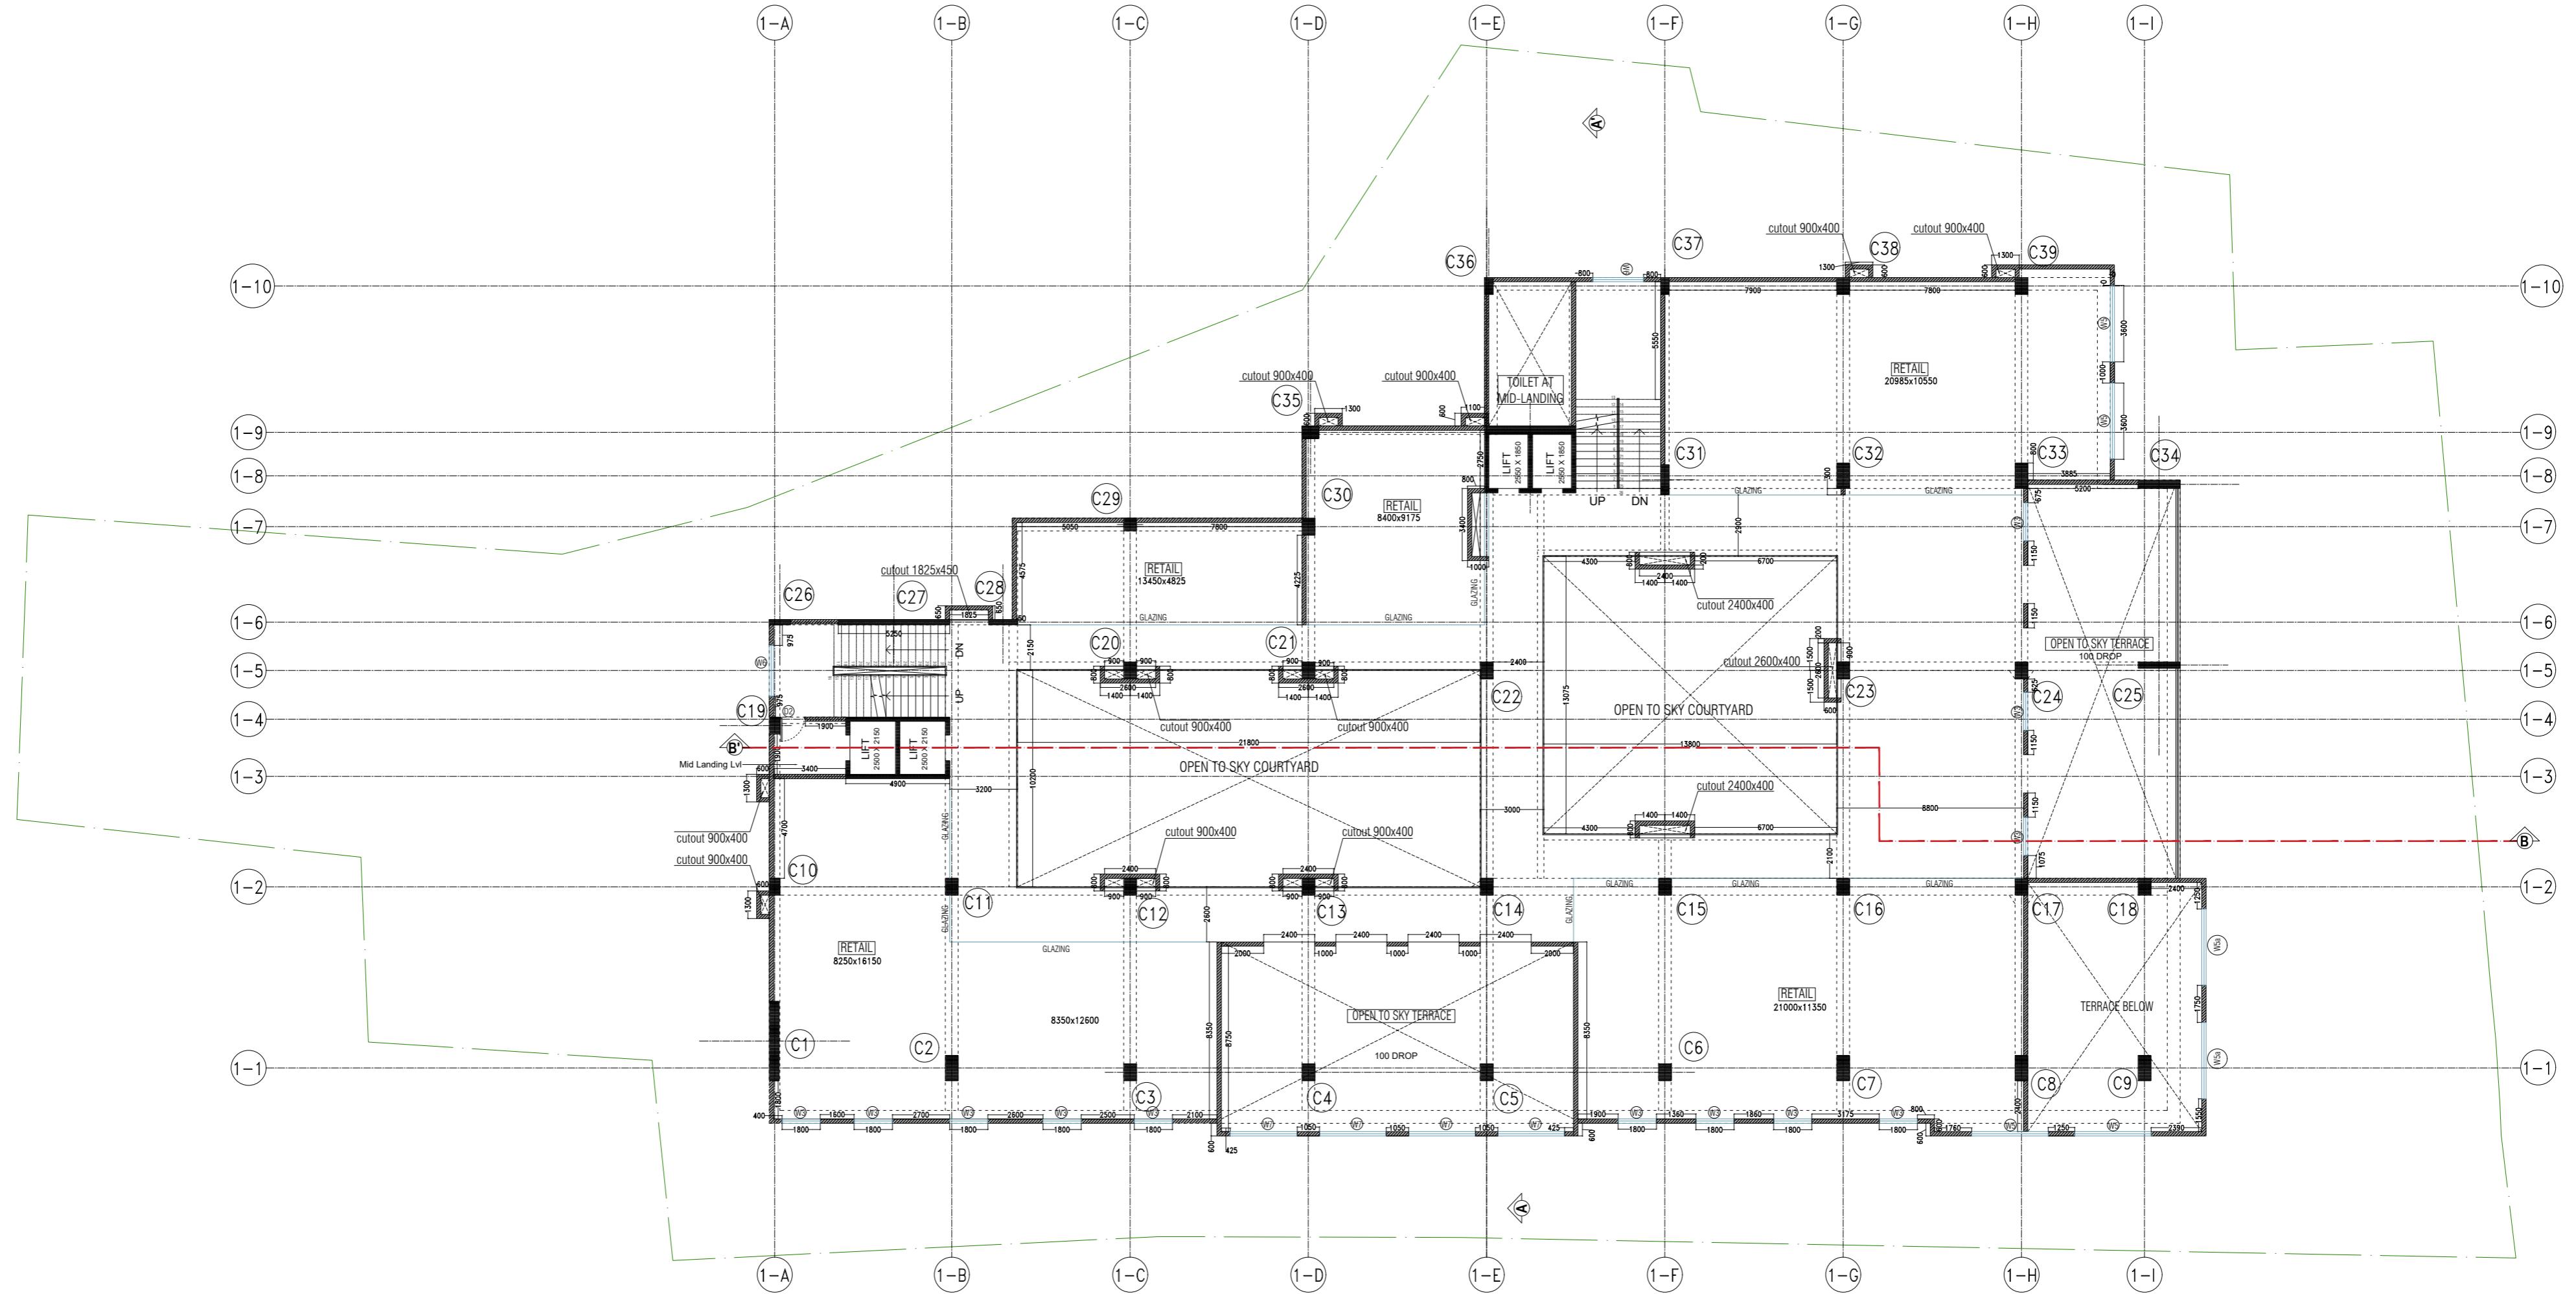

5TH FLOOR PLAN

BUA 15160 SQFT

SCHEDULE OF DOORS & WINDOWS

WINDOWS: DOORS:

| MKD. | WIDTH | HEIGHT | SILL | LINTEL | MKD | WIDTH | HEIGHT | SILL | LINTEL |
|------|-------|-----------------|------|--------|-----|-------|--------|------|--------|
| W1 | 2700 | 6550 | | | | | | | |
| W2 | 3150 | 6290 (ARCH TOP) | | | | | | | |
| W3 | 1800 | 2800 | | | | | | | |
| W4 | 3600 | 6600 | | | | | | | |
| W5 | 3600 | 7500 (ARCH TOP) | | | | | | | |

NOTE:
ALL BRICK WALLS ARE 200 MM THK

DRAWING PURPOSE :

WORKING DRAWING

TITLE :

FIFTH FLOOR PLAN

CLIENT :

PROJECT :

SHIVADITYA GLOBAL

DRAWING STATUS :

ADVANCED COPY


ARCHITECT : Kamal Periwai

SCALE 1:150

DATE


DRAWN BY Simply Das


DRG NO.

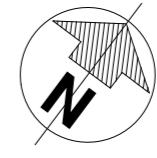

MAHESWARI & ASSOCIATES
37A, BAKER ROAD, 2nd FLOOR
ALIPUR, KOLKATA - 700 027
www.architectm.com



INTERIORS

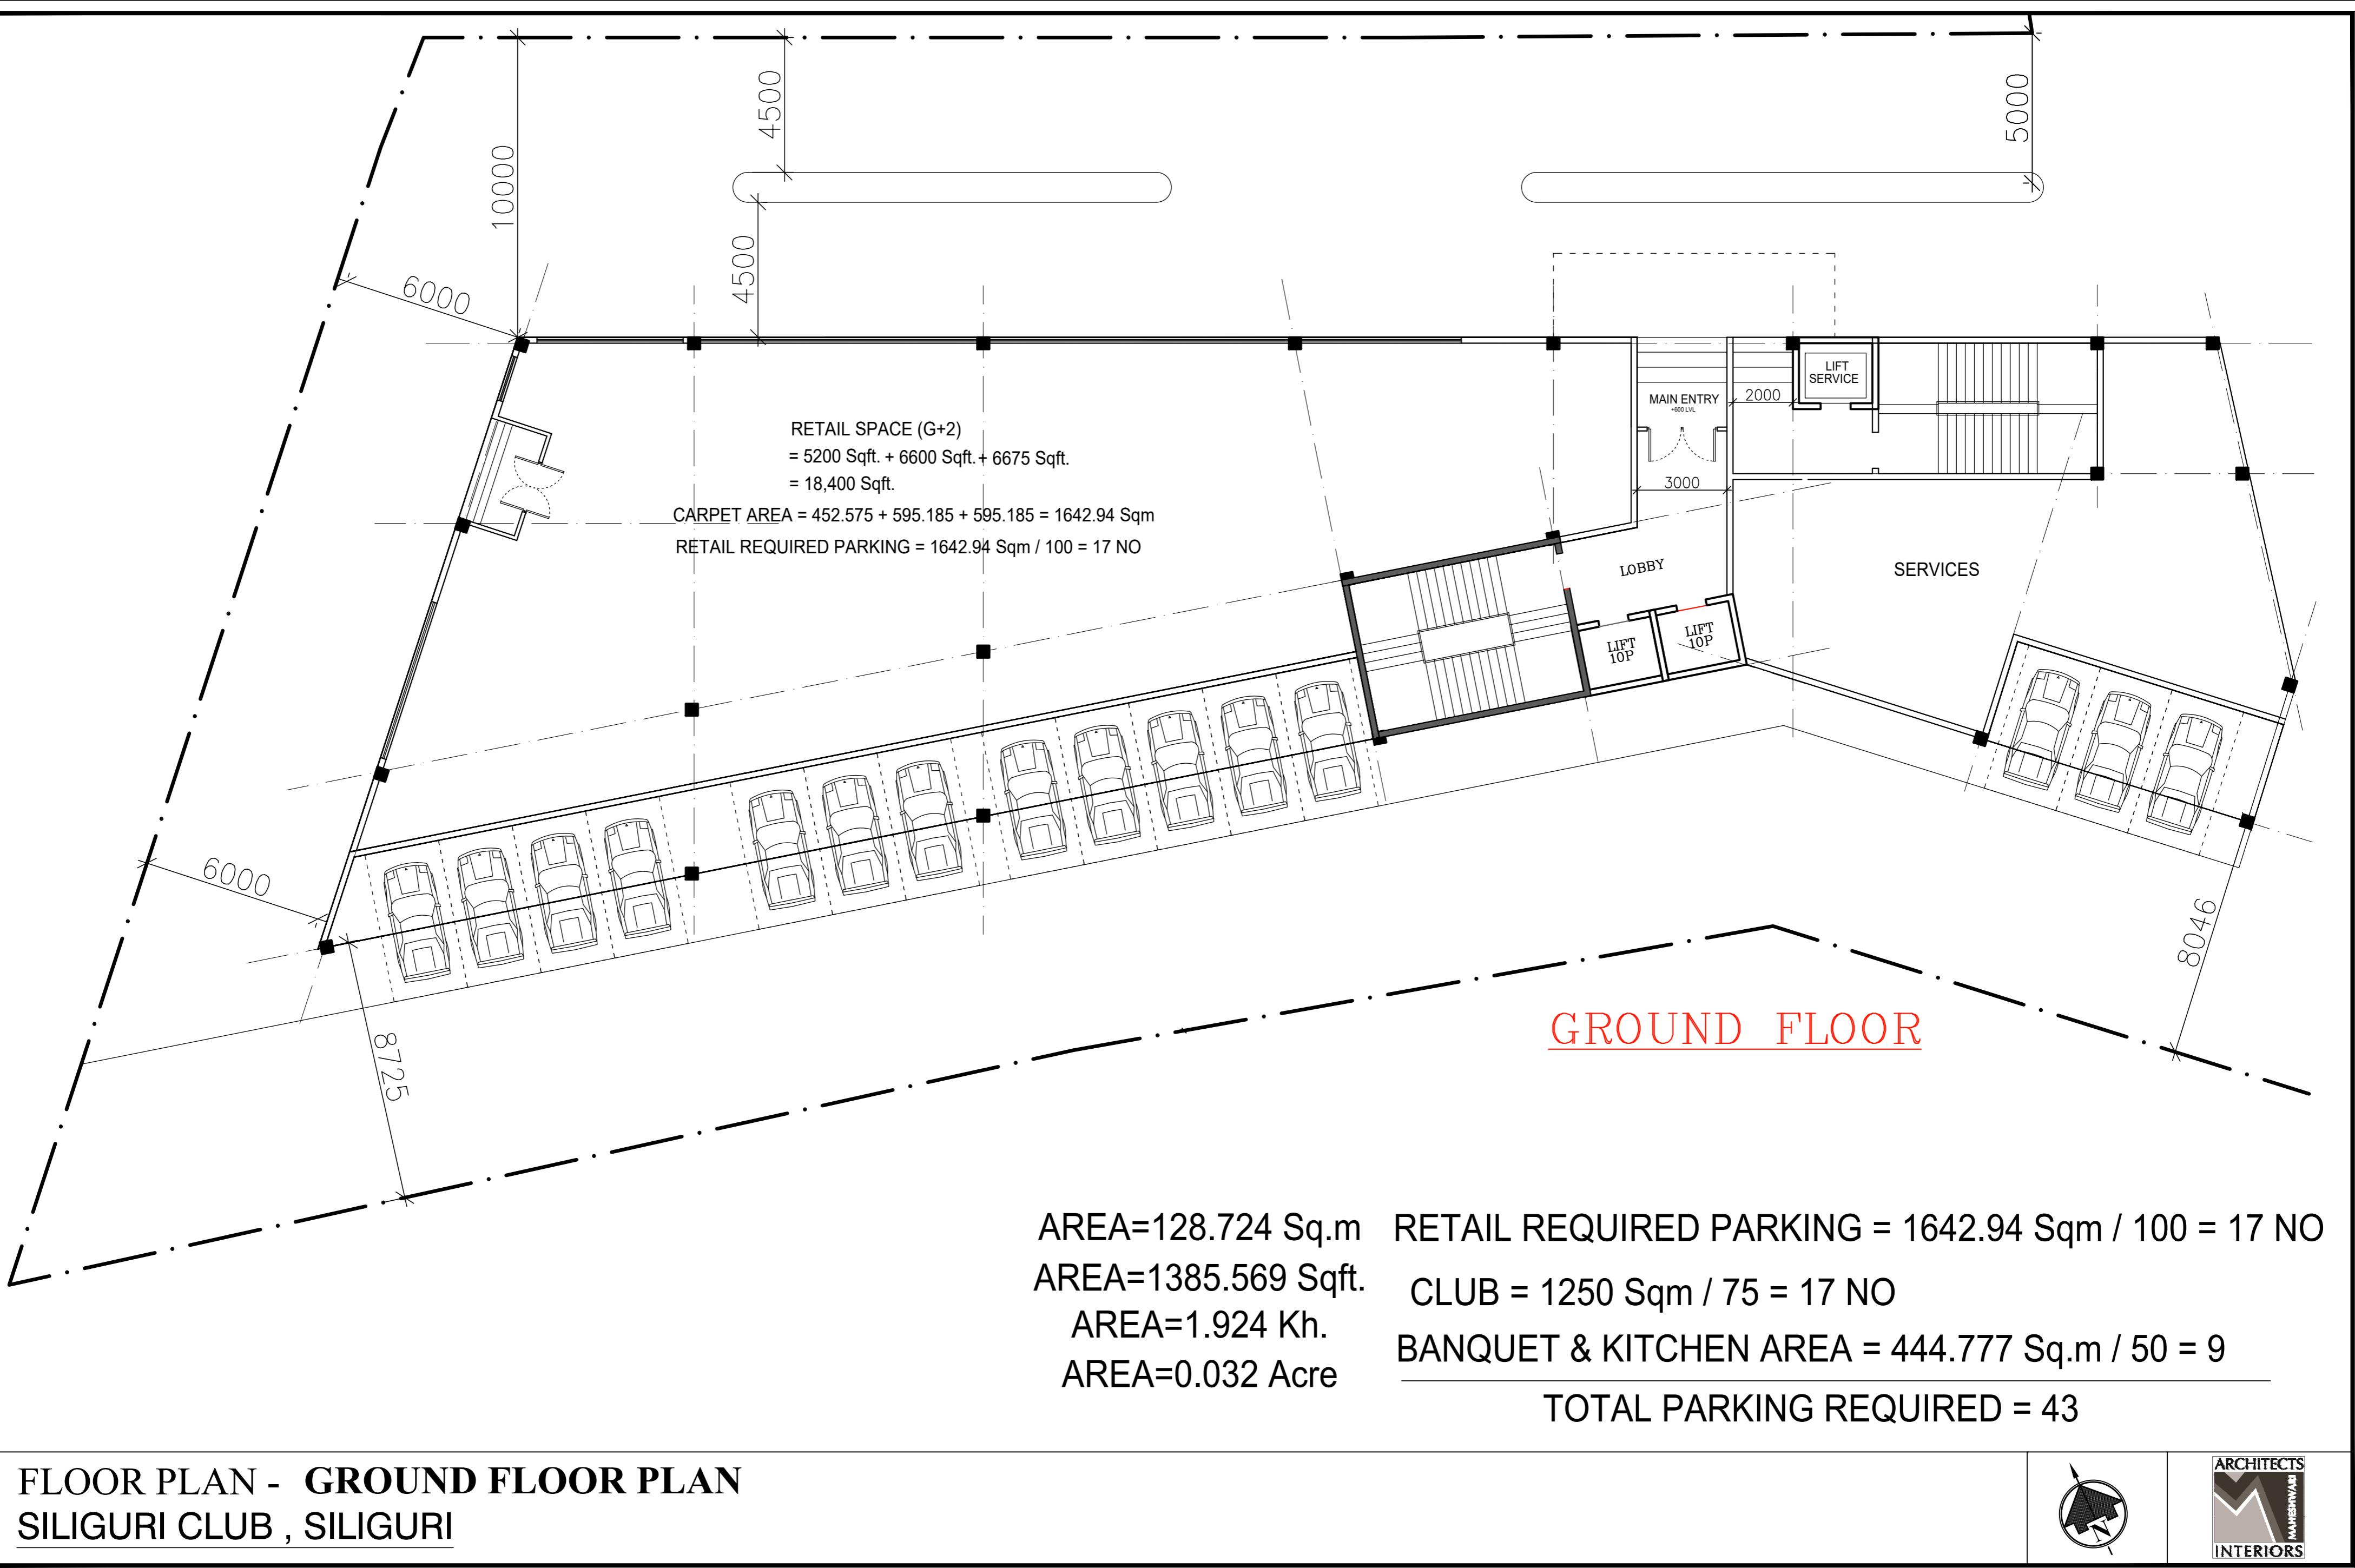

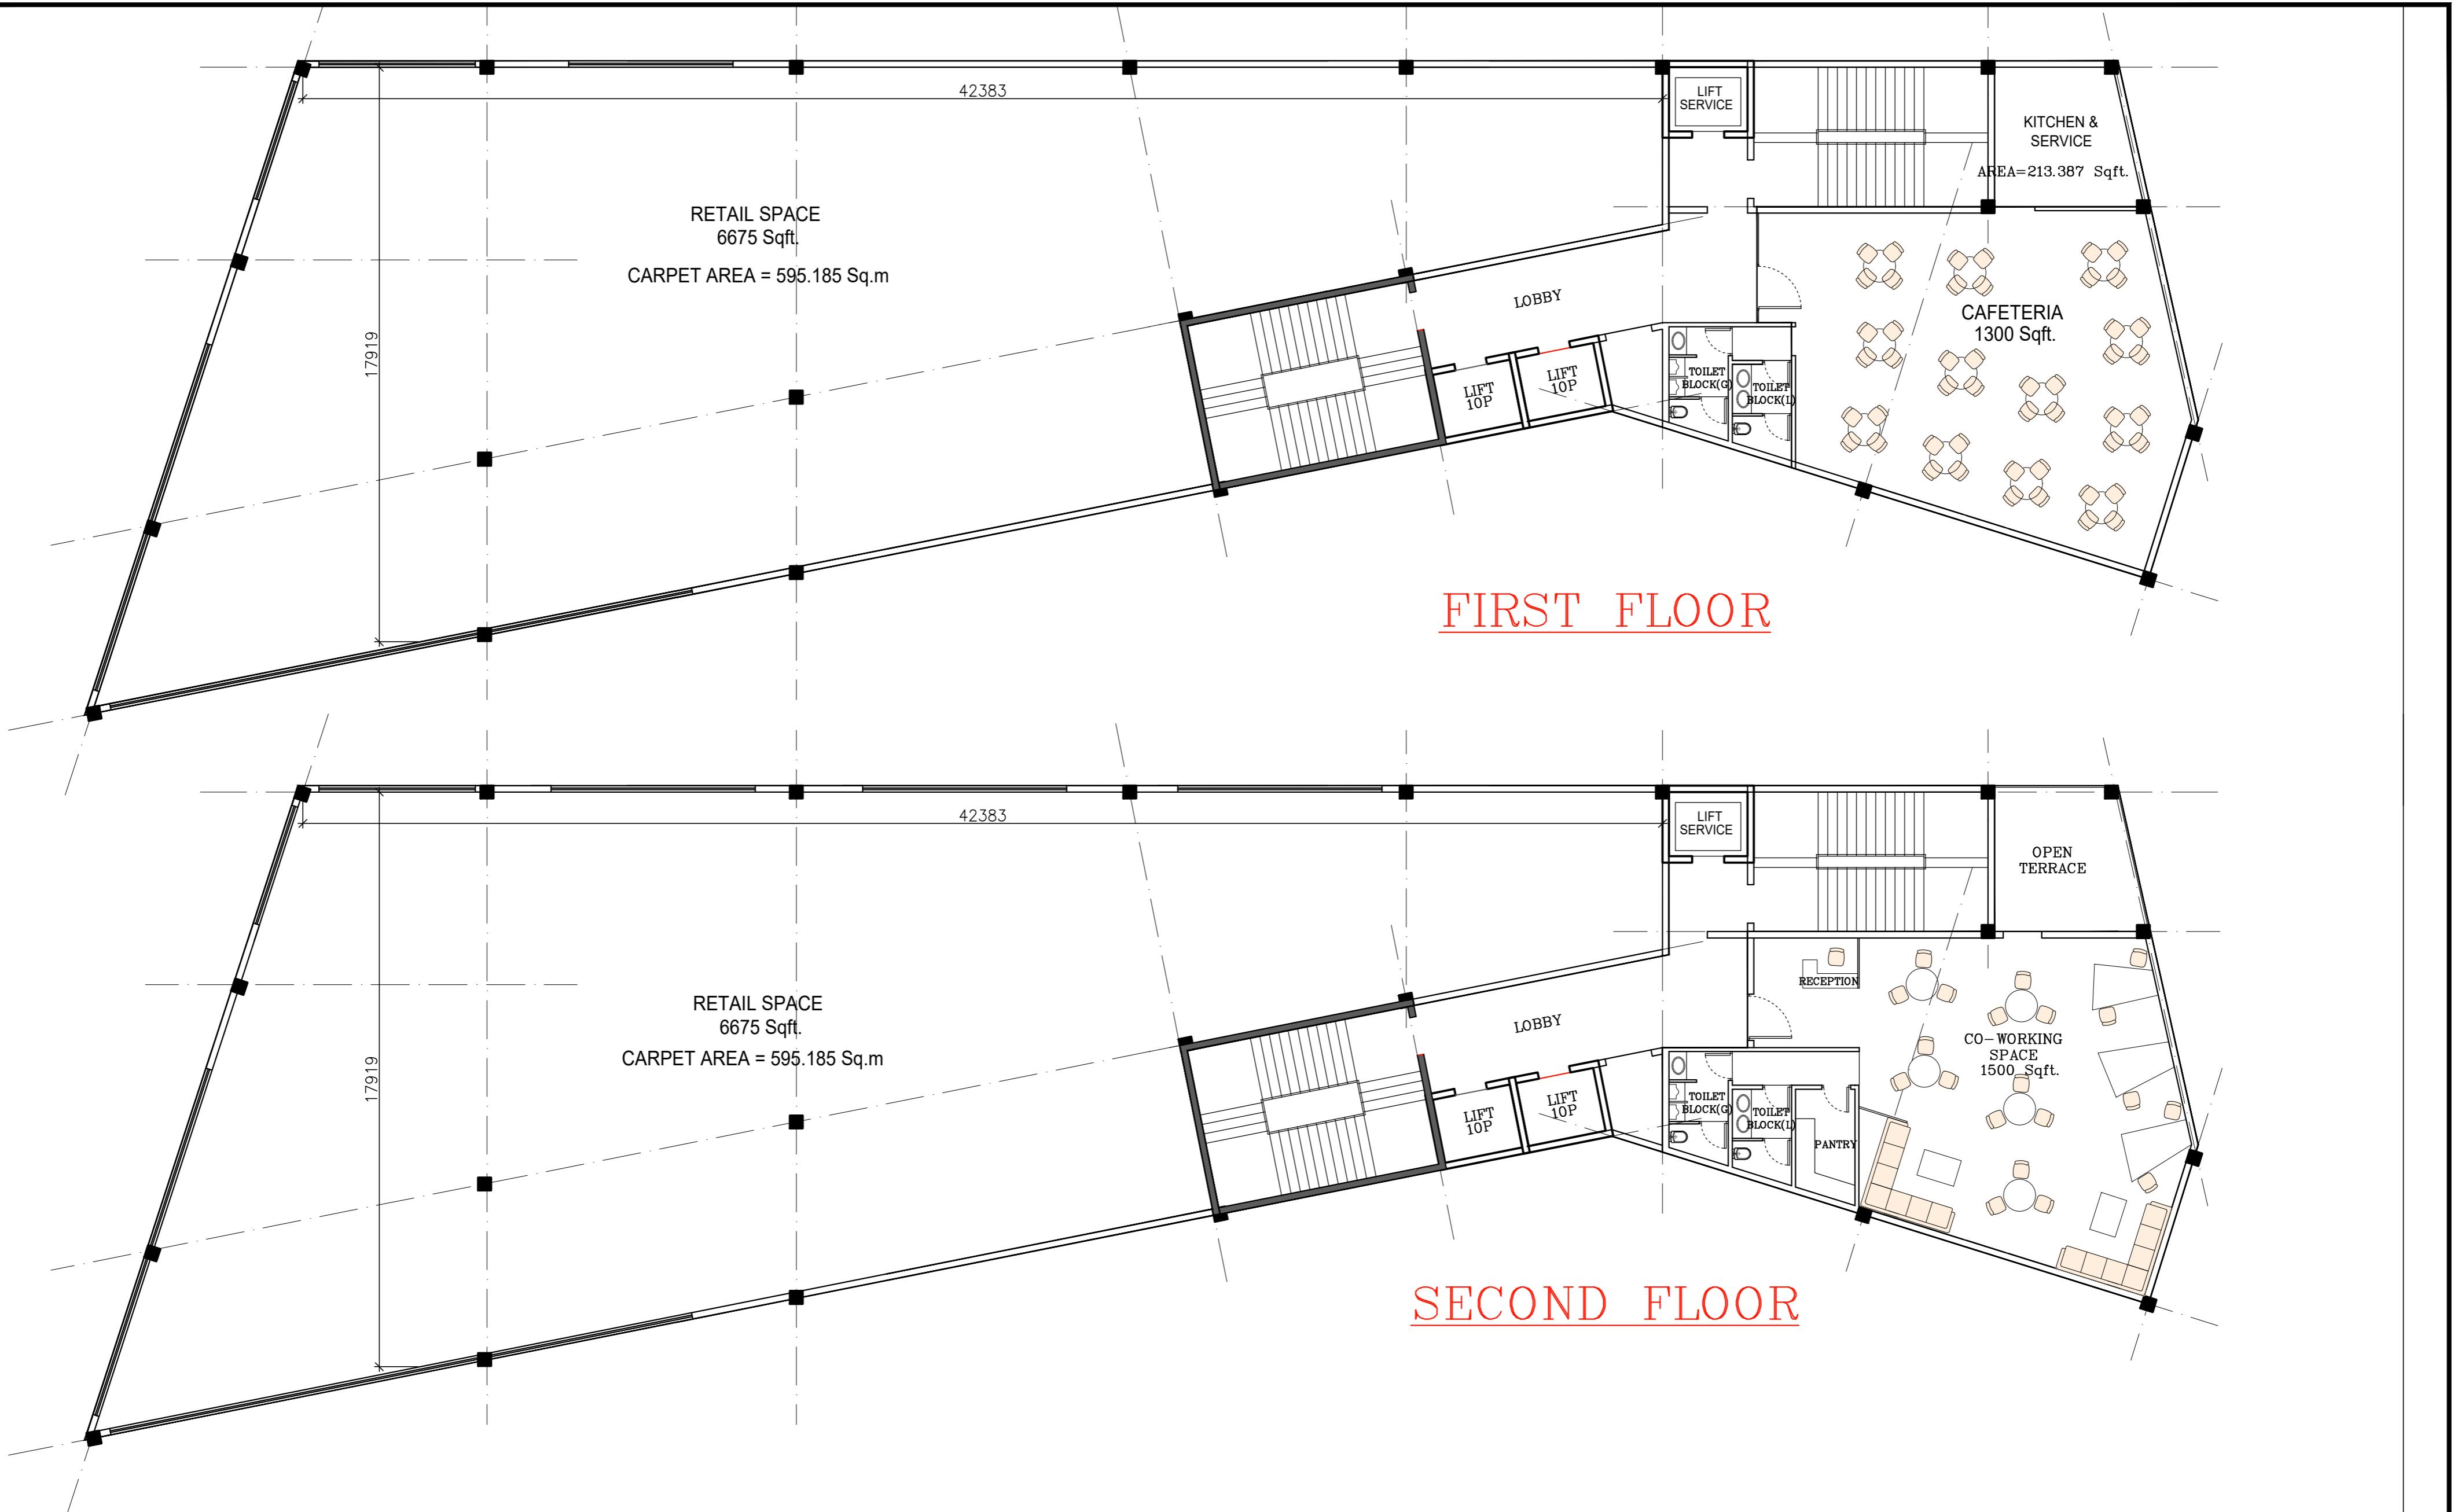



FLOOR PLAN - FIRST FLOOR PLAN & SECOND FLOOR PLAN
SILIGURI CLUB , SILIGURI



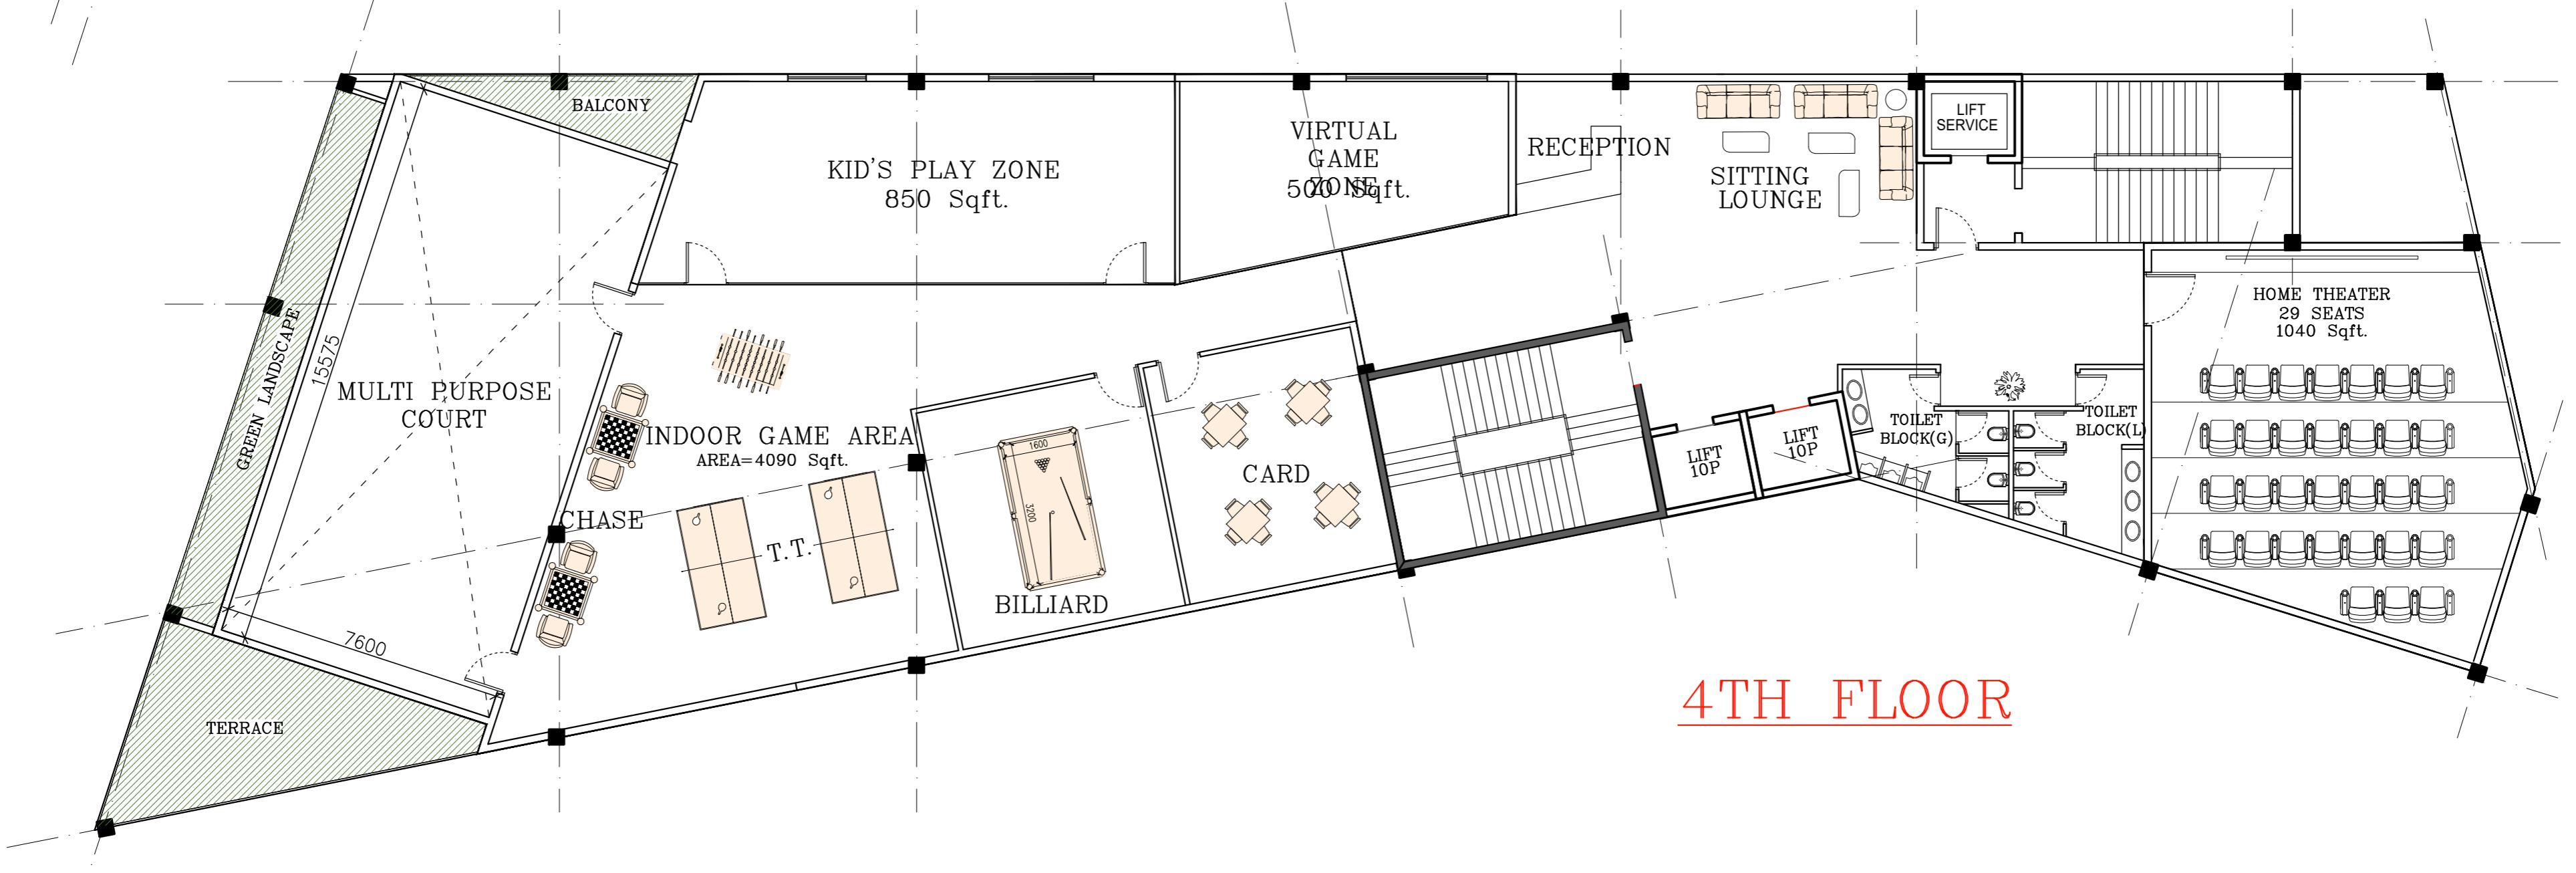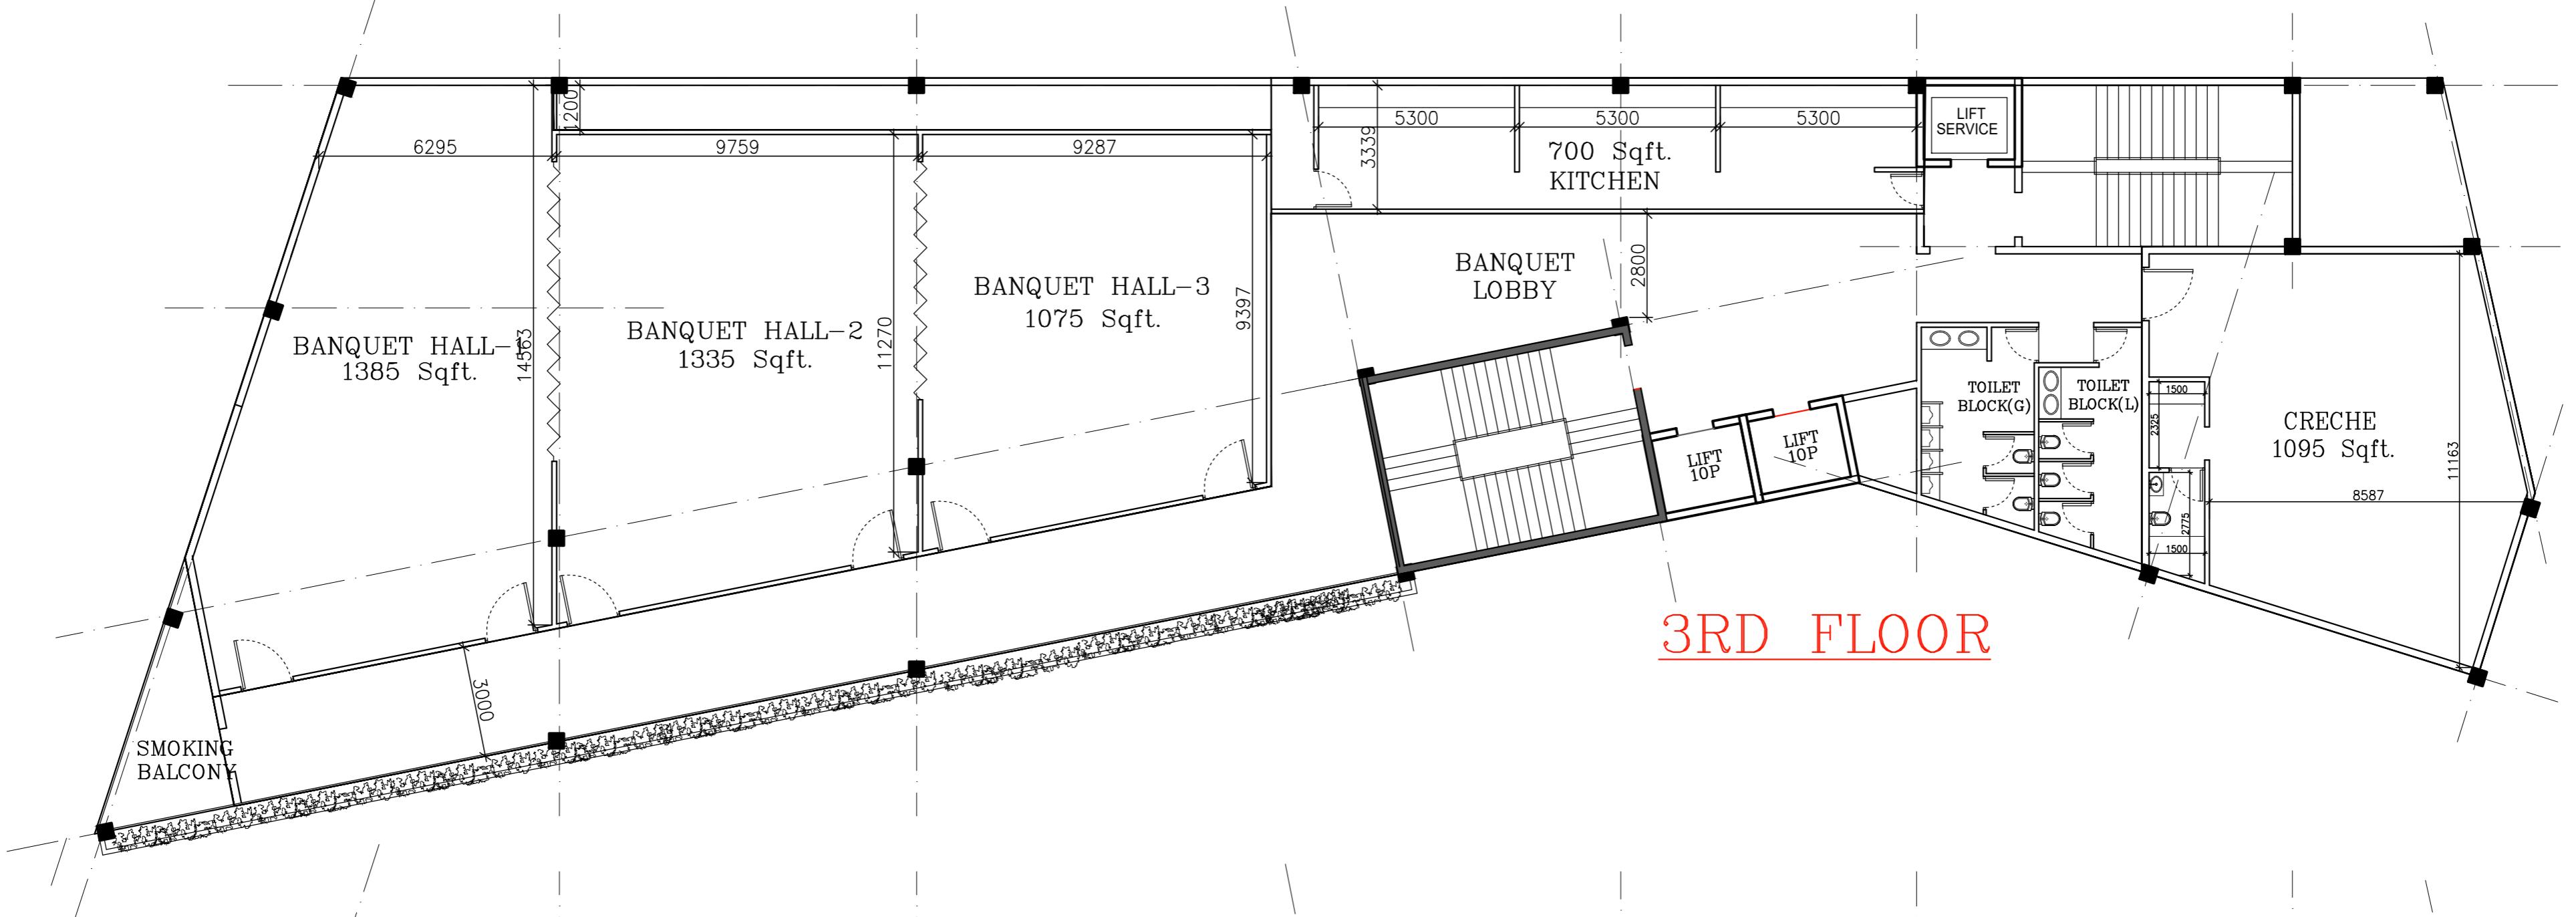


FLOOR PLAN - THIRD FLOOR PLAN & FORTH FLOOR PLAN
SILIGURI CLUB , SILIGURI

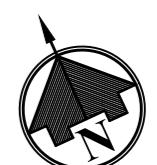

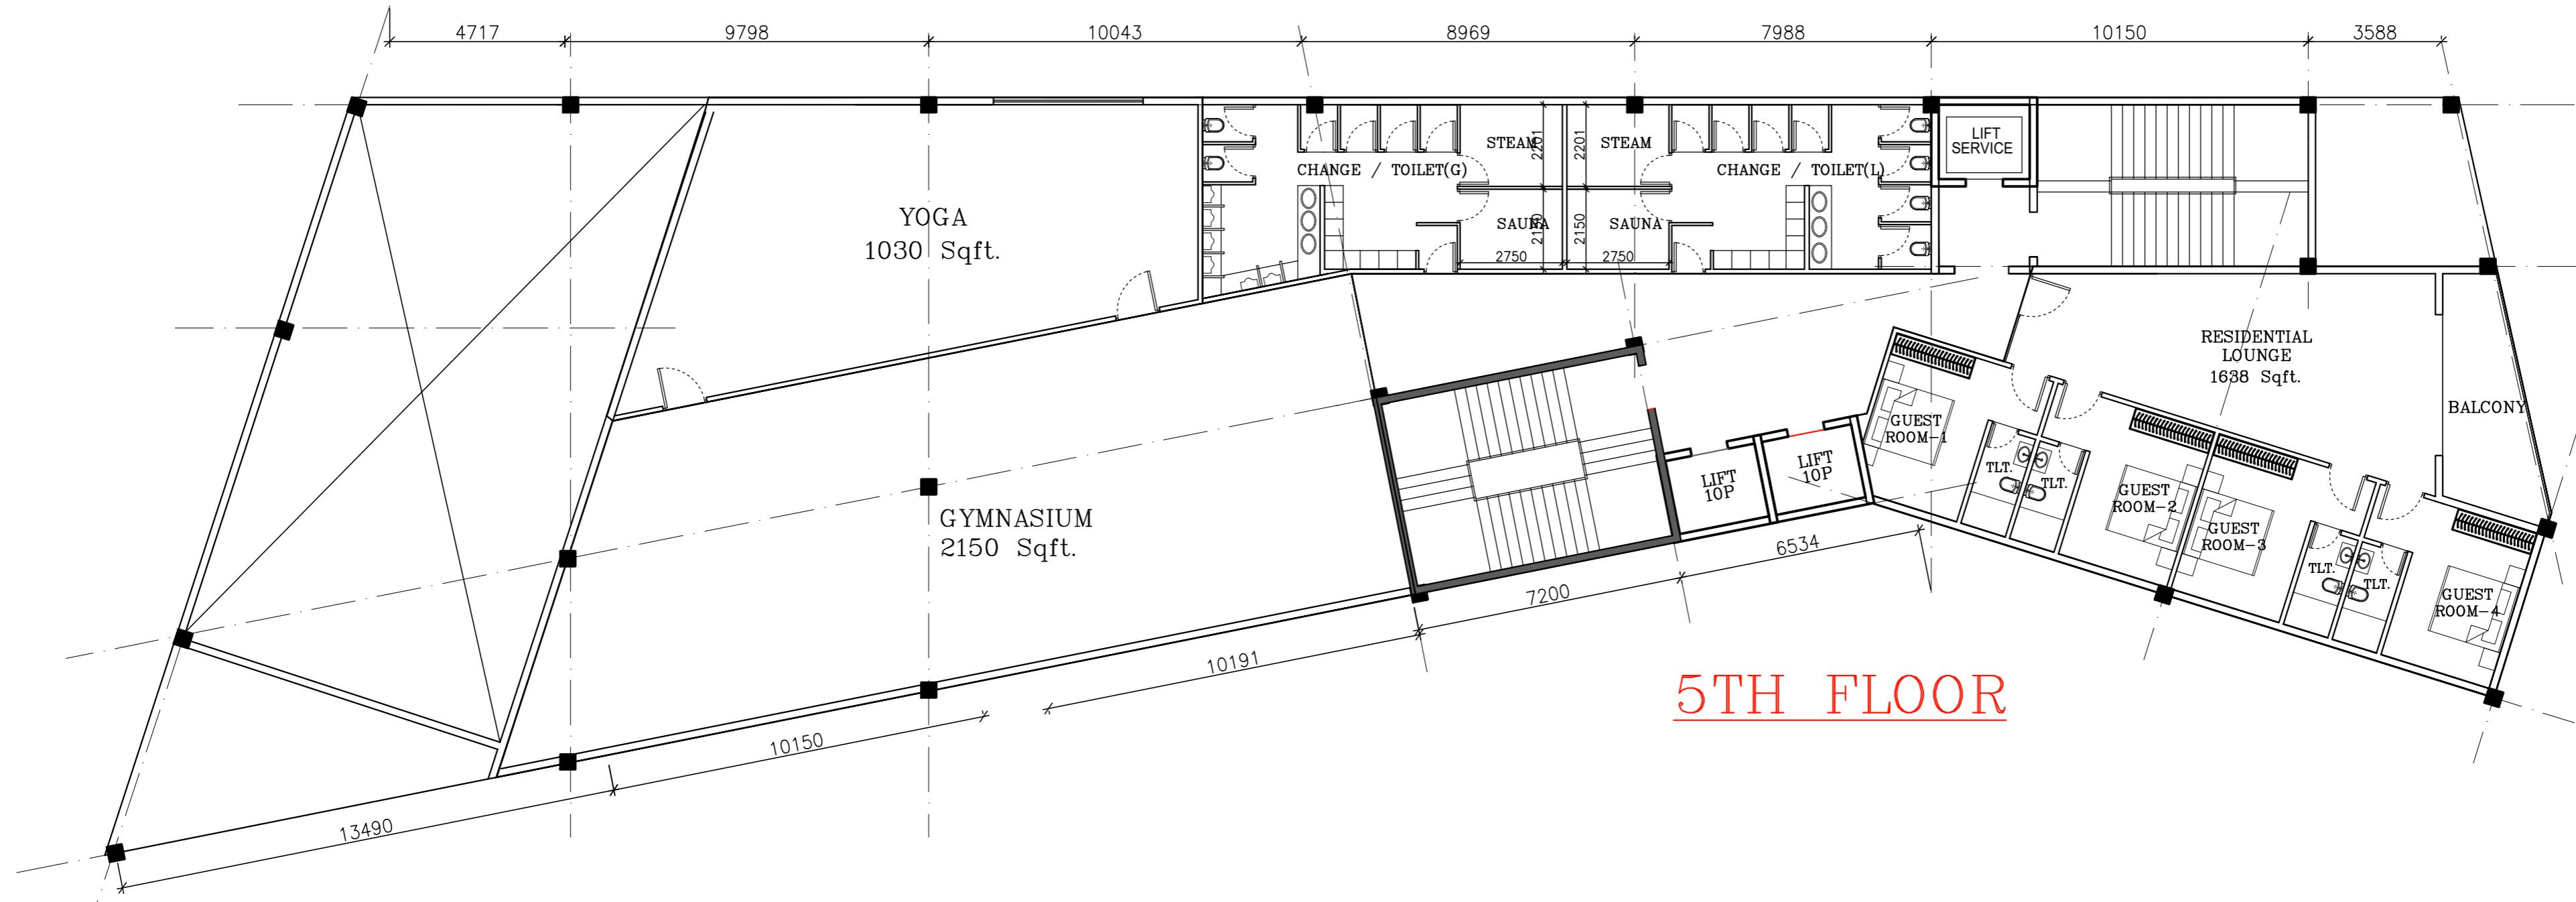

5TH FLOOR

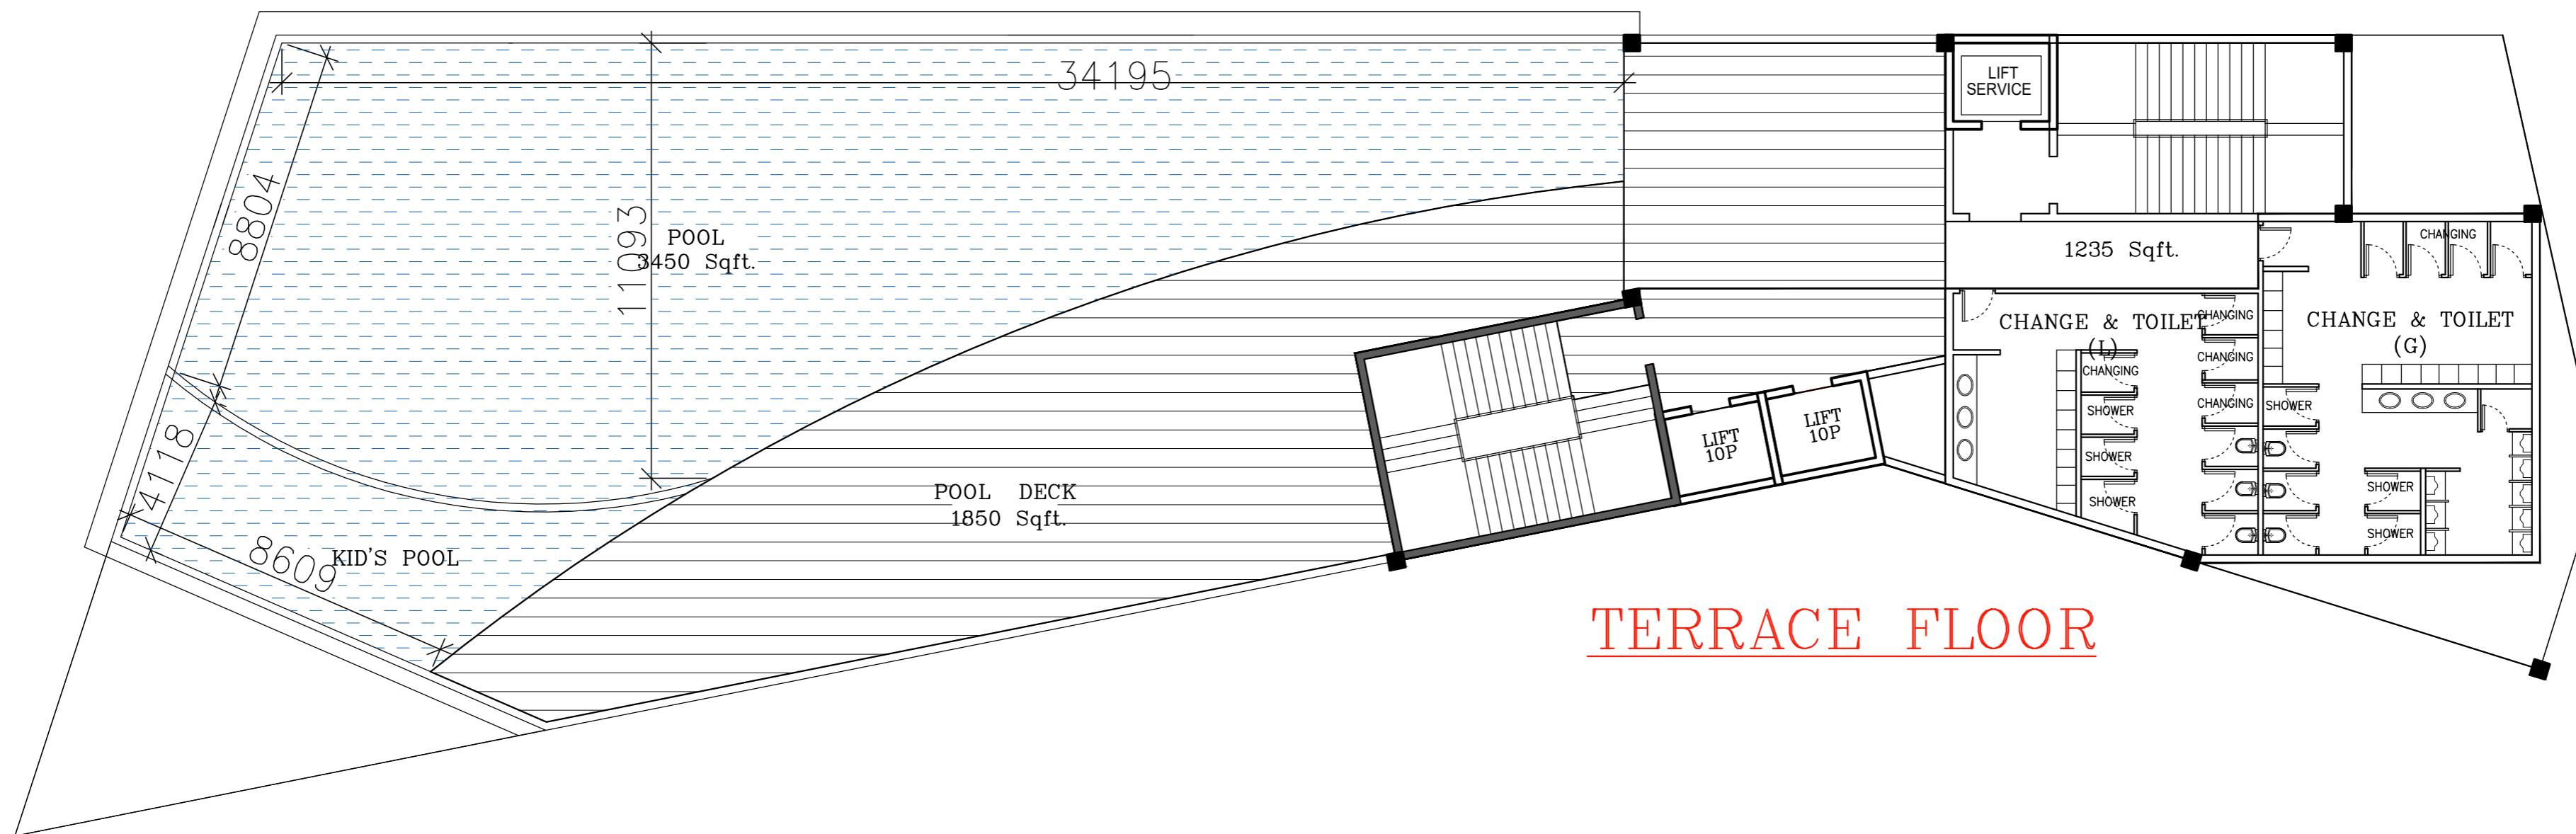

TERRACE FLOOR

FLOOR PLAN - FIFTH FLOOR PLAN AND TERRACE PLAN SILIGURI CLUB , SILIGURI

