


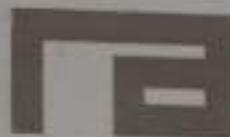

**RAJ AGARWAL AND ASSOCIATES
8B, ROYD STREET, KOLKATA**



Date: 15.11.2017


TO WHOMSOEVER IT MAY CONCERN

This is to certify that Ms Simply Das, final year student of Architecture Department of Piloo Mody College of Architecture, Cuttack has undergone training with us from **5th June 2017 to 15th November 2017** as a trainee.


During the period of her assignment, we have found her very hardworking, sincere, disciplined, and devoted to her work. We wish her good luck & wish her all the very best in her future endeavor.


Thanks & Regards,


RAJ AGARWAL & ASSOCIATES

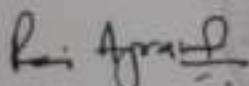

(Ar. Raj Kumar Agarwal)

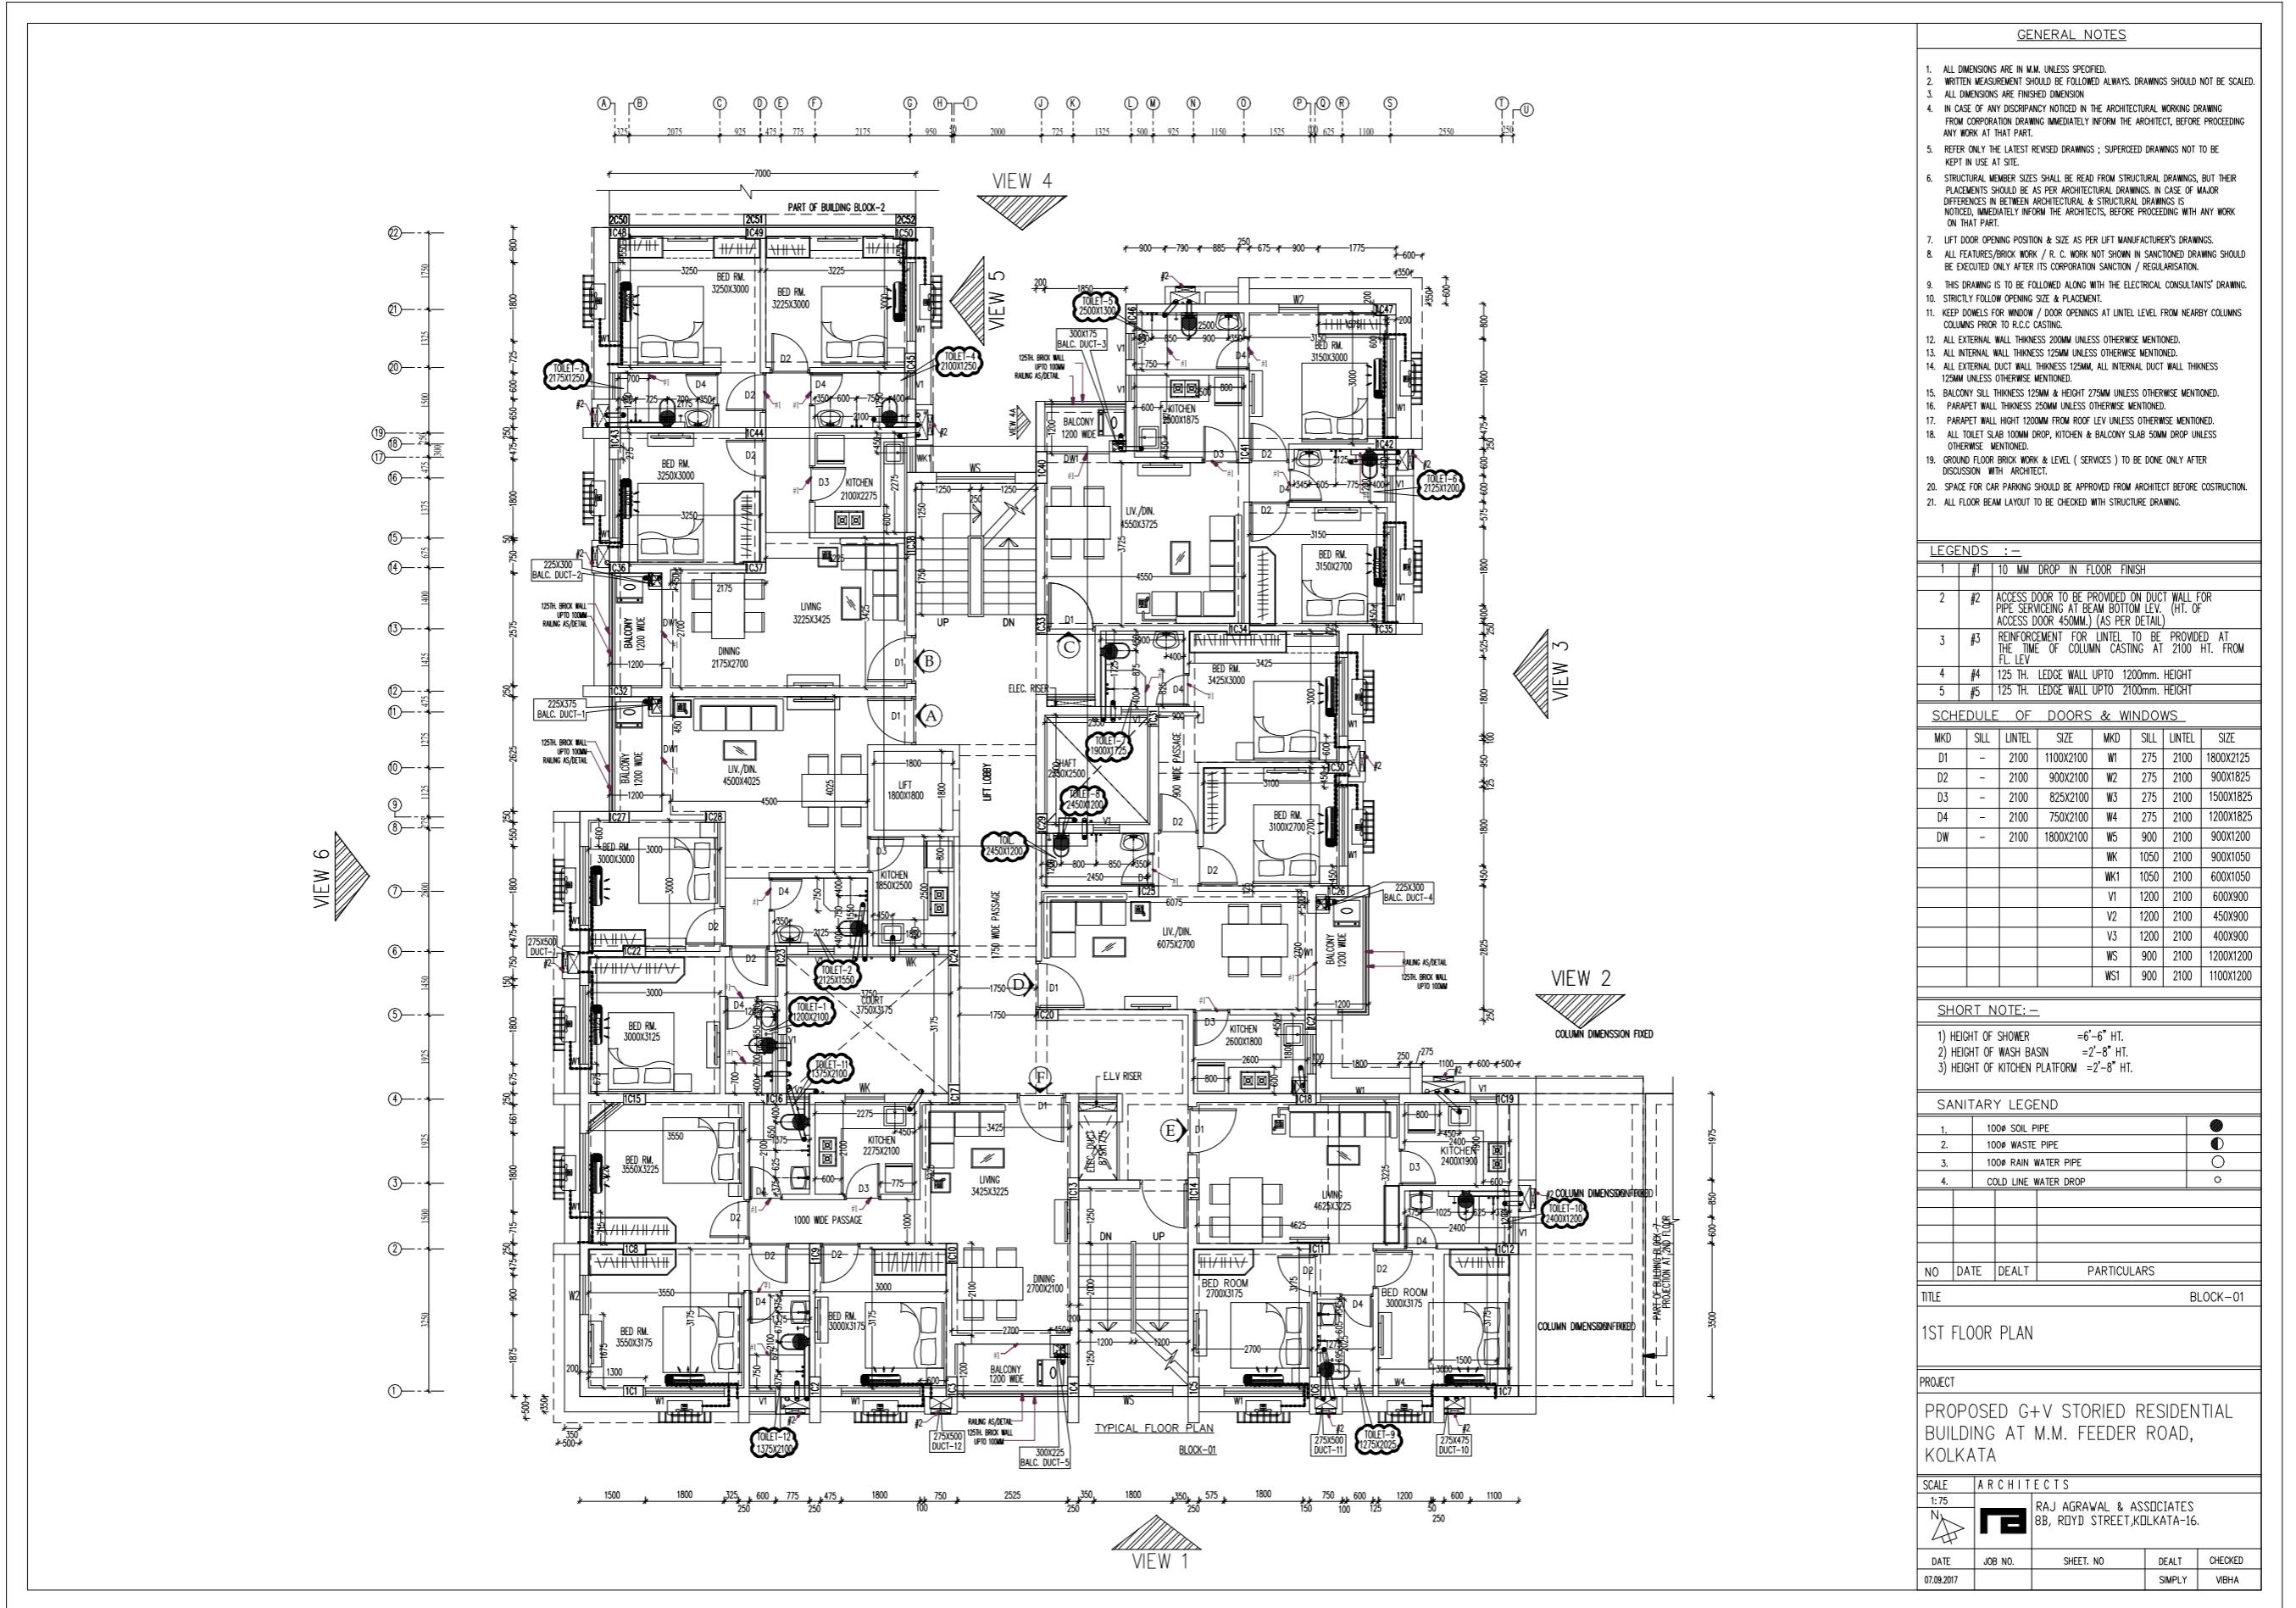

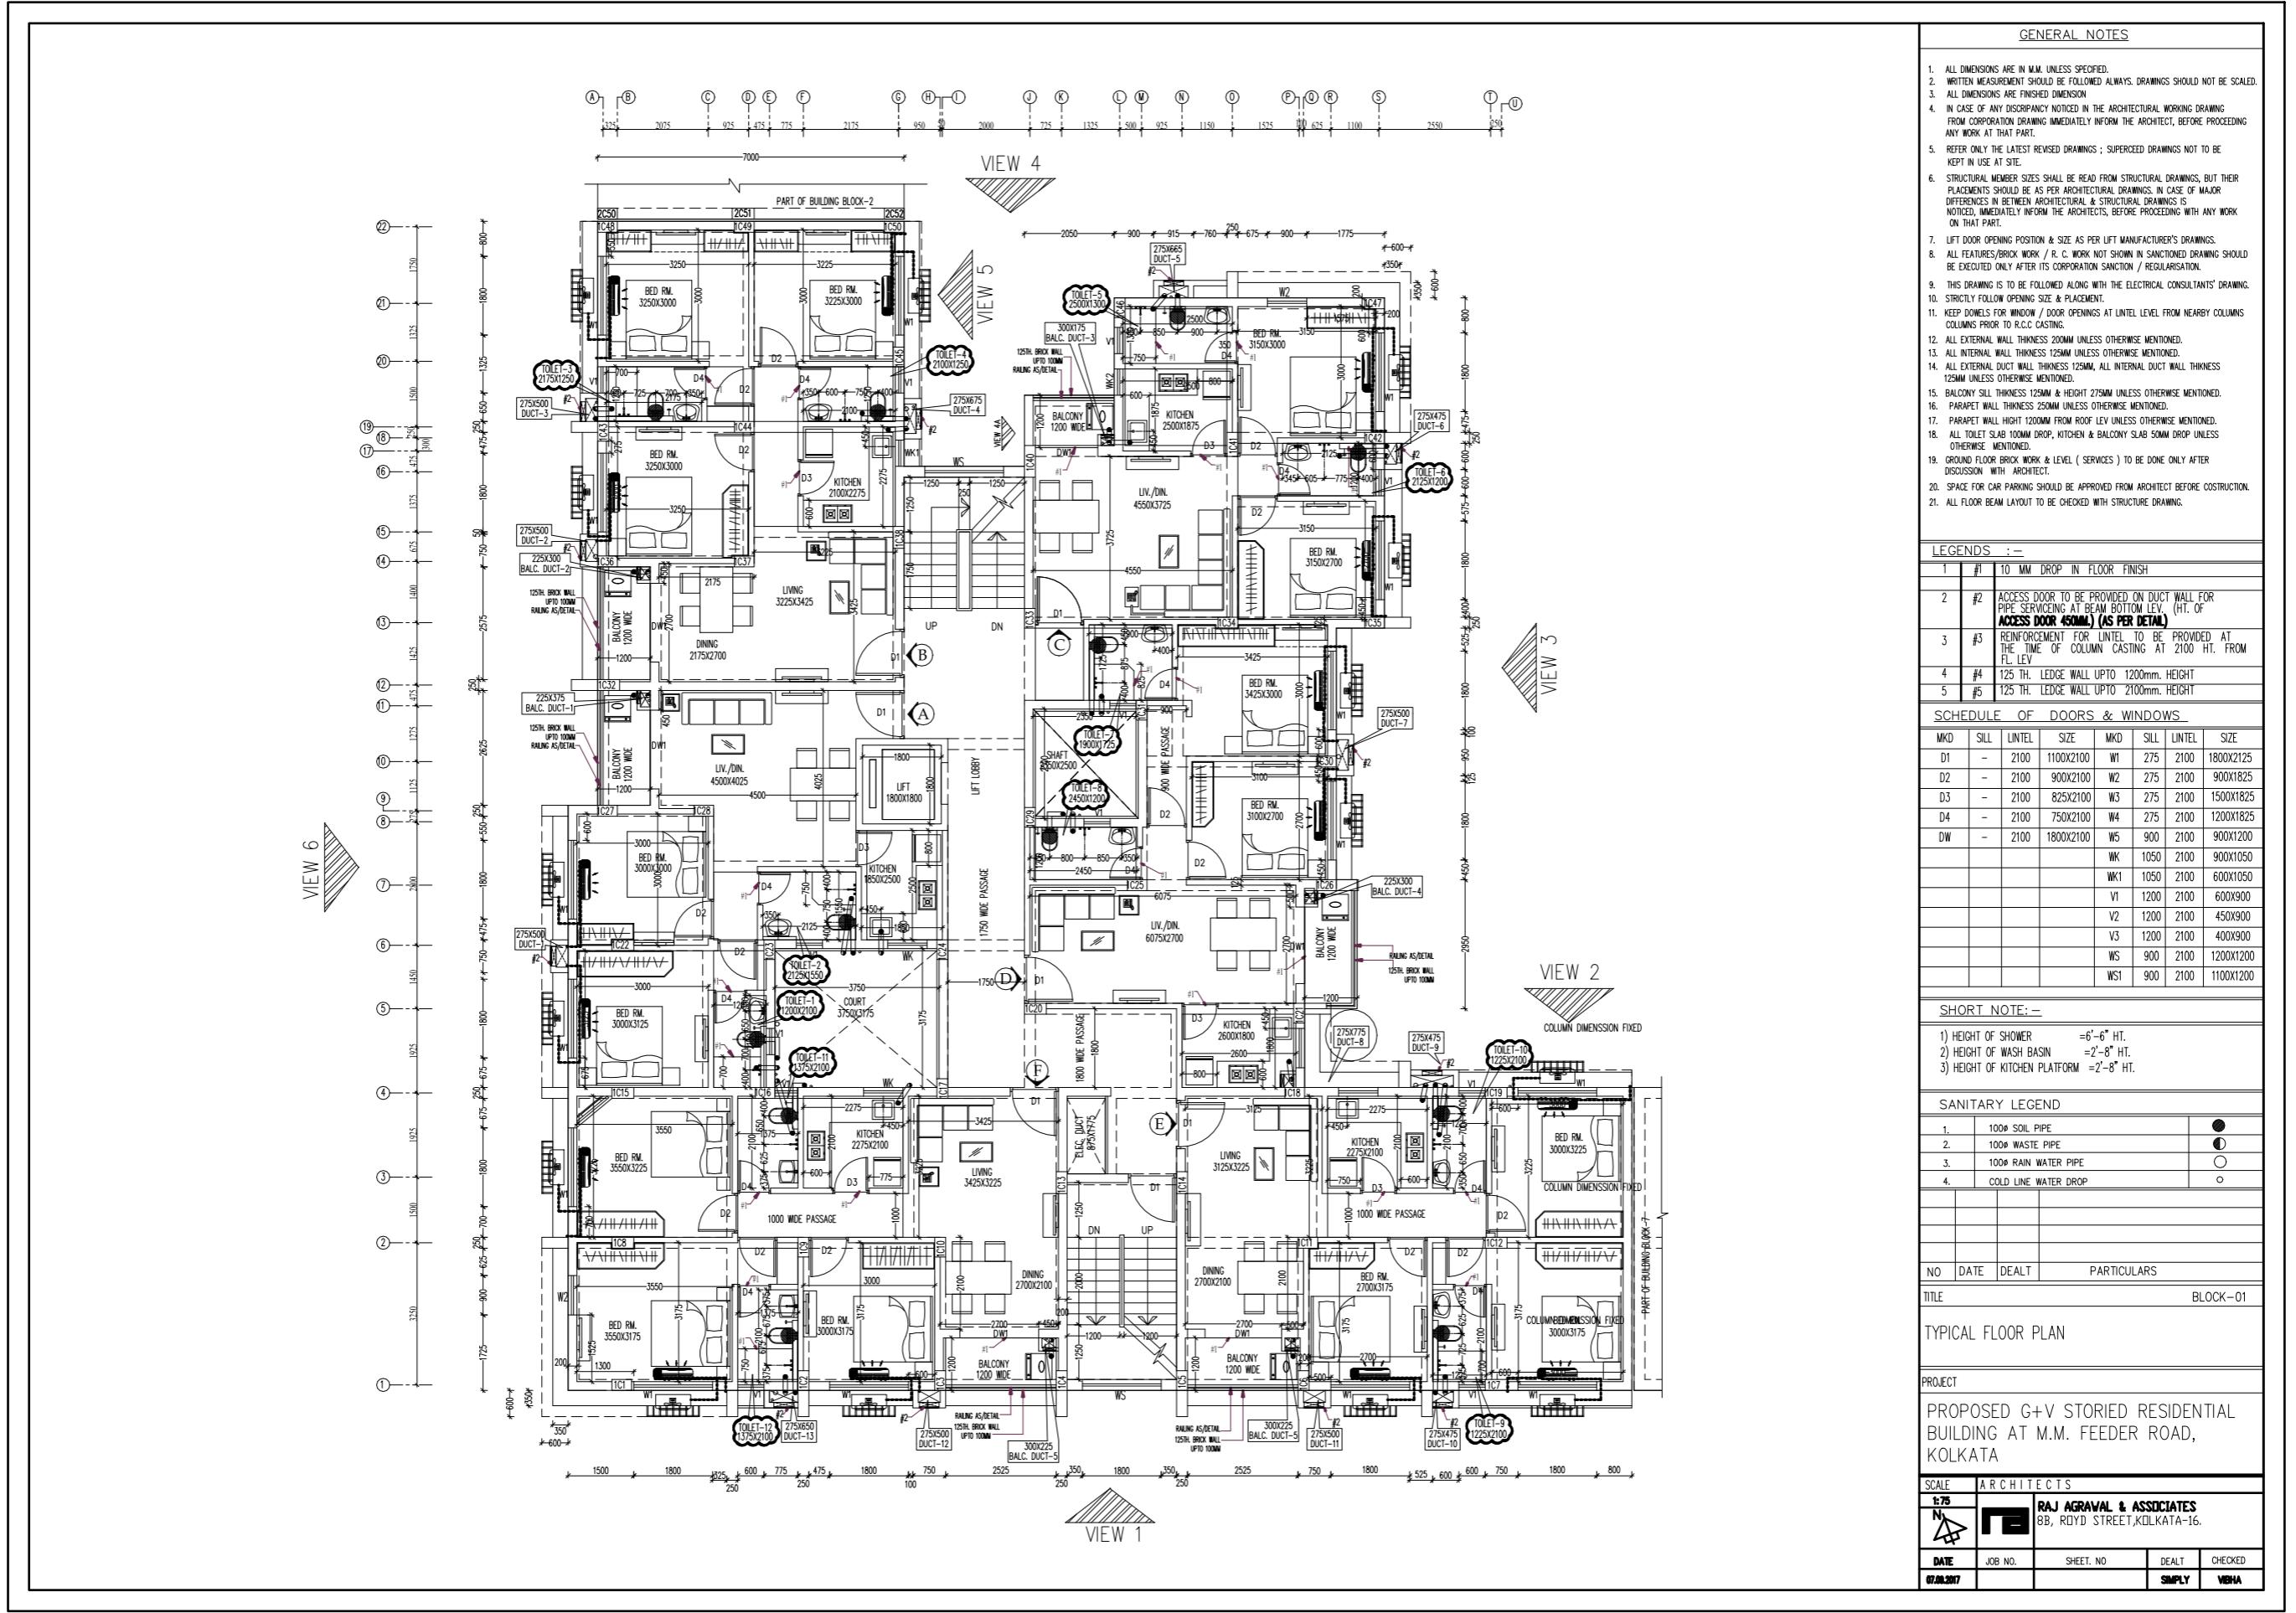

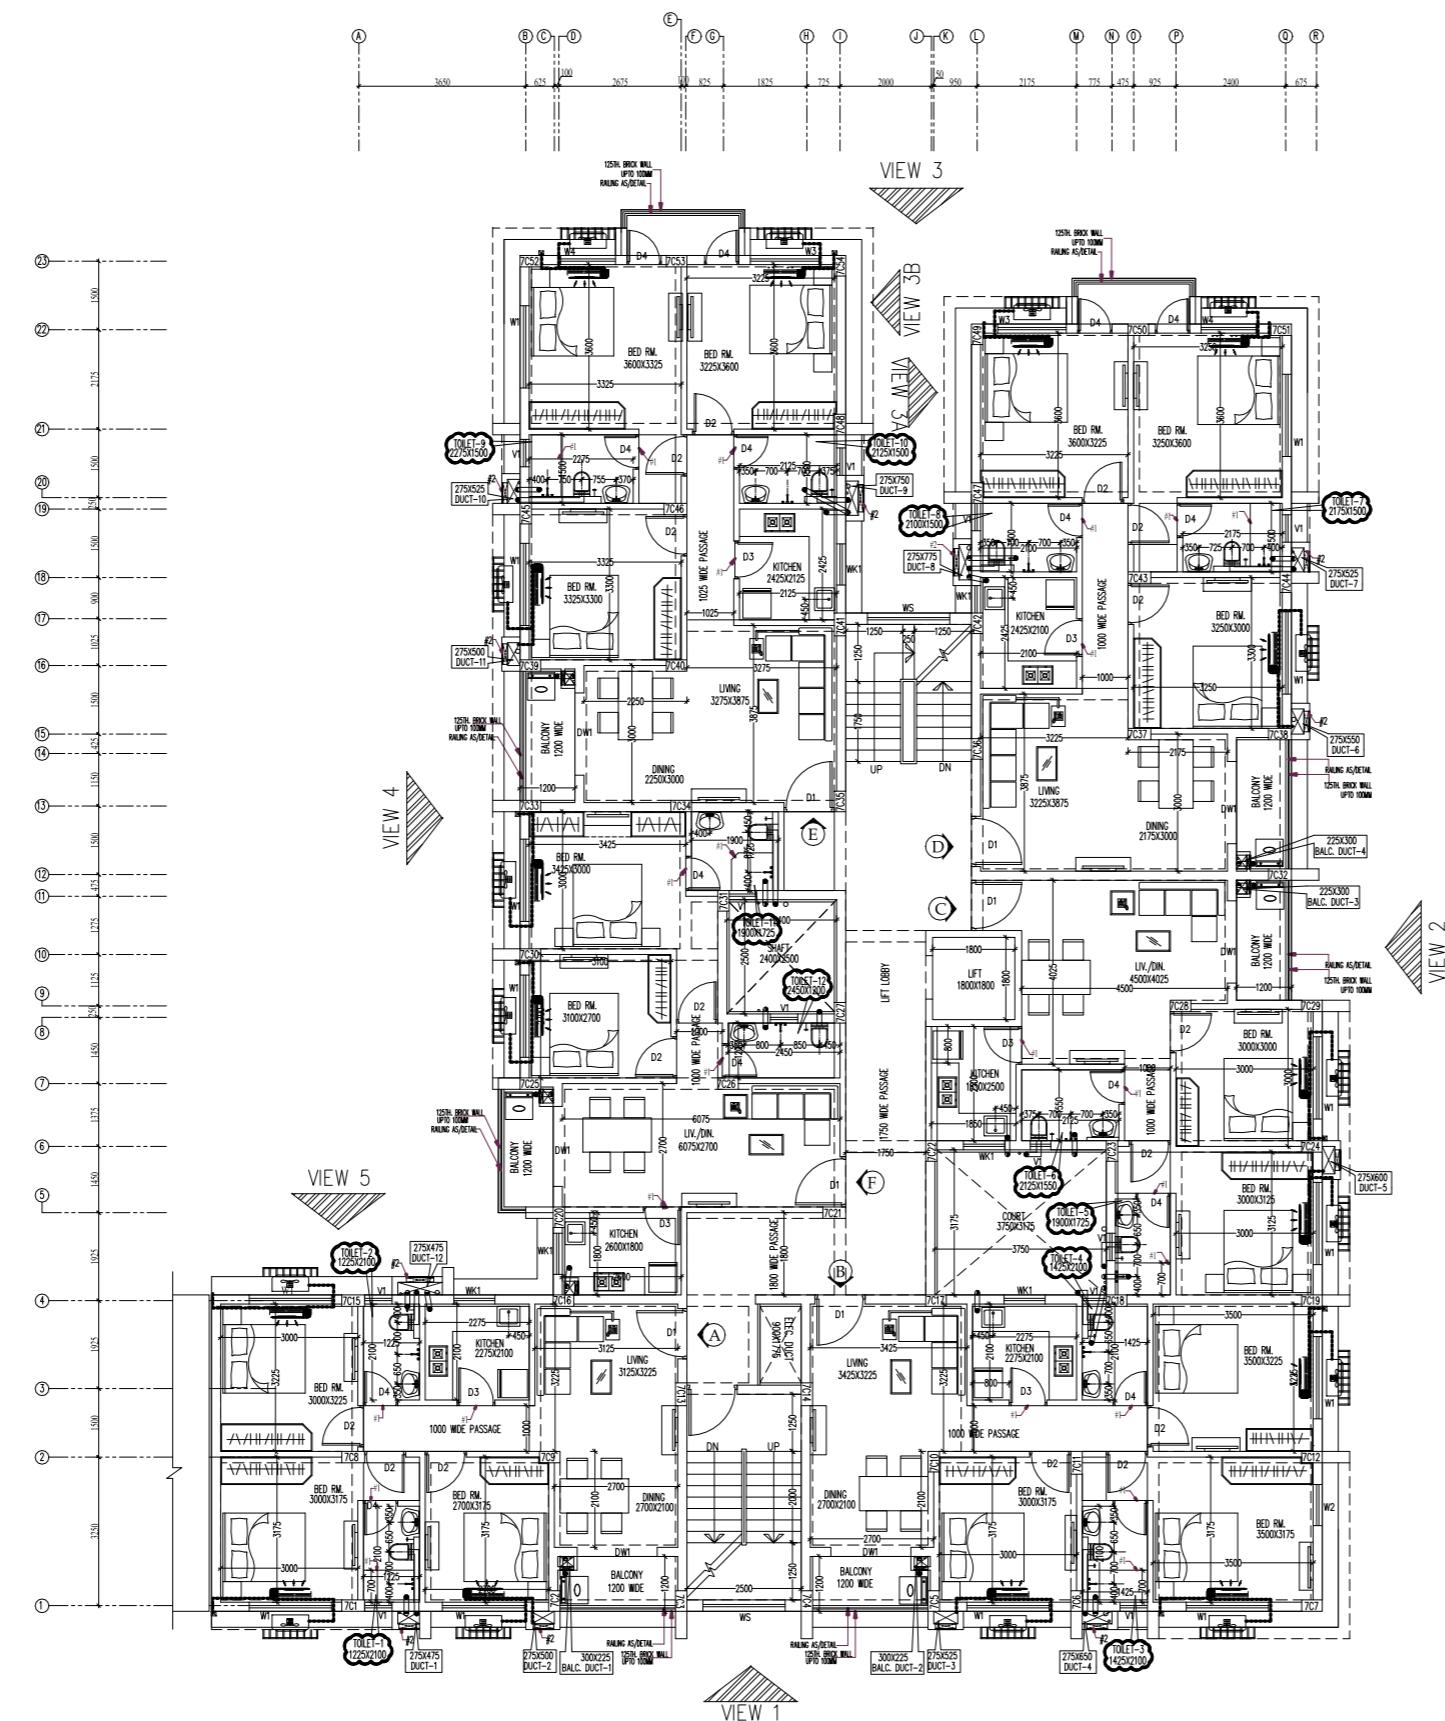

TYPICAL FLOOR PLAN

GENERAL NOTES

- ALL DIMENSIONS ARE IN MM. UNLESS SPECIFIED.
WRITTEN MEASUREMENT SHOULD BE FOLLOWED ALWAYS. DRAWINGS SHOULD NOT BE SCALED.
ALL DIMENSIONS ARE FINISHED DIMENSION
IN CASE OF ANY DISPUTE NOTICED IN THE ARCHITECTURAL WORKING DRAWING
FROM CORPORATION DRAWING IMMEDIATELY INFORM THE ARCHITECT, BEFORE PROCEEDING
ANY WORK AT THAT PART.
REFER ONLY TO THE LATEST REVISED DRAWINGS ; SUPERCEDED DRAWINGS NOT TO BE
KEPT IN USE AT SITE.
STRUCTURAL MEMBER SIZES SHALL BE READ FROM STRUCTURAL DRAWINGS, BUT THEIR
PLACEMENTS SHOULD AS PER ARCHITECTURAL DRAWINGS, IN CASE OF MAJOR
DIFFERENCES IN BETWEEN ARCHITECTURAL & STRUCTURAL DRAWINGS IS
NOTED, IMMEDIATELY INFORM THE ARCHITECTS, BEFORE PROCEEDING WITH ANY WORK
ON THAT PART.
LIFT DOOR OPENING POSITION & SIZE AS PER LIFT MANUFACTURER'S DRAWINGS.
ALL FEATURES/BRICK WORK / R. C. WORK NOT SHOWN IN SANCTIONED DRAWING SHOULD
BE EXECUTED ONLY AFTER ITS CORPORATION SANCTION / REGULARISATION.
THIS DRAWING IS TO BE FOLLOWED ALONG WITH THE ELECTRICAL CONSULTANTS' DRAWING.
STRICTLY FOLLOW OPENING SIZE & PLACEMENT.
KEEP DOWELS FOR WINDOW / DOOR OPENINGS AT UNTIL LEVEL FROM NEARBY COLUMNS
COLUMNS PRIOR TO R.C.C. CASTING.
ALL EXTERNAL WALL THICKNESS 200MM UNLESS OTHERWISE MENTIONED.
ALL INTERNAL WALL THICKNESS 125MM UNLESS OTHERWISE MENTIONED.
ALL EXTERNAL DUCT WALL THICKNESS 125MM, ALL INTERNAL DUCT WALL THICKNESS
125MM UNLESS OTHERWISE MENTIONED.
BALCONY SLAB THICKNESS 25MM & HEIGHT 275MM UNLESS OTHERWISE MENTIONED.
PARAPET WALL THICKNESS 250MM UNLESS OTHERWISE MENTIONED.
PARAPET WALL HEIGHT 1200MM FROM ROOF LEV UNLESS OTHERWISE MENTIONED.
ALL TOILET SLAB 100MM DROP, KITCHEN & BALCONY SLAB 50MM DROP UNLESS
OTHERWISE MENTIONED.
GROUND FLOOR BRICK WORK & LEVEL (SERVICES) TO BE DONE ONLY AFTER
DISCUSSION WITH ARCHITECT.
SPACE FOR CAR PARKING SHOULD BE APPROVED FROM ARCHITECT BEFORE CONSTRUCTION.
ALL FLOOR BLEM LAYOUT TO BE CHECKED WITH STRUCTURE DRAWING.

LEGENDS :-

1	#1	10 MM DROP IN FLOOR FINISH
2	#2	ACCESS DOOR TO BE PROVIDED ON DUCT WALL FOR PIPE SERVICING AT BEAM BOTTOM LEV. (HT. OF ACCESS DOOR 450MM.) (AS PER DETAIL)
3	#3	REINFORCEMENT FOR LINTEL TO BE PROVIDED AT THE TIME OF COLUMN CASTING AT 2100 HT. FROM FL. LEV.
4	#4	125 TH. LEDGE WALL UPTO 1200mm. HEIGHT
5	#5	125 TH. LEDGE WALL UPTO 2100mm. HEIGHT

SCHEDULE OF DOORS & WINDOWS

MKD	SILL	LINTEL	SIZE	MKD	SILL	LINTEL	SIZE
D1	-	2100	1100X2100	W1	275	2100	1800X2125
D2	-	2100	900X2100	W2	275	2100	900X1825
D3	-	2100	825X2100	W3	275	2100	1500X1825
D4	-	2100	750X2100	W4	275	2100	1200X1825
DW	-	2100	1800X2100	W5	900	2100	900X1200
				W6	1050	2100	900X1050
				W61	1050	2100	600X1050
				V1	1200	2100	600X900
				V2	1200	2100	450X900
				V3	1200	2100	400X900
				WS	900	2100	1200X1200
				WS1	900	2100	1100X1200

SHORT NOTE:-

- 1) HEIGHT OF SHOWER = 6'-6" HT.
 2) HEIGHT OF WASH BASIN = 2'-8" HT.
 3) HEIGHT OF KITCHEN PLATFORM = 2'-8" HT.

SANITARY LEGEND

SANITARY LEGEND	
1.	100Ø SOIL PIPE
2.	100Ø WASTE PIPE
3.	100Ø RAIN WATER PIPE

	DATE	DEALT	PARTICULARS
--	------	-------	-------------

) DATE DEALT PARTICULARS

SYNTHETIC FLOOD PLAN

PICAL FLOOR PLAN

JECT


**ROPOSED G+V STORIED RESIDENTIAL
UILDING AT M.M. FEEDER ROAD,
OKATA**

ONE ARCHITECTS

RAJ AGRAWAL & ASSOCIATES
8B, BLDG STREET, KOLKATA-16.

Digitized by srujanika@gmail.com

DATE	JOB NO.	SHEET. NO	DEALT	CHECKED
09.2017			SIMPLY	VIBHA

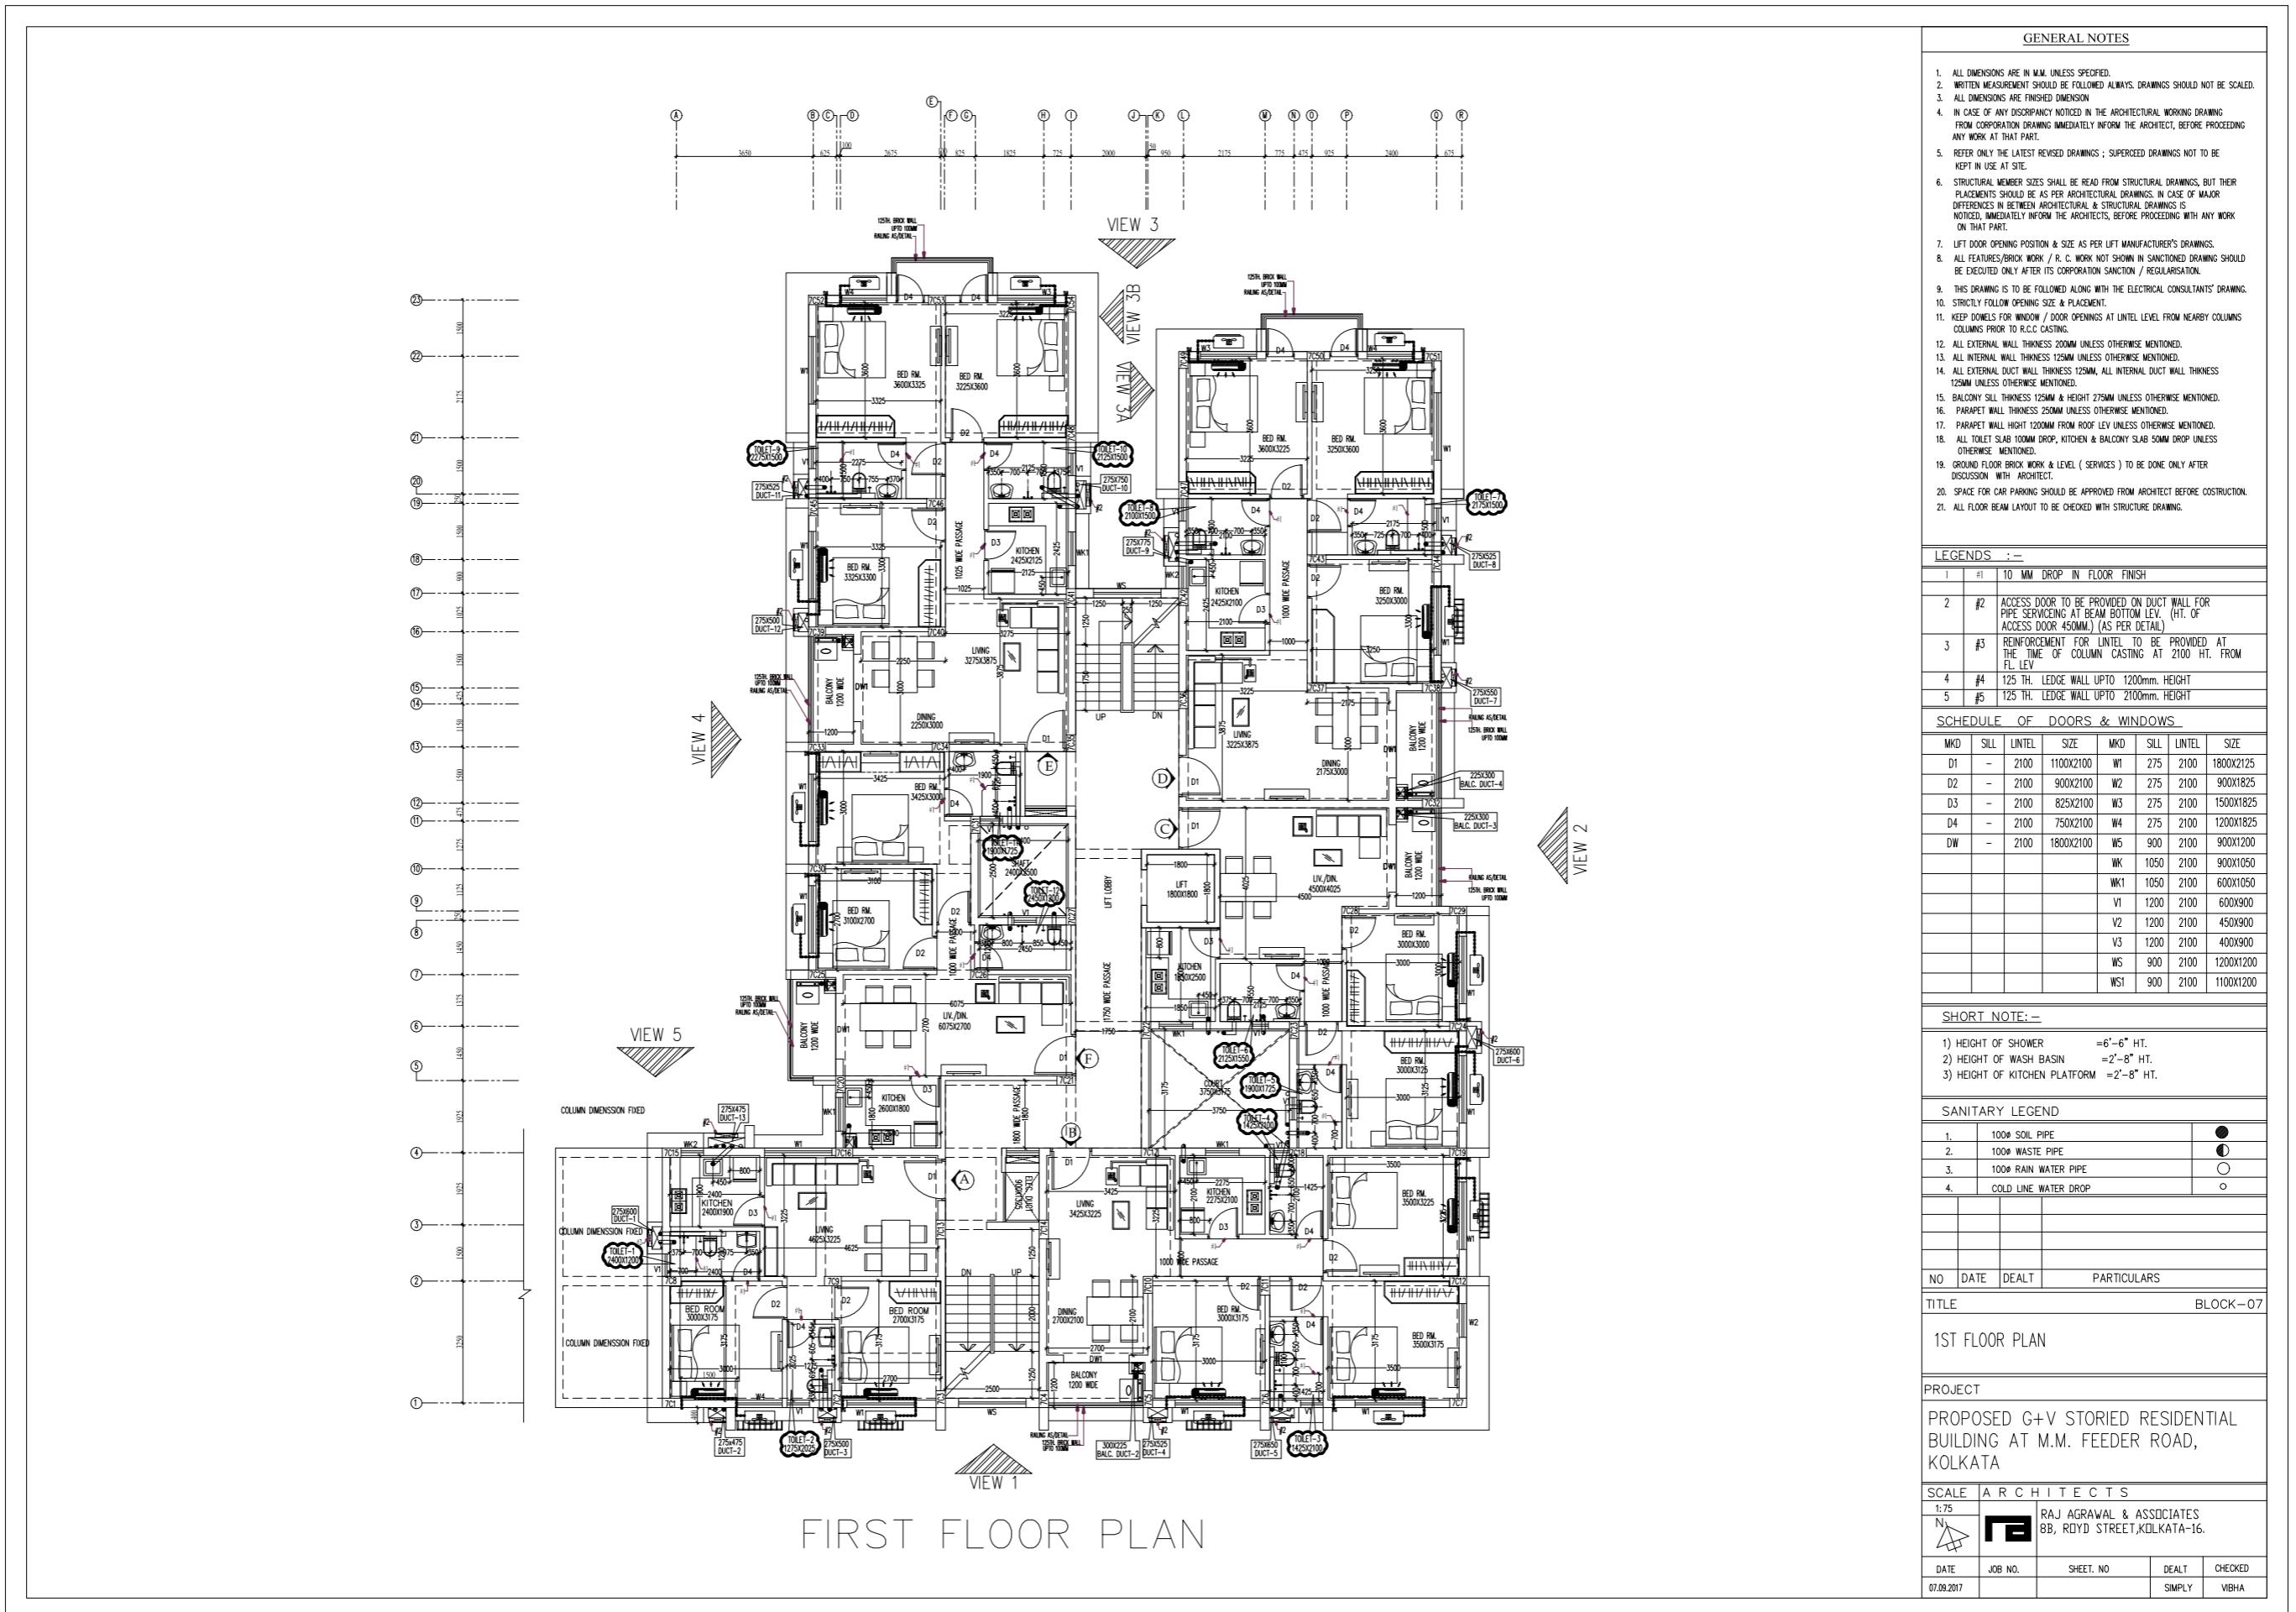

GENERAL NOTES

- ALL DIMENSIONS ARE IN MM. UNLESS SPECIFIED.
- WRITTEN MEASUREMENT SHOULD BE FOLLOWED ALWAYS. DRAWINGS SHOULD NOT BE SCALED.
- ALL DIMENSIONS ARE FINISHED DIMENSION.
- IN CASE OF ANY DISCREPANCY NOTED IN THE ARCHITECTURAL WORKING DRAWING FROM CORPORATION DRAWING IMMEDIATELY INFORM THE ARCHITECT, BEFORE PROCEEDING ANY WORK AT THAT PART.
- REFER ONLY THE LATEST REVISED DRAWINGS ; SUPERSEDED DRAWINGS NOT TO BE KEPT IN USE AT SITE.
- STRUCTURAL MEMBER SIZES SHALL BE READ FROM STRUCTURAL DRAWINGS, BUT THEIR PLACEMENTS SHOULD BE AS PER MODERN EDITION DRAWINGS. IN CASE OF MAJOR DIFFERENCES IN BETWEEN ARCHITECTURAL & STRUCTURAL DRAWINGS IS NOTICED, IMMEDIATELY INFORM THE ARCHITECTS, BEFORE PROCEEDING WITH ANY WORK ON THAT PART.
- LIFT DOOR OPENING POSITION & SIZE AS PER LIFT MANUFACTURER'S DRAWINGS.
- ALL FEATURES/BROCK WORK / R. C. WORK NOT SHOWN IN SANCTIONED DRAWING SHOULD BE EXECUTED ONLY AFTER ITS CORPORATION SANCTION / REGULARISATION.
- THE DRAWING IS TO BE FOLLOWED ALONG WITH THE ELECTRICAL CONSULTANTS' DRAWING.
- STRICTLY FOLLOW OPENING SIZE & PLACEMENT.
- KEEP DOWELS FOR WINDOW / DOOR OPENINGS AT LINTEL LEVEL FROM NEARBY COLUMNS
- ALL EXTERNAL WALL THICKNESS 200MM UNLESS OTHERWISE MENTIONED.
- ALL INTERNAL WALL THICKNESS 125MM UNLESS OTHERWISE MENTIONED.
- ALL EXTERNAL PLATE WALL THICKNESS 125MM, ALL INTERNAL DUCT WALL THICKNESS 125MM UNLESS OTHERWISE MENTIONED.
- BALCONY SILL THICKNESS 125MM & HEIGHT 275MM UNLESS OTHERWISE MENTIONED.
- PARAPET WALL THICKNESS 250MM UNLESS OTHERWISE MENTIONED.
- PARAPET WALL HEIGHT 1200MM FROM ROOF LEV UNLESS OTHERWISE MENTIONED.
- ALL TOILET SLAB 100MM DROP, KITCHEN & BALCONY SLAB 50MM DROP UNLESS OTHERWISE MENTIONED.
- GROUND FLOOR BRICK WORK & LEVEL (SERVICES) TO BE DONE ONLY AFTER DISCUSSION WITH ARCHITECT.
- SPACE FOR CAR PARKING SHOULD BE APPROVED FROM ARCHITECT BEFORE CONSTRUCTION.
- ALL FLOOR BEAM LAYOUT TO BE CHECKED WITH STRUCTURE DRAWING.

LEGENDS :-

1	#1	10 MM. DROP IN FLOOR FINISH
2	#2	ACCESS DOOR TO BE PROVIDED ON DUCT WALL FOR PIPE SERVICING AT BEAM BOTTOM LEV. (HT. OF ACCESS DOOR 450MM) (AS PER DETAIL)
3	#3	REINFORCEMENT FOR LINTEL TO BE PROVIDED AT THE TIME OF COLUMN CASTING AT 2100 HT. FROM FL. LEV
4	#4	125 TH. LEDGE WALL UPTO 1200mm. HEIGHT
5	#5	125 TH. LEDGE WALL UPTO 2100mm. HEIGHT

SCHEDULE OF DOORS & WINDOWS

MKD	SILL	LINTEL	SIZE	MKD	SILL	LINTEL	SIZE
D1	-	2100	1100X2100	W1	275	2100	1800X2125
D2	-	2100	900X2100	W2	275	2100	900X1825
D3	-	2100	825X2100	W3	275	2100	1500X1825
D4	-	2100	750X2100	W4	275	2100	1200X1825
DW	-	2100	1800X2100	W5	900	2100	900X1200
				WK	1050	2100	900X1050
				WK1	1050	2100	600X1050
				V1	1200	2100	600X900
				V2	1200	2100	450X900
				V3	1200	2100	400X900
				WS	900	2100	1200X1200
				WS1	900	2100	1100X1200

SHORT NOTE:-

- HEIGHT OF SHOWER = 6'-6" HT.
- HEIGHT OF WASH BASIN = 2'-8" HT.
- HEIGHT OF KITCHEN PLATFORM = 2'-8" HT.

SANITARY LEGEND

1.	100# SOIL PIPE	●
2.	100# WASTE PIPE	●
3.	100# RAIN WATER PIPE	○
4.	COLD LINE WATER DROP	○

NO DATE DEALT PARTICULARS

TITLE BLOCK-07

1ST FLOOR PLAN


PROJECT


PROPOSED G+V STORIED RESIDENTIAL
BUILDING AT M.M. FEEDER ROAD,
KOLKATA

SCALE ARCHITECTS

1:75
N RAJ AGRAWAL & ASSOCIATES
BB, ROYD STREET,KOLKATA-16.

DATE JOB NO. SHEET. NO. DEALT CHECKED
07.09.2017 SIMPLY VBHA

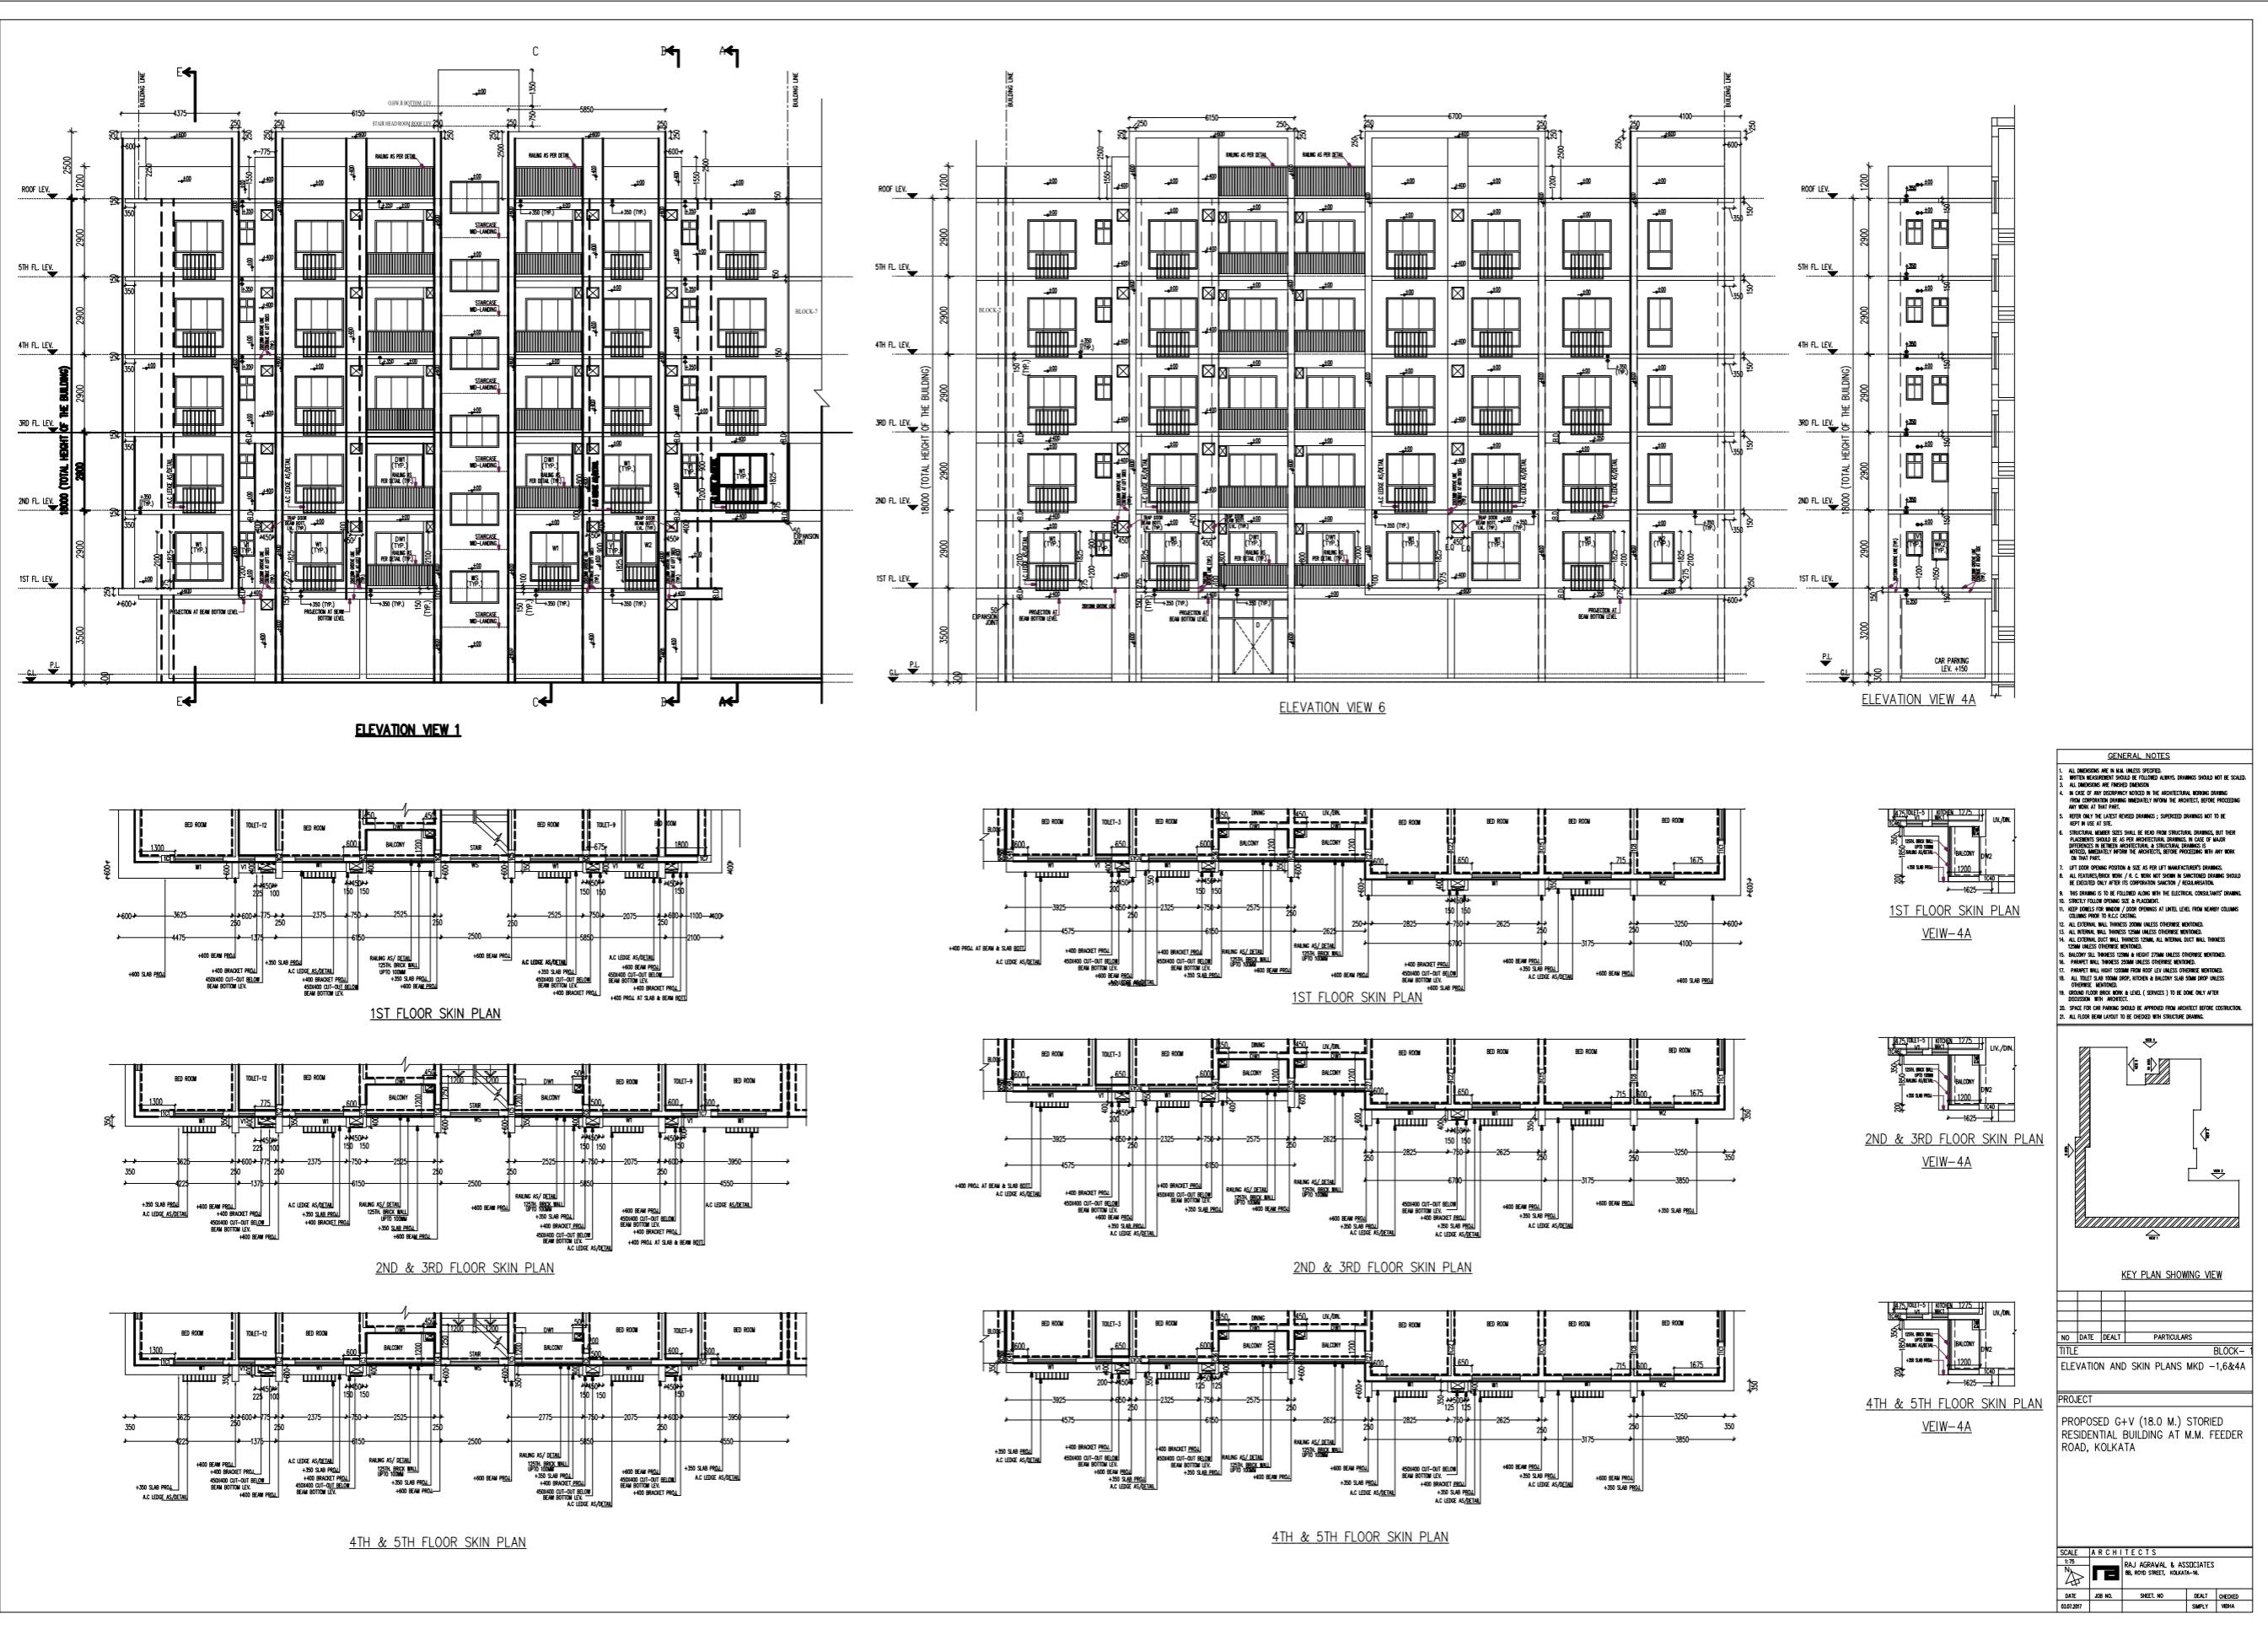


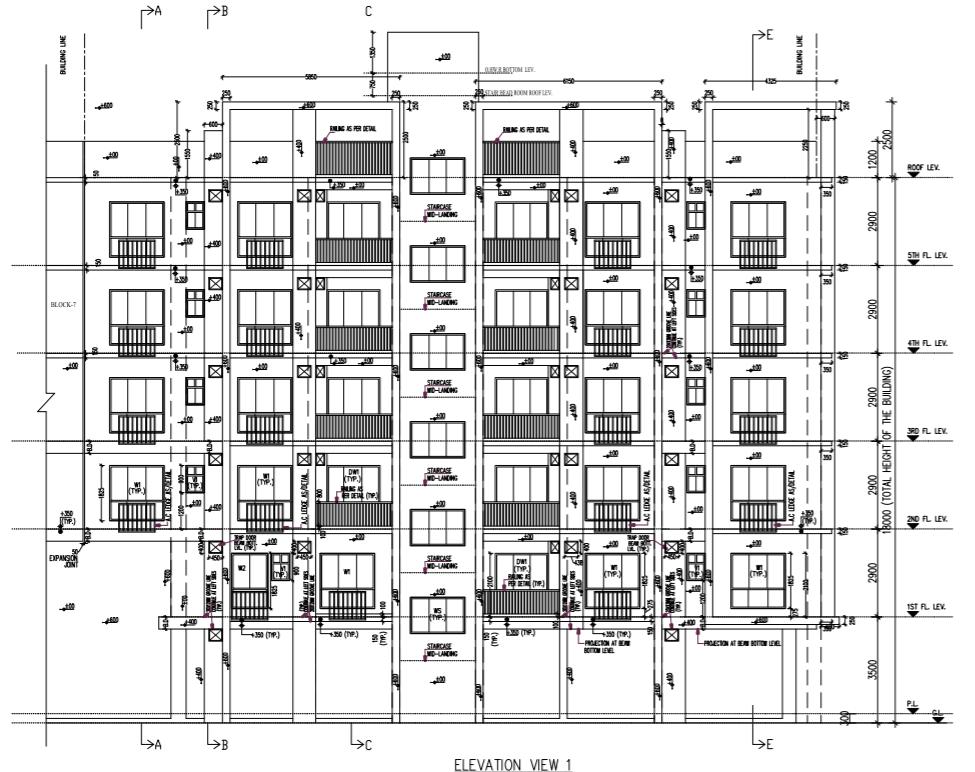


ELEVATION VIEW 1




ELEVATION VIEW 2

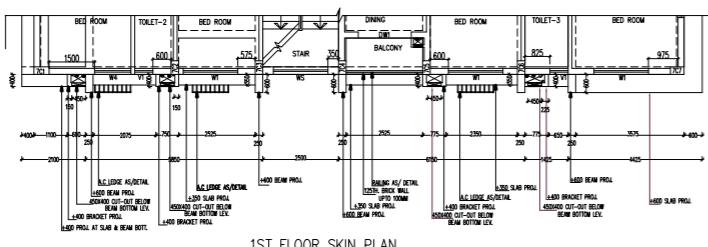


1ST FLOOR SKIN PLAN

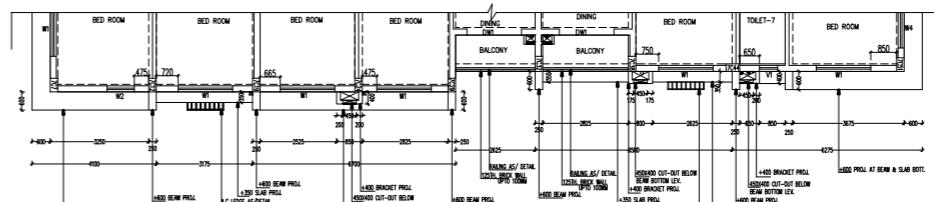


1ST FLOOR SKIN PLAN

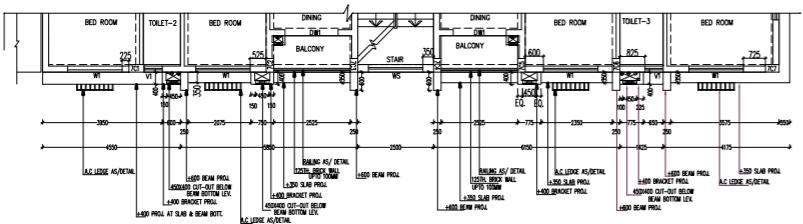


2ND & 3RD FLOOR SKIN PLAN

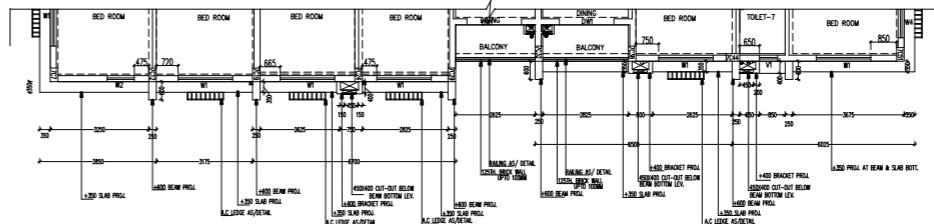

2ND & 3RD FLOOR SKIN PLAN

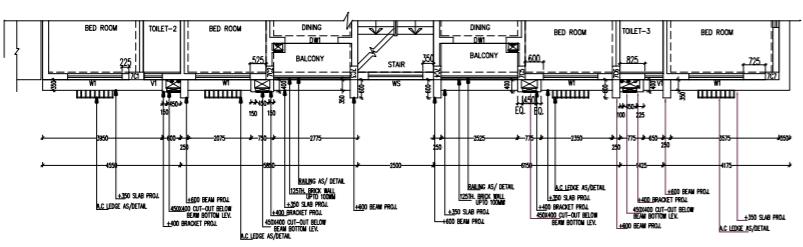


4TH & 5TH FLOOR SKIN PLAN

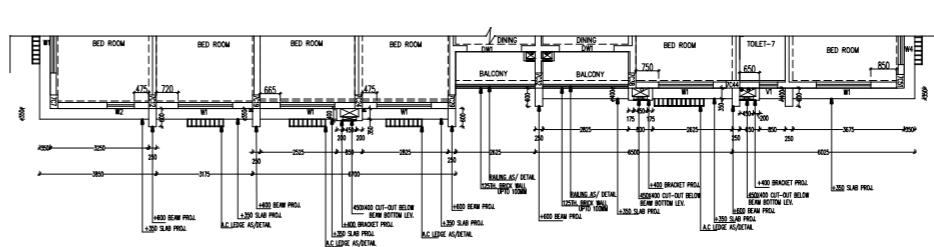

4TH & 5TH FLOOR SKIN PLAN

GENERAL NOTES

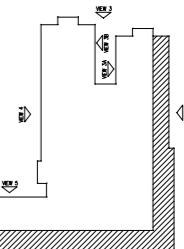

KEY PLAN SHOWING VIEW

		PARTICULARS
E	DEALT	BLOCK- 7


ANSWER


**SED G+V (18.0 M.) STORED
INTIAL BUILDING AT M.M. FEEDER
KOLKATA**


10.000-15.000 €


Page 1


RAJ AGRAWAL & ASSOCIATES
88, ROYD STREET, KOLKATA-16.

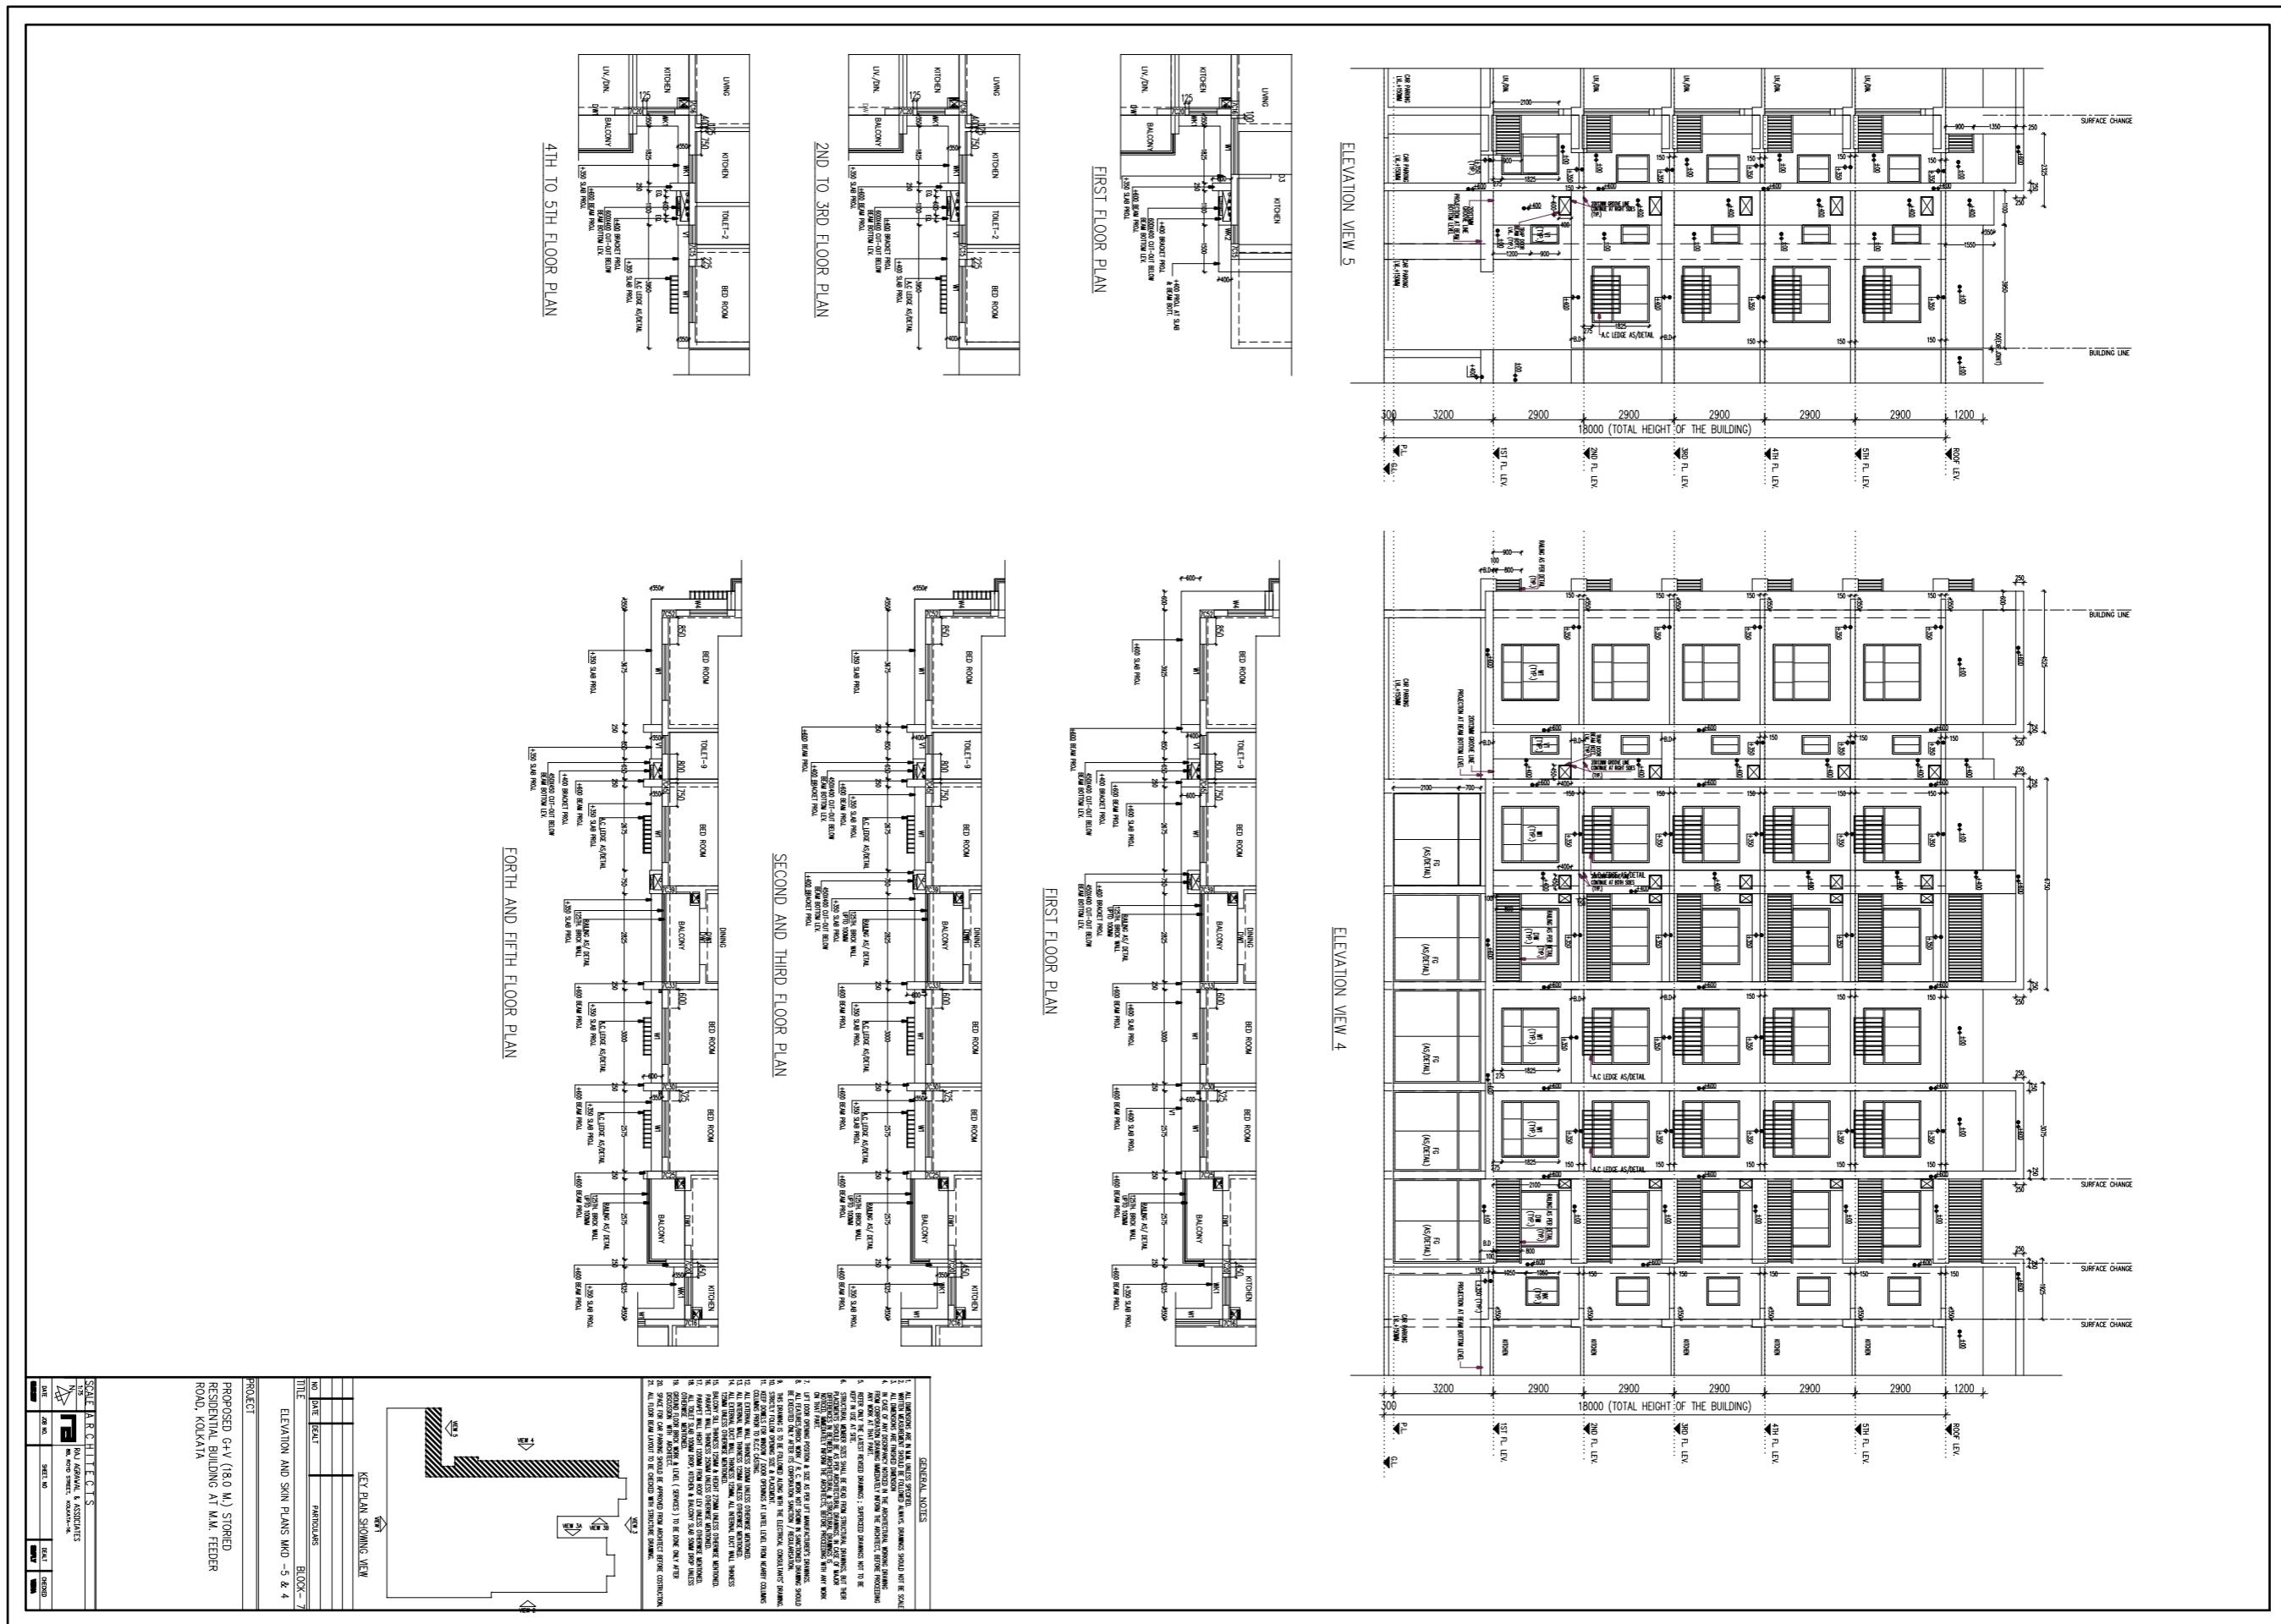


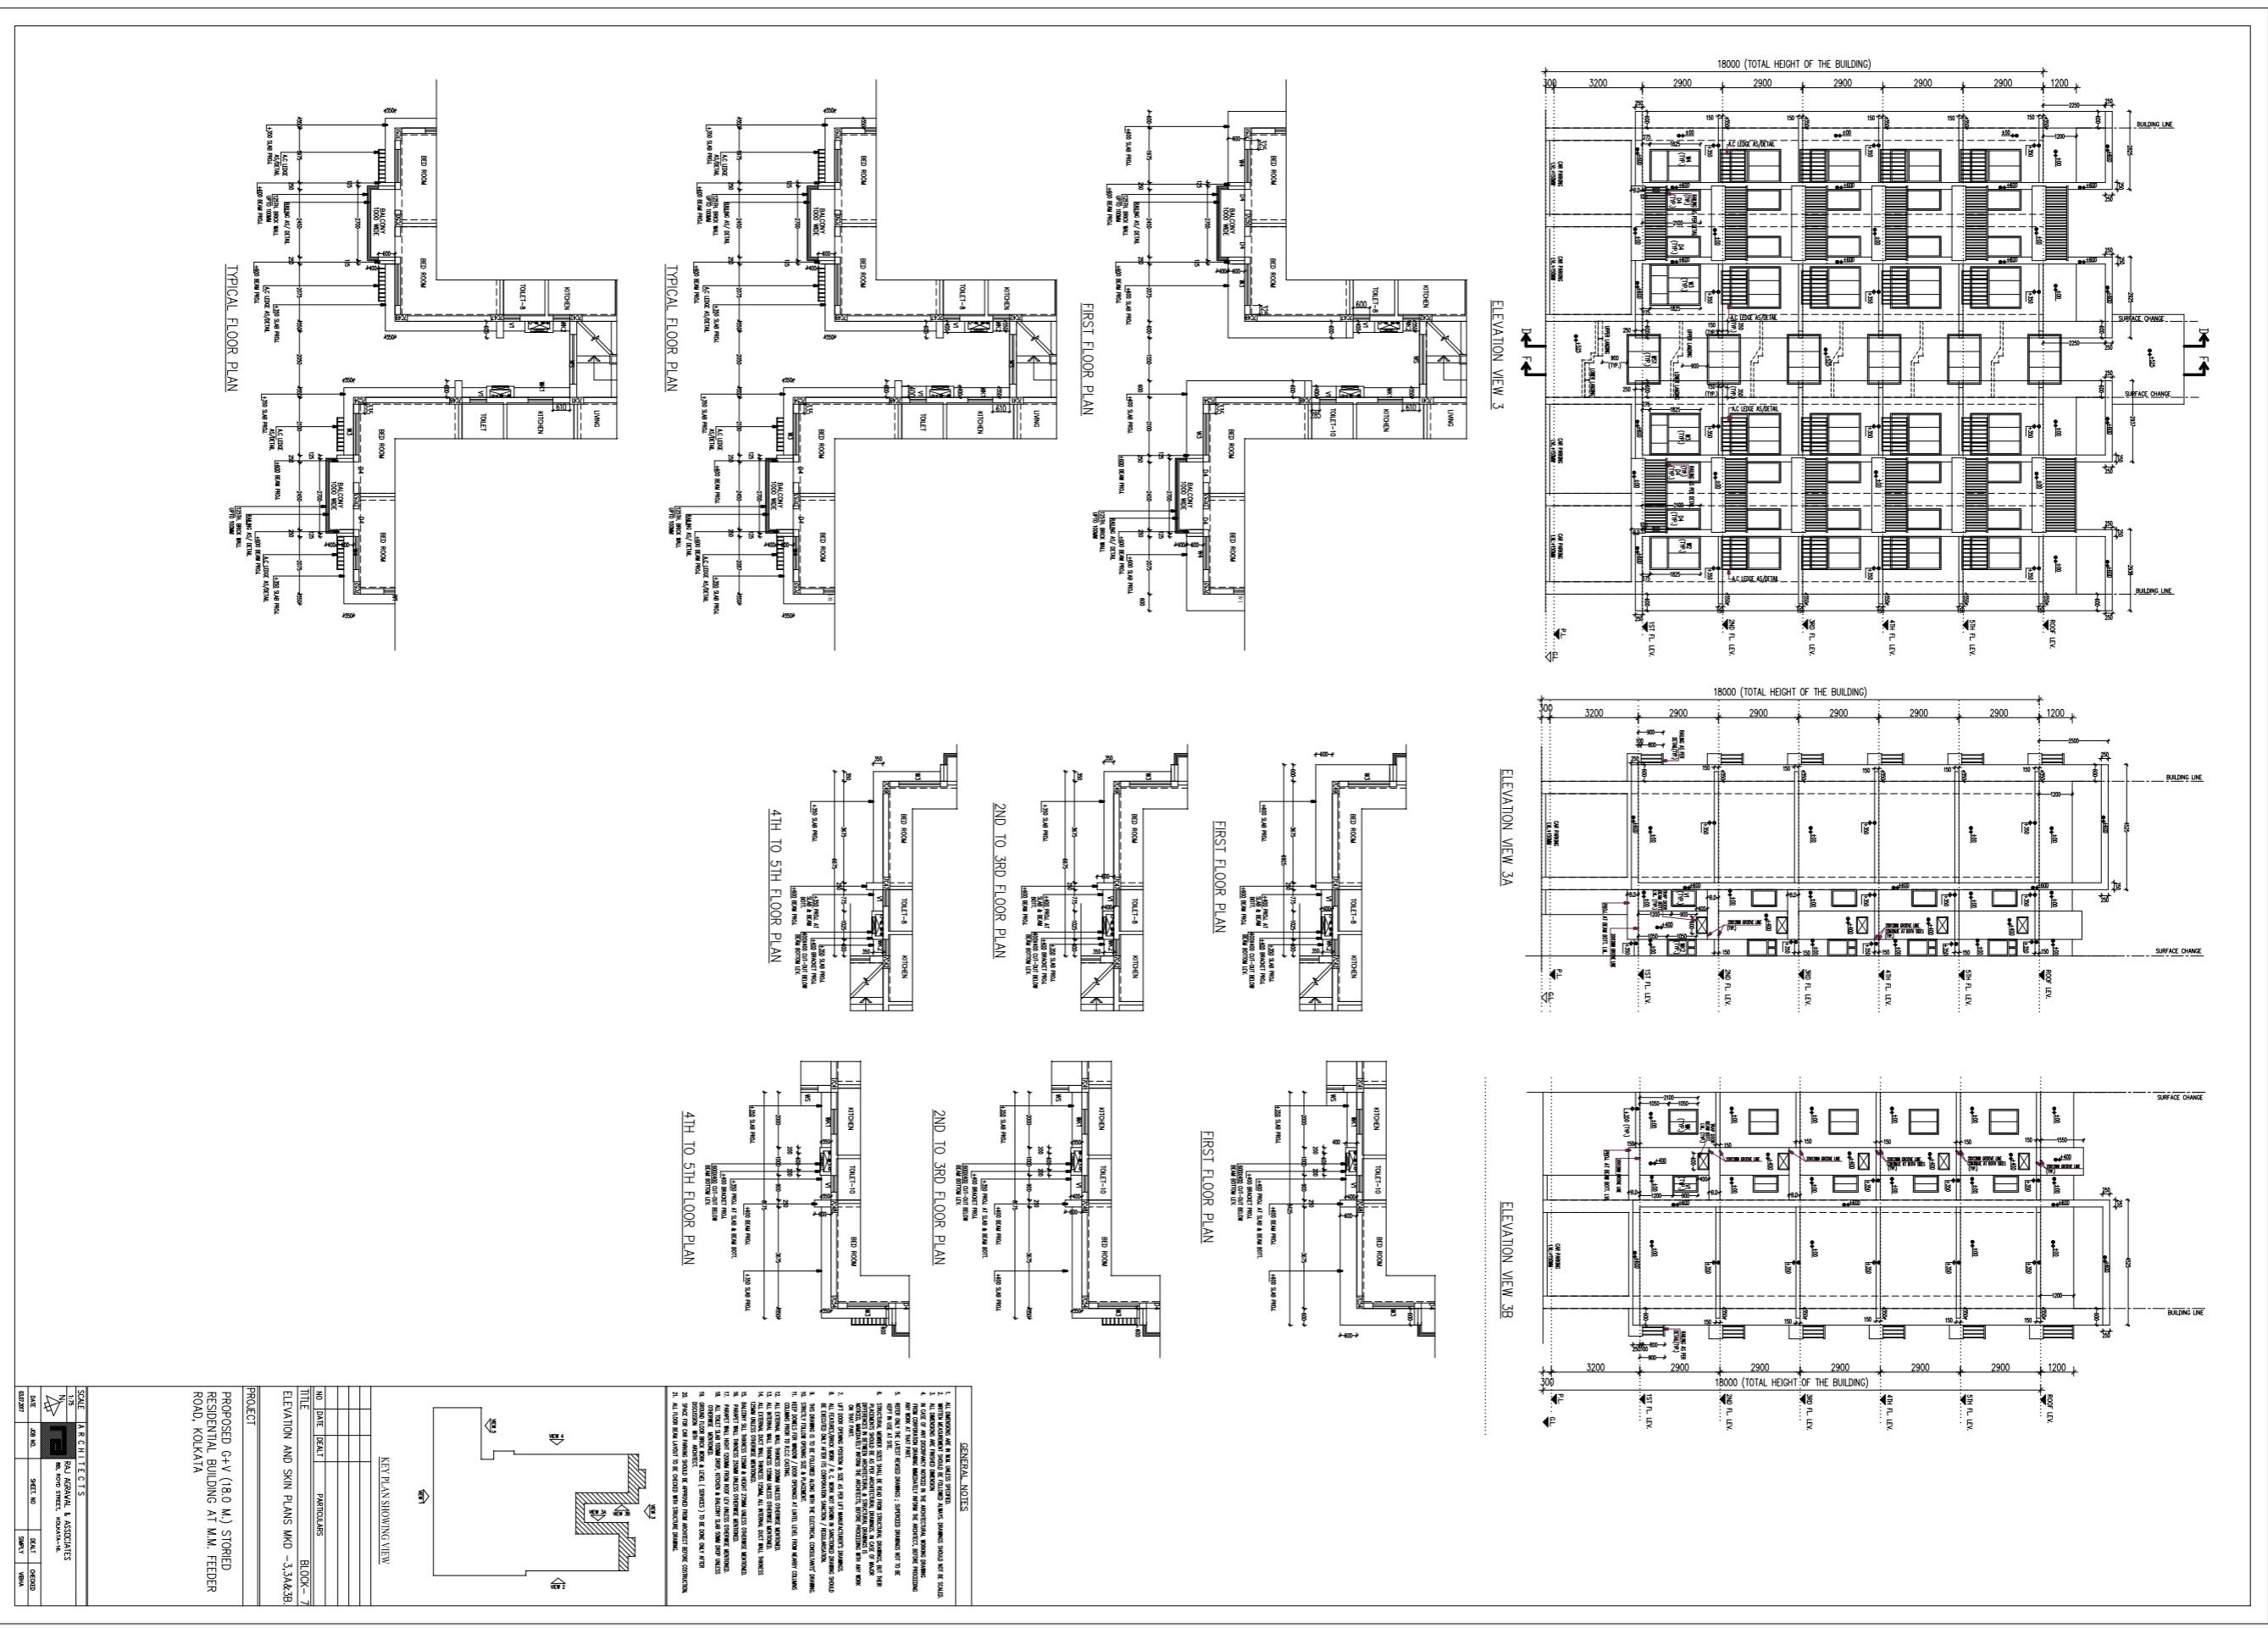


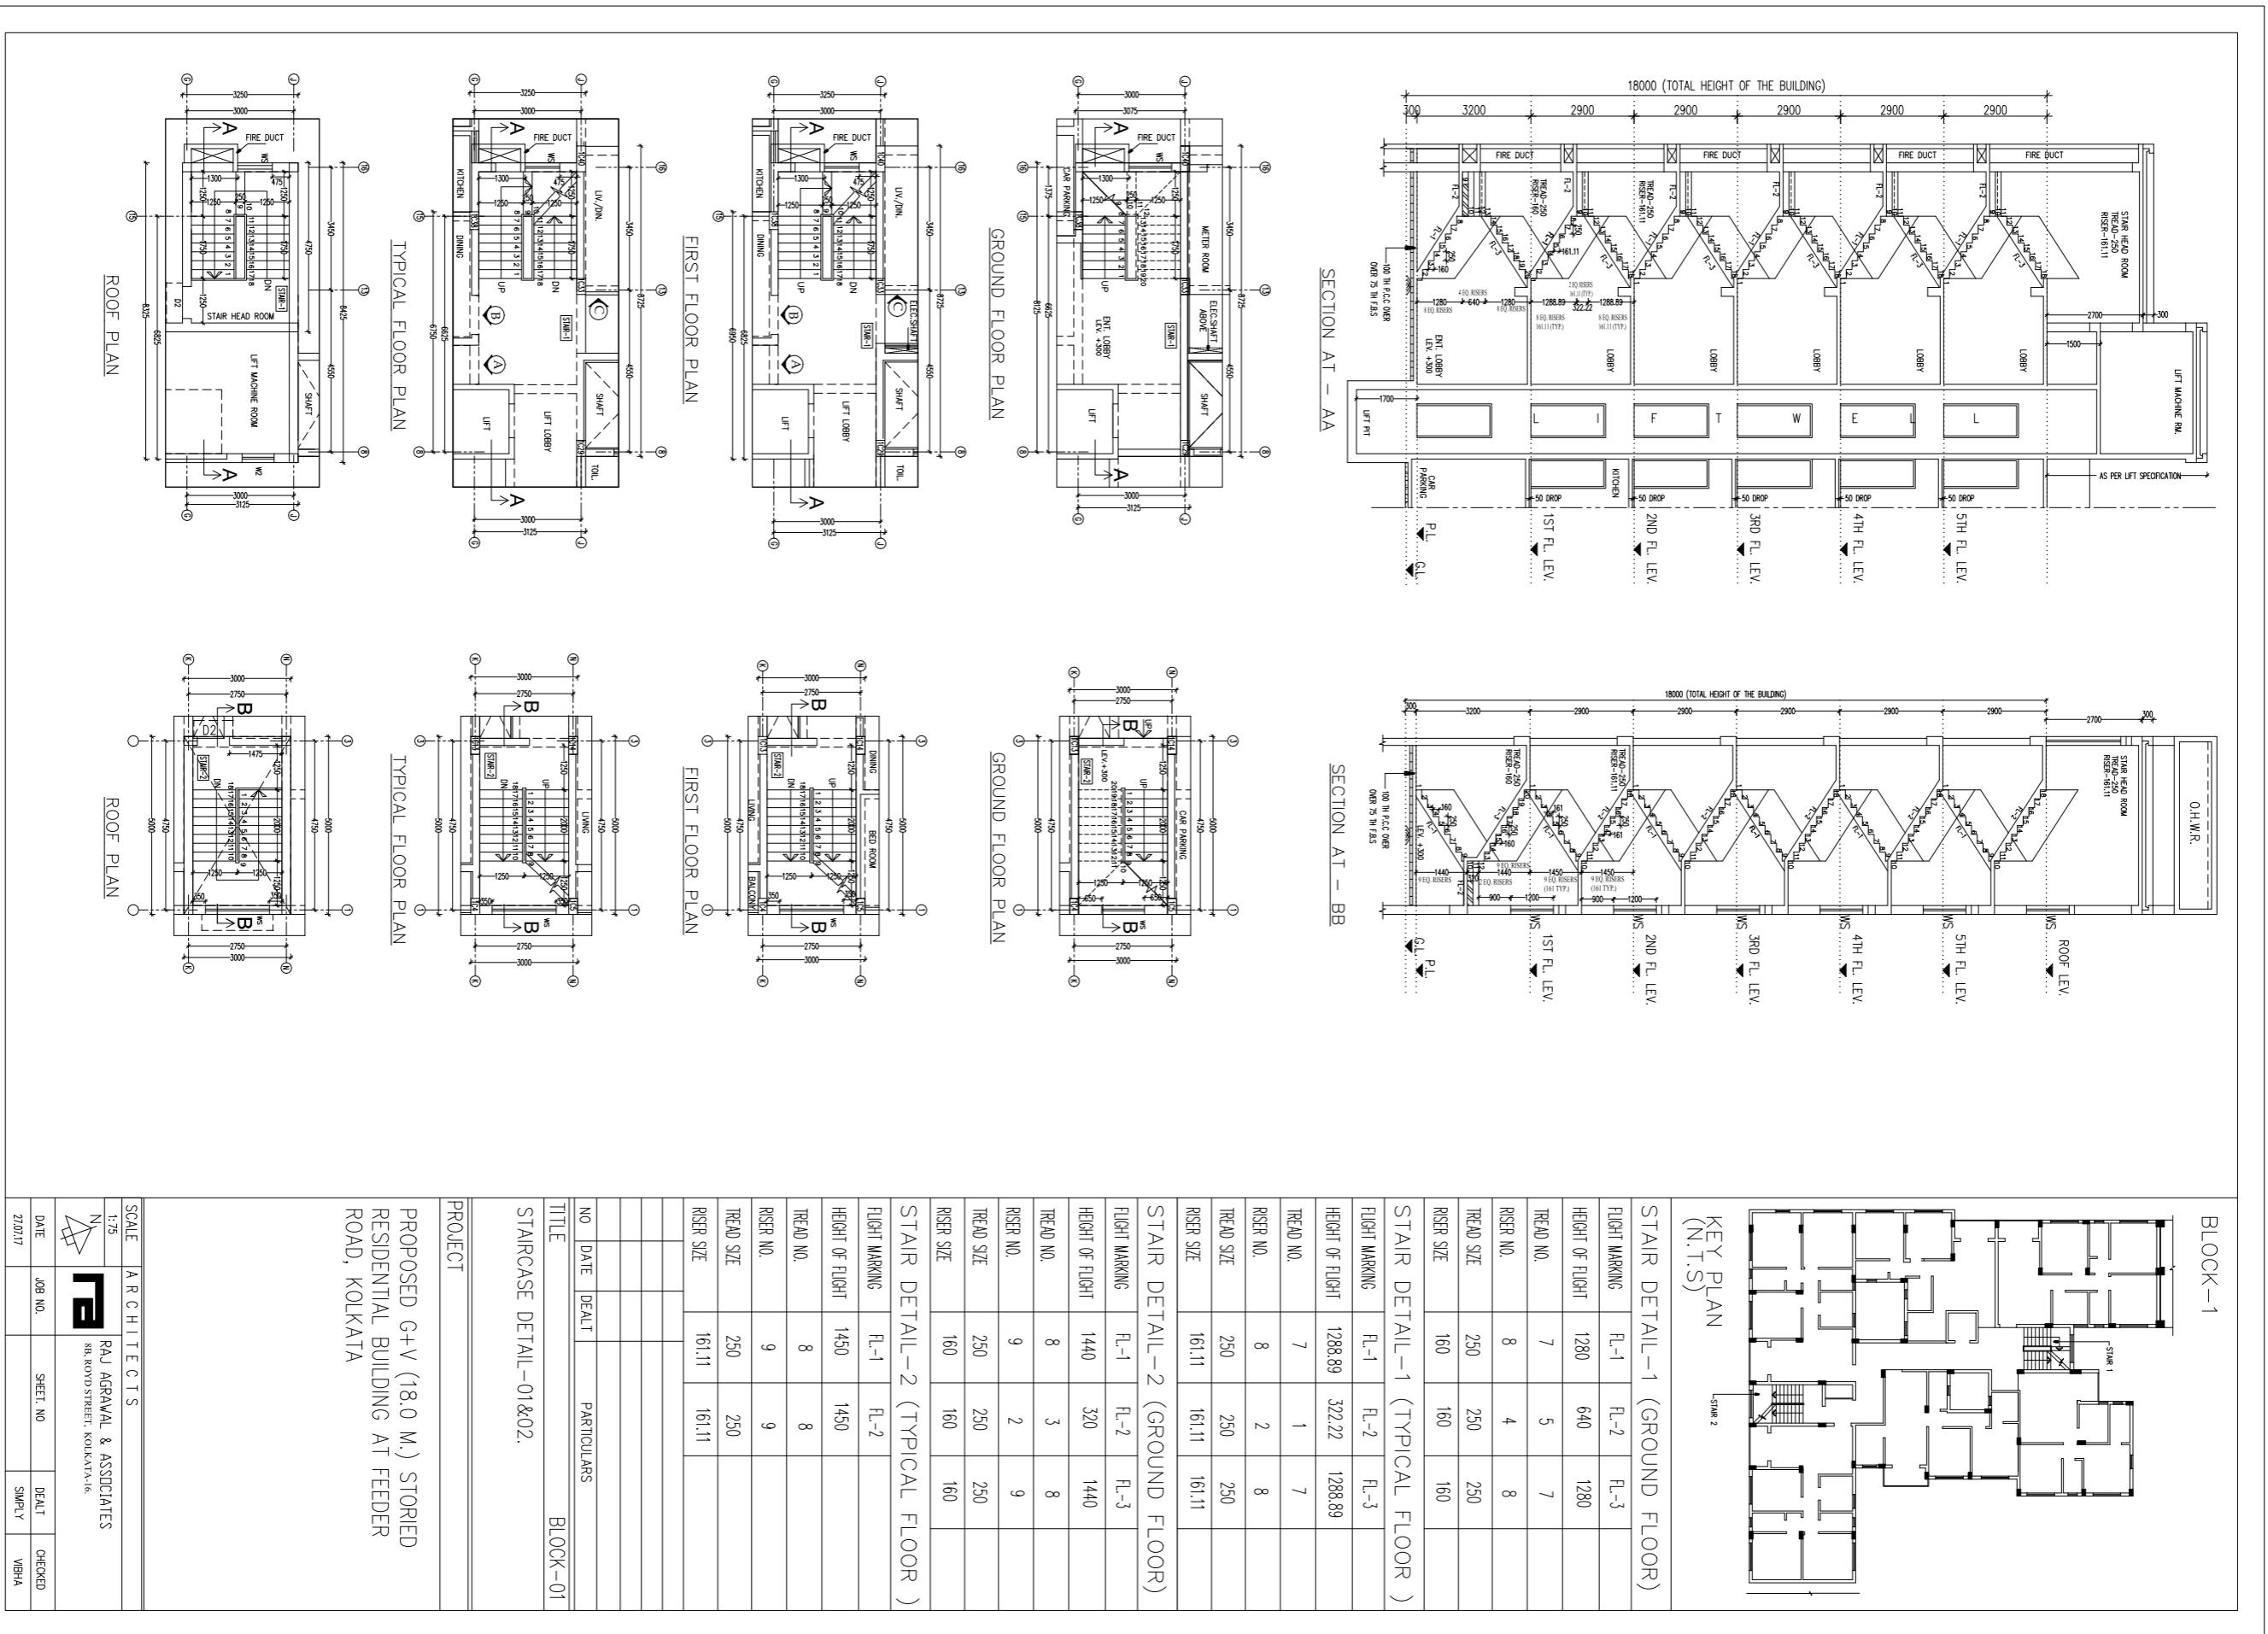


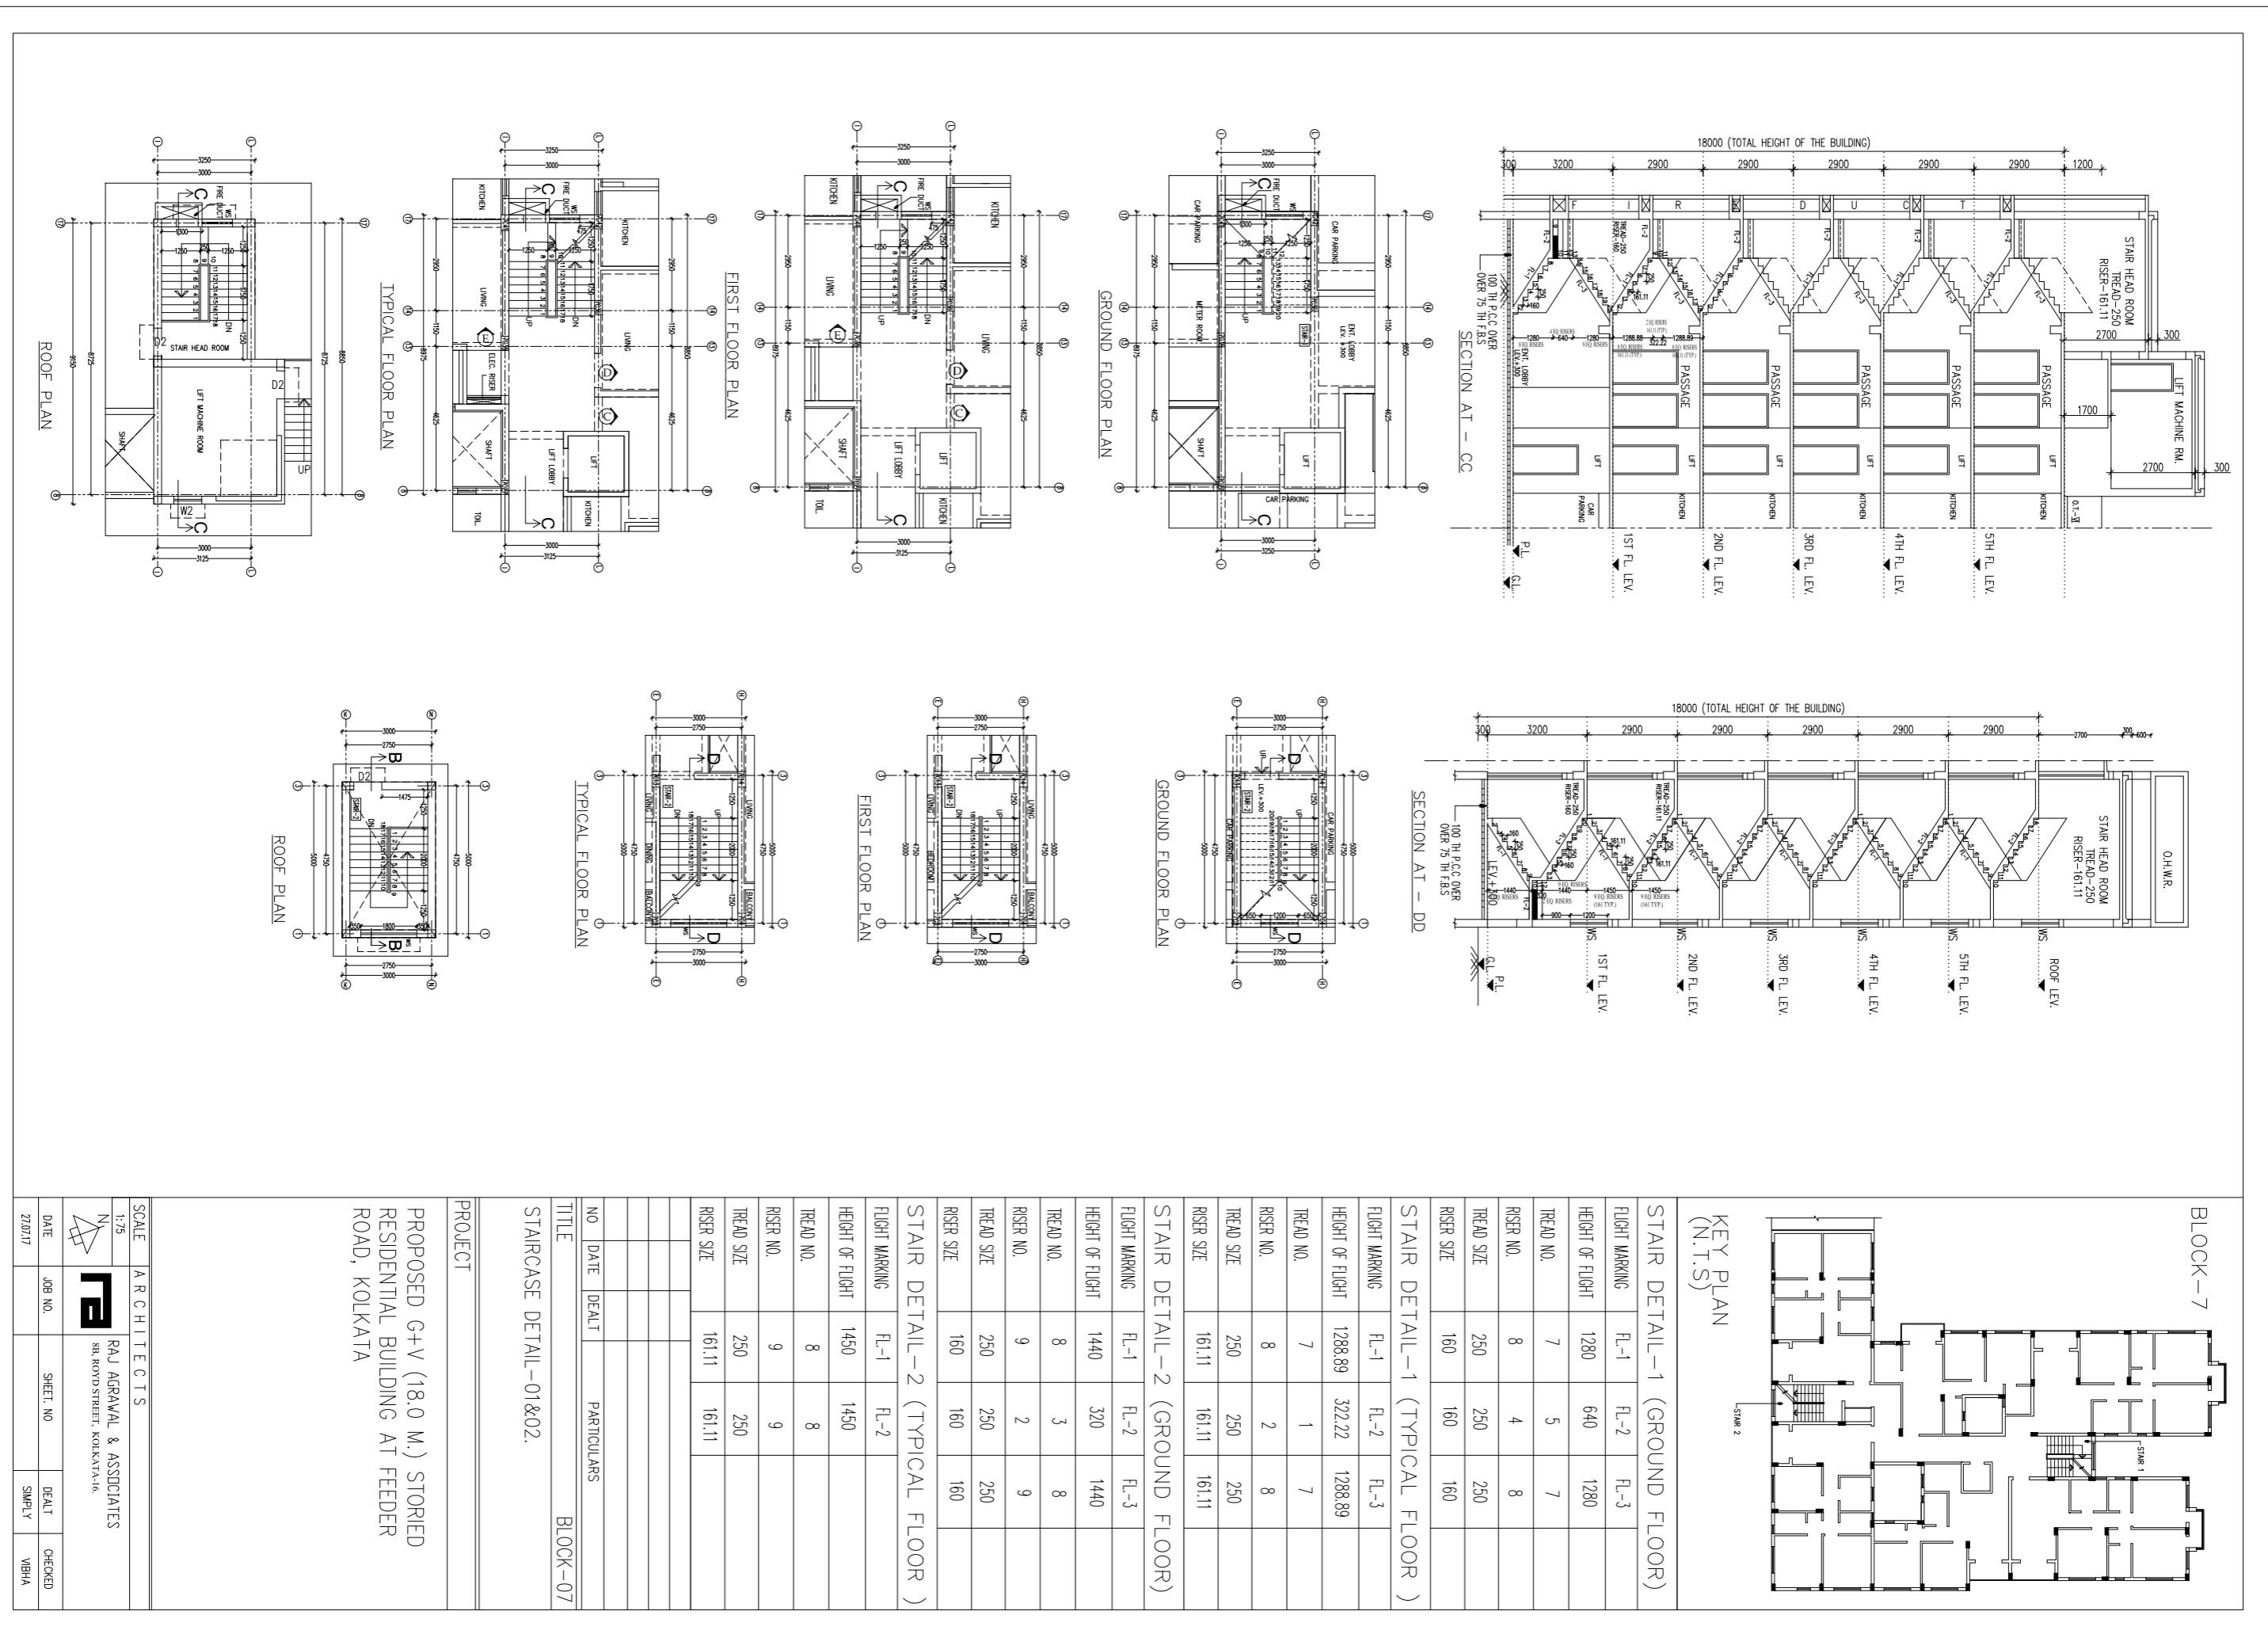


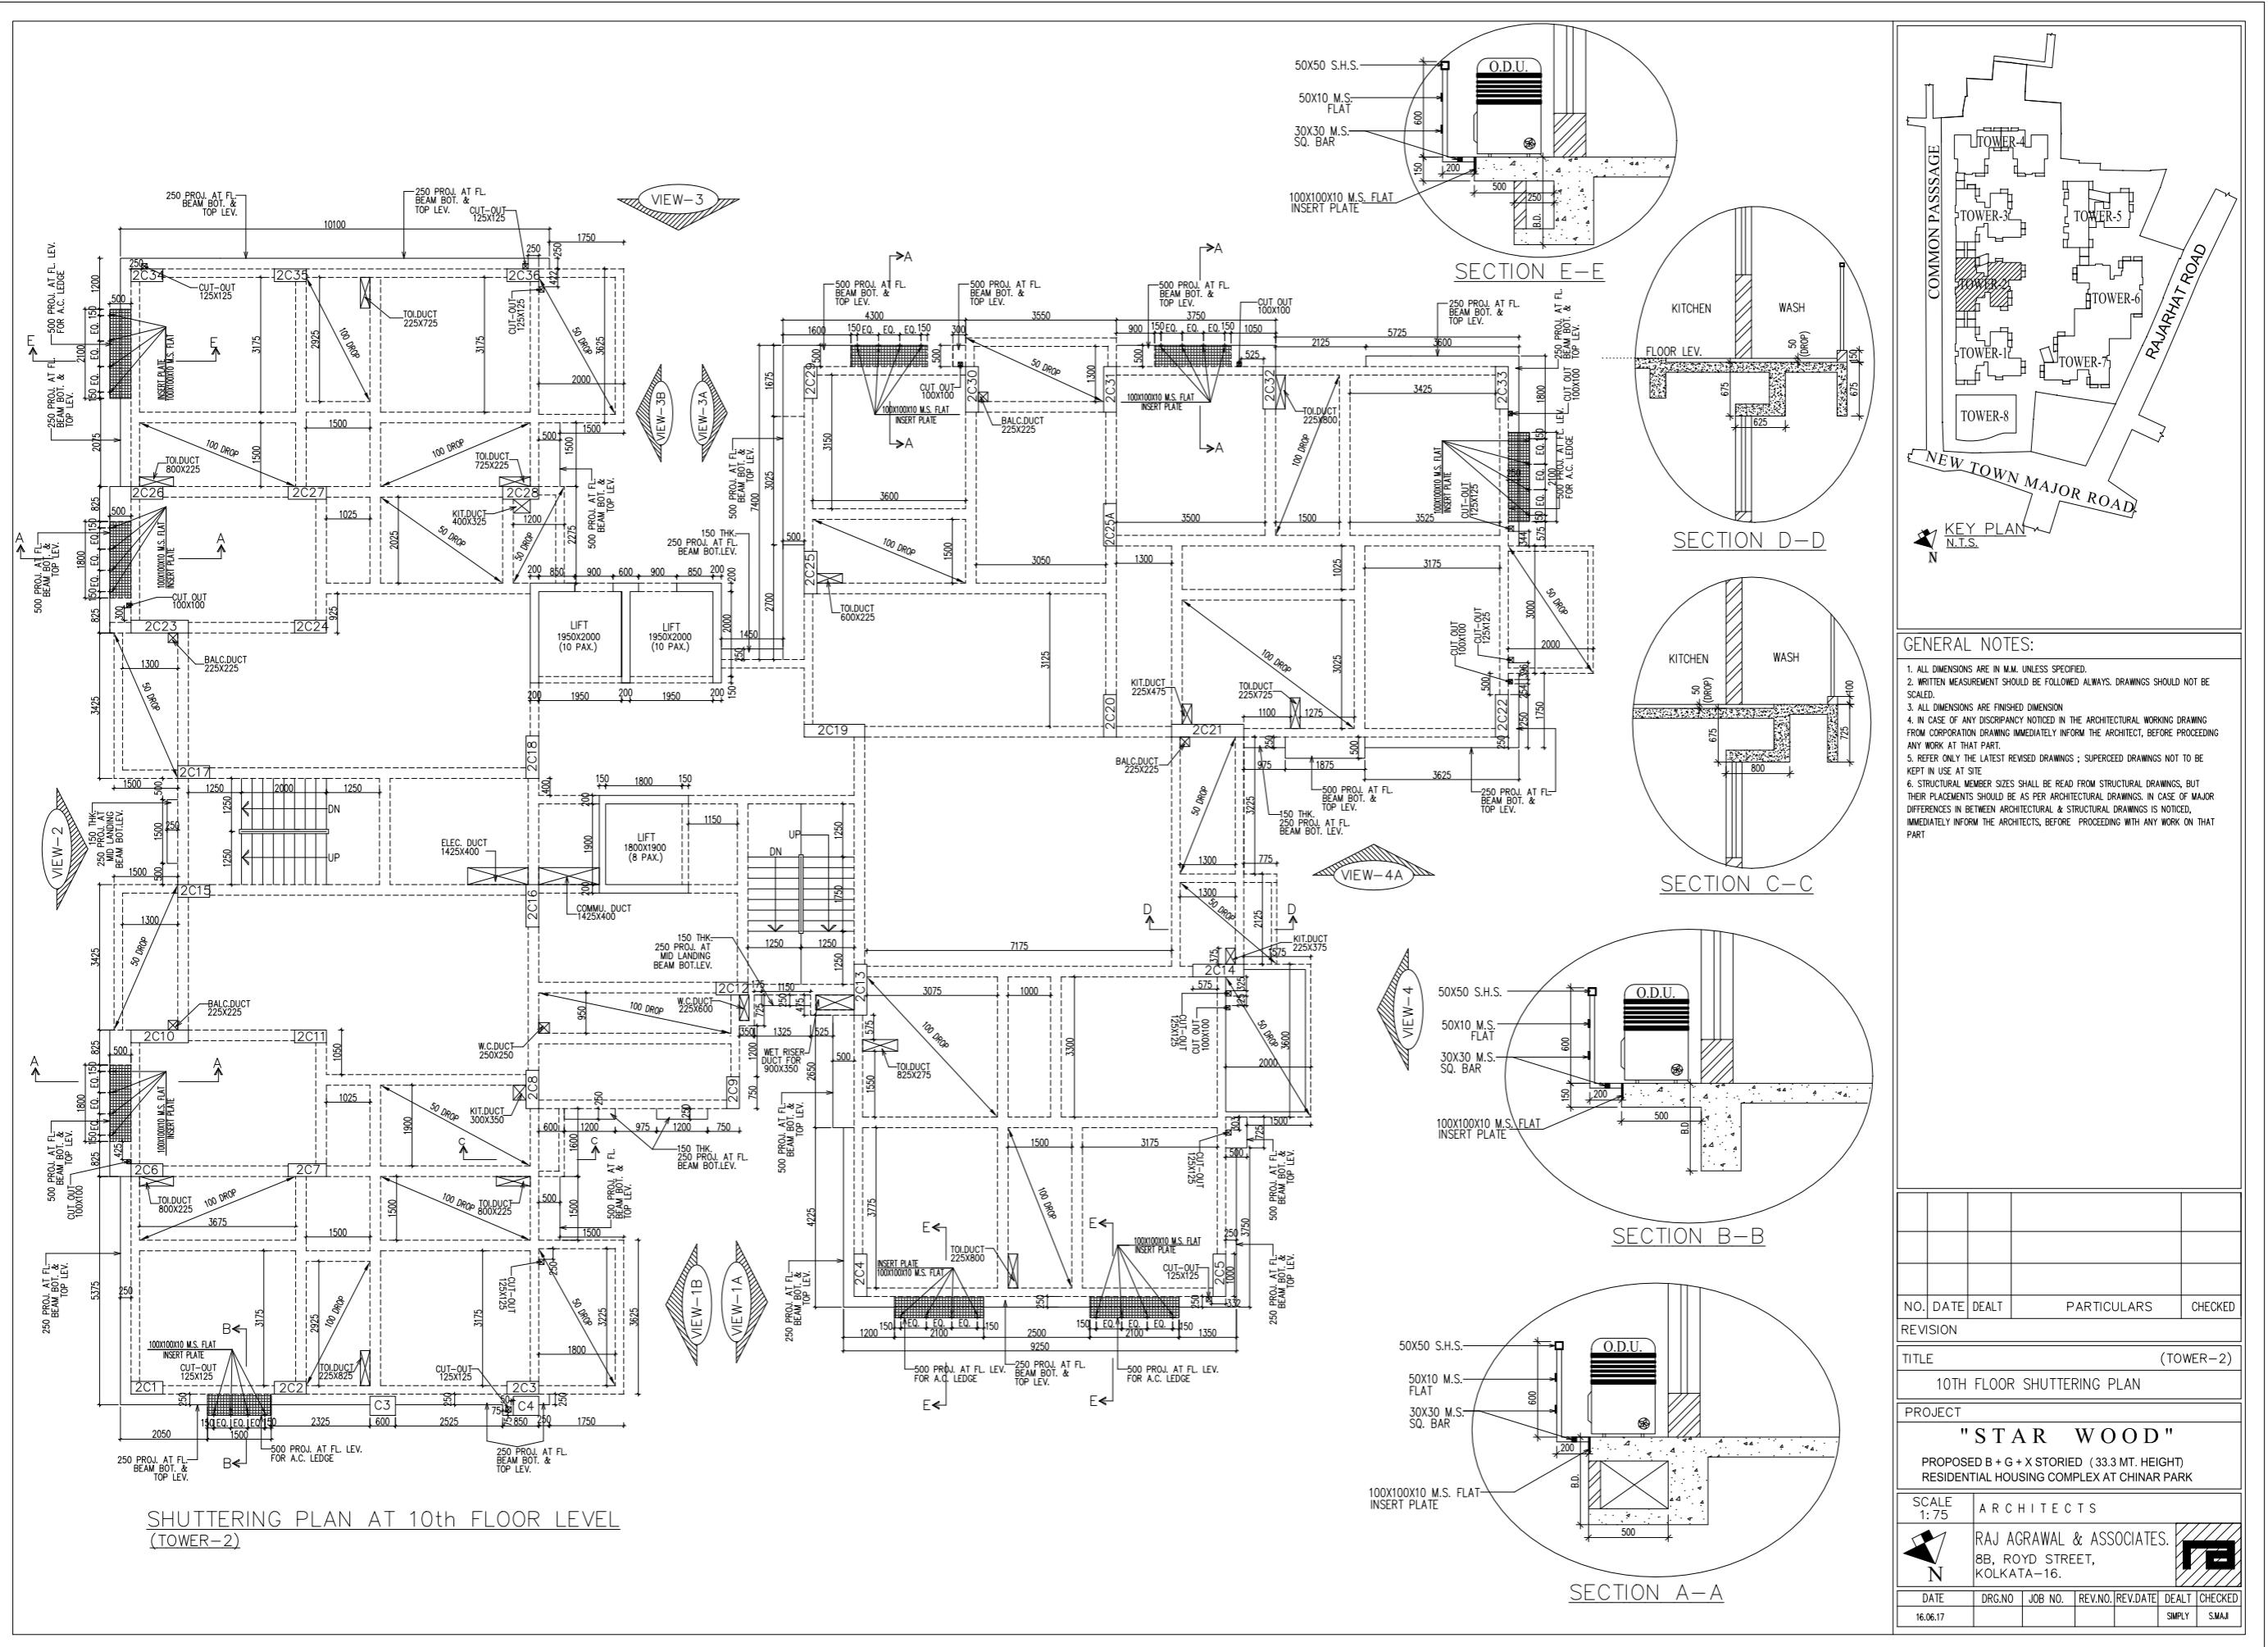


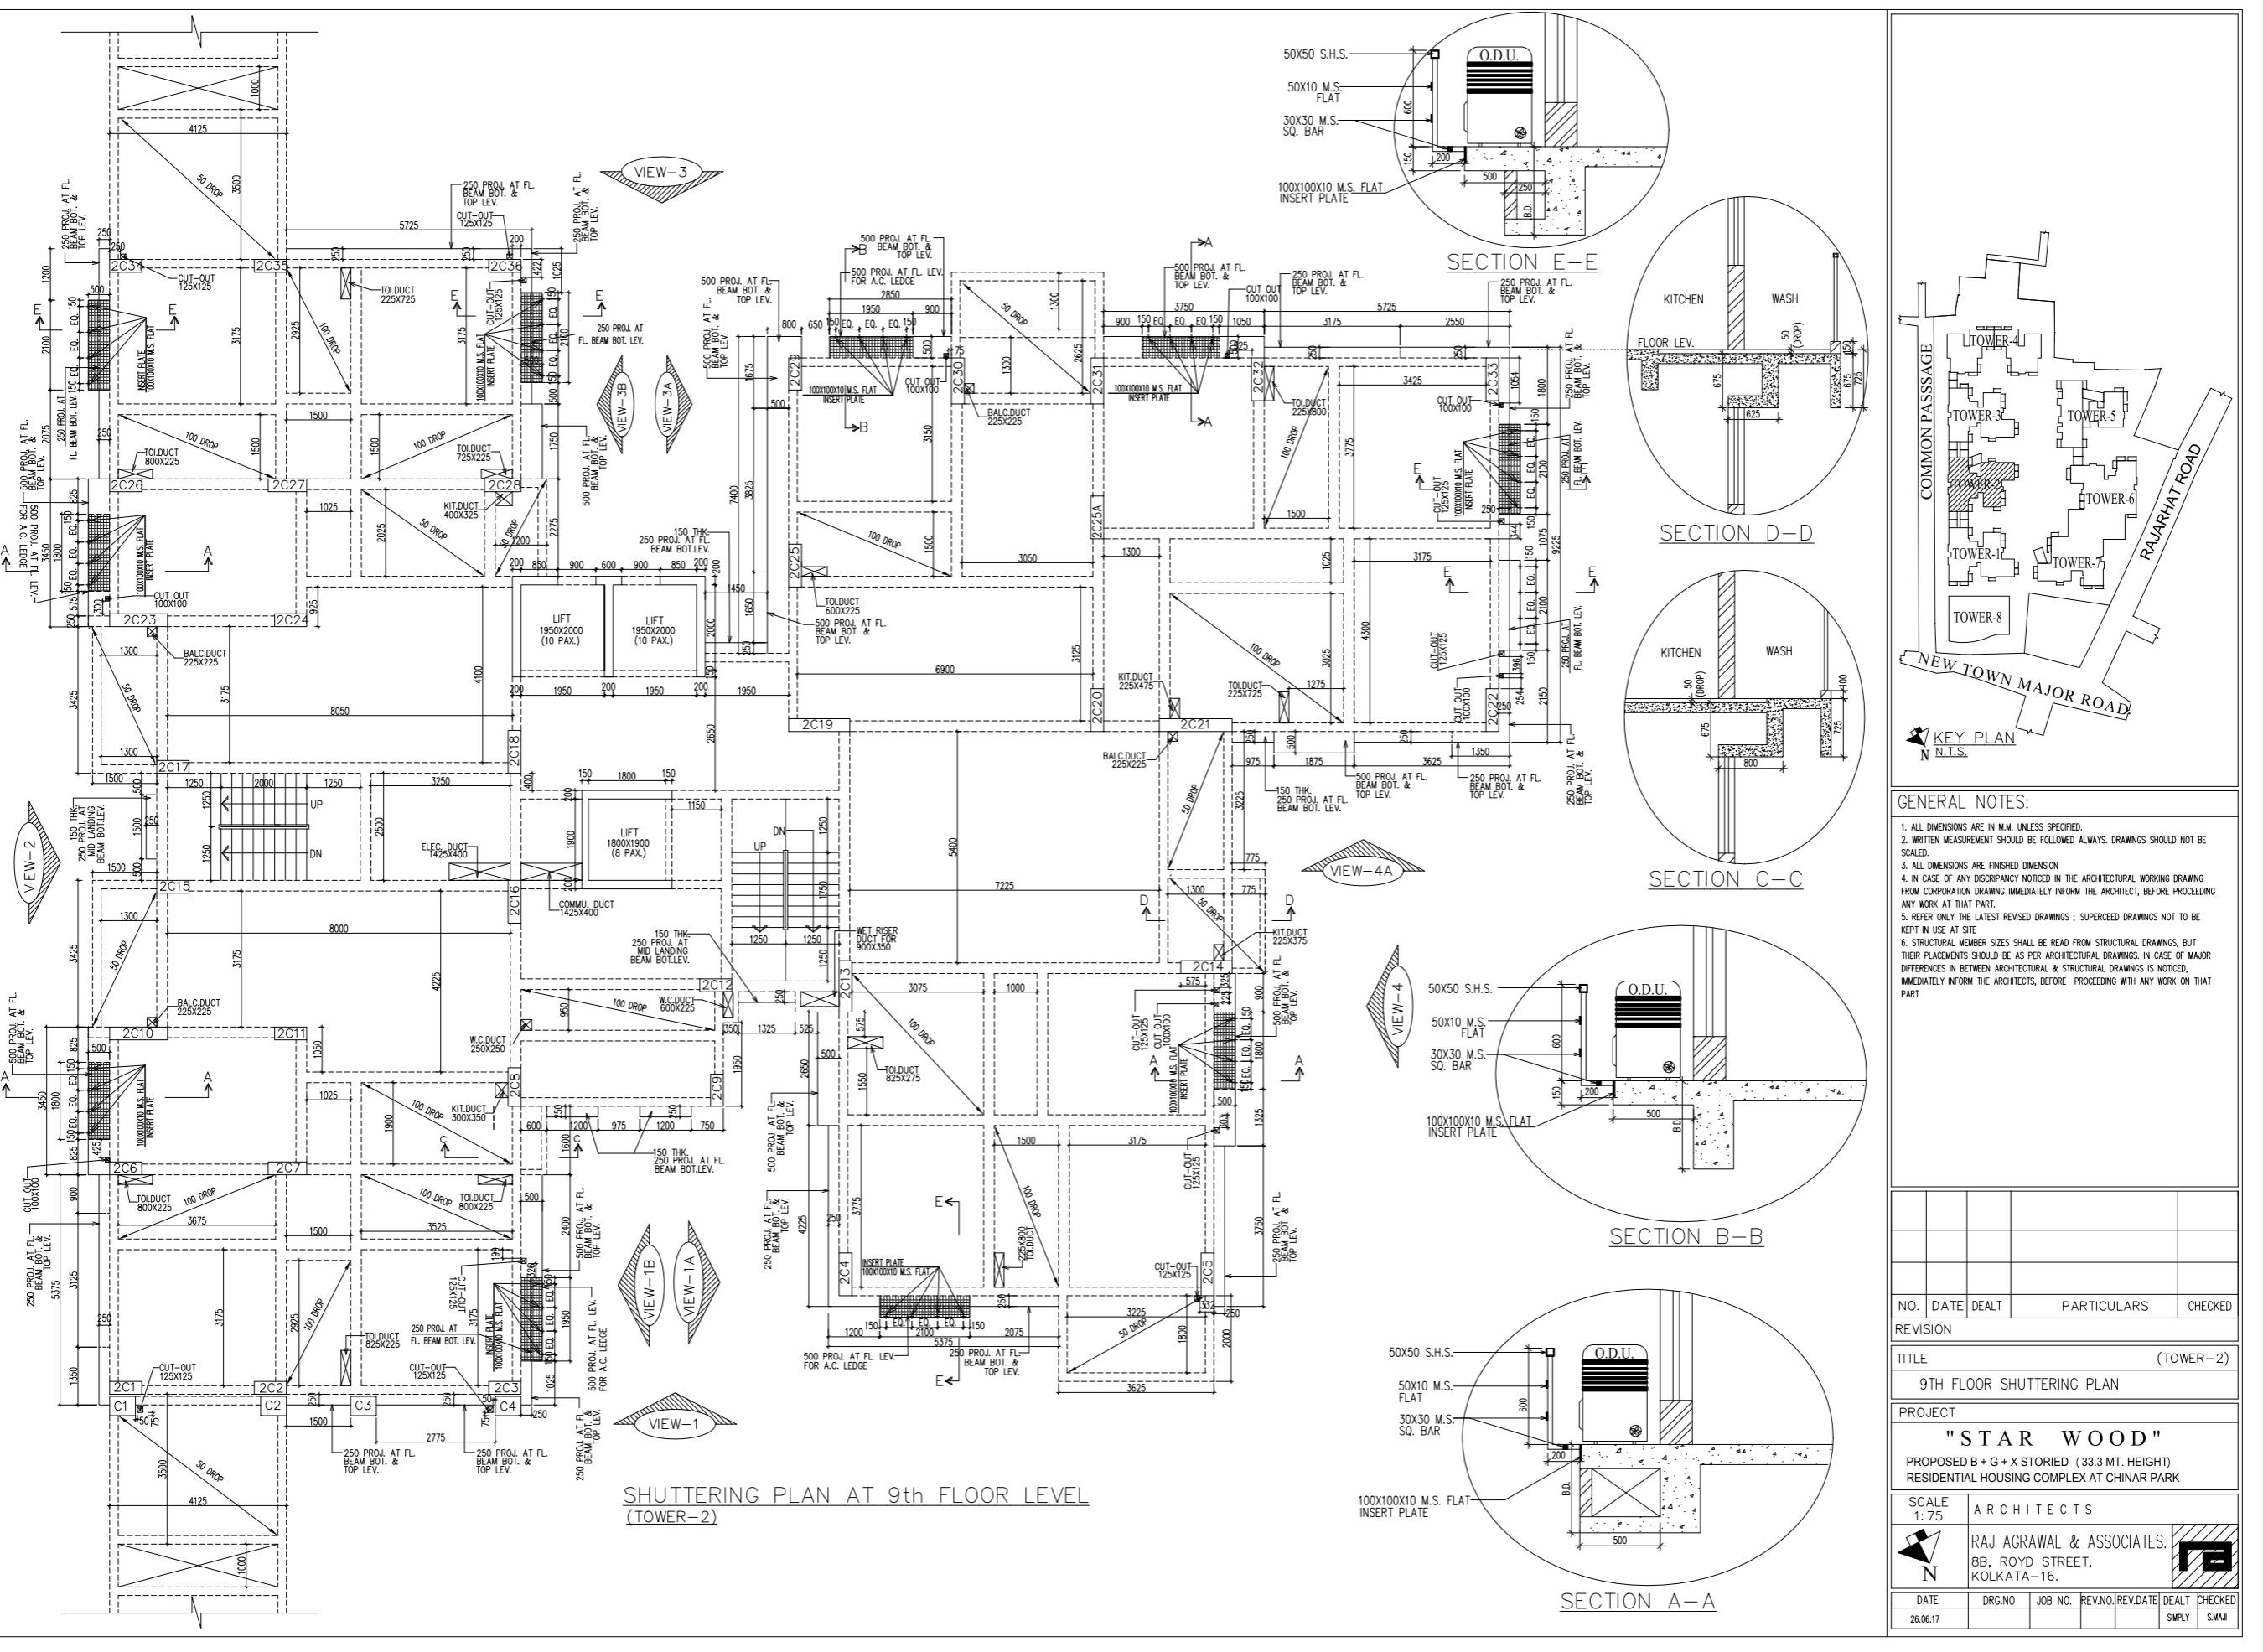

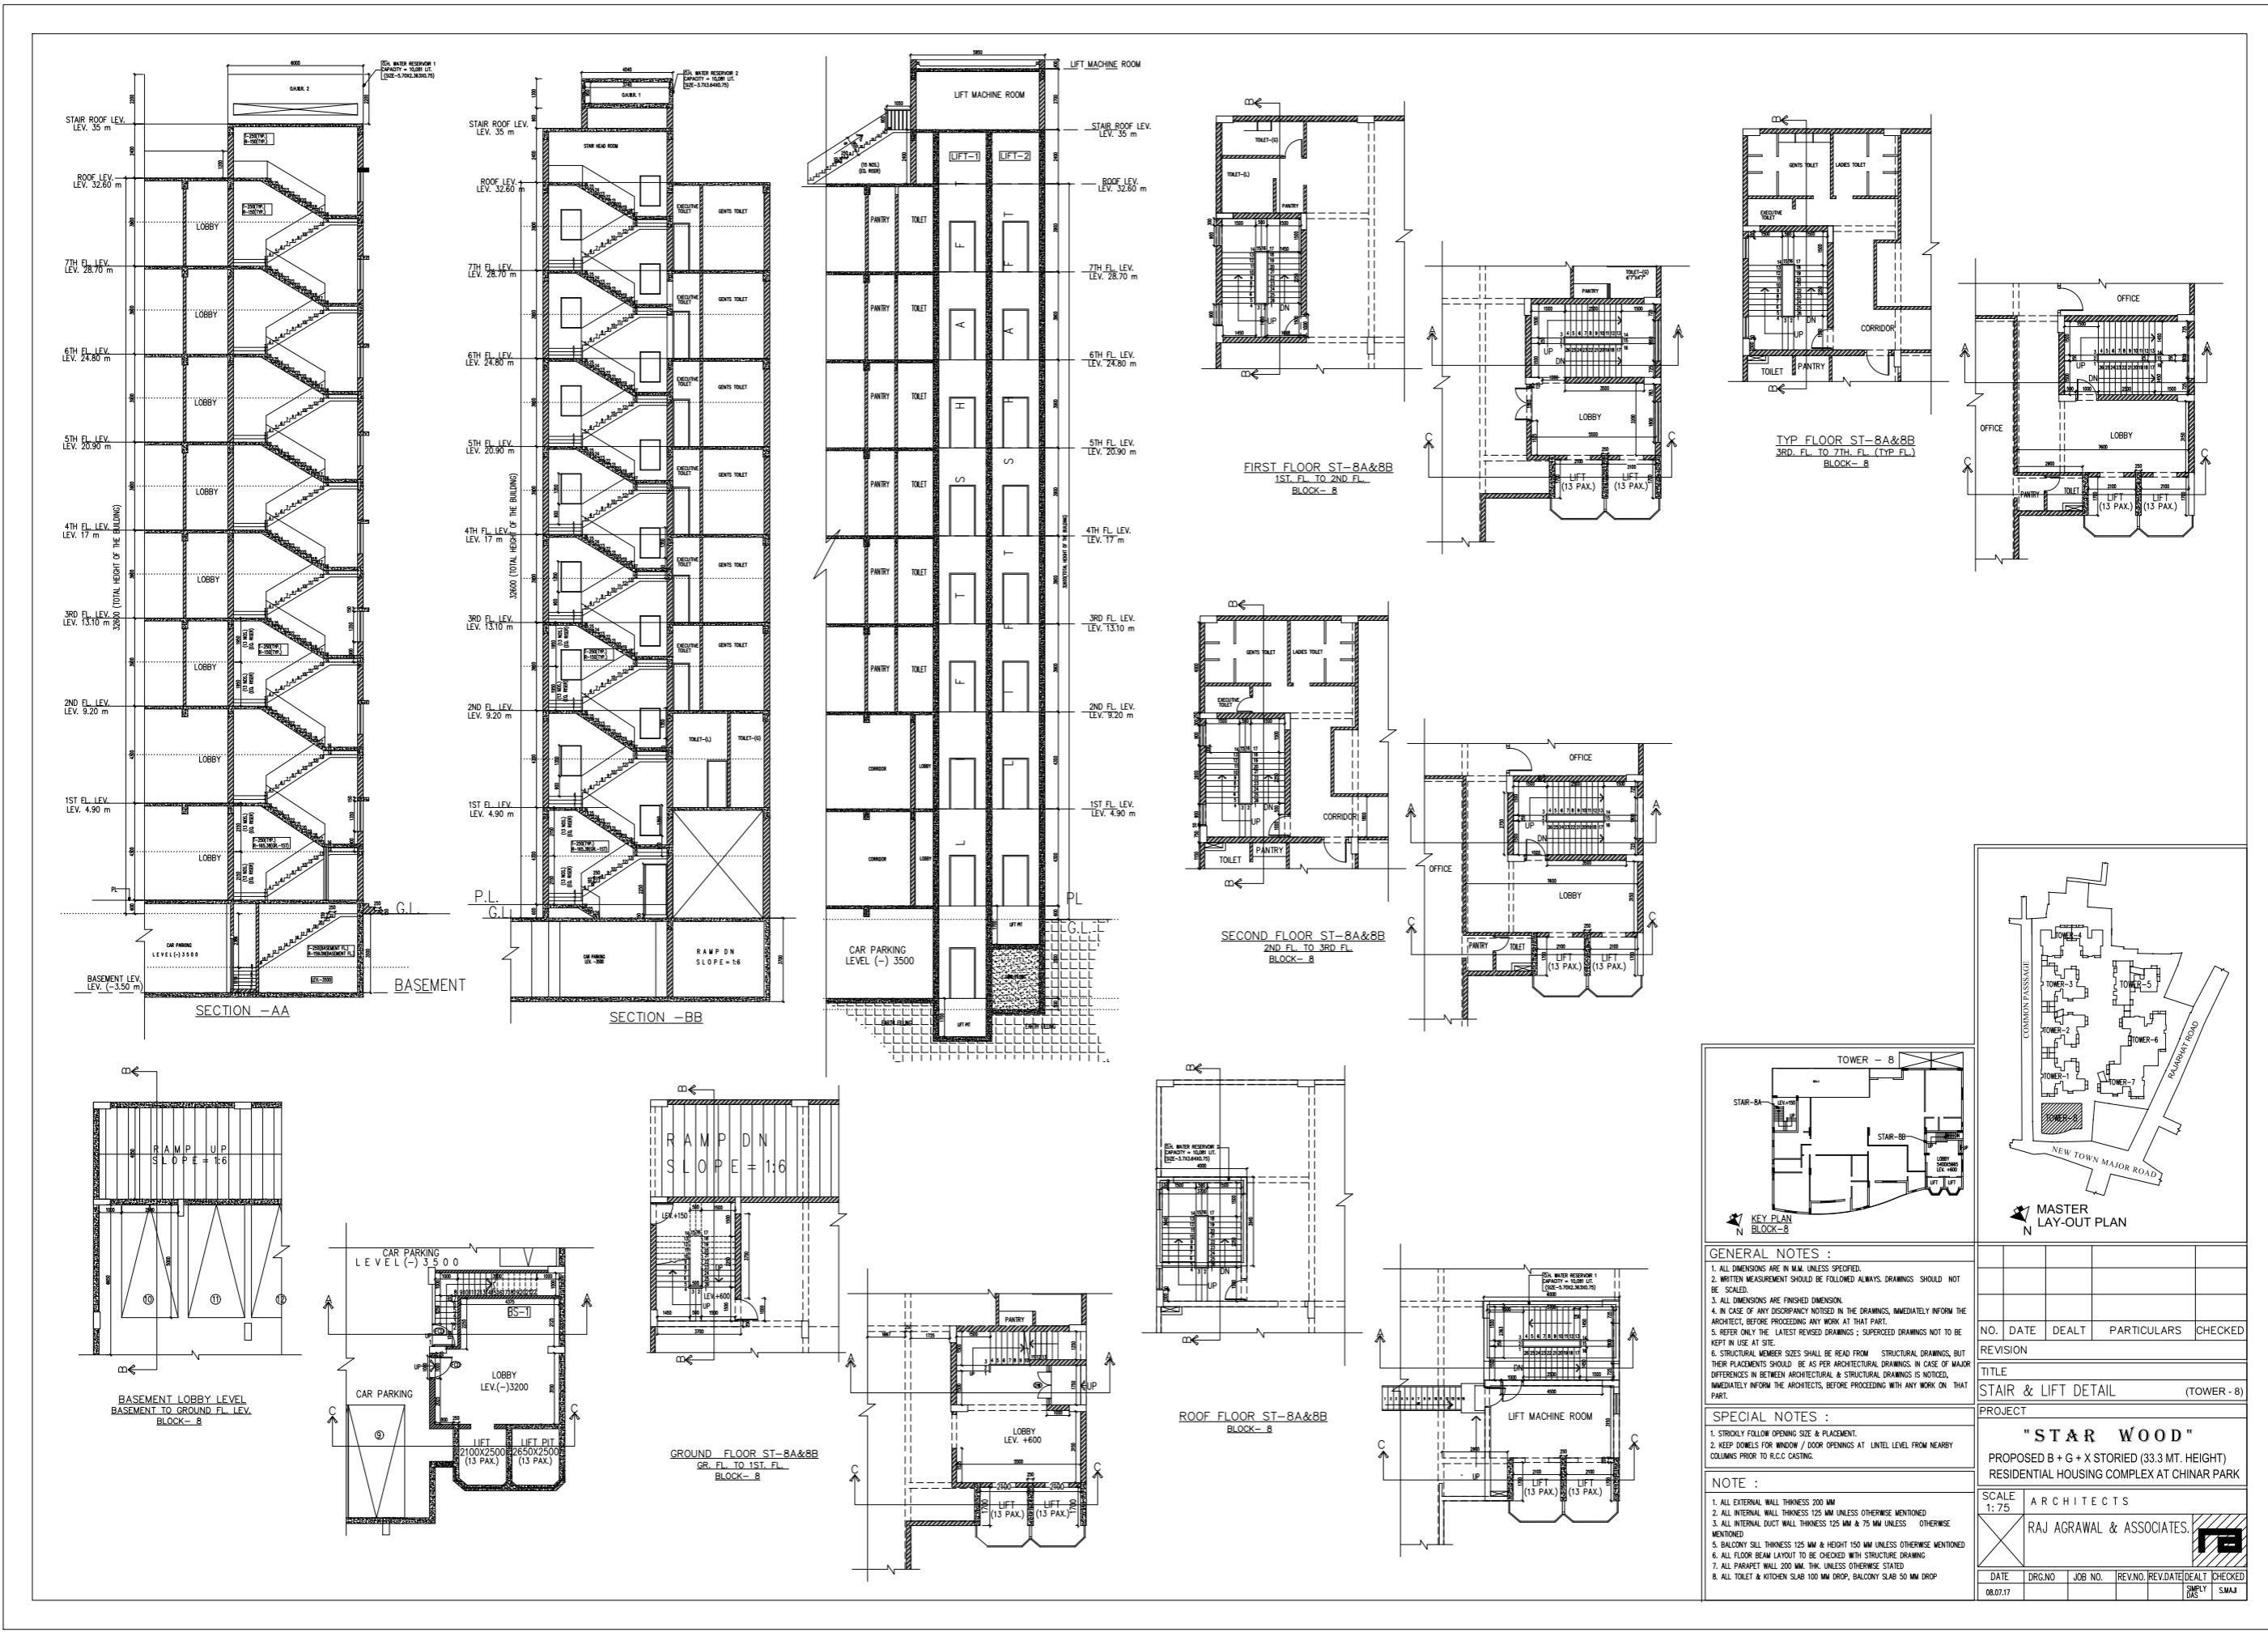

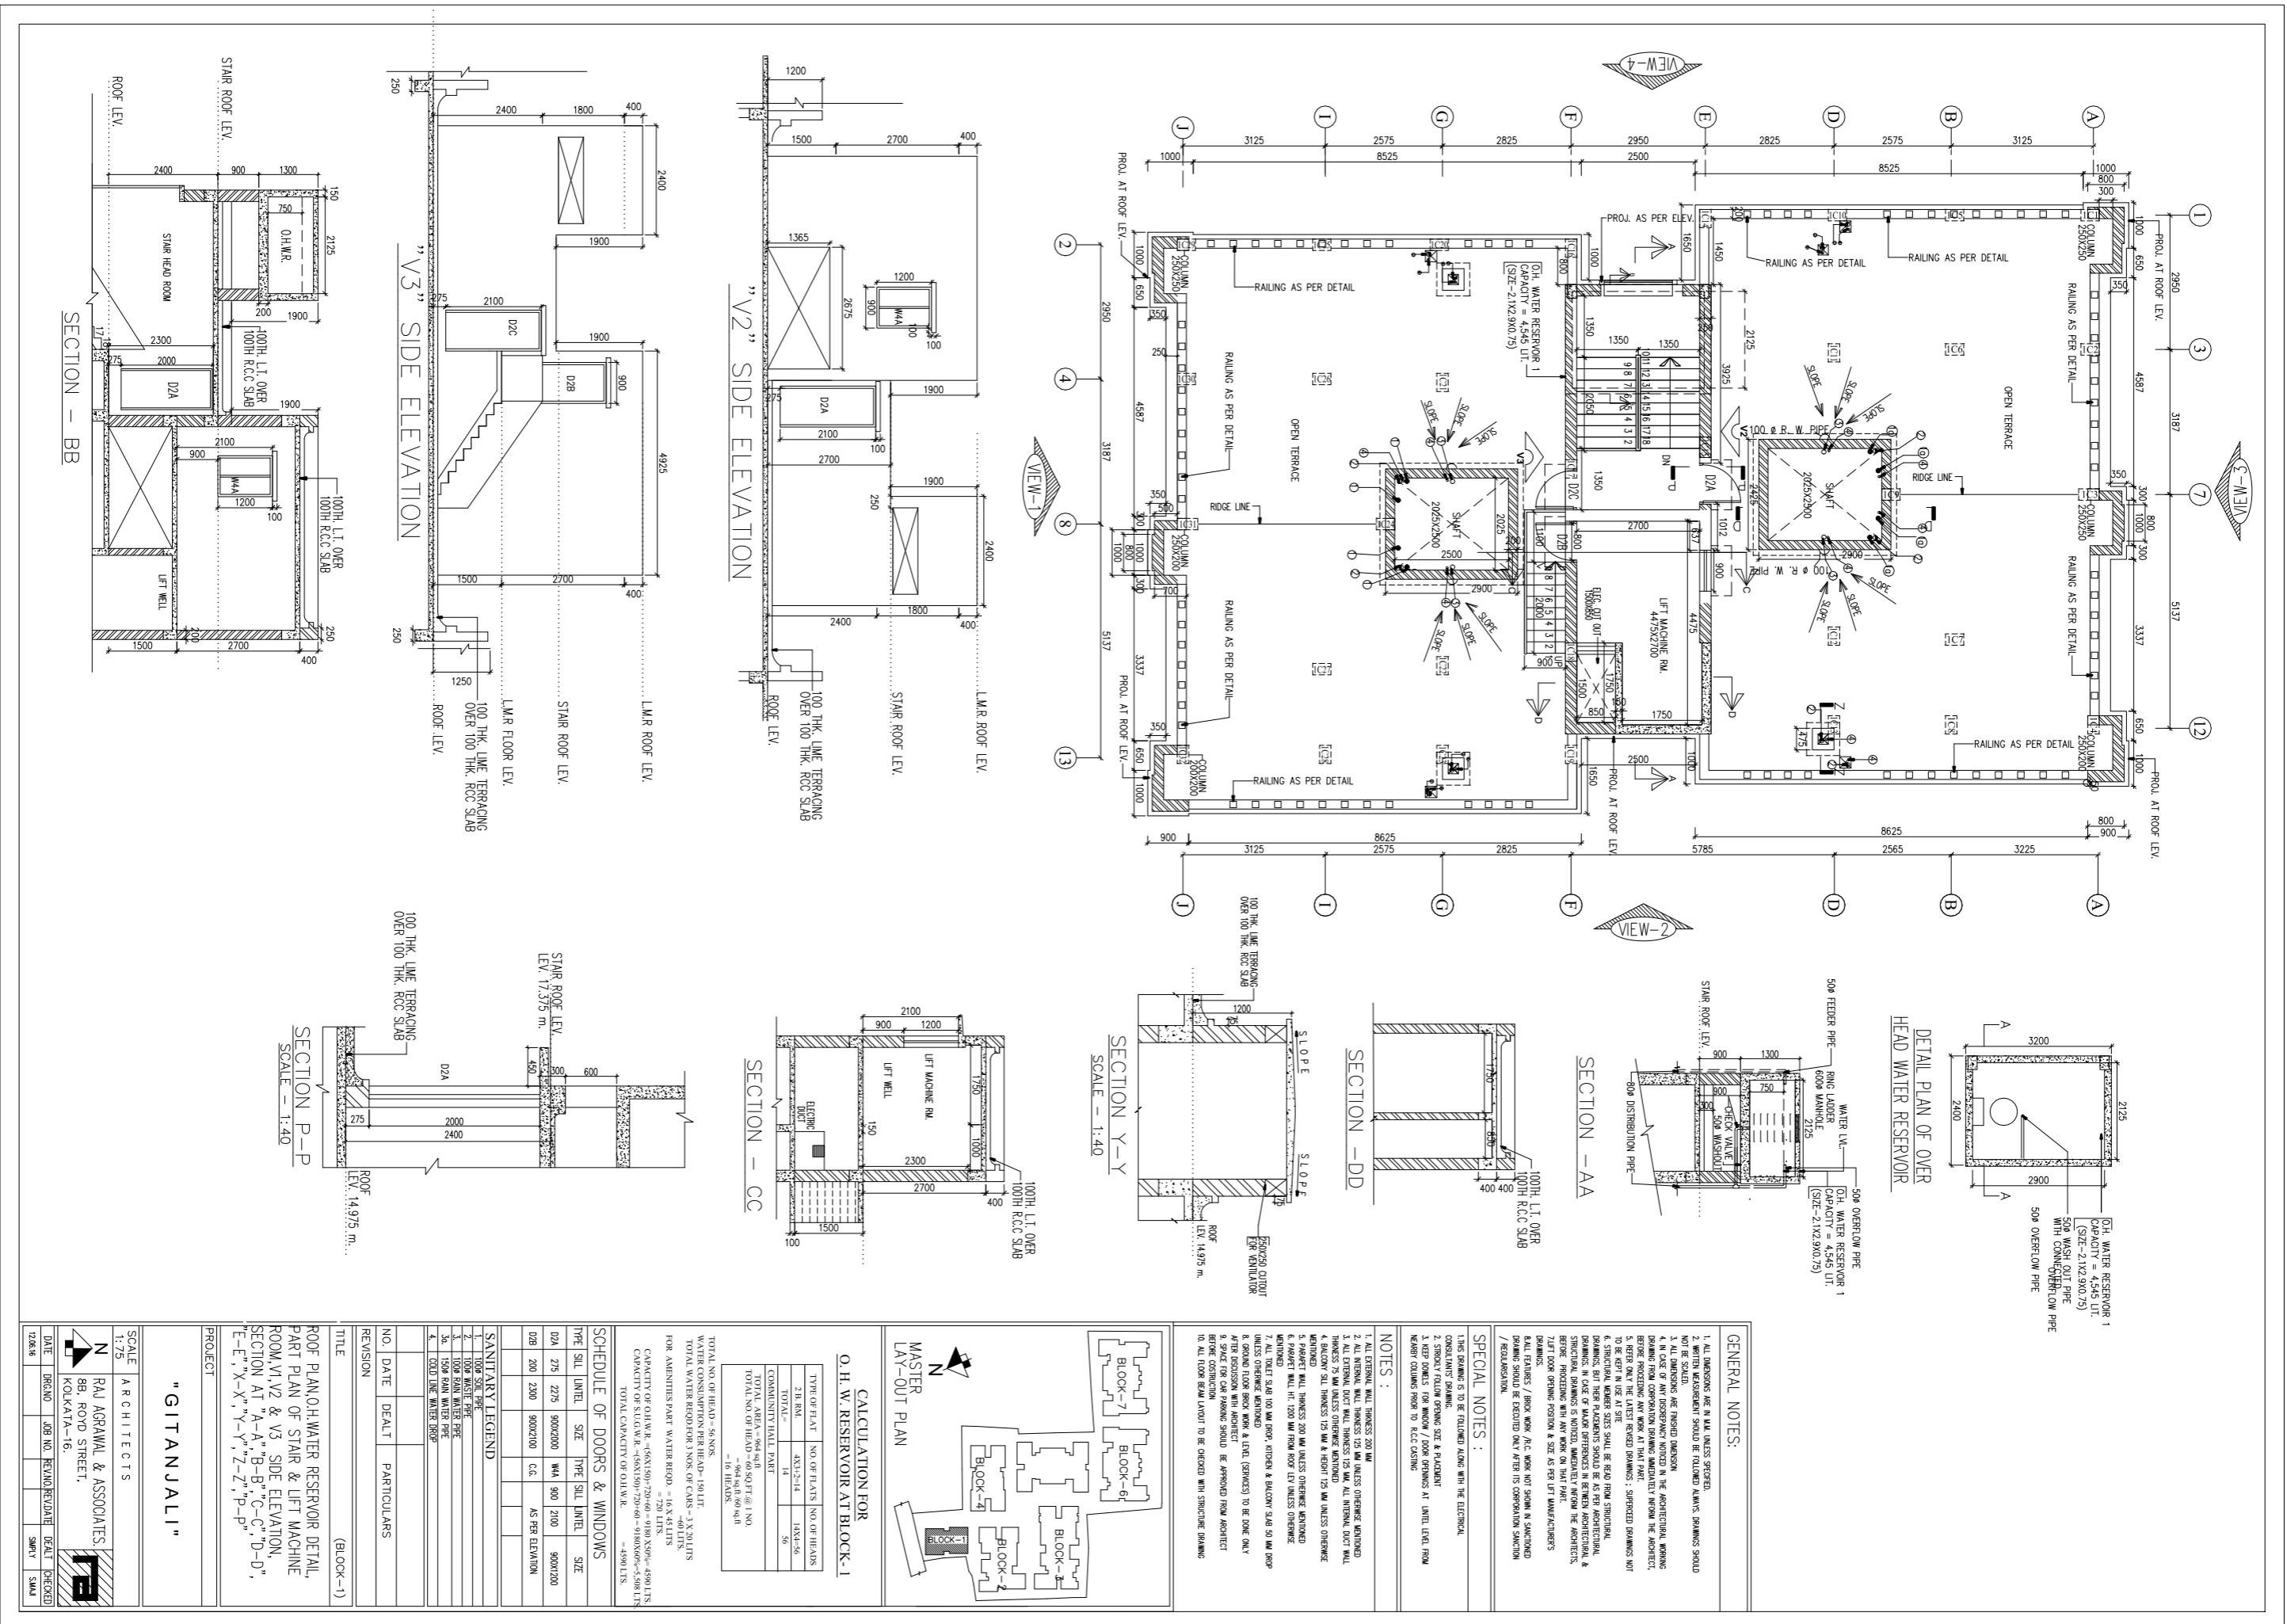

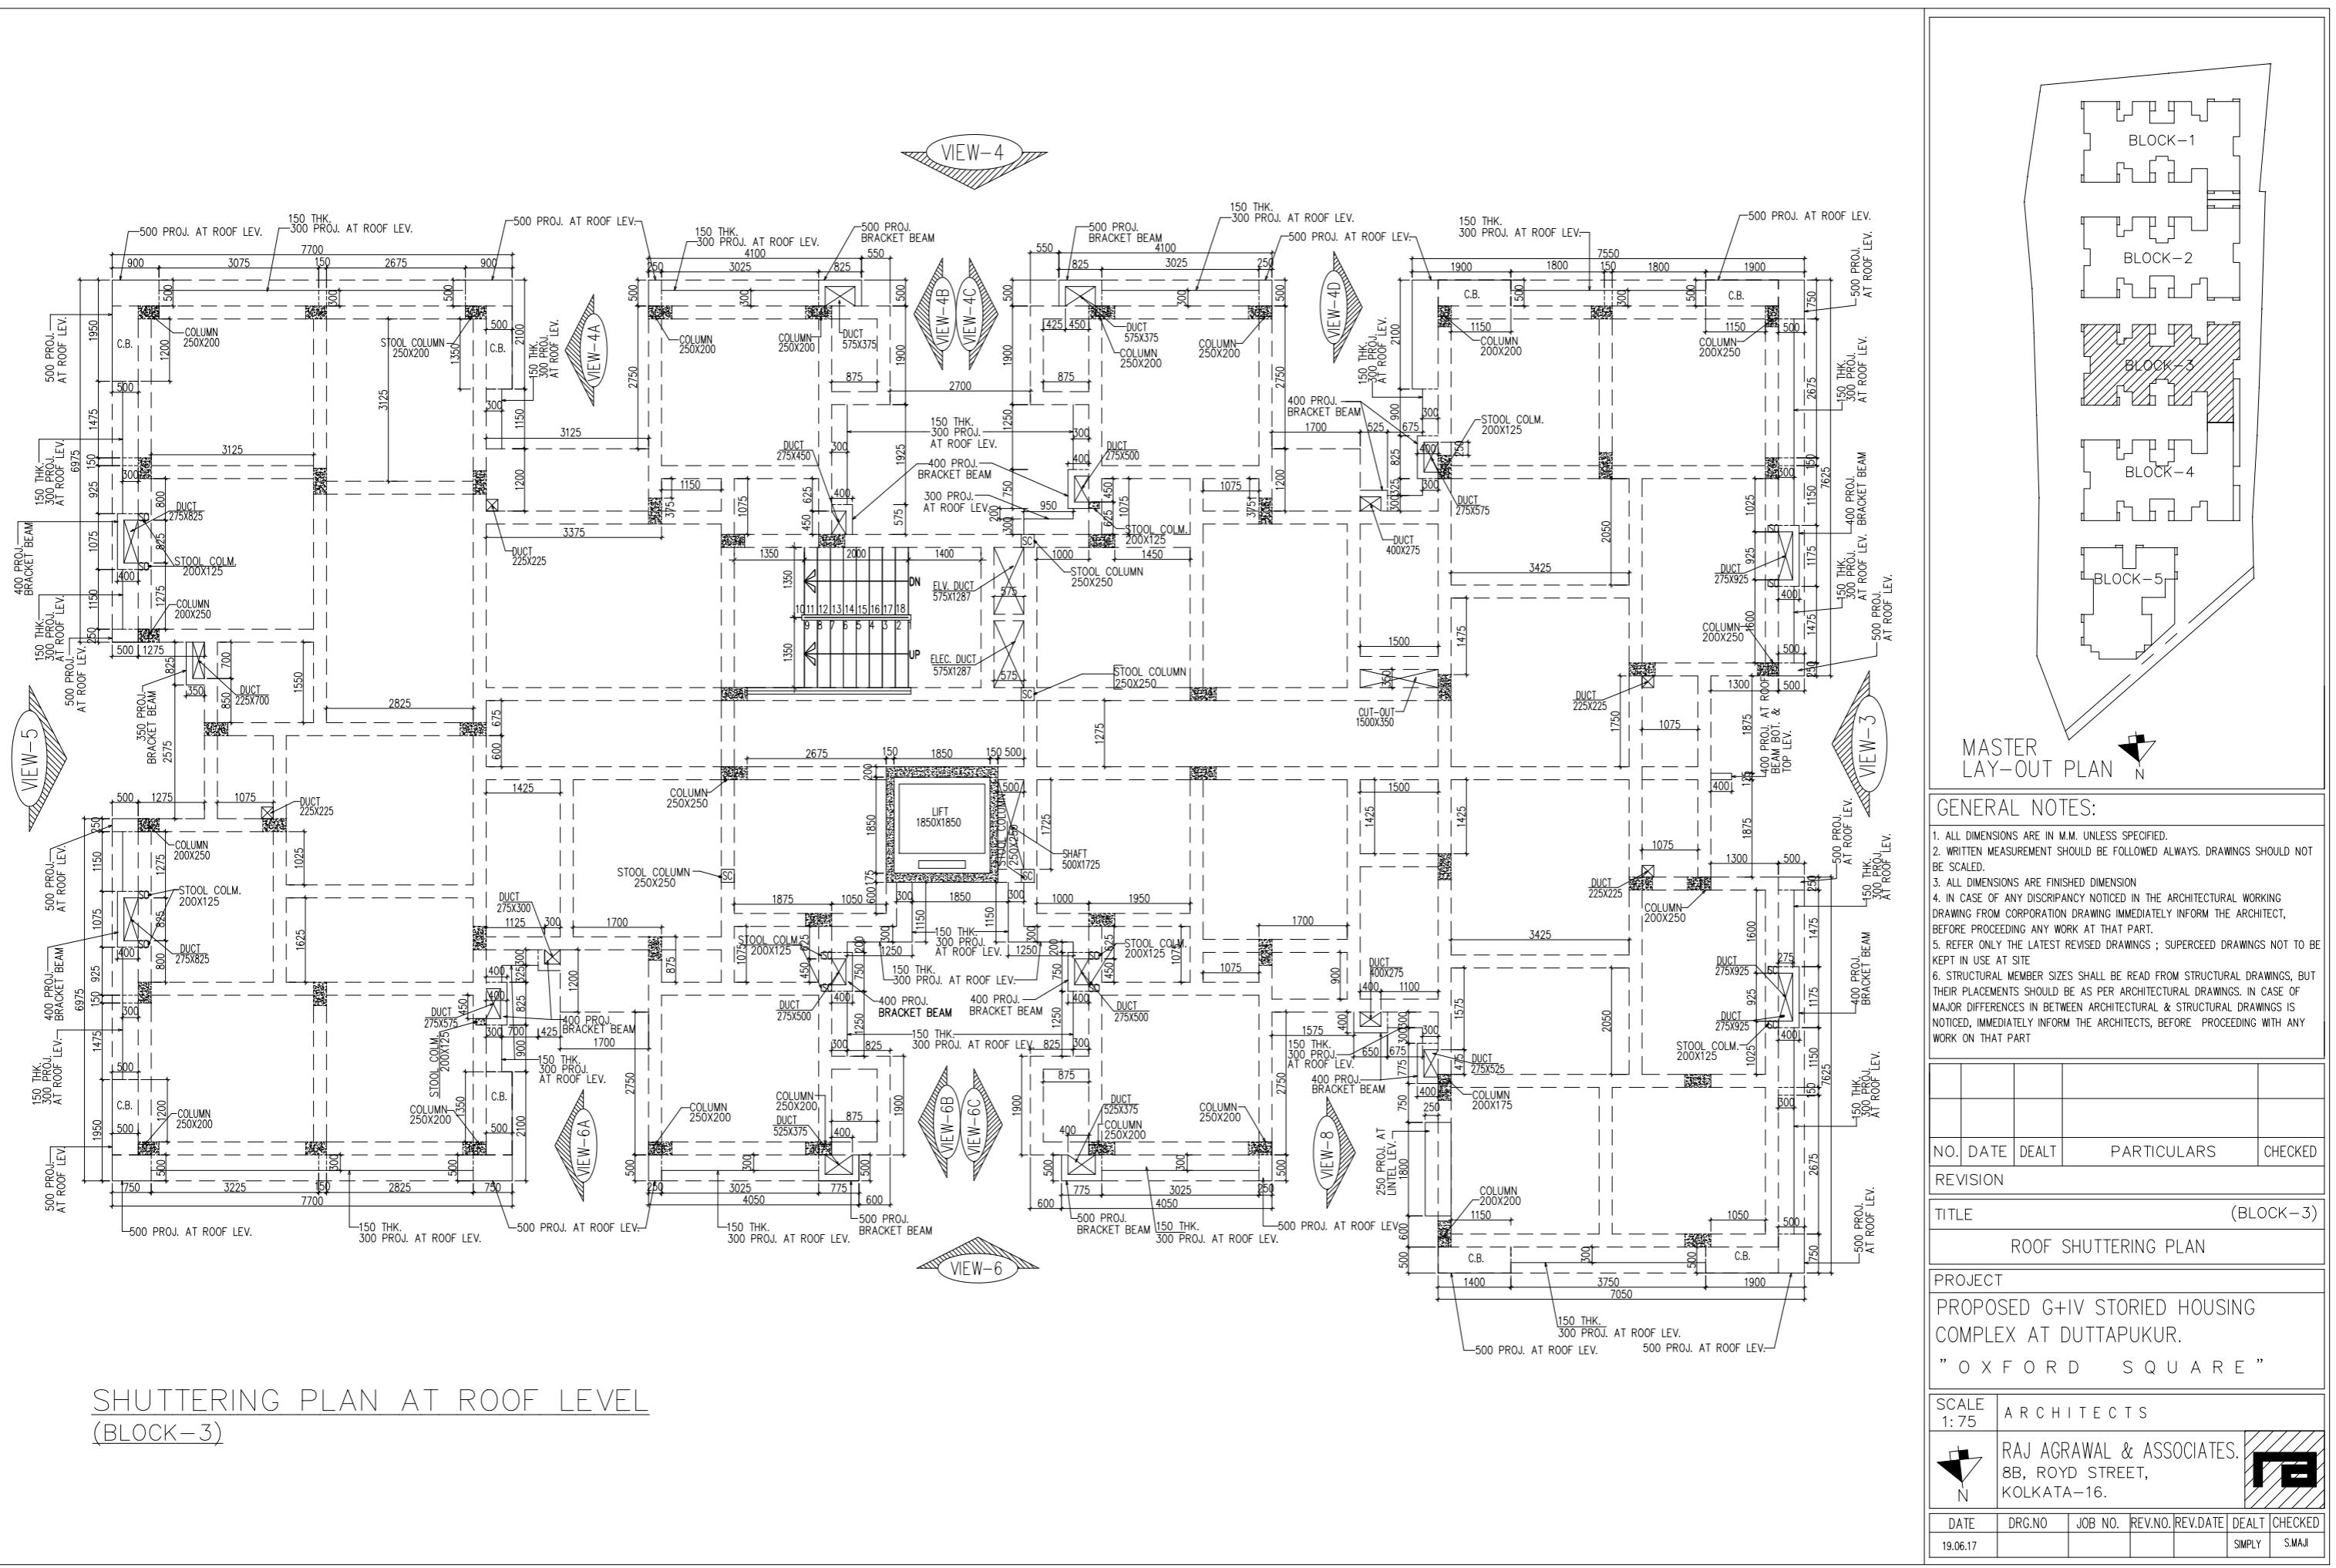

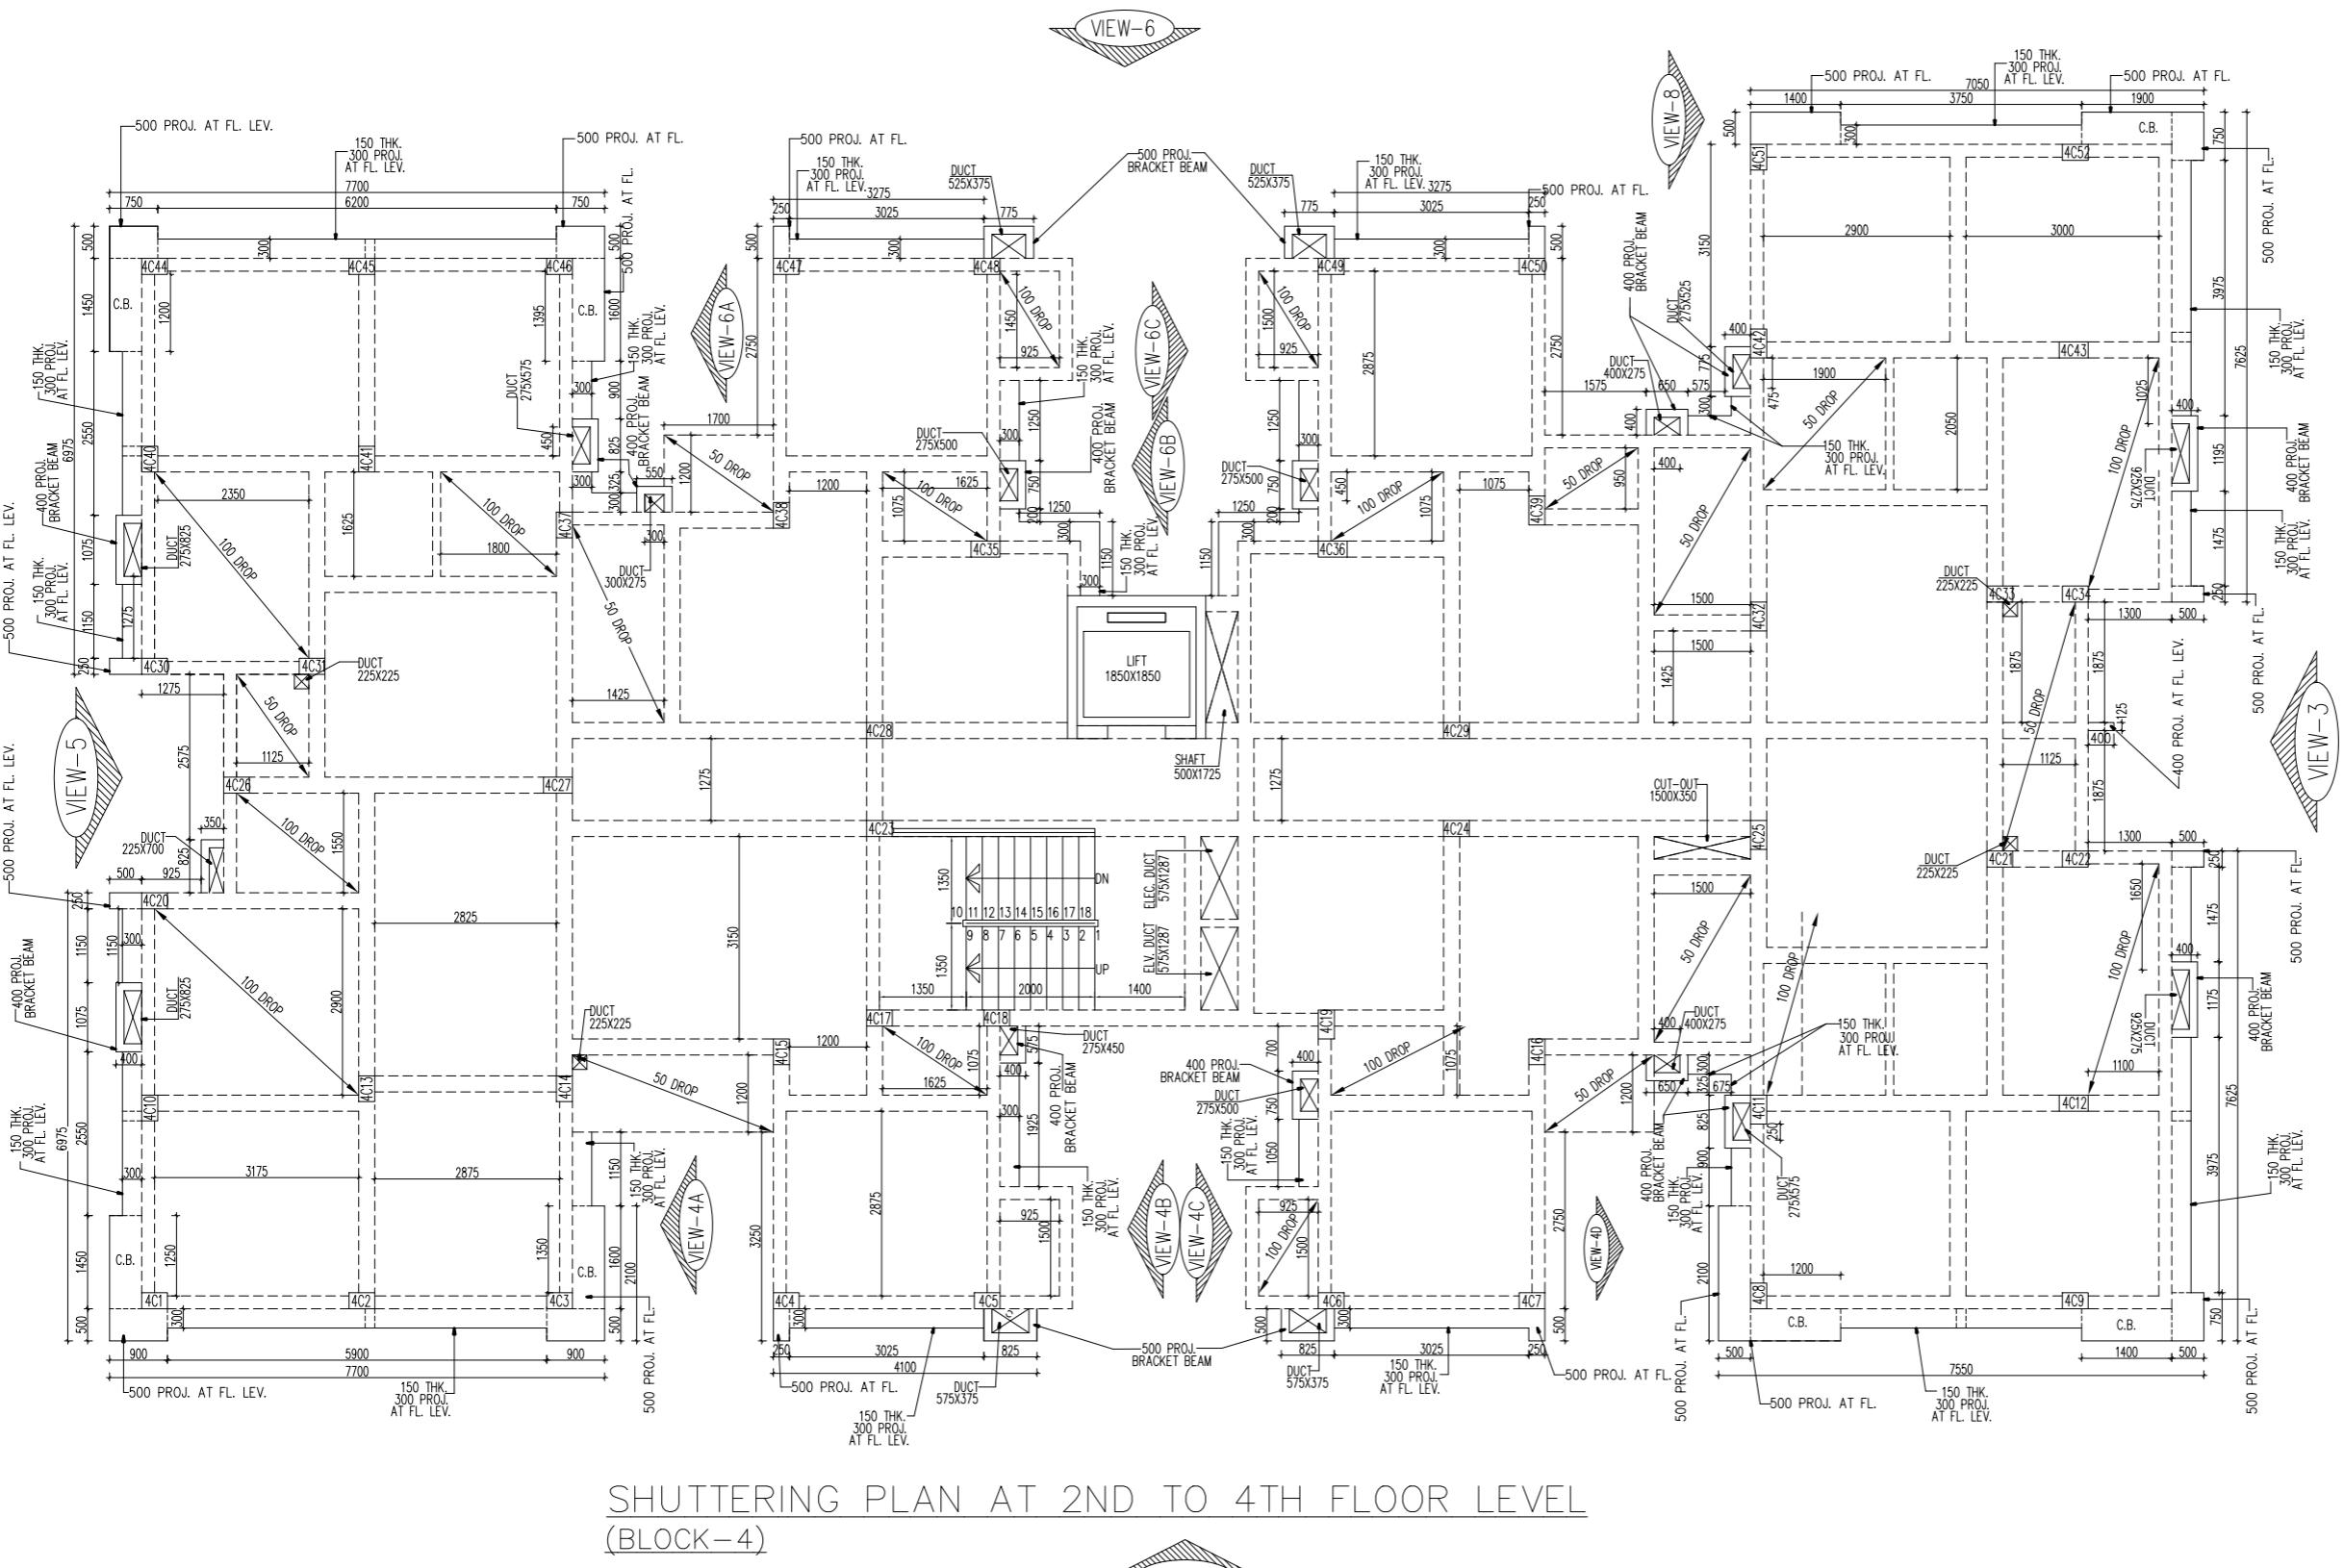

GENERAL NOTES:

- ALL DIMENSIONS ARE IN M.M. UNLESS SPECIFIED.
- WRITTEN MEASUREMENT SHOULD BE FOLLOWED ALWAYS. DRAWINGS SHOULD NOT BE SCALED.
- ALL DIMENSIONS ARE FINISHED DIMENSION
- IN CASE OF ANY DISCREPANCY NOTICED IN THE ARCHITECTURAL WORKING DRAWING FROM CORPORATION DRAWING IMMEDIATELY INFORM THE ARCHITECT, BEFORE PROCEEDING ANY WORK AT THAT PART.
- REFER ONLY THE LATEST REVISED DRAWINGS ; SUPERSEDED DRAWINGS NOT TO BE KEPT IN USE AT SITE.
- STRUCTURAL MEMBER SIZES SHALL BE READ FROM STRUCTURAL DRAWINGS, BUT THEIR PLACEMENTS SHOULD BE AS PER ARCHITECTURAL DRAWINGS. IN CASE OF MAJOR DIFFERENCES IN BETWEEN ARCHITECTURAL & STRUCTURAL DRAWINGS IS NOTICED, IMMEDIATELY INFORM THE ARCHITECTS, BEFORE PROCEEDING WITH ANY WORK ON THAT PART


NO.	DATE	DEALT	PARTICULARS	CHECKED
REVISION				



TITLE (BLOCK-4)			
1ST FLOOR SHUTTERING PLAN			

PROJECT	
PROPOSED G+IV STORED HOUSING COMPLEX AT DUTTAPUKUR.	

" OXFORD SQUARE "

SCALE 1:75	ARCHITECTS
N	RAJ AGRAWAL & ASSOCIATES. 8B, ROYD STREET, KOLKATA-16.
DATE 09.06.17	DRG.NO JOB NO. REV.NO. REV.DATE DEALT SIMPLY S.MAJI

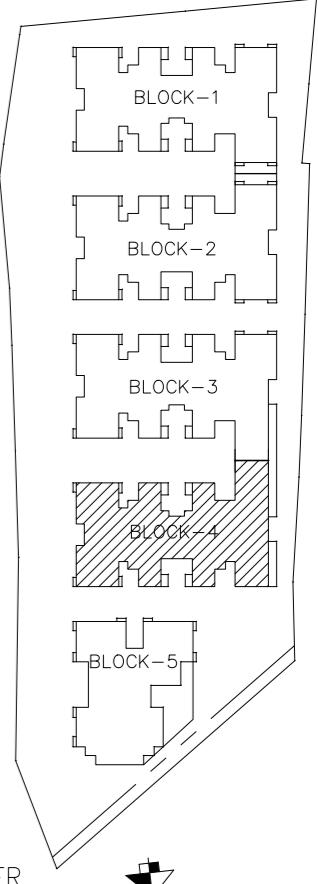

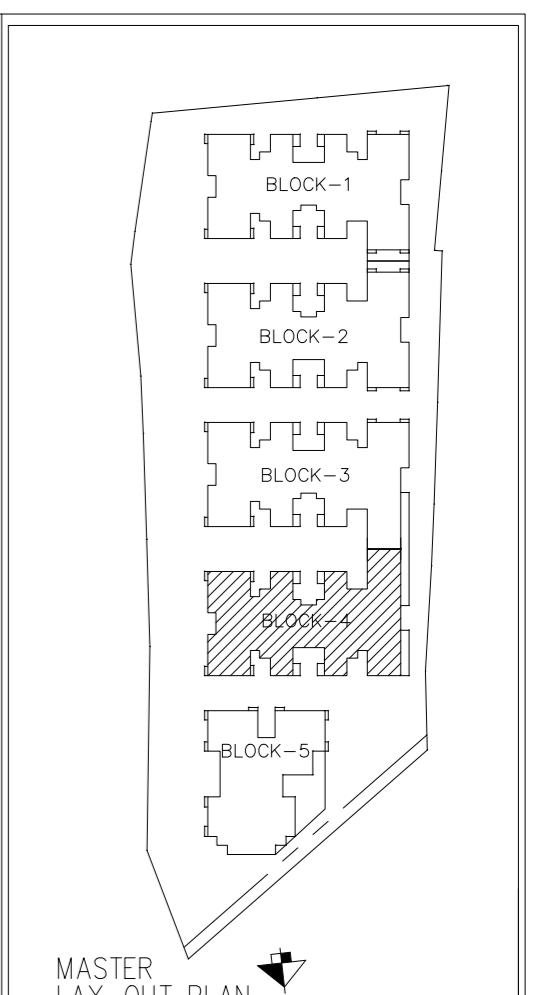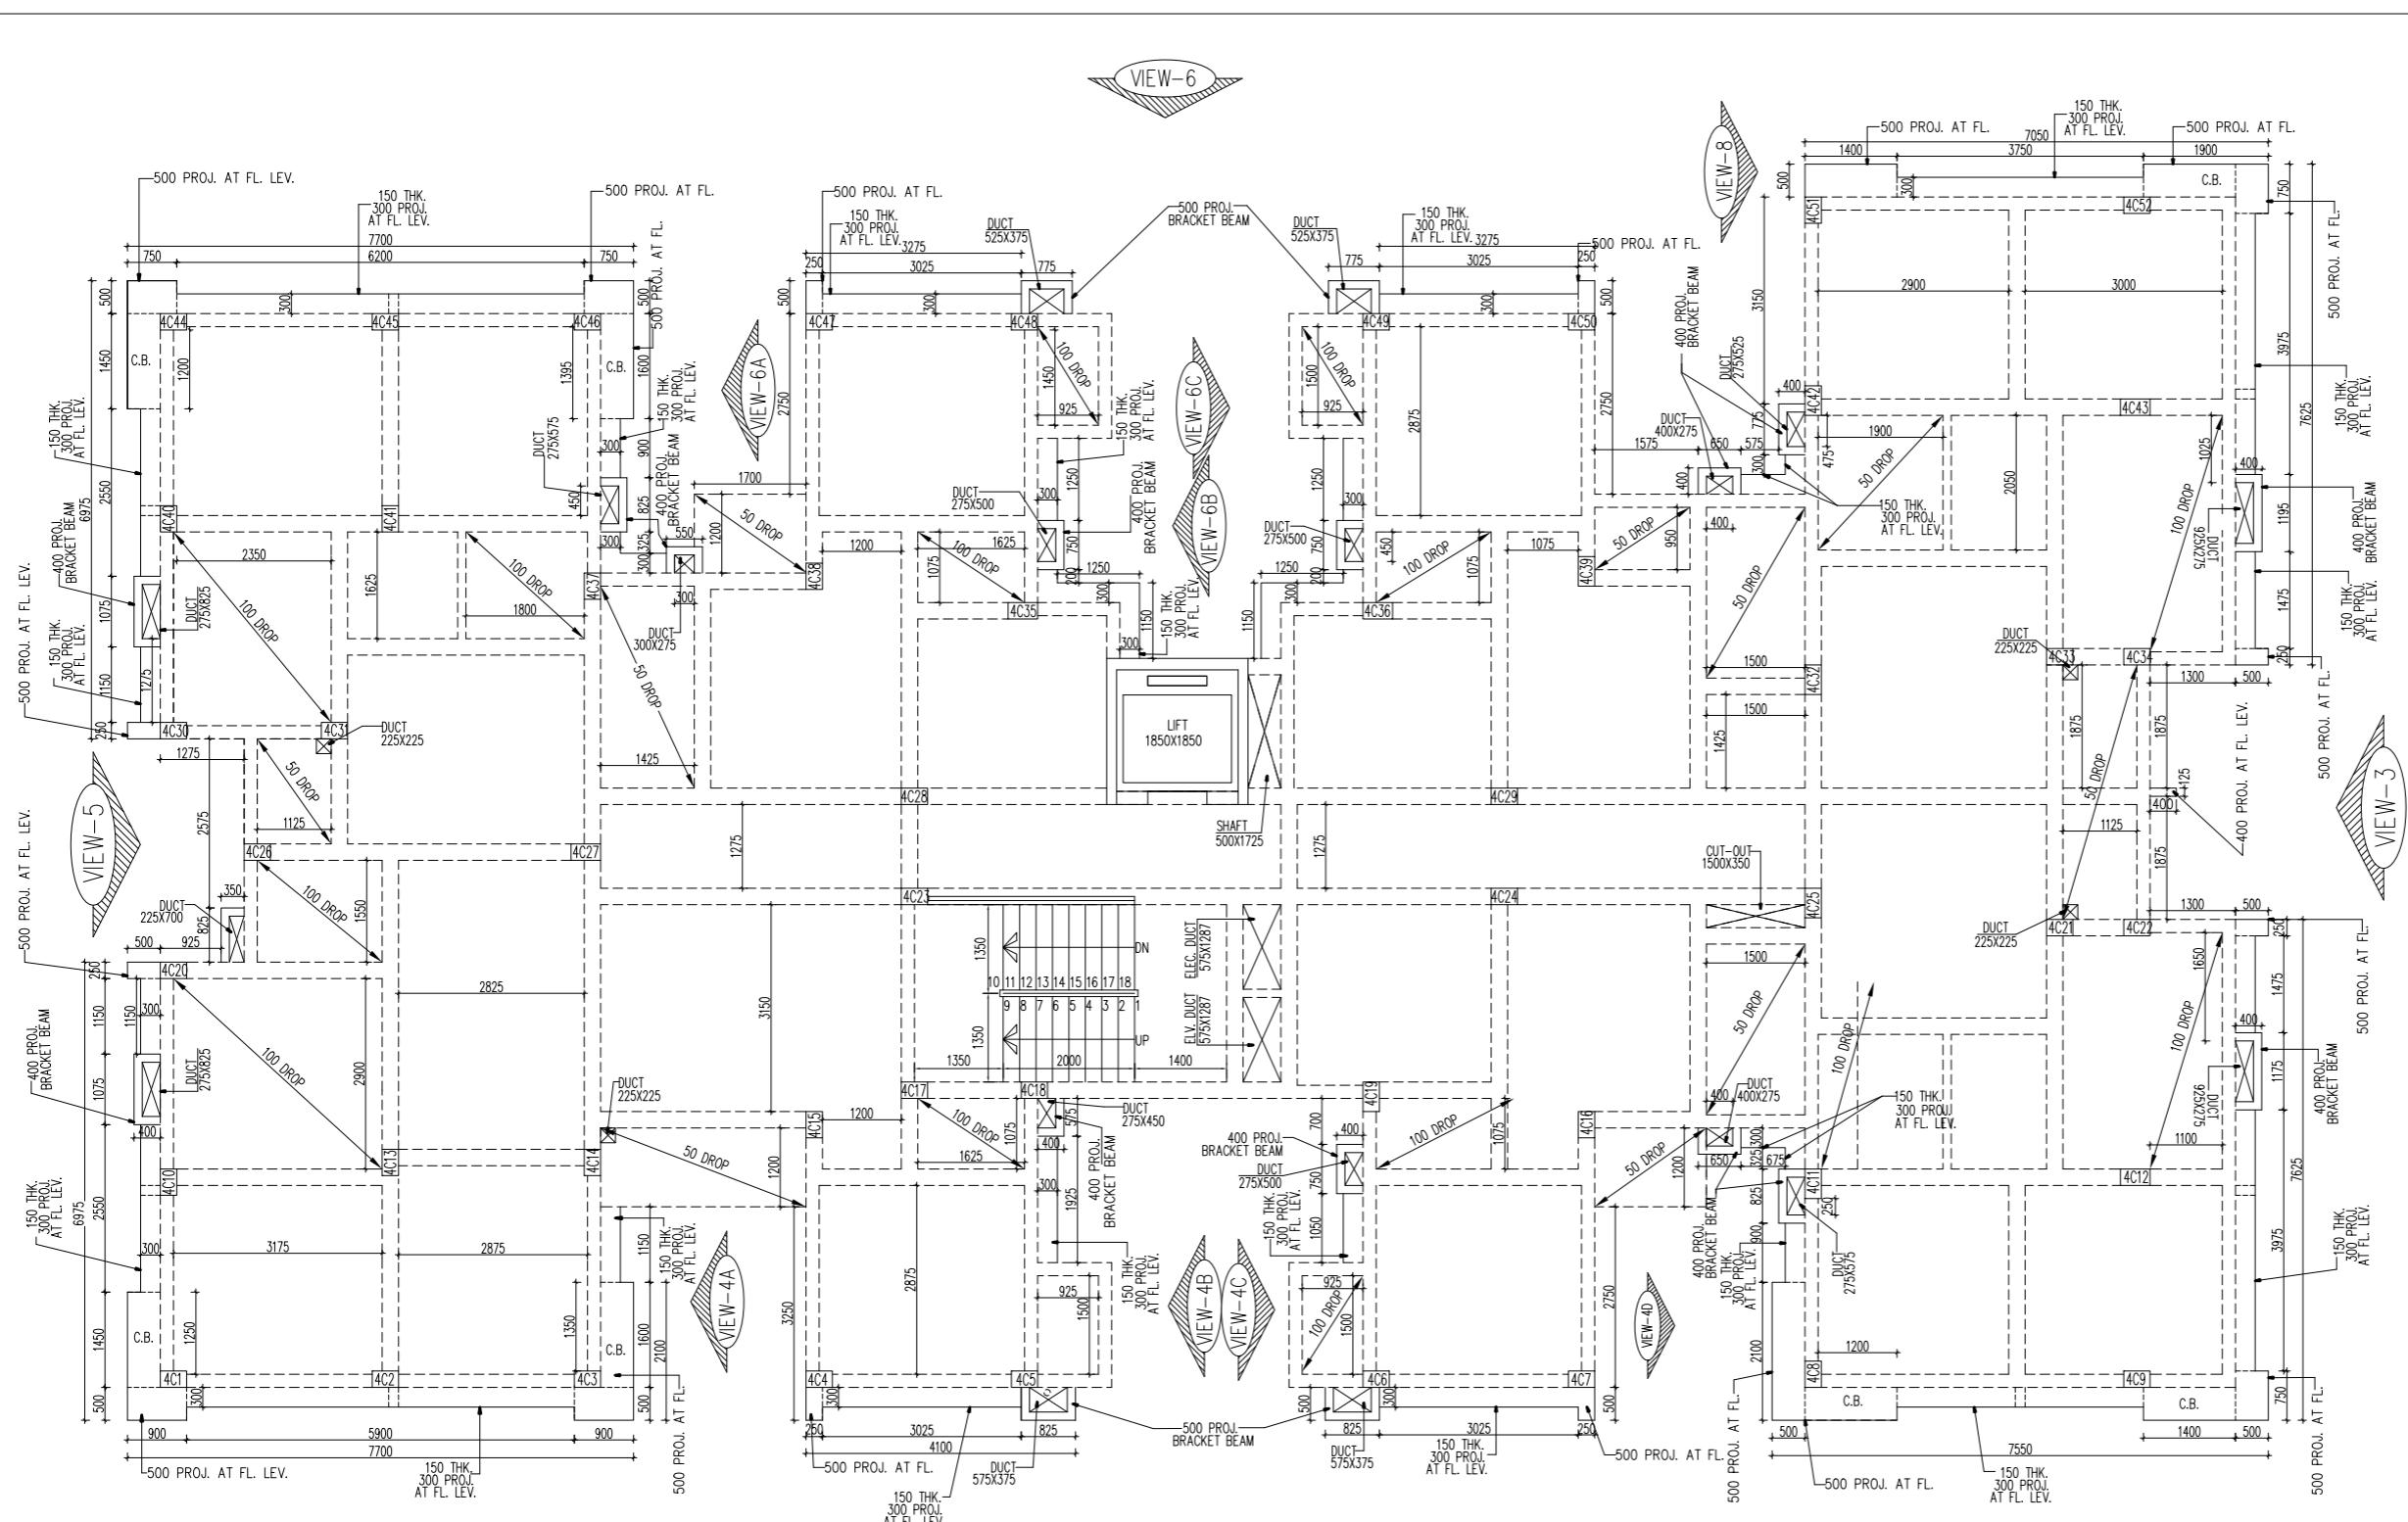

GENERAL NOTES:

- ALL DIMENSIONS ARE IN M.M. UNLESS SPECIFIED.
- WRITTEN MEASUREMENT SHOULD BE FOLLOWED ALWAYS. DRAWINGS SHOULD NOT BE SCALED.
- ALL DIMENSIONS ARE FINISHED DIMENSION
- IN CASE OF ANY DISCREPANCY NOTICED IN THE ARCHITECTURAL WORKING DRAWING FROM CORPORATION DRAWING IMMEDIATELY INFORM THE ARCHITECT, BEFORE PROCEEDING ANY WORK AT THAT PART.
- REFER ONLY THE LATEST REVISED DRAWINGS ; SUPERSEDED DRAWINGS NOT TO BE KEPT IN USE AT SITE
- STRUCTURAL MEMBER SIZES SHALL BE READ FROM STRUCTURAL DRAWINGS, BUT THEIR PLACEMENTS SHOULD BE AS PER ARCHITECTURAL DRAWINGS. IN CASE OF MAJOR DIFFERENCES IN BETWEEN ARCHITECTURAL & STRUCTURAL DRAWINGS IS NOTICED, IMMEDIATELY INFORM THE ARCHITECTS, BEFORE PROCEEDING WITH ANY WORK ON THAT PART

NO.	DATE	DEALT	PARTICULARS	CHECKED
REVISION				

TITLE (BLOCK-4)


1ST FLOOR SHUTTERING PLAN

PROJECT


PROPOSED G+IV STORED HOUSING
COMPLEX AT DUTTAPUKUR.

"OXFORD SQUARE"

SCALE 1: 75	ARCHITECTS
	RAJ AGRAWAL & ASSOCIATES. 8B, ROYD STREET, KOLKATA-16.
DATE 09.06.17	DRG.NO JOB NO. REV.NO. REV.DATE SIMPLY S.MAJI

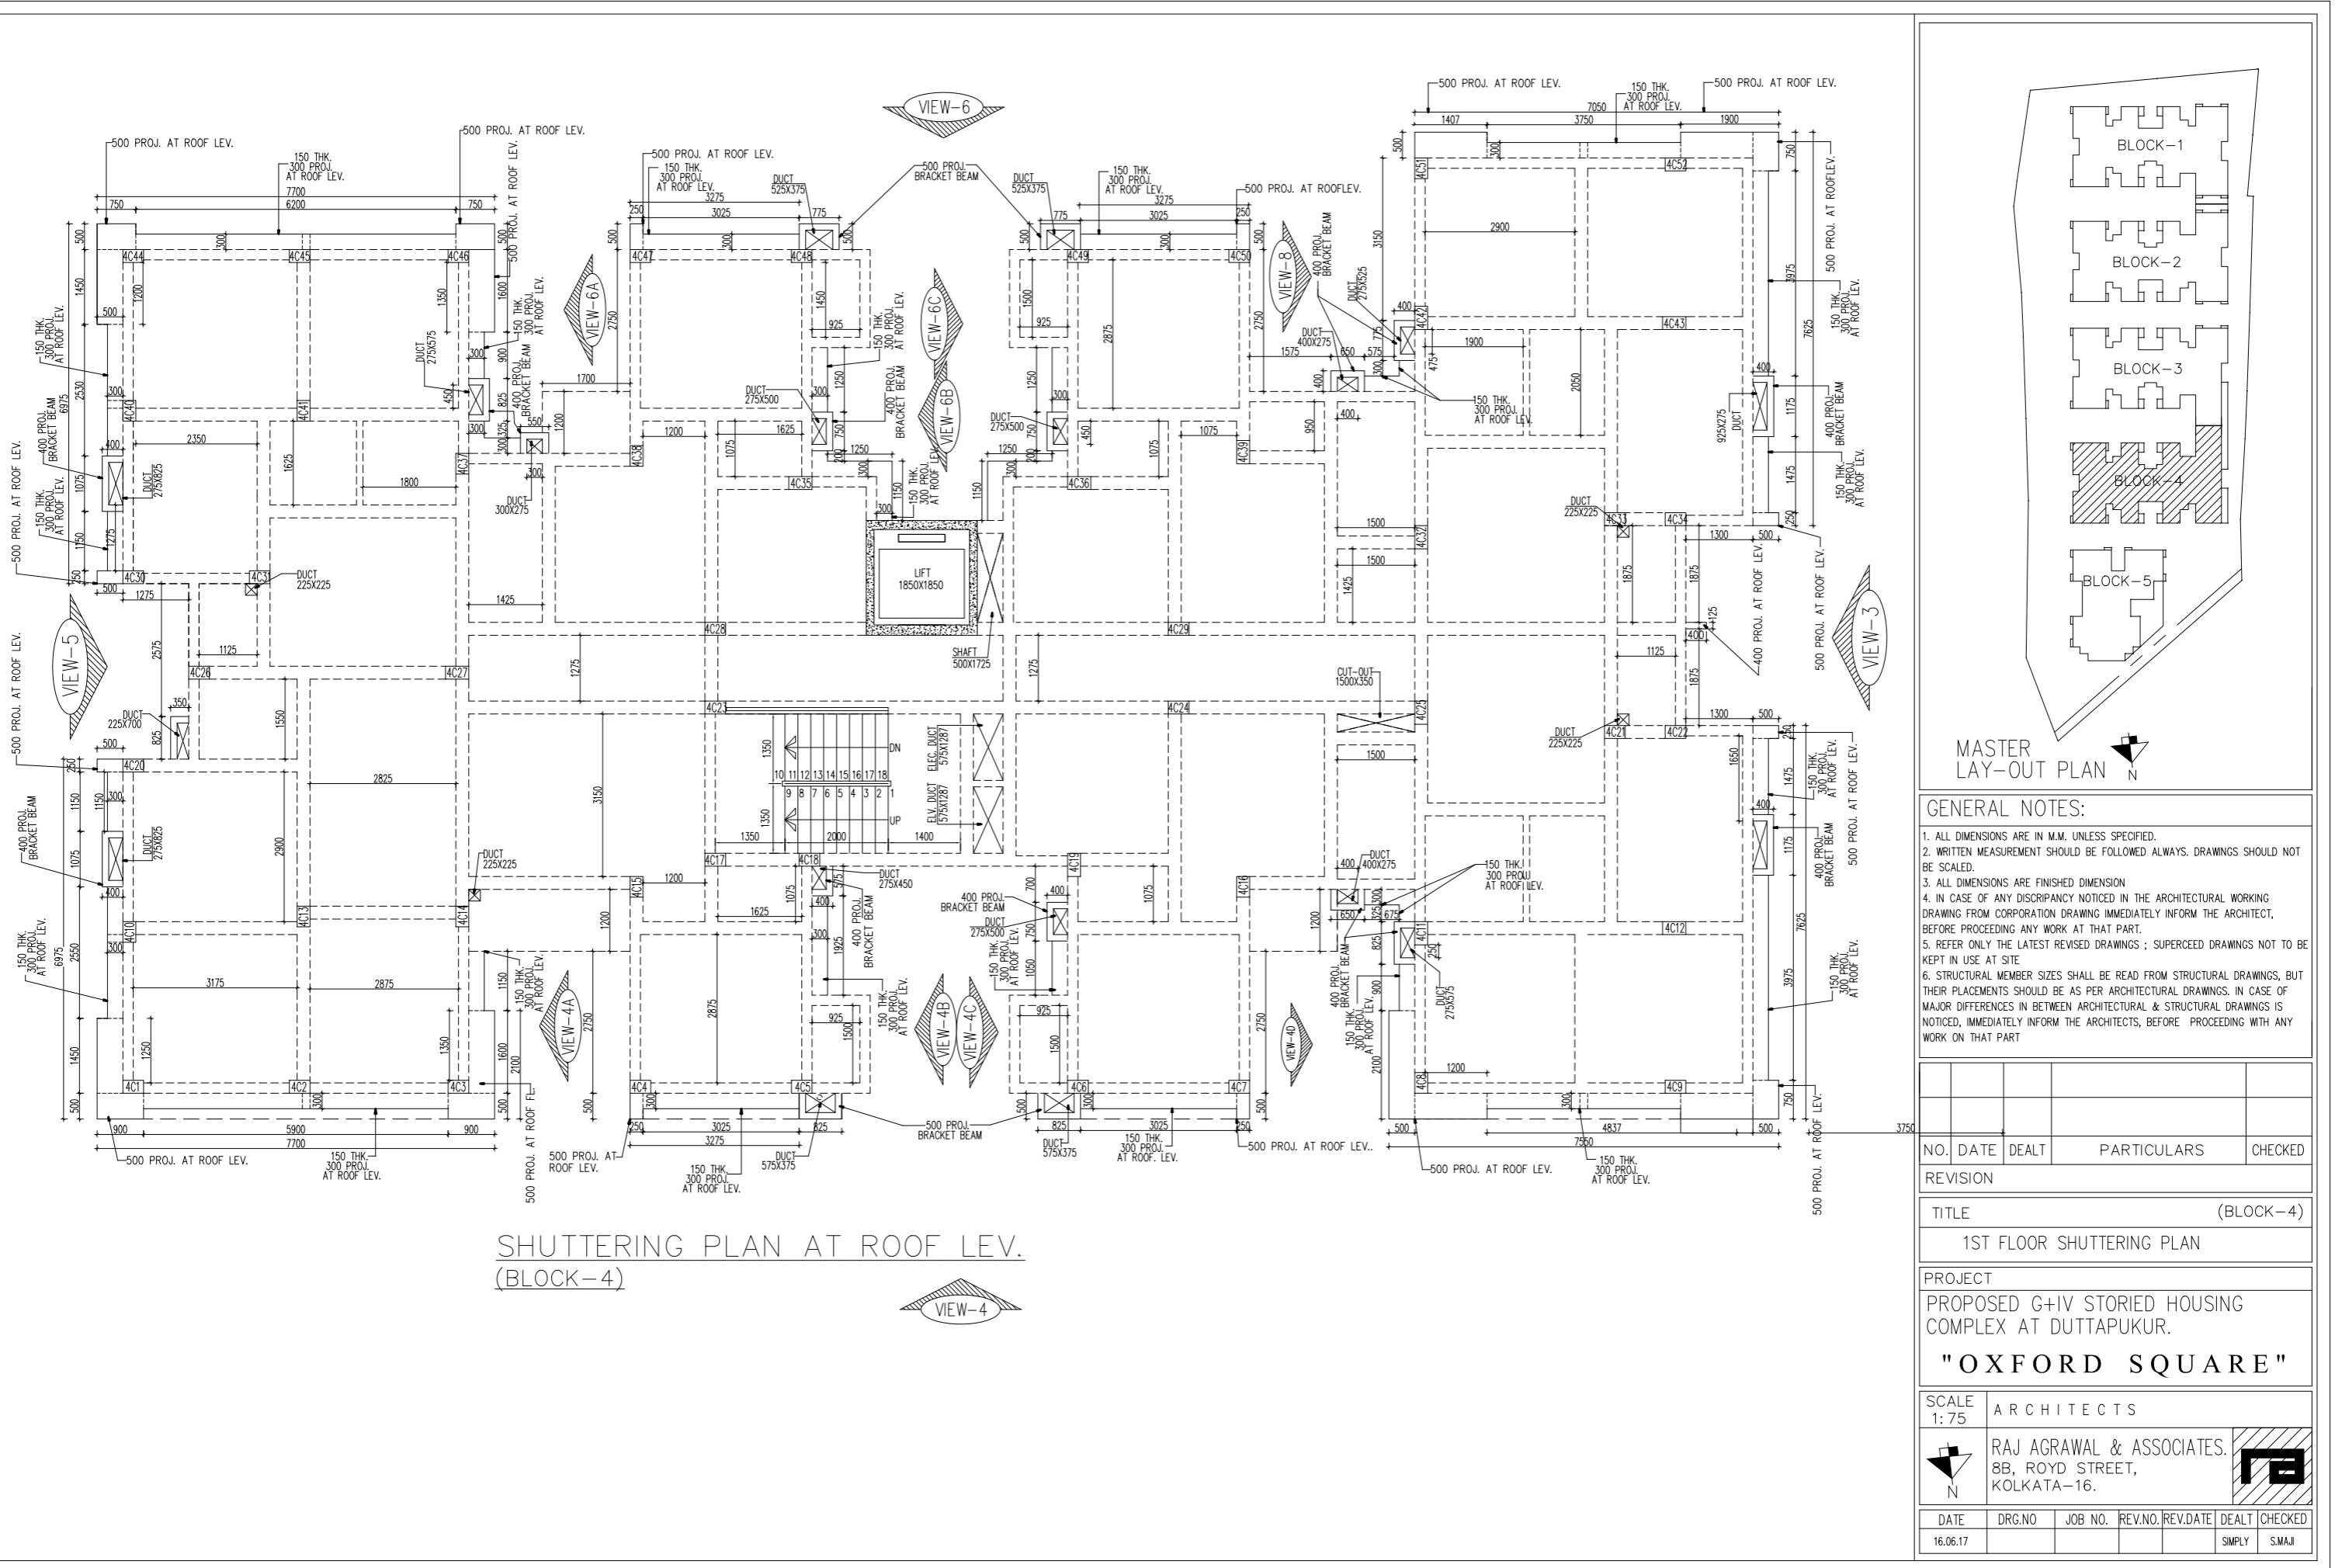

SECOND FLOOR SHUTTERING PLAN

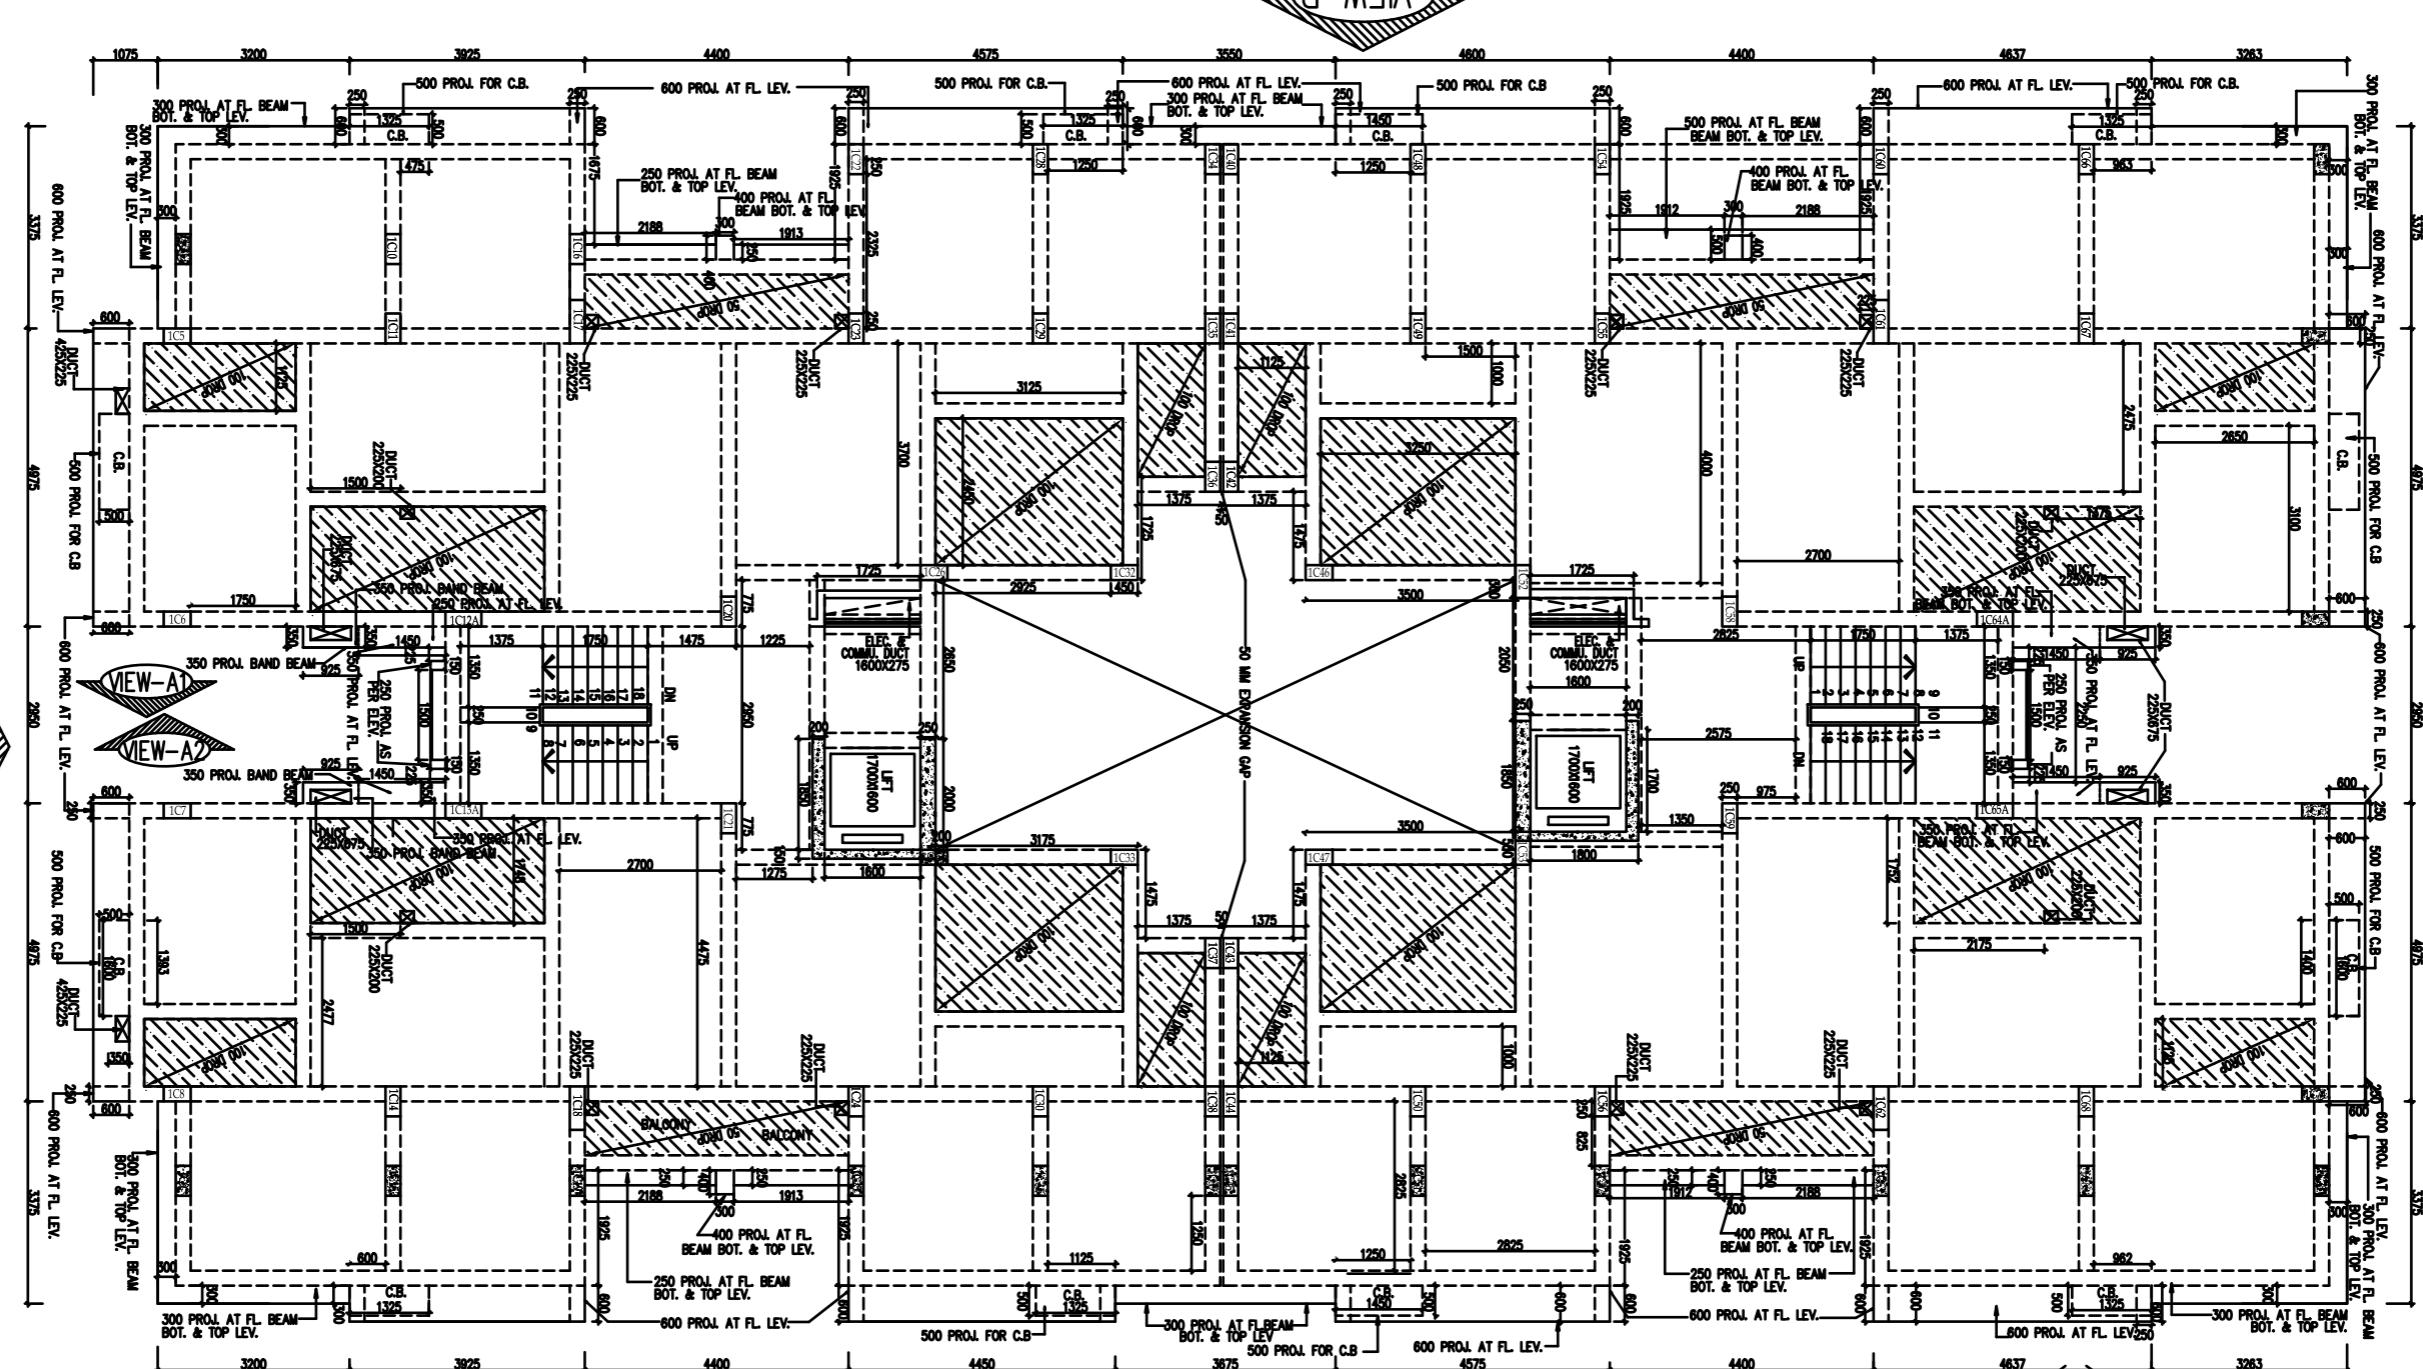

KEY PLAN

N.T.S.

GENERAL NOTES:

1. ALL DIMENSIONS ARE IN MM UNLESS SPECIFIED.

2. WRITTEN MEASUREMENT SHOULD BE FOLLOWED ALWAYS. DRAWINGS SHOULD NOT BE SCALED.


3. ALL DIMENSIONS ARE FINISHED DIMENSION.

4. IN CASE OF ANY DISCREPANCY NOTICED IN THE ARCHITECTURAL WORKING DRAWING FROM CORPORATION DRAWING IMMEDIATELY INFORM THE ARCHITECT BEFORE PROCEEDING ANY WORK AT THAT PART.


5. REFER ONLY THE LATEST REvised DRAWINGS ; SUPERSEDED DRAWINGS NOT TO BE KEPT IN USE AT SITE.

6. STRUCTURAL MEMBER SIZES SHALL BE READ FROM STRUCTURAL DRAWINGS, BUT THEIR PLACEMENTS SHOULD AS PER ARCHITECTURAL DRAWINGS. IN CASE OF MAJOR DIFFERENCES IN BETWEEN ARCHITECTURAL & STRUCTURAL DRAWINGS IS NOTICED IMMEDIATELY INFORM THE ARCHITECTS, BEFORE PROCEEDING WITH ANY WORK ON THAT PART.

7. ALL PROJECTION SHOULD BE FOLLOWED THIS DRAWS. NO. [AR-12 (B-3)] & AR-13 (B-3)]

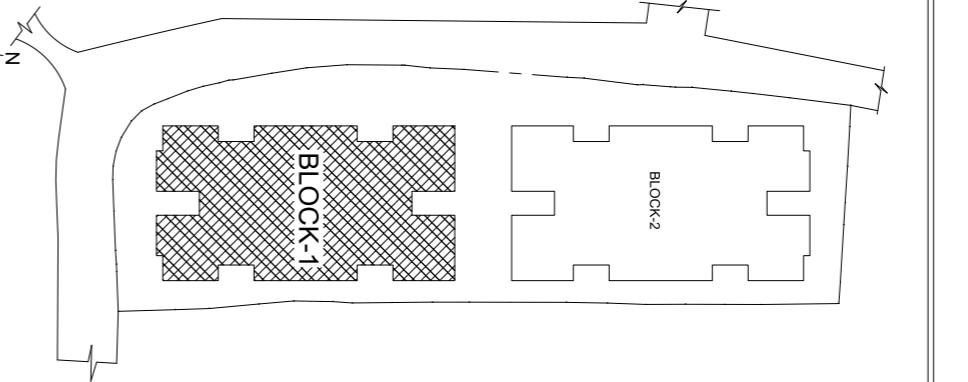

SCALE	1:75	ARCHITECTS	N RAVI AGRAWAL & ASSOCIATES	
			8B, ROYD STREET, KOKATA-16.	
DATE	04/07/17	DRG. NO.	REVNO/REDATE	DEALT CHECKED
				SIMPLY S.M.A.J

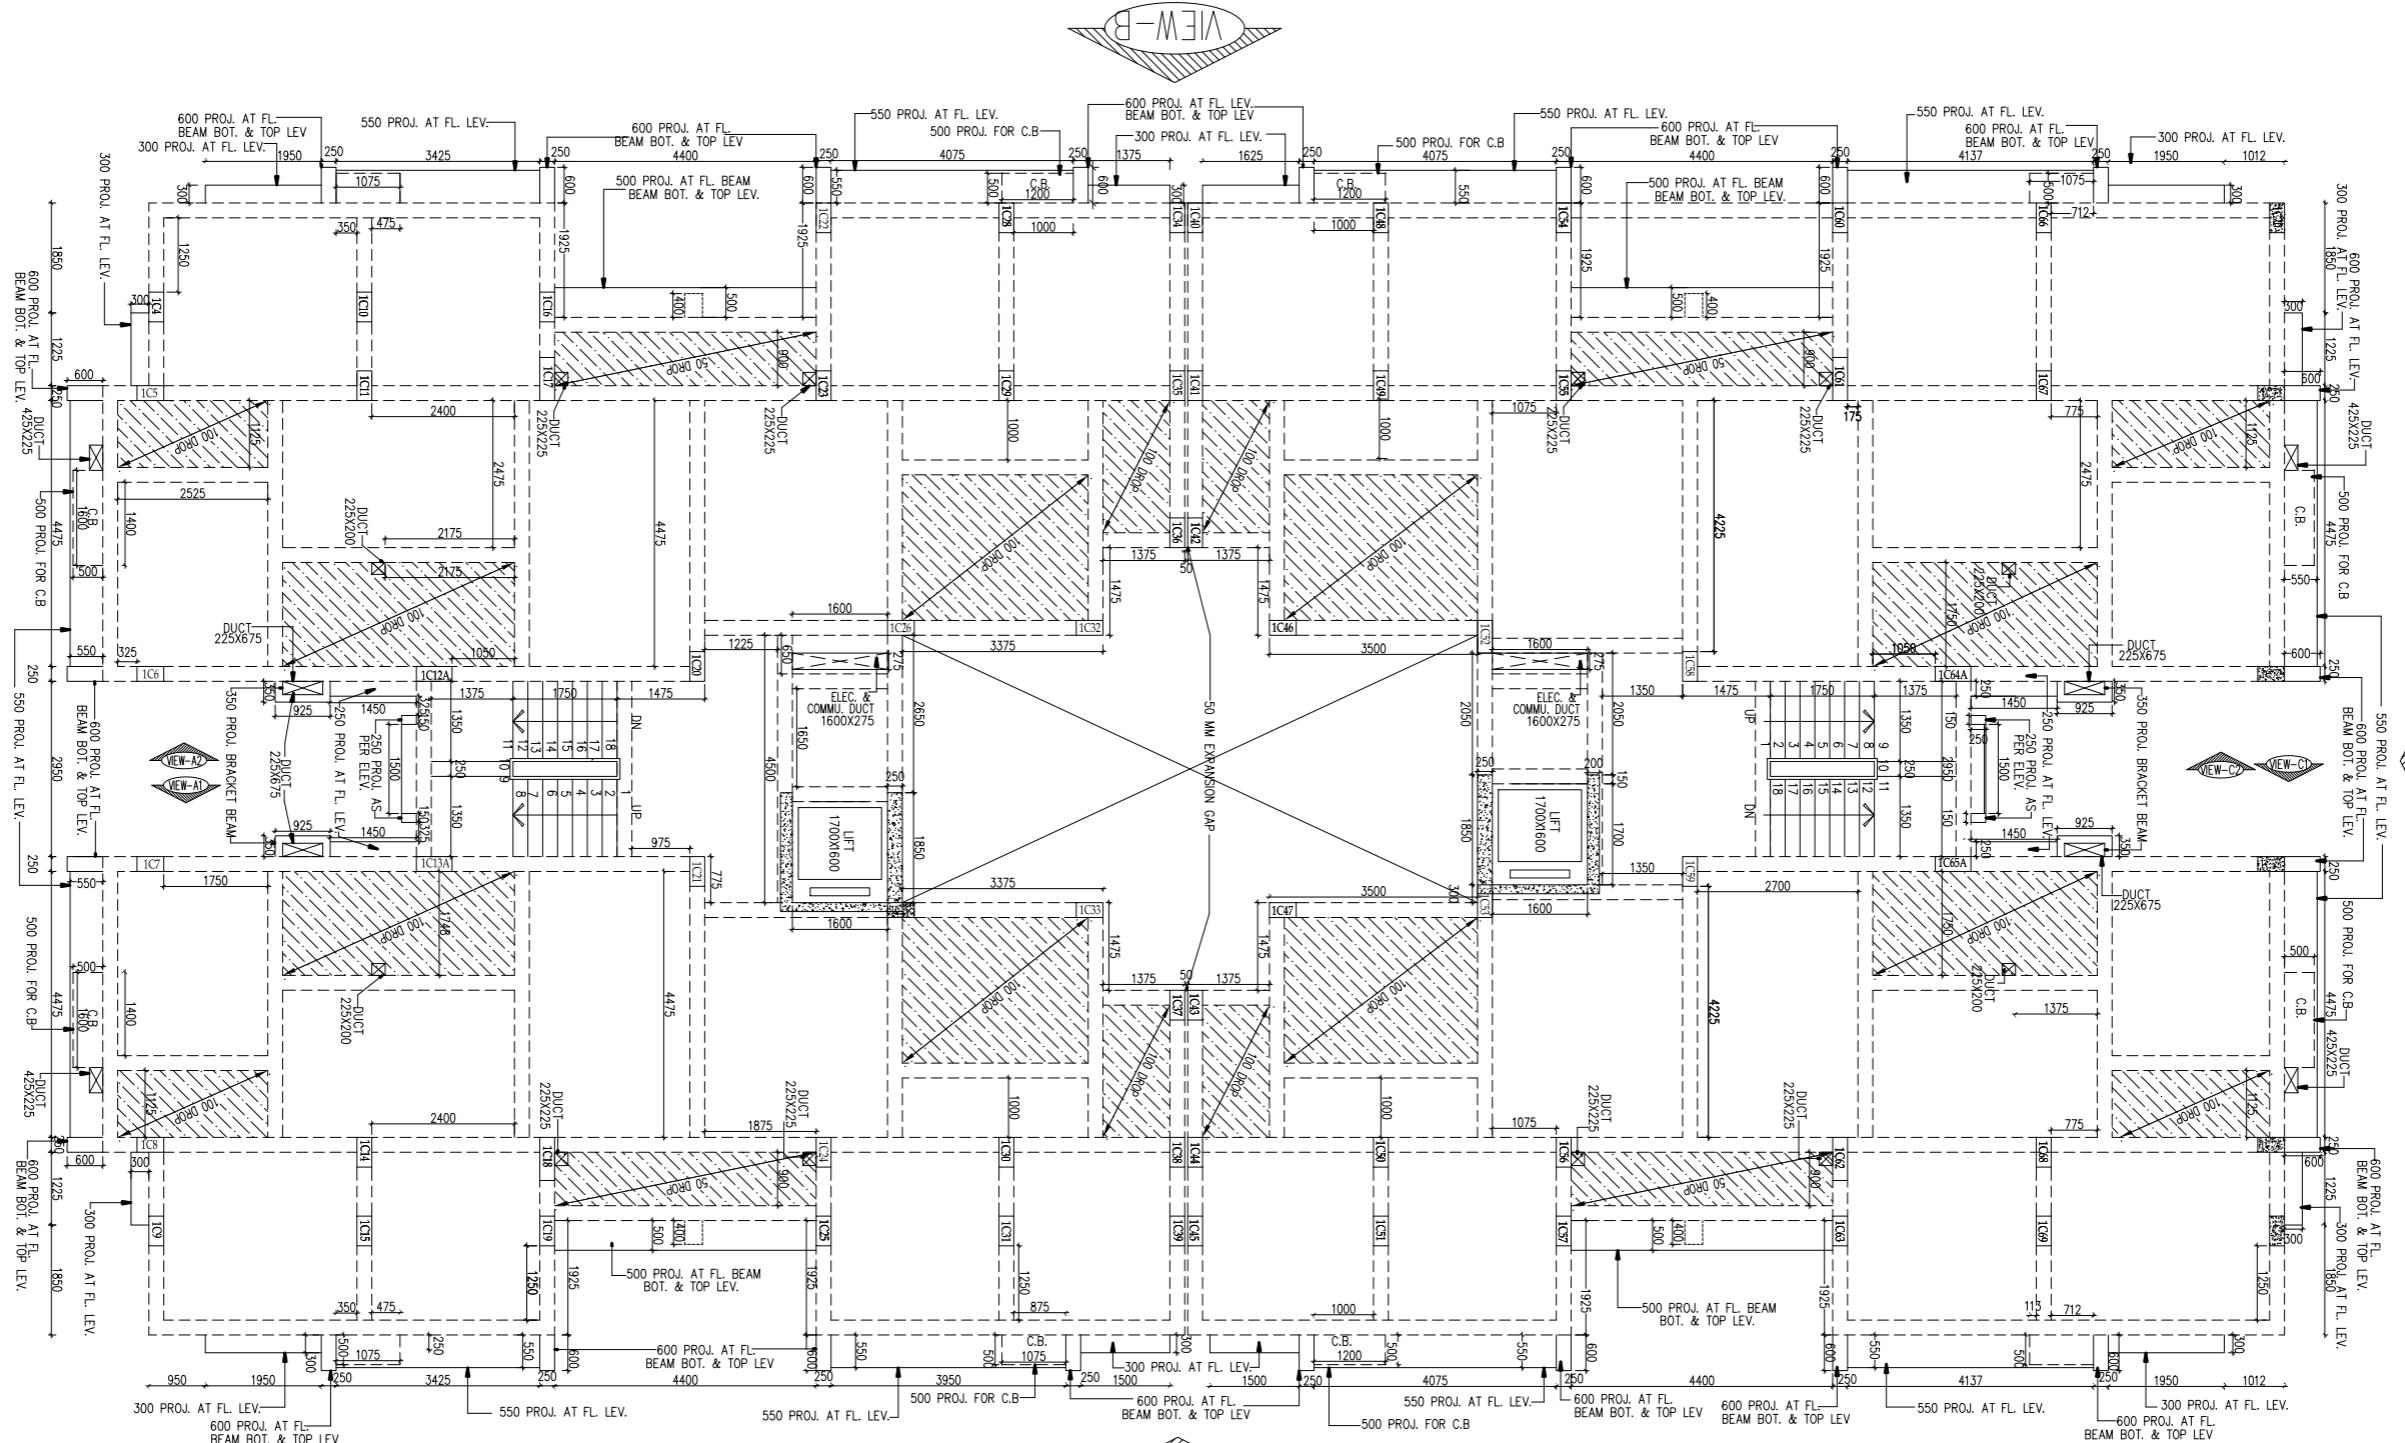

**KEY PLAN
N.L.S.**

GENERAL NOTES:

1. ALL DIMENSIONS ARE IN MM UNLESS SPECIFIED.
2. WRITTEN MEASUREMENT SHOULD BE FOLLOWED ALWAYS. DRAWINGS SHOULD NOT BE SCALED.


3. ALL DIMENSIONS ARE FINISHED DIMENSION IN THE ARCHITECTURAL WORKING DRAWING FROM CORROBORATION IMMEDIATELY INFORM THE ARCHITECT.

4. IN CASE OF ANY DISCREPANCY NOTICED IN THE ARCHITECTURAL WORKING DRAWING FROM CORROBORATION IMMEDIATELY INFORM THE ARCHITECT.

5. REFER ONLY THE LATEST REVISED DRAWINGS : SUPERSEDED DRAWINGS NOT TO BE KEPT IN USE AT SITE.


6. STRUCTURAL MEMBER SIZES SHALL BE READ FROM STRUCTURAL DRAWINGS BUT THEIR PLACEMENTS SHOULD BE AS PER ARCHITECTURAL DRAWINGS. IN CASE OF MAJOR DIFFERENCES IN BETWEEN ARCHITECTURAL & STRUCTURAL DRAWINGS IS NOTICED, IMMEDIATELY INFORM THE ARCHITECTS, BEFORE PROCEEDING WITH ANY WORK ON THAT PART.

7. ALL PRODUCTION SHOULD BE FOLLOWED THIS DRAWING NO. [AR-12 (B-3)] & AR-13 (B-3).

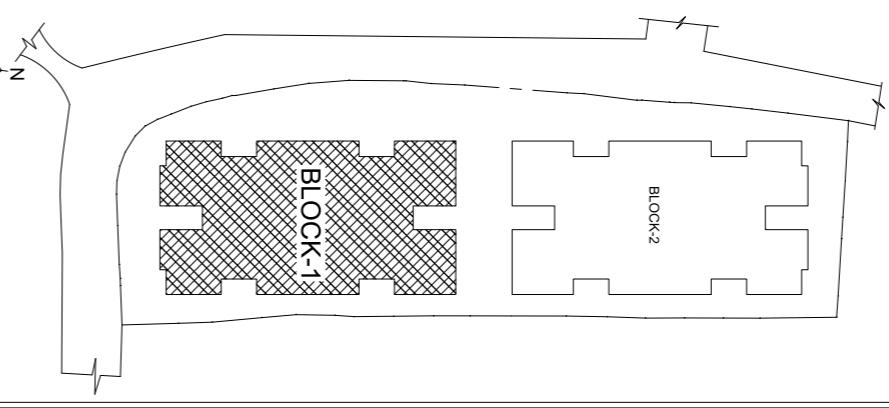



SCALE	A R C H I T E C T S
1:75	
N	RAJ AGRAWAL & ASSOCIATES
	8B, ROYD STREET,
	KOLKATA-16.
DATE	DRGNO
04/07/17	JOB NO.
	REV NO.
	REVDATE
	DEALT CHECKED
	SIMPLY SWAP

THIRD FLOOR SHUTTERING PLAN
(BLOCK-1)

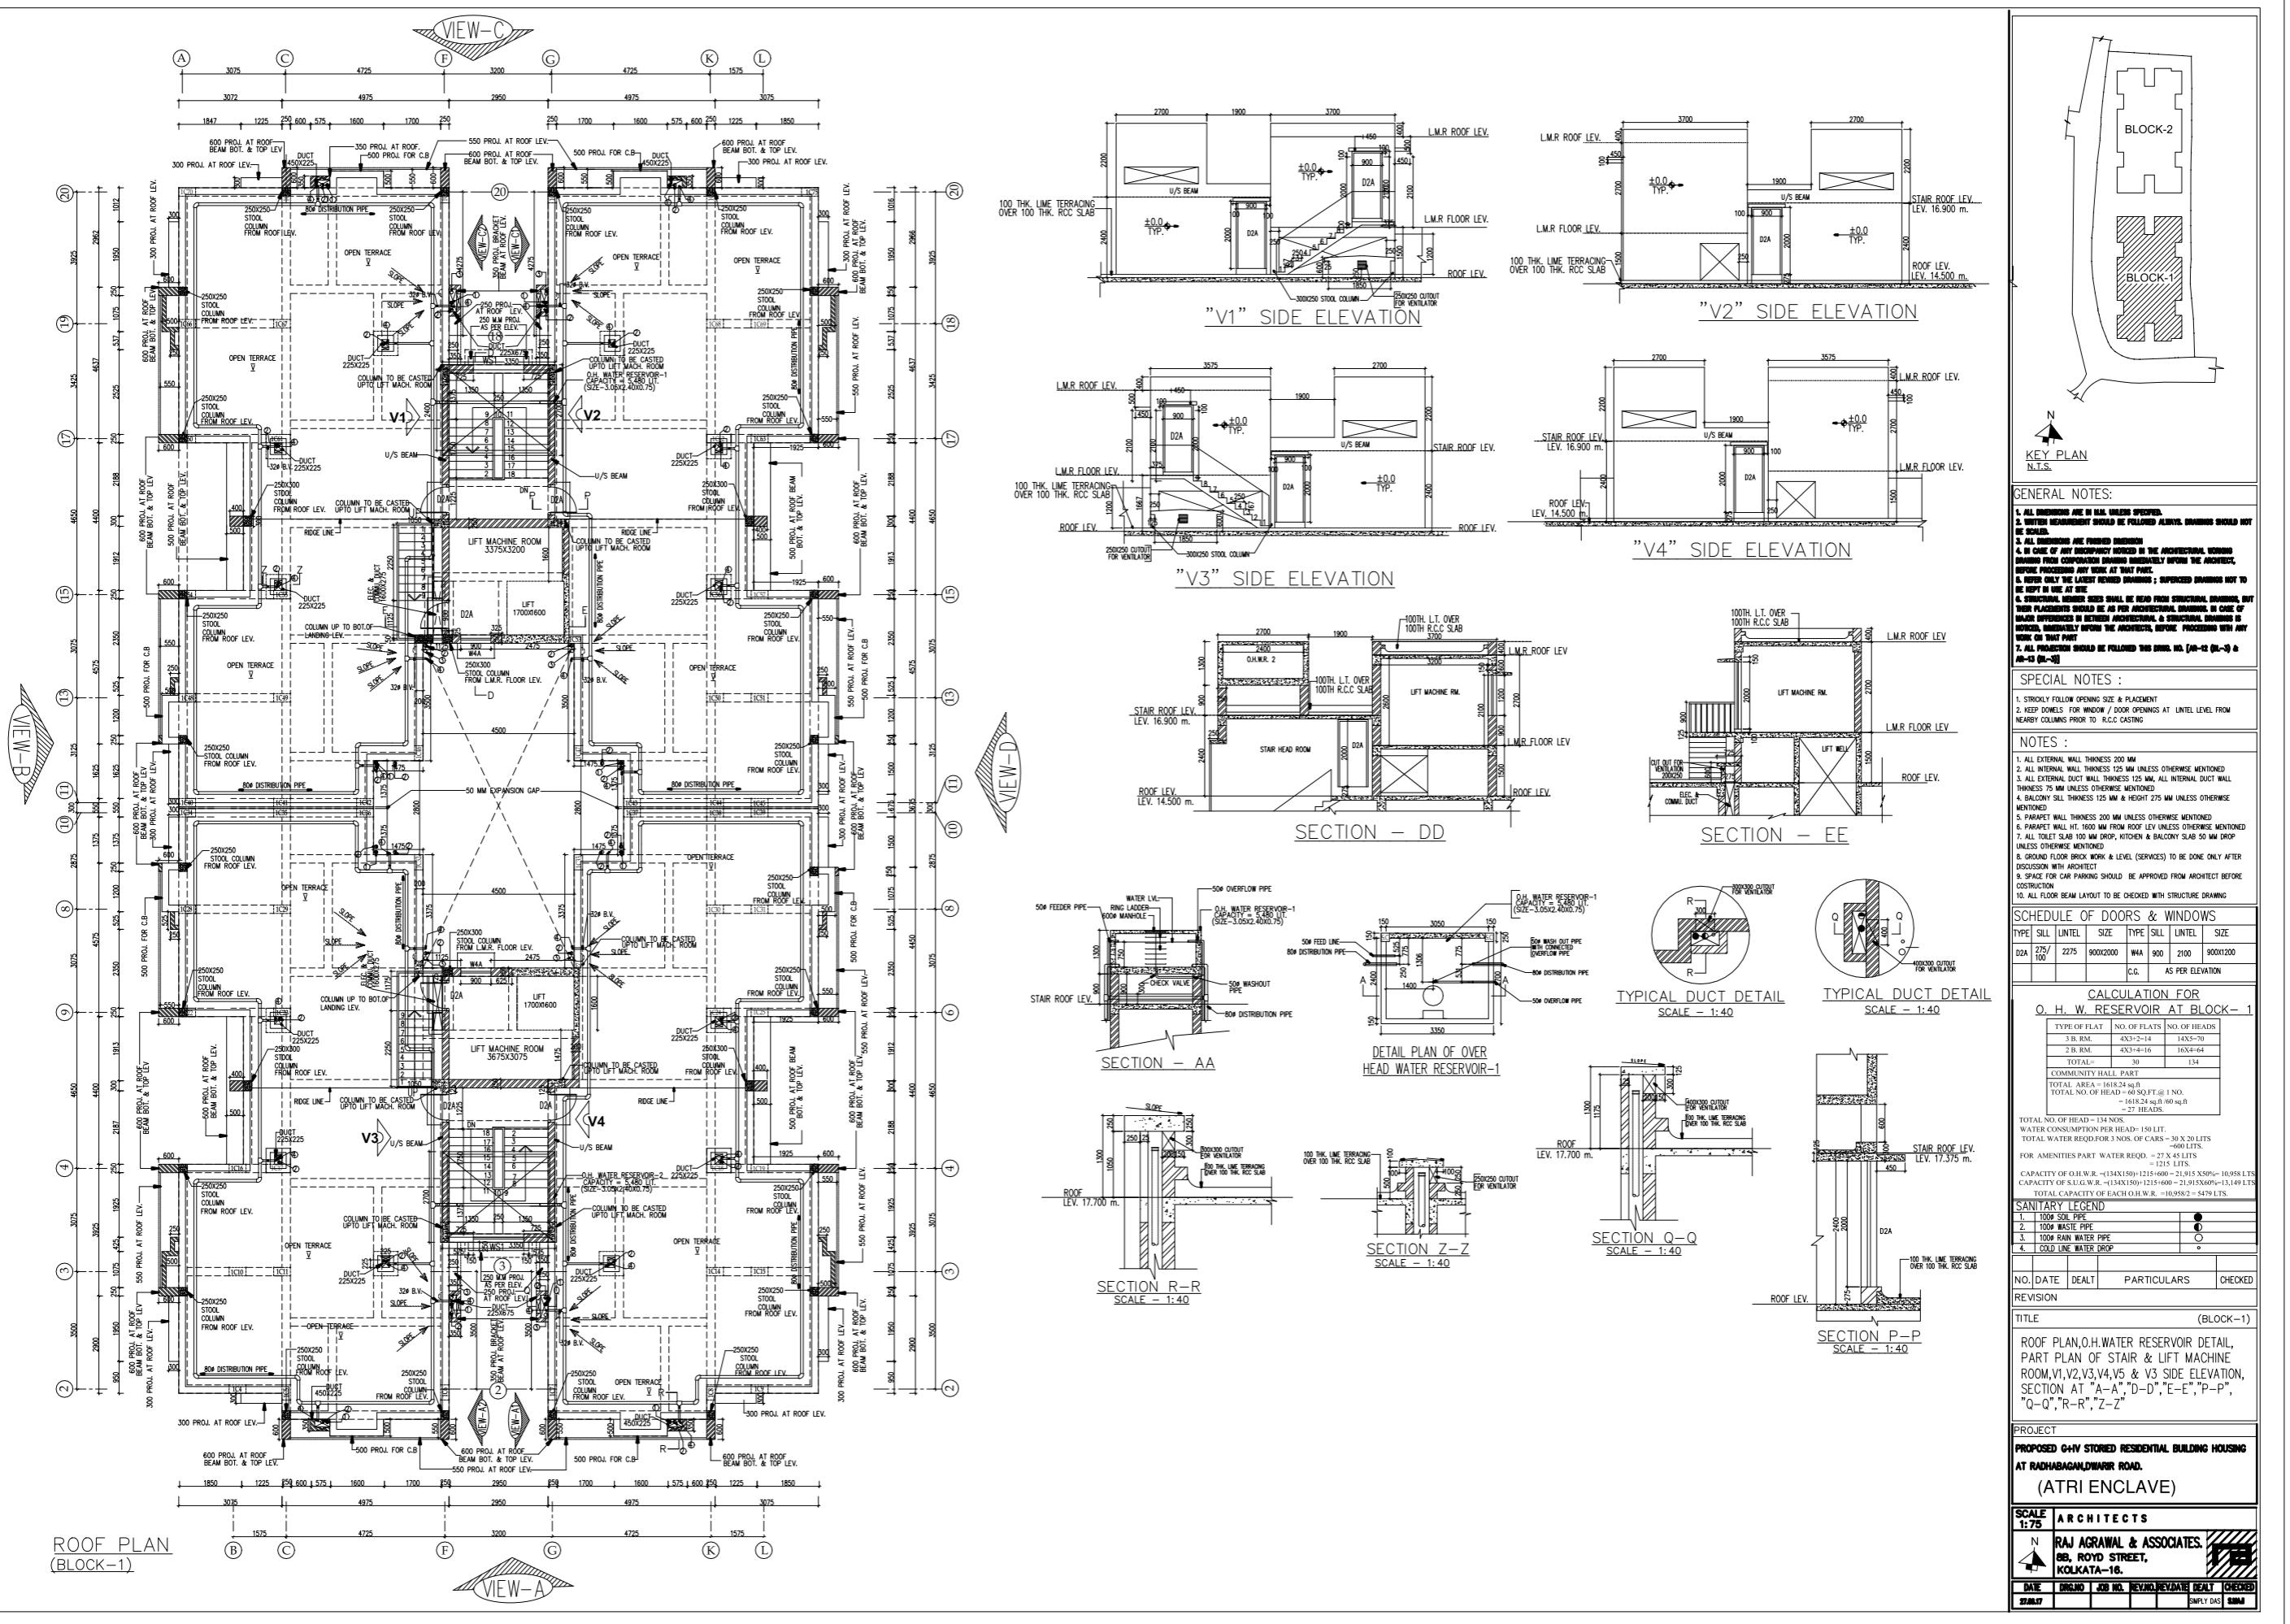

ROOF SHUTTERING PLAN

(BLOCK-1)

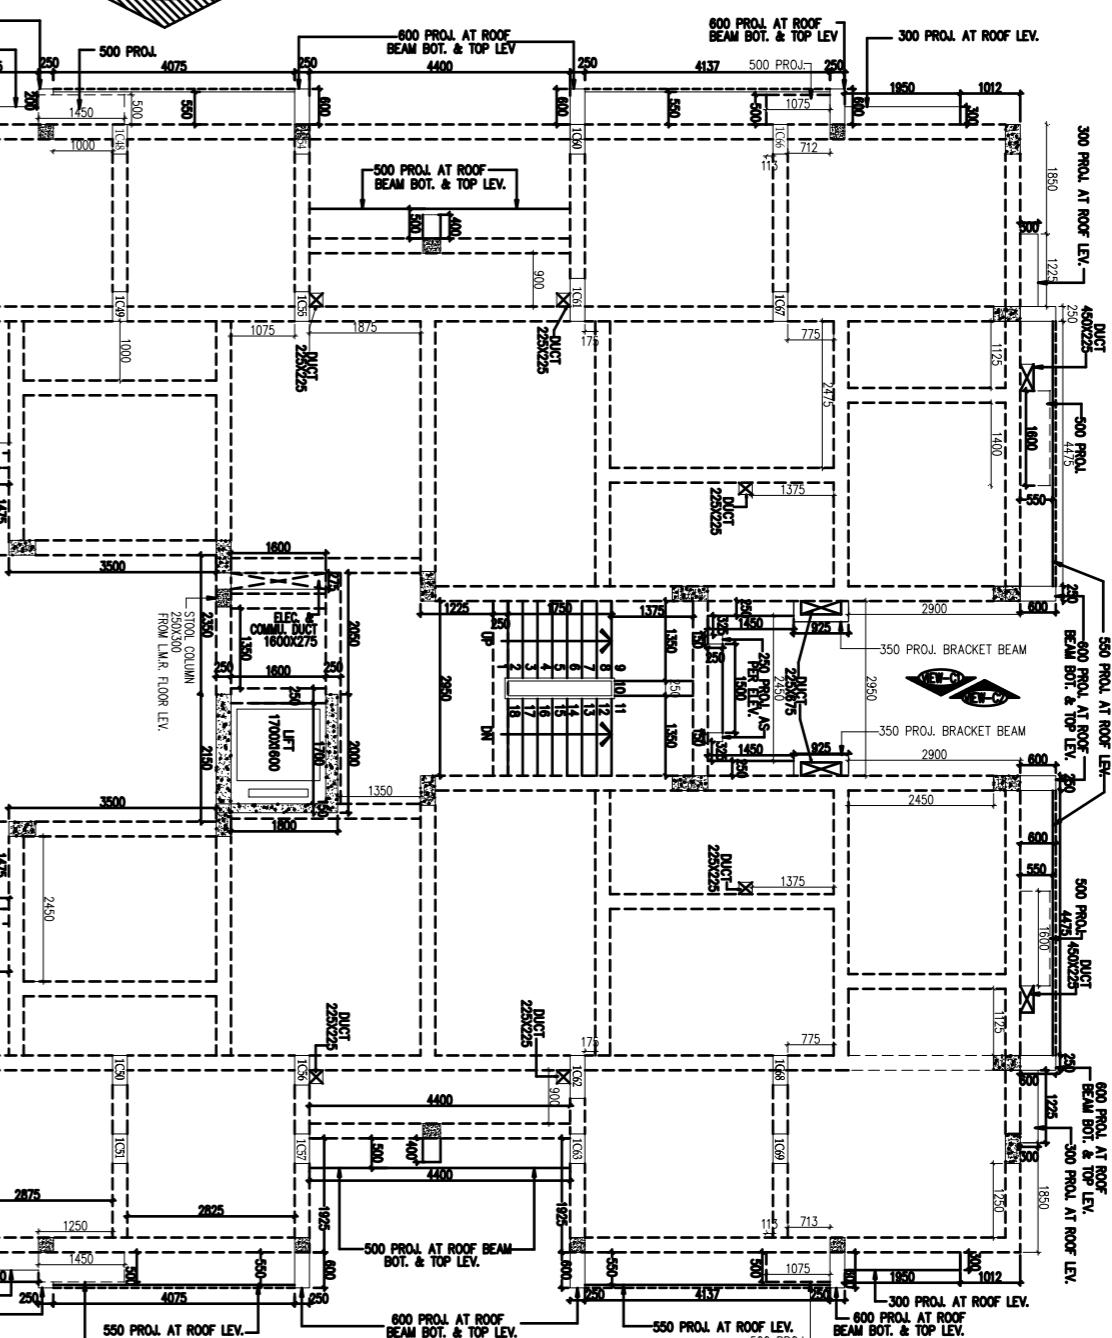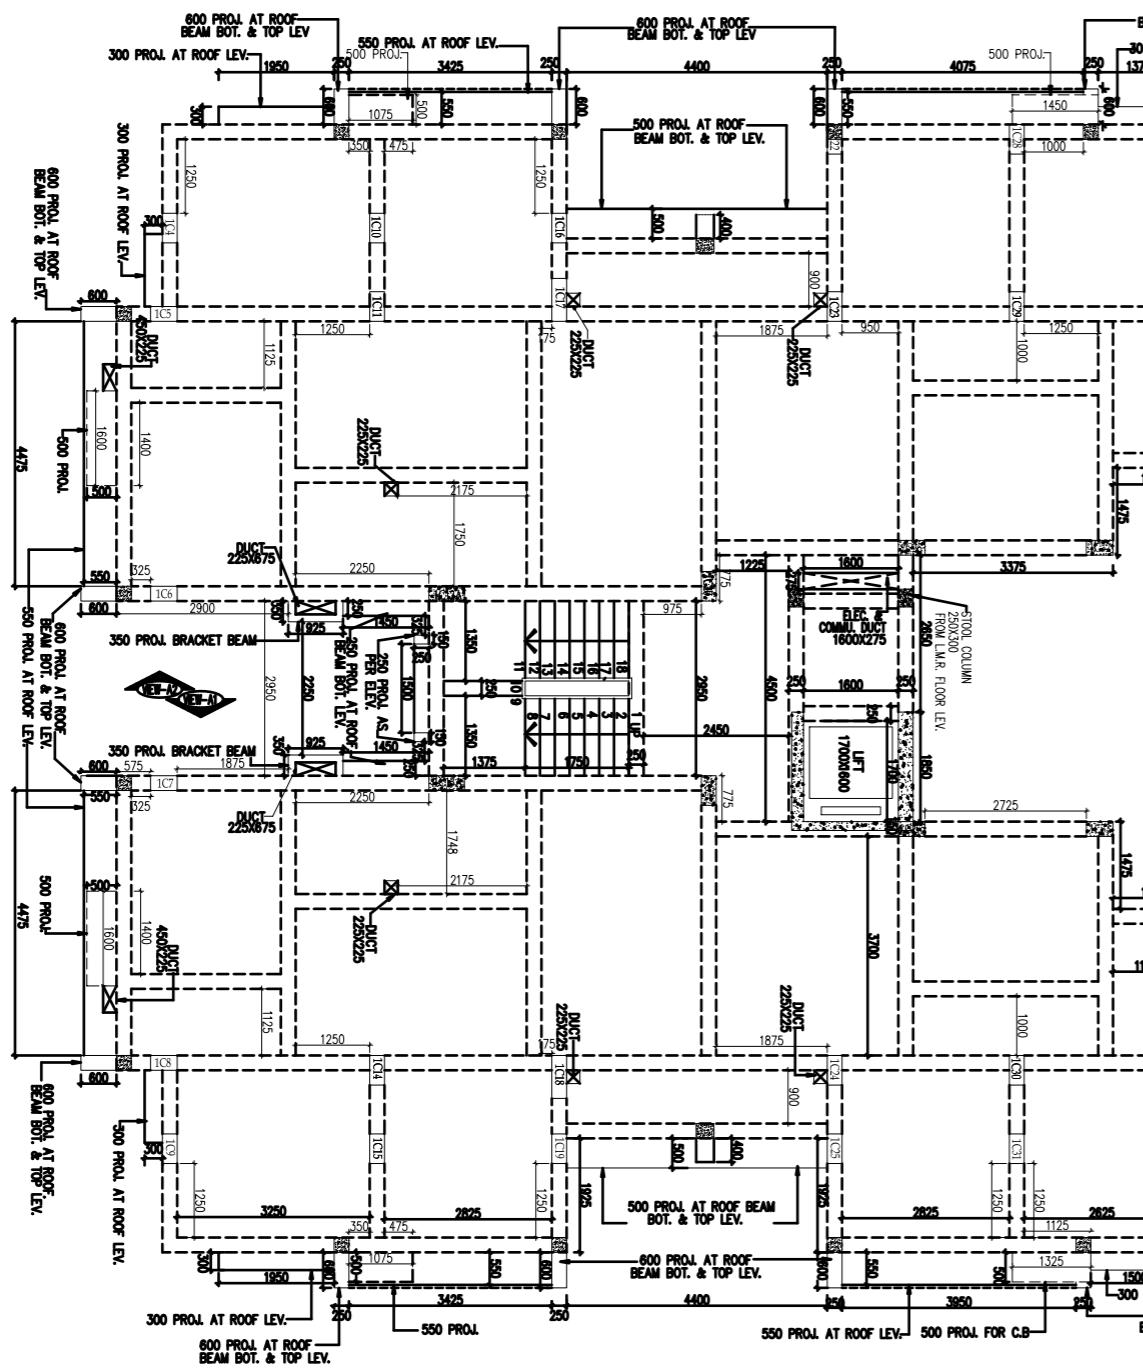


600 PROL AT ROOF LEV.
500 PROL AT ROOF LEV.
550 PROL AT ROOF LEV.
300 PROL AT ROOF LEV.



**KEY PLAN
N.T.S.**

GENERAL NOTES:


- ALL DIMENSIONS ARE IN MM. UNLESS SPECIFIED.
- WRITTEN MEASUREMENT SHOULD BE FOLLOWED. ALWAYS. DRAWINGS SHOULD NOT BE SCALED.
- ALL DIMENSIONS ARE FINISHED DIMENSION.
- IN CASE OF ANY DISCREPANCY NOTED IN THE ARCHITECTURAL WORKING DRAWINGS FROM CORPORATION DRAWING IMMEDIATELY INFORM THE ARCHITECT, BEFORE PROCEEDING ANY WORK AT THAT PART.
- KEEP ONLY THE LATEST RELEASED DRAWINGS ; SUPERSEDED DRAWINGS NOT TO BE KEPT IN USE AT SITE.
- STRUCTURAL MEMBER SIZES SHALL BE READ FROM STRUCTURAL DRAWINGS. BUT THEIR PLACEMENTS SHOULD BE AS PER ARCHITECTURAL & STRUCTURAL DRAWINGS. IF MAJOR DIFFERENCES IN BETWEEN ARCHITECTURAL & STRUCTURAL DRAWINGS IS NOTED, IMMEDIATELY INFORM THE ARCHITECTS, BEFORE PROCEEDING WITH ANY WORK ON THAT PART.
- ALL PROJECTION SHOULD BE FOLLOWED. THIS DRAWING NO. [AR-12 (BL-3)] & AR-13 (BL-3)]

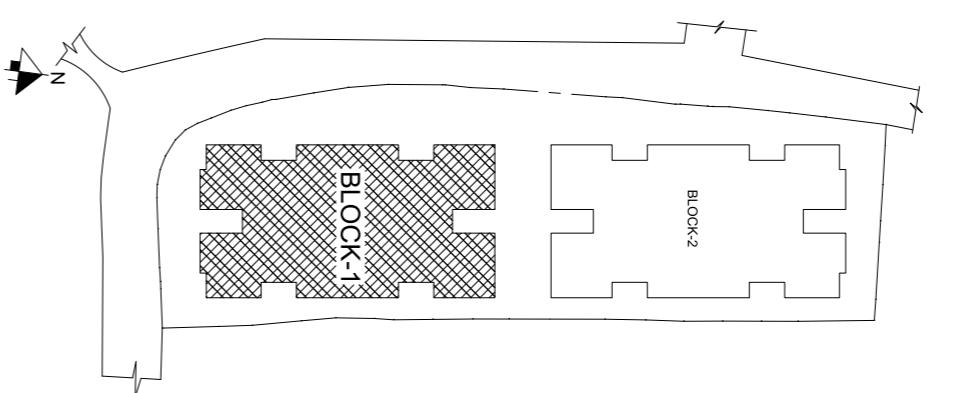

ROOF FLOOR SHUTTERING PLAN




(BLOCK-1)

SCALE	1:75
ARCHITECTS	RAN AGRAWAL & ASSOCIATES,
	8B, ROYD STREET,
	KOLKATA-16.
DATE	04/07/17
REG. NO.	
JOB NO.	
REV NO./REV DATE	
DEALT CHECKED	SIMPLY SMAJ

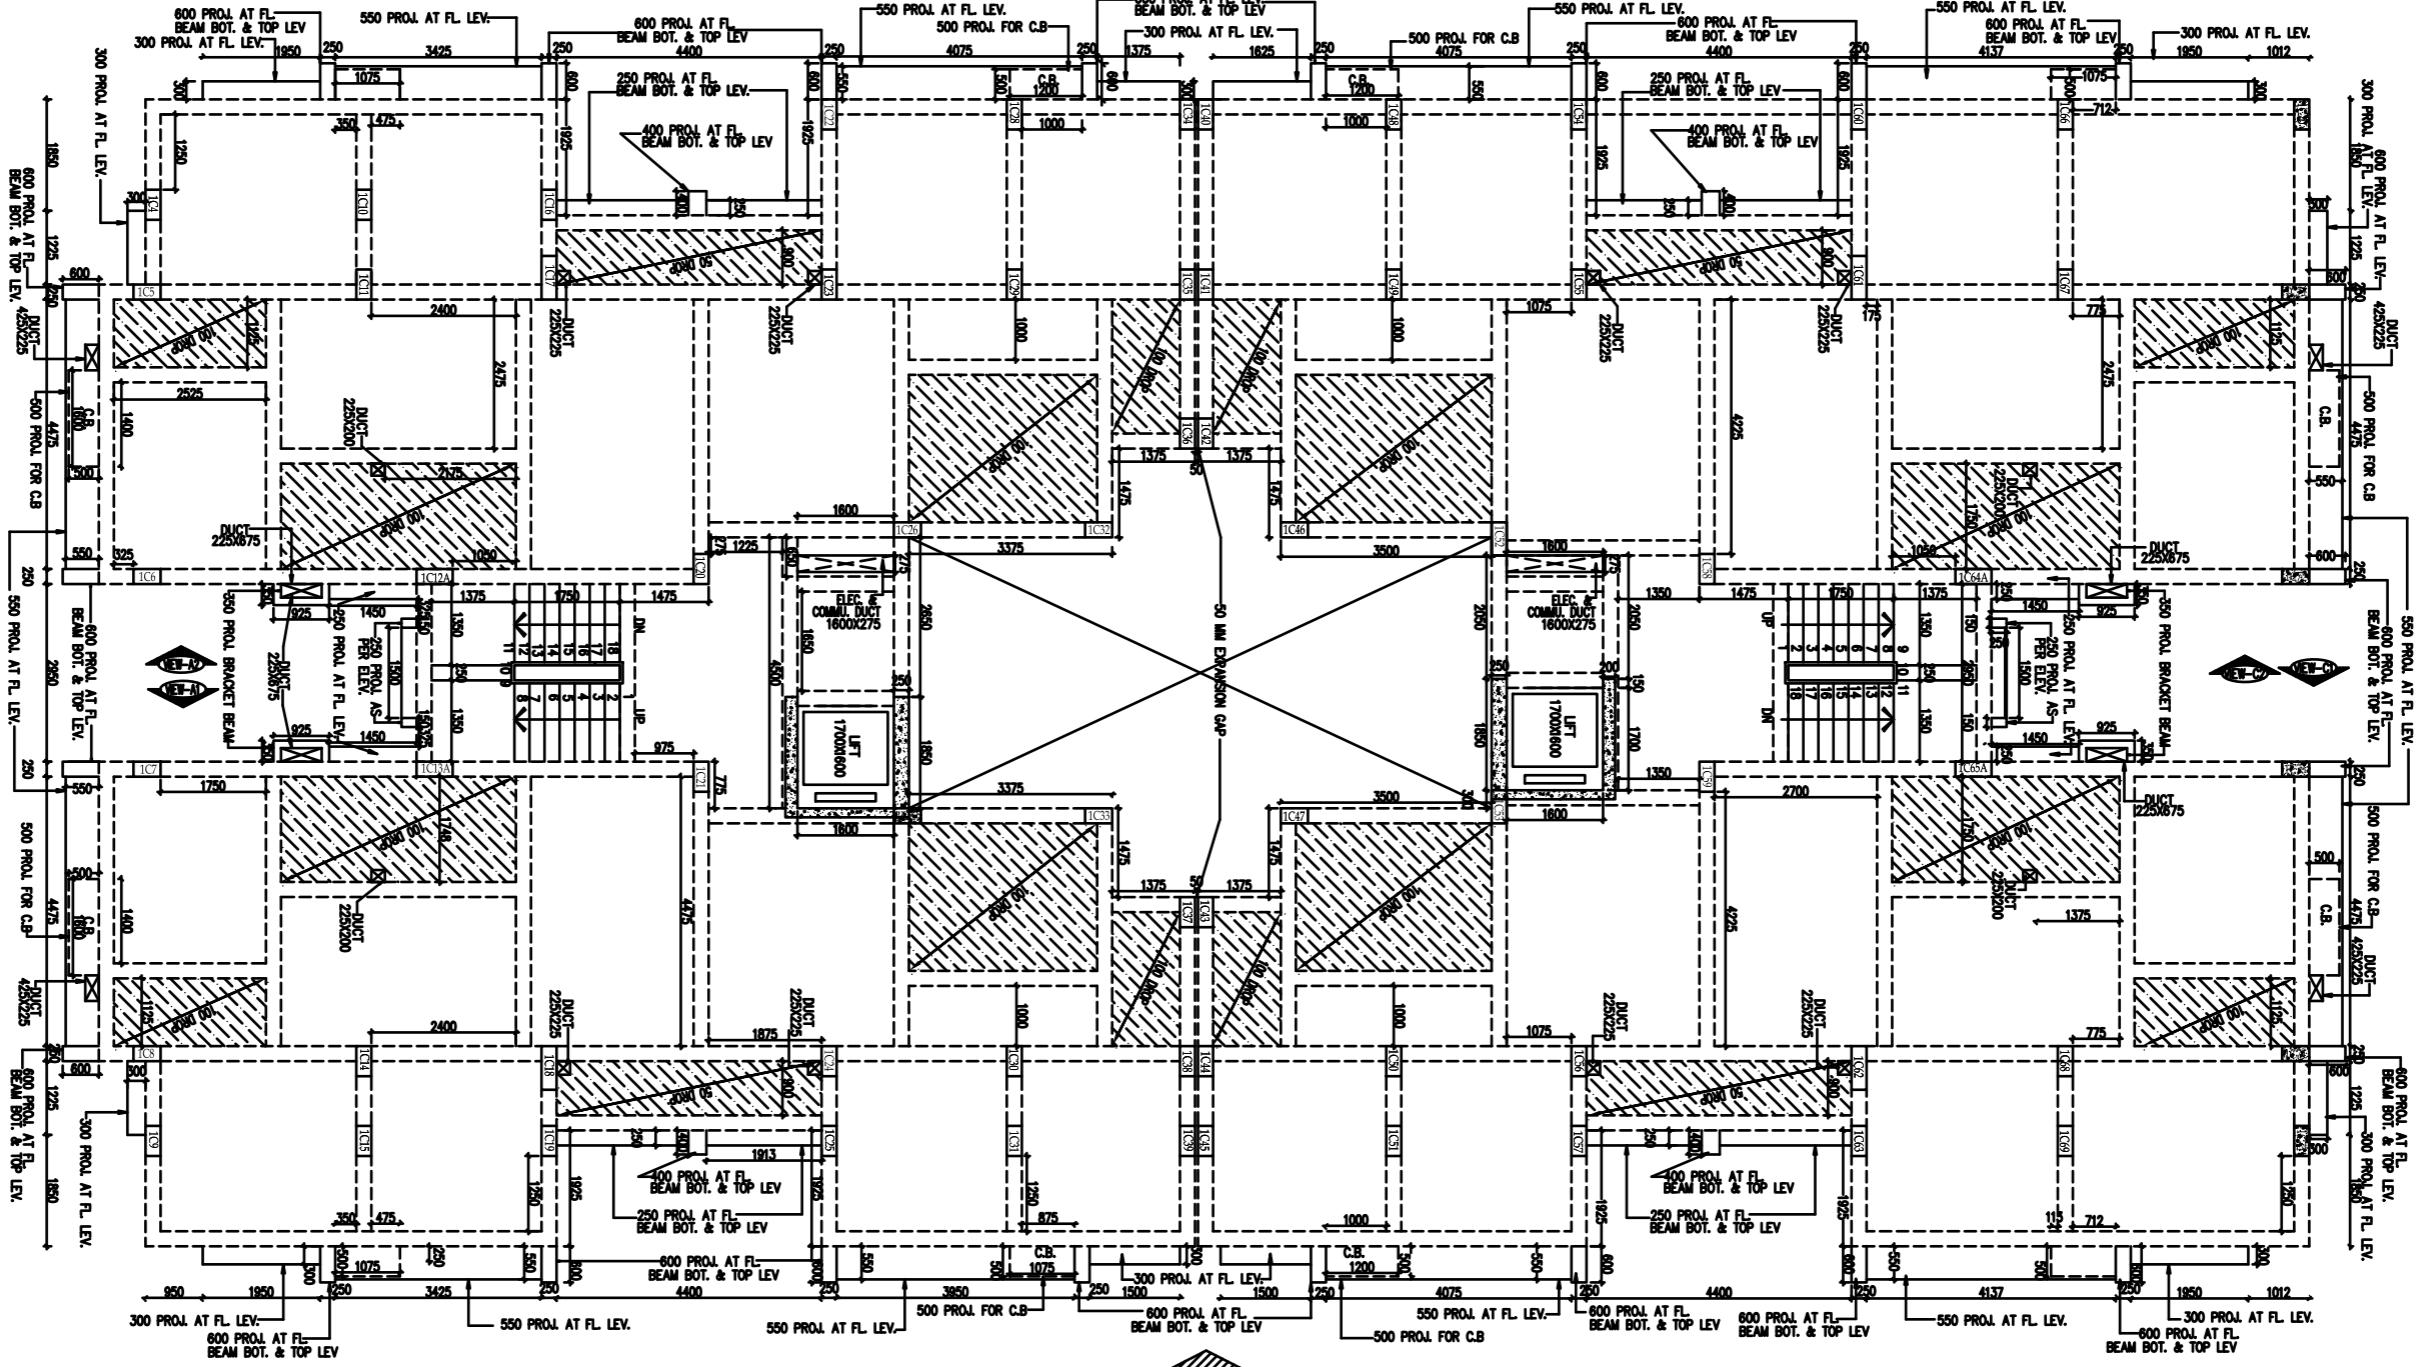


SCALE 1:75	ARCHITECTS N RAJU AGRAWAL & ASSOCIATES. 8B ROYD STREET, KOLKATA-16.
DATE 27/06/17	DRG NO JOB NO. REVAO, REVDATE DEALT CHECKED SIMPY S.MAJI

UGR AS PER DETAIL
NO CHANGE IN POSITION

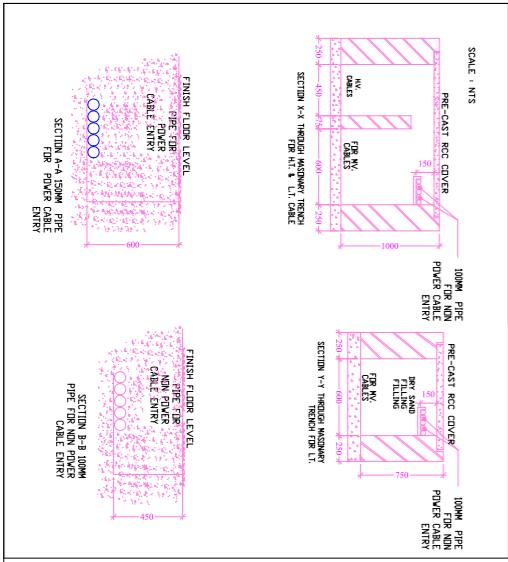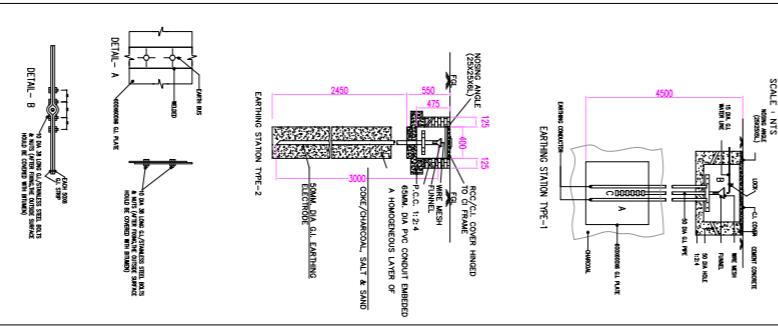
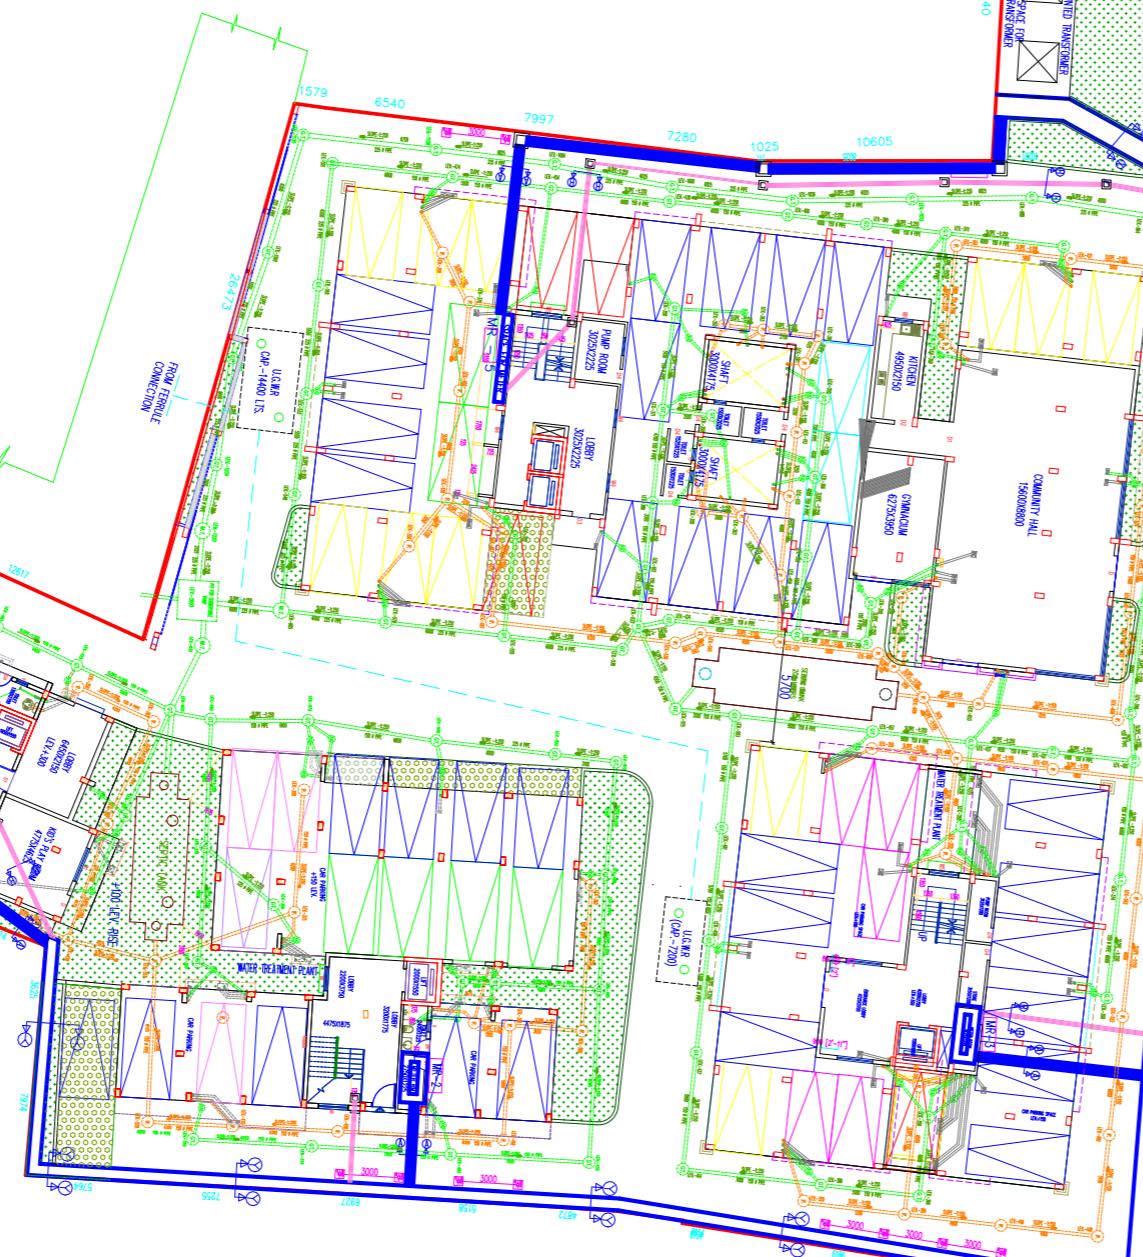


**TITLE- PHASE-I,PHASE-II,PHASE-III
COMBINED GROUND FLOOR INFRASTRUCTURE PLAN
PROJECT-
PROPOSED (G+IV) RESIDENTIAL BUILDING AT
NEW TOWN, KOLKATA.











(MAHSIBATHAN)**




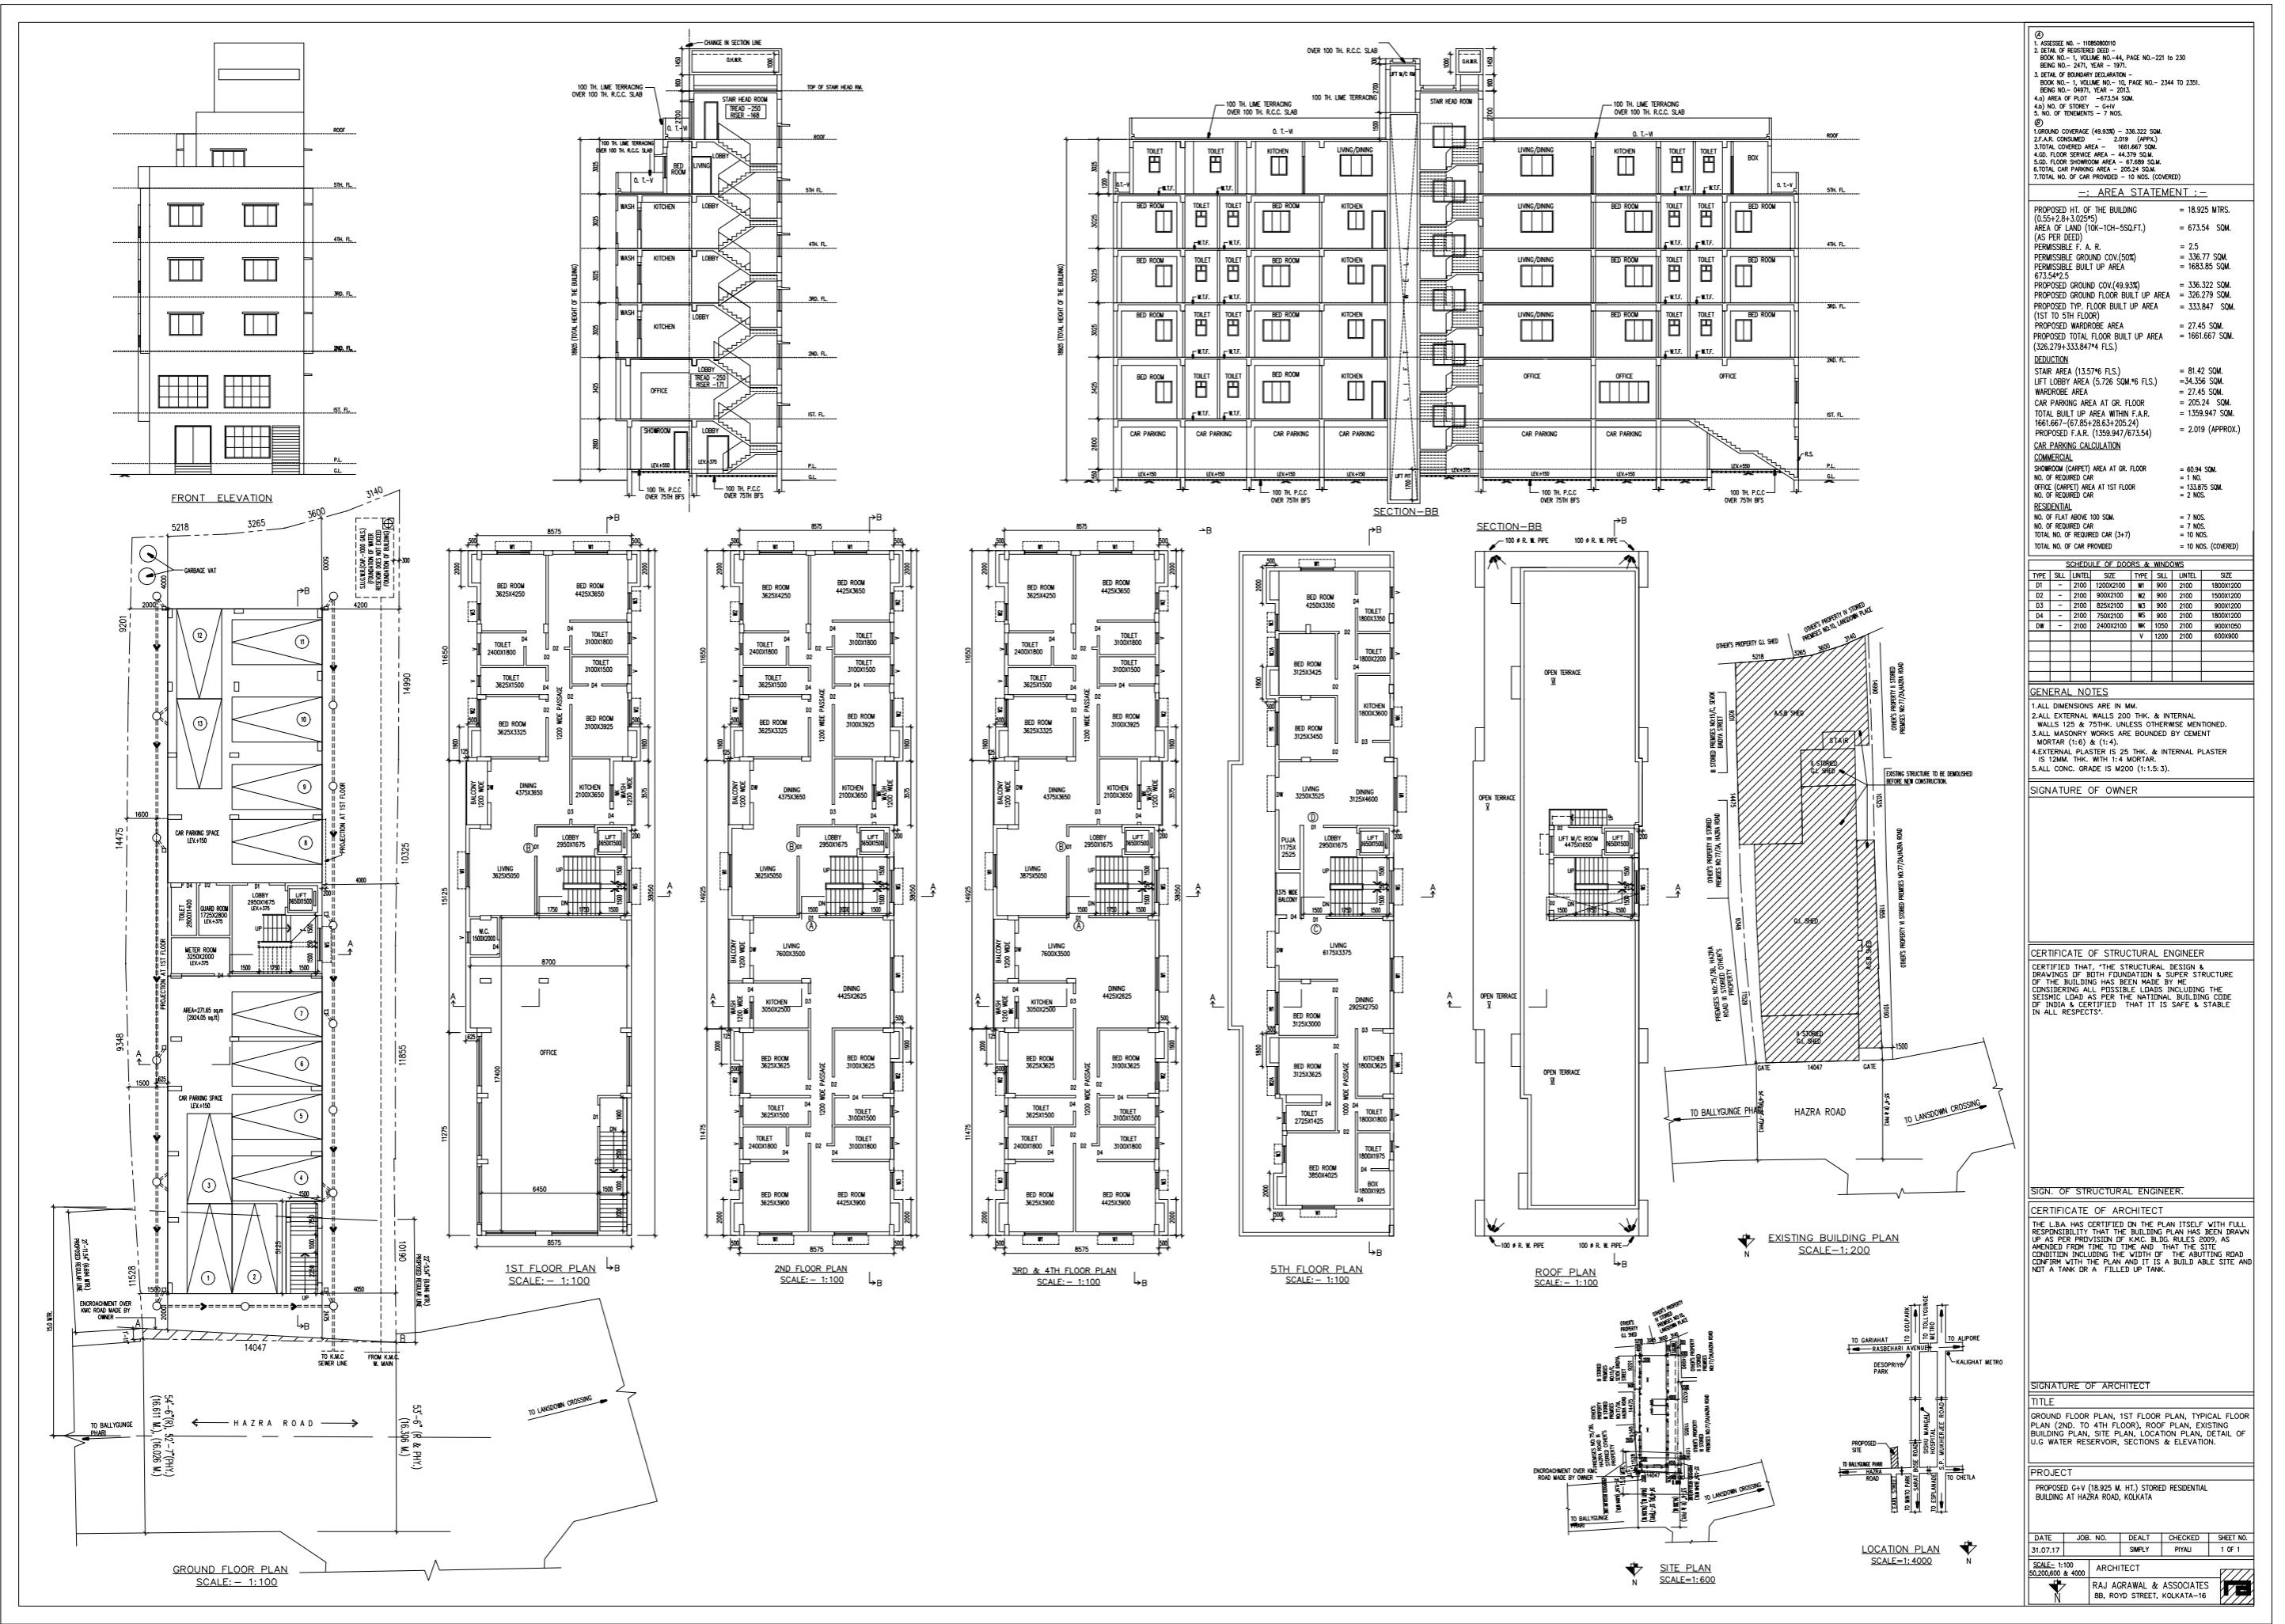




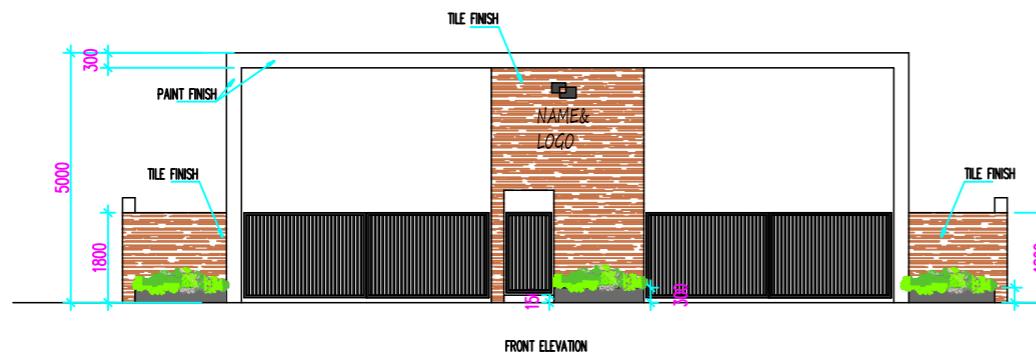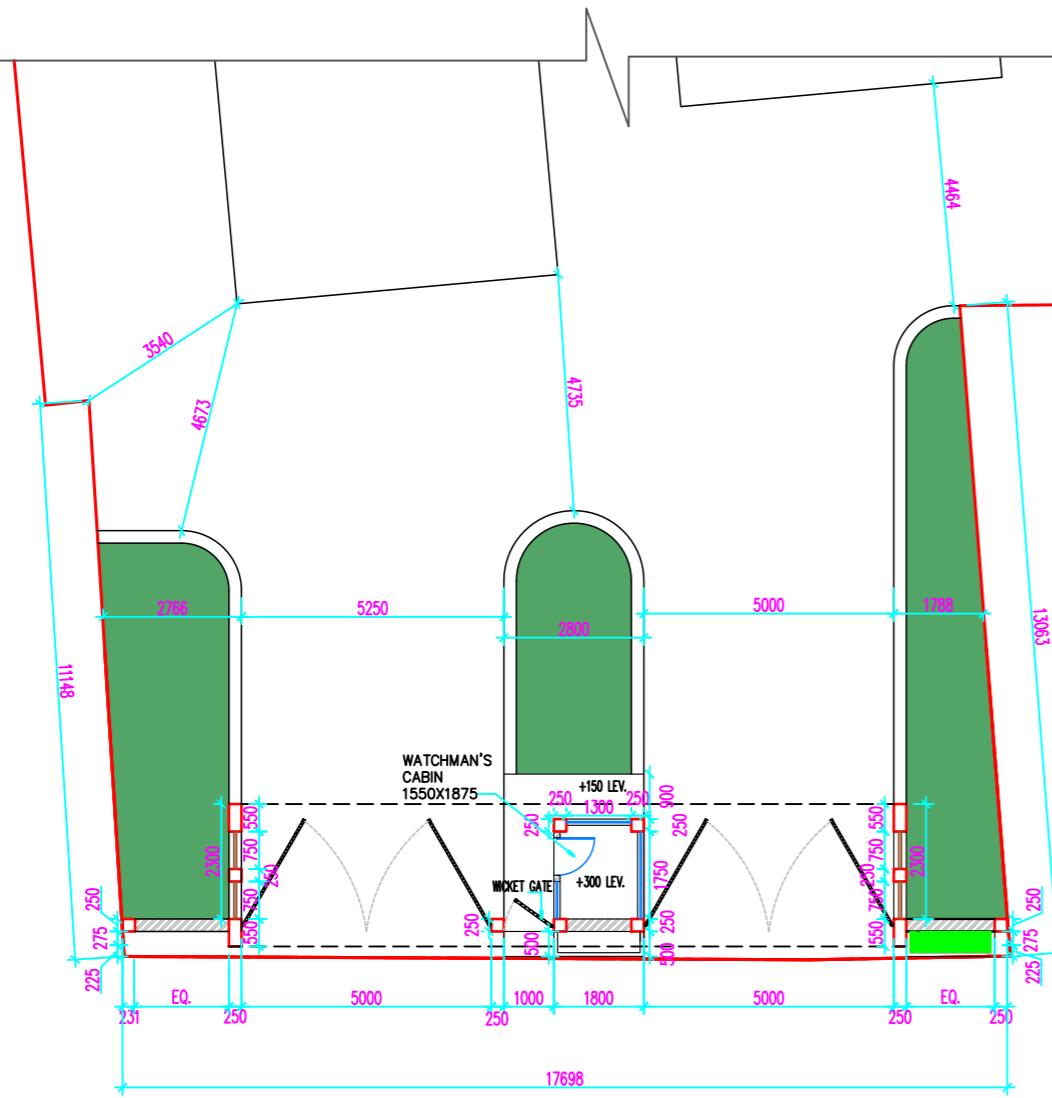

FRONT SIDE WALL AND MAIN GATE ELEVATION

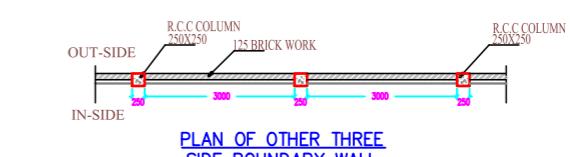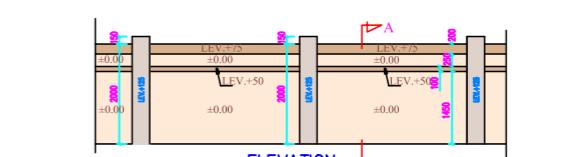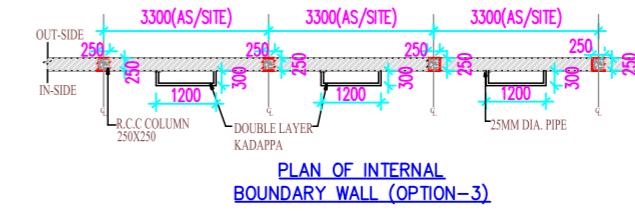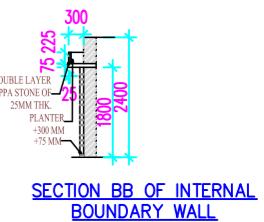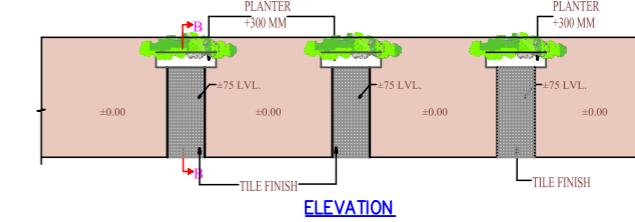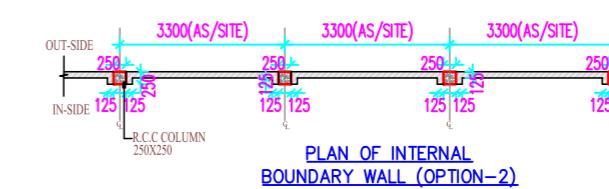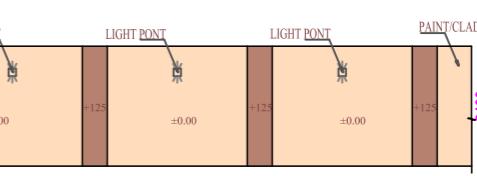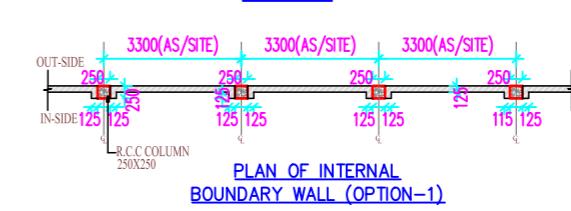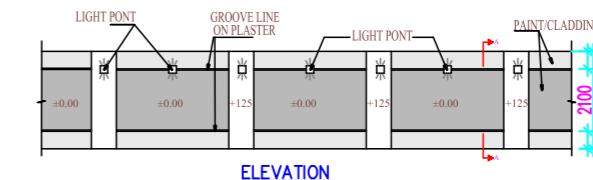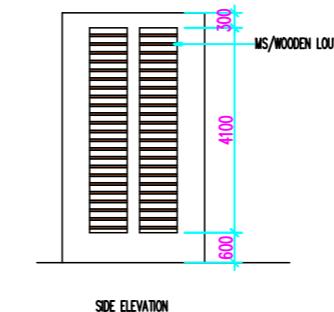

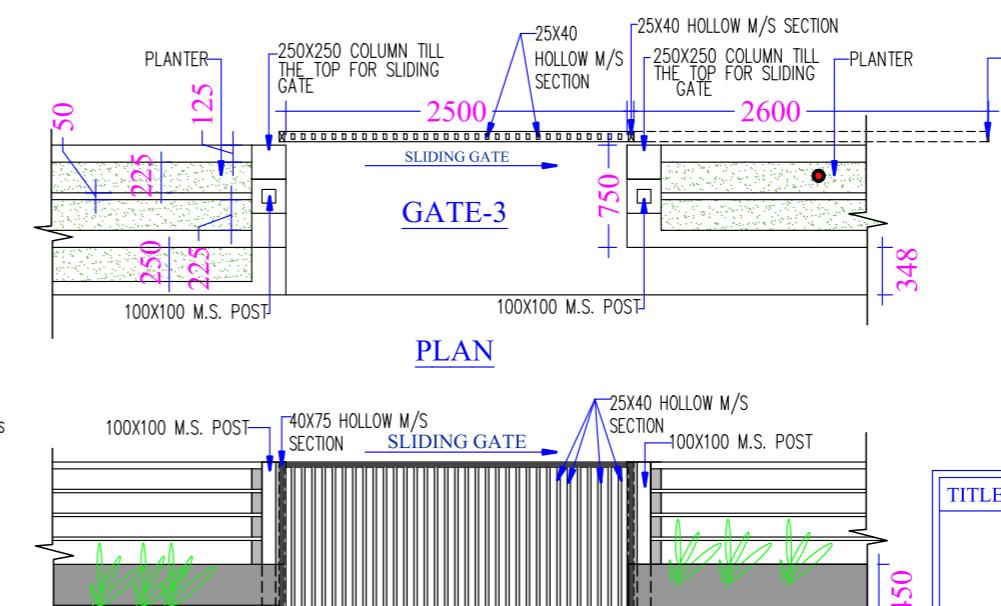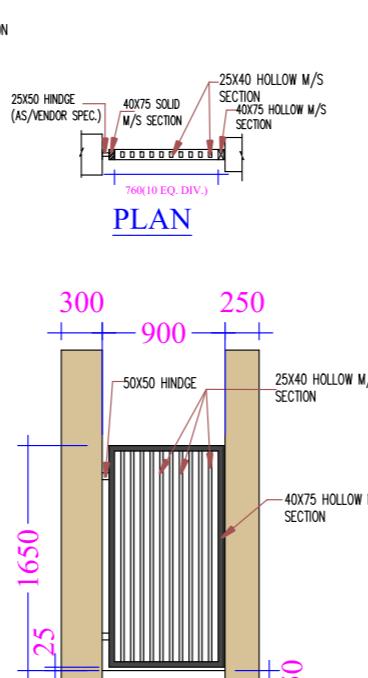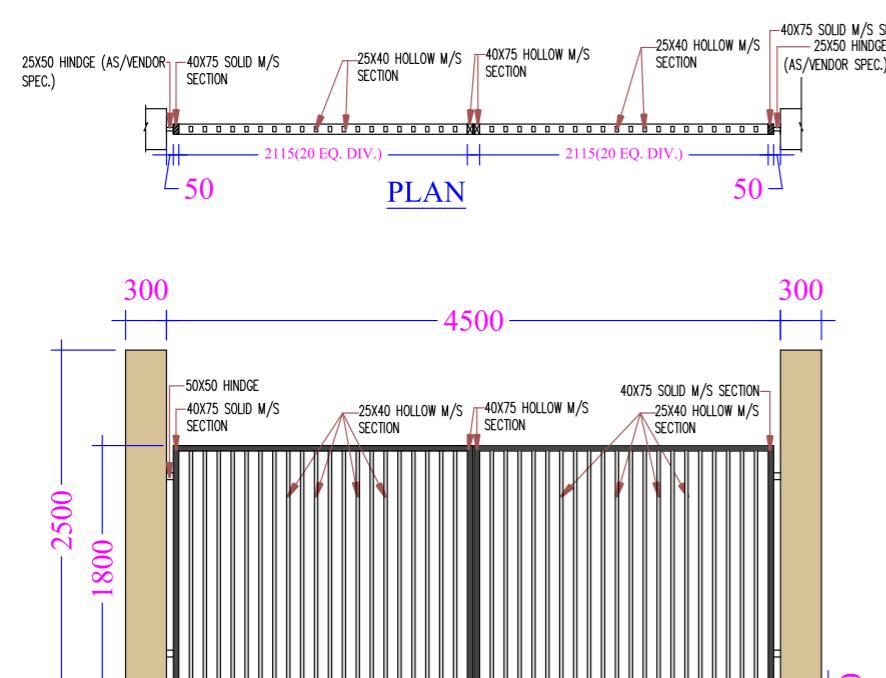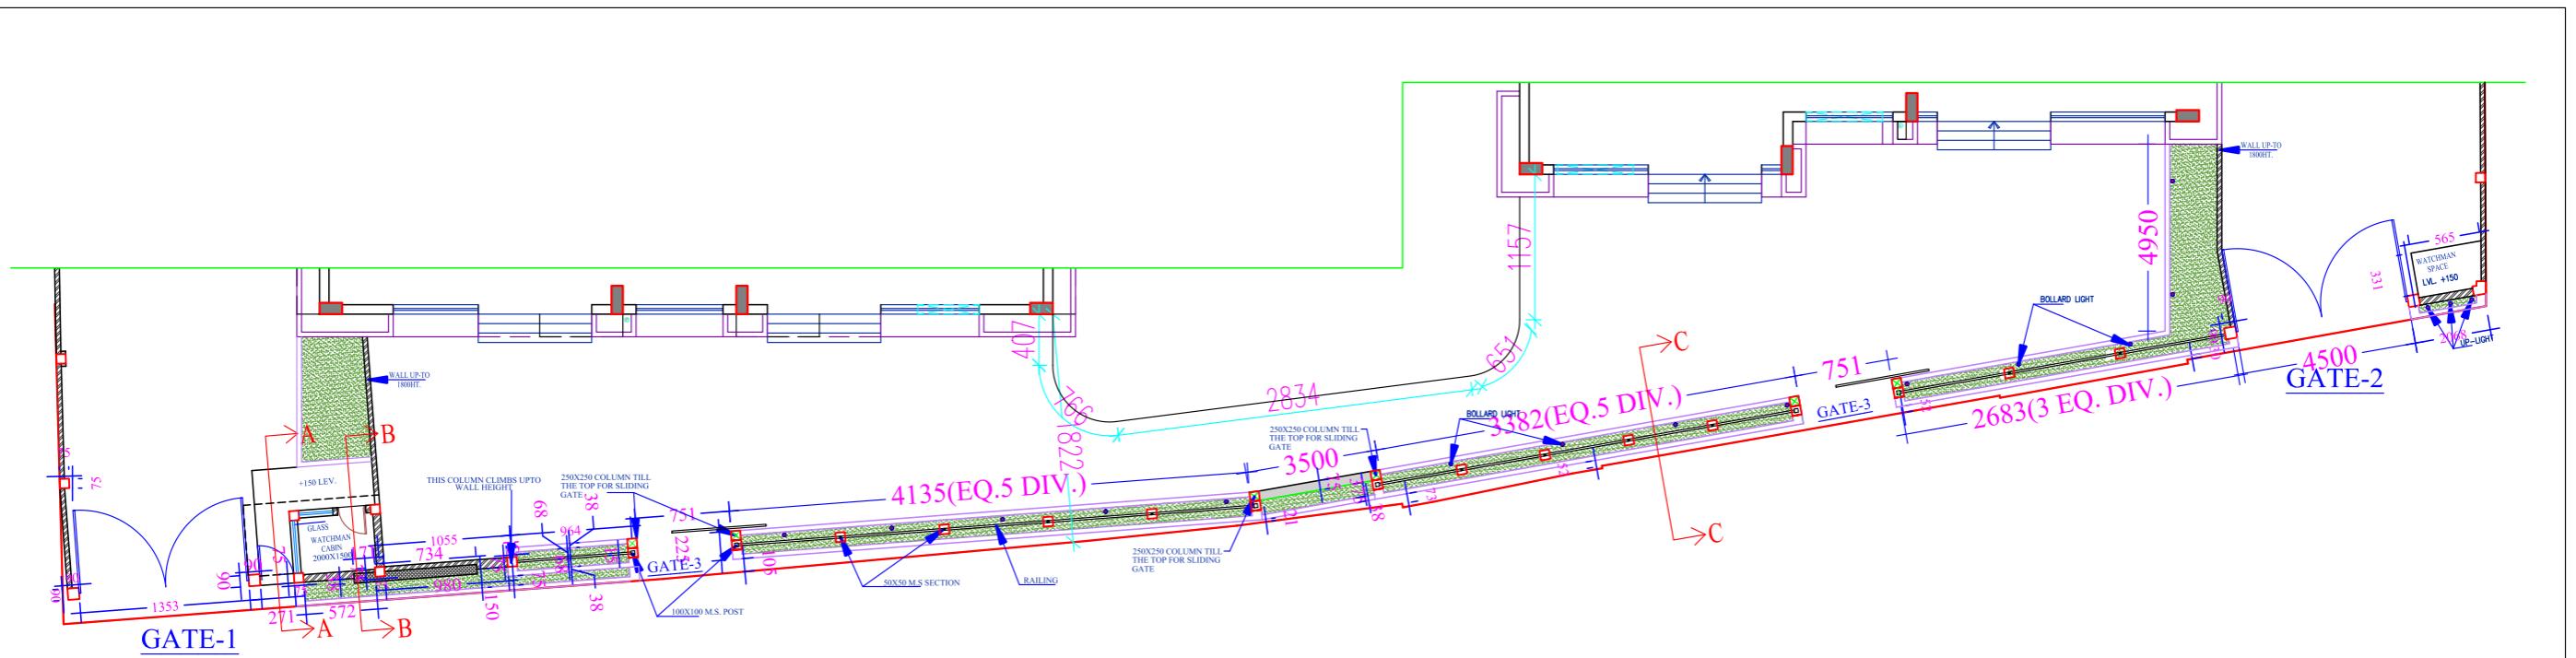

TITLE
GATE DETAIL (PLAN , ELEVATION)

PROJECT








**PLAN OF PROPOSED G+IX
STORIED (30.60 MT. HT.)
BUILDING AT RAJARHAT
GOPALPUR,KOLKATA**

SCALE 1:100 ARCHITECTS

**RAJ AGRAWAL & ASSOCIATES.
8B, ROYD STREET,
KOLKATA - 16.**



DATE	DRG. NO.	JOB NO.	REV. NO.	REV. DATE	DEALT	CHKD.
11.10.2017						SIMPLY SHEULI

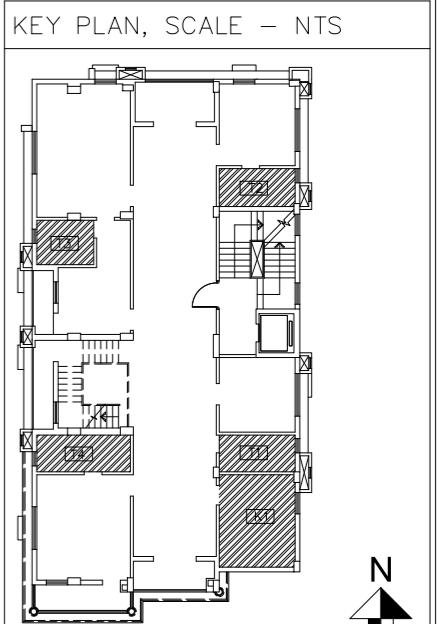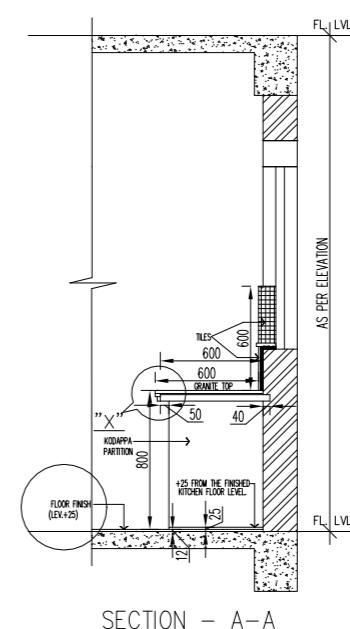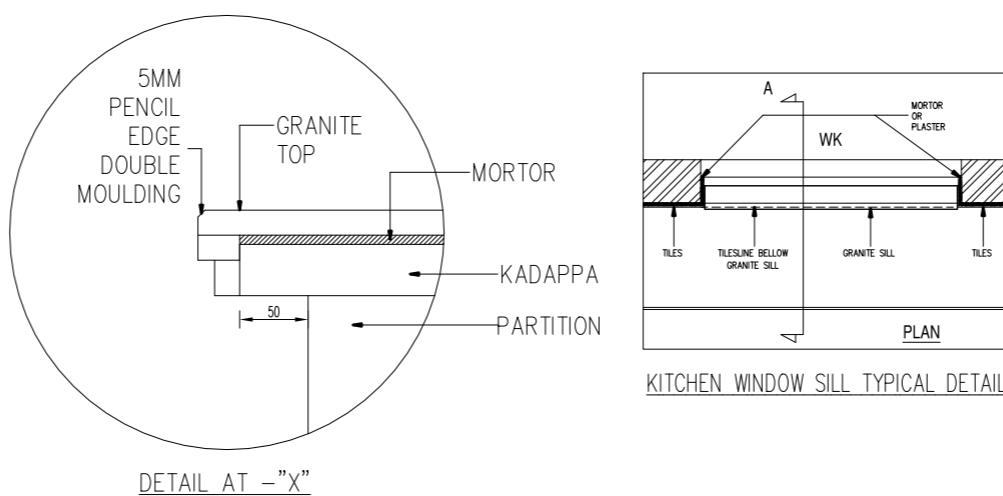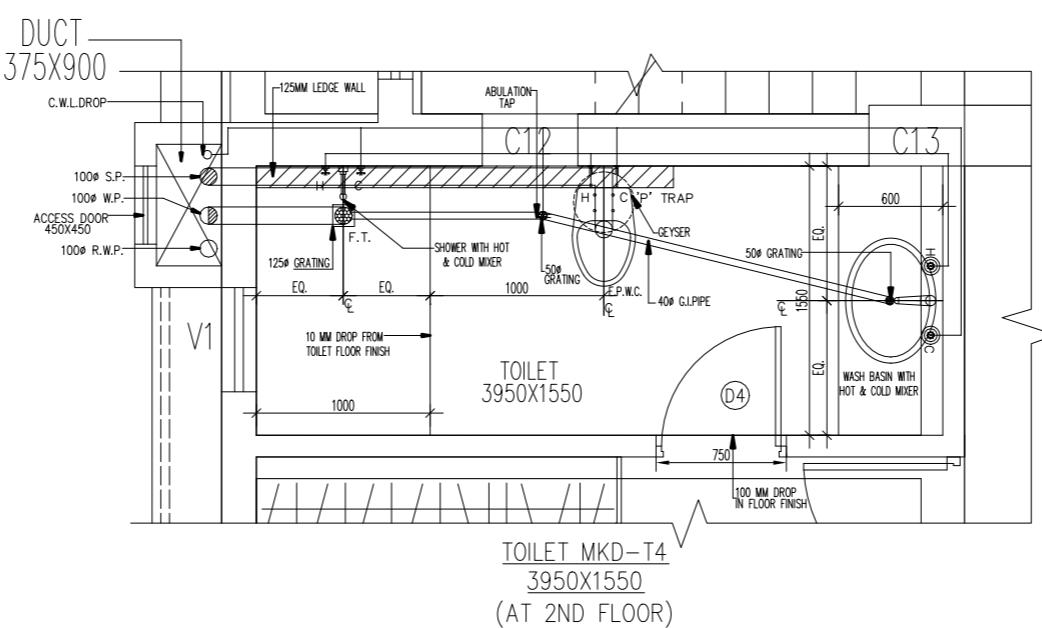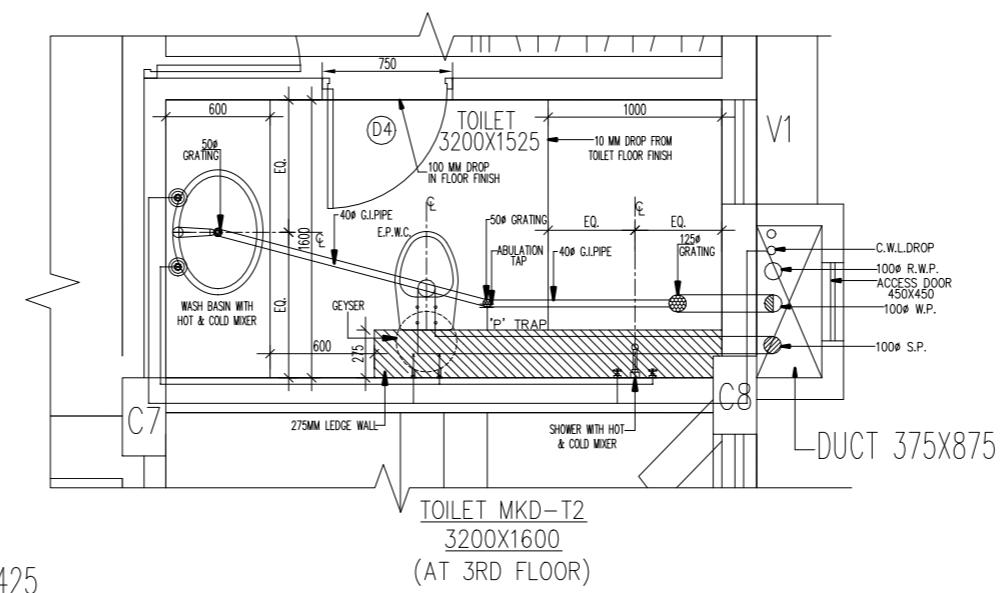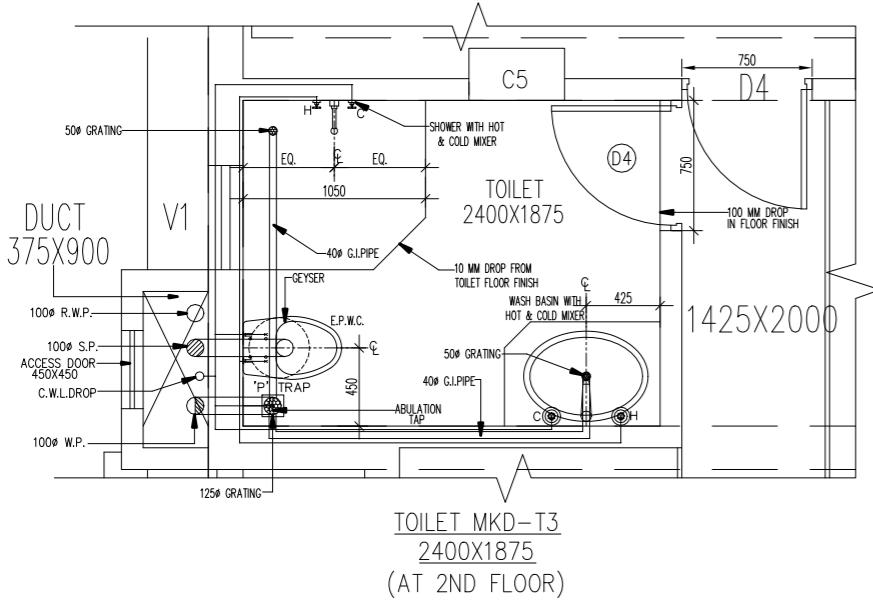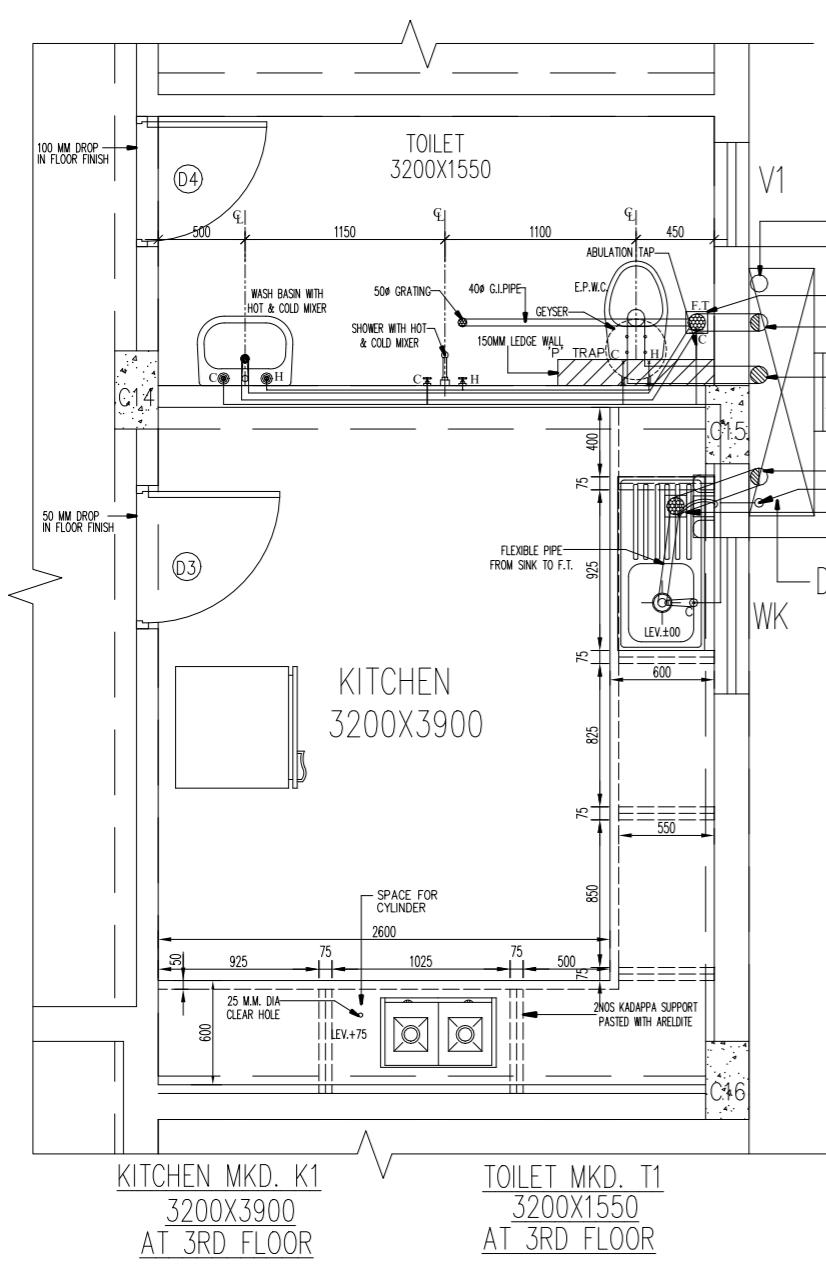

GENERAL NOTES:

- WRITTEN MEASUREMENTS SHOULD BE FOLLOWED ALWAYS, DRAWING SHOULD NOT BE SCALLED.
- IN CASE OF ANY DISCREPANCY NOTICED IN THE DRAWINGS, IMMEDIATELY INFORM THE ARCHITECTS, BEFORE PROCEEDING WITH ANY WORK ON THAT PART.
- REFER ONLY THE LATEST REVISED DRAWINGS; SUPERSEDED DRAWINGS NOT TO BE KEPT IN USE AT SITE.
- ALL DIMENSIONS ARE FINISHED DIMENSIONS (INCLUDING CLADDING).
- PIPE FROM CYLINDER CAN BE TAKEN ALTERNATIVELY THROUGH WALL.
- WASHING MACHINE POSITION IS ALREADY SHOWN IN FLOOR PLAN.

SANITARY PIPE LEGEND	
1. 100# SOIL PIPE	●
2. 100# WASTE PIPE	○
3. 100# RAIN WATER PIPE	○
4. 150# RAIN WATER PIPE	○
5. COLD LINE WATER DROP	○

SANITARY FIXTURE LEGEND		HT. OF FIX. FROM FLOOR FINISH mm
E.P.W.C.	EUROPEAN WALL MOUNTED	LEV mm
W.H.B.	WASH HAND BASIN	800 mm
A.T.	ABULATION TAP	450 mm
SHOWER MIXTURE	SHOWER ROSE	800 mm
GEYSER		1950 mm
F.T.	FLOOR TRAP	

SANITARY CONSULTANT









1. 19.02.13 SONALI WASH AREA DETAIL SRABANTI
NO. DATE DEALT PARTICULARS CHECKED

REVISION

TITLE
DETAIL OF 2ND FLOOR TOILET KITCHEN DETAIL

PROJECT
PROPOSED G+IV STORED BUILDING AT SOUTH DUMDUM

SCALE	ARCHITECTS
1:25	RAJ AGRAWAL & ASSOCIATES. 8B, ROYD STREET, KOLKATA-16.
DATE	DRG.NO. JOB NO. REV.NO. REV.DATE DEALT CHECKED 30.10.17 SIMPLY SHEULI

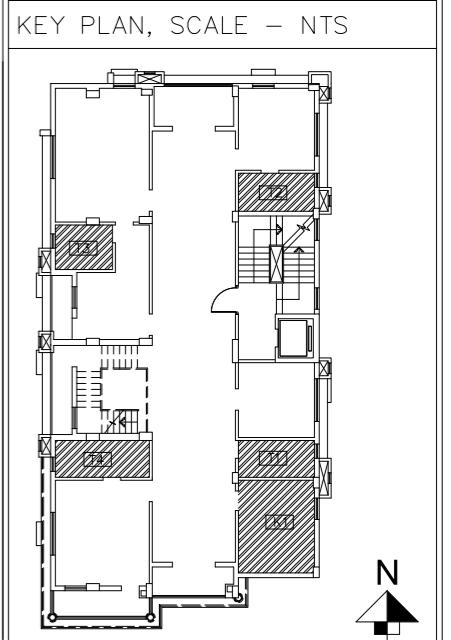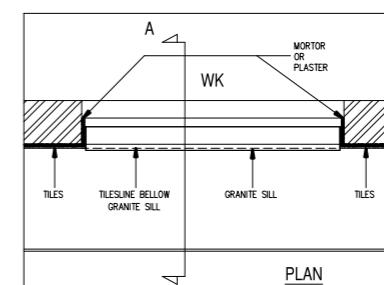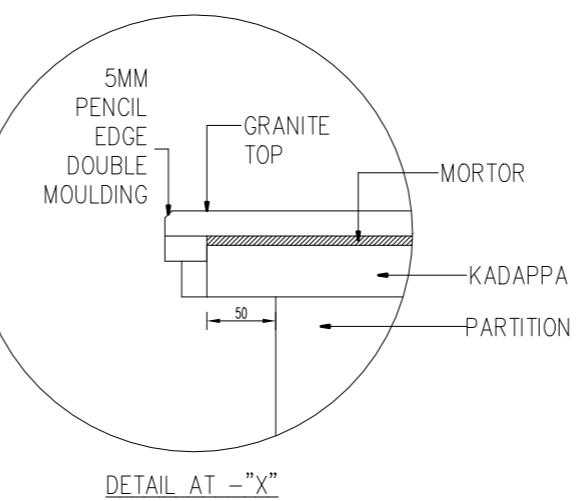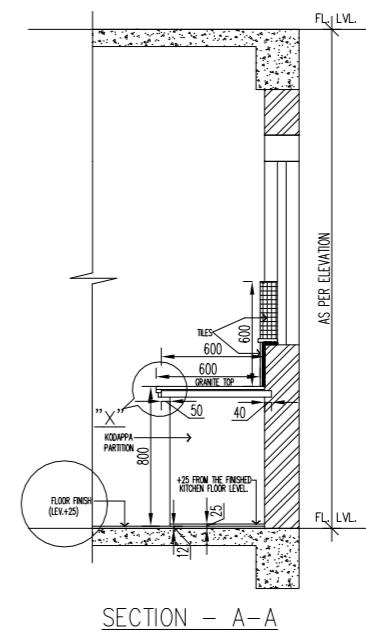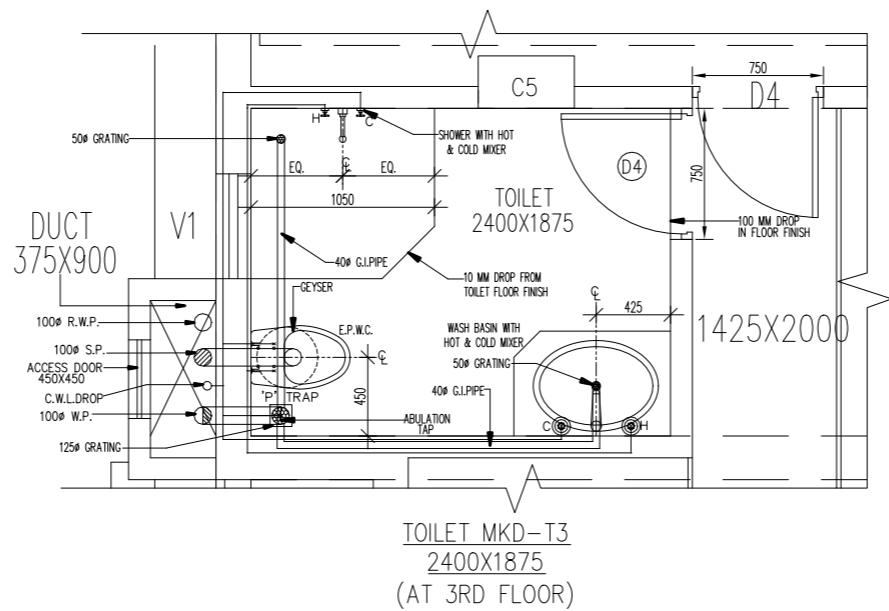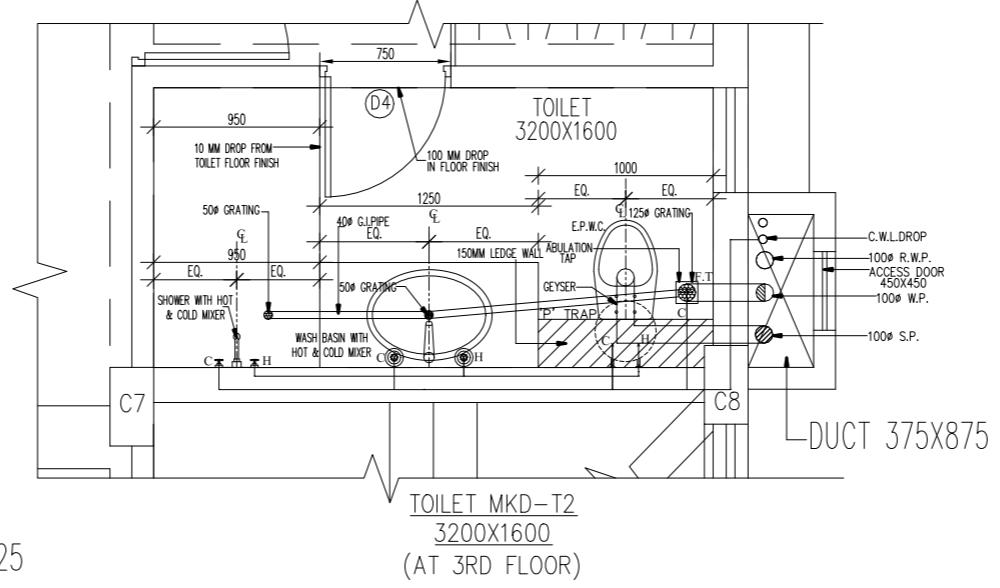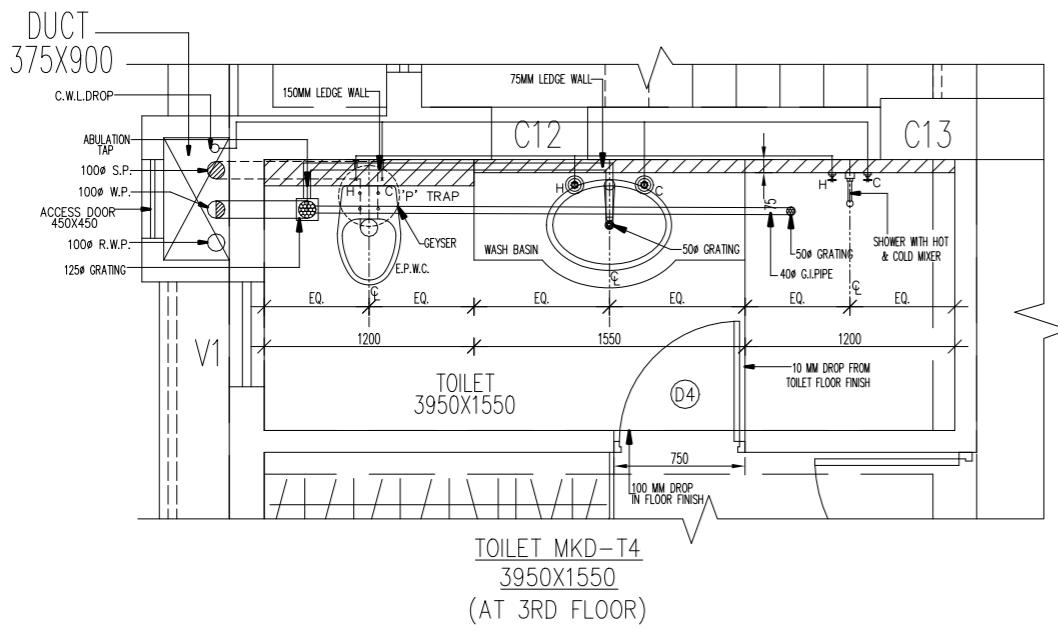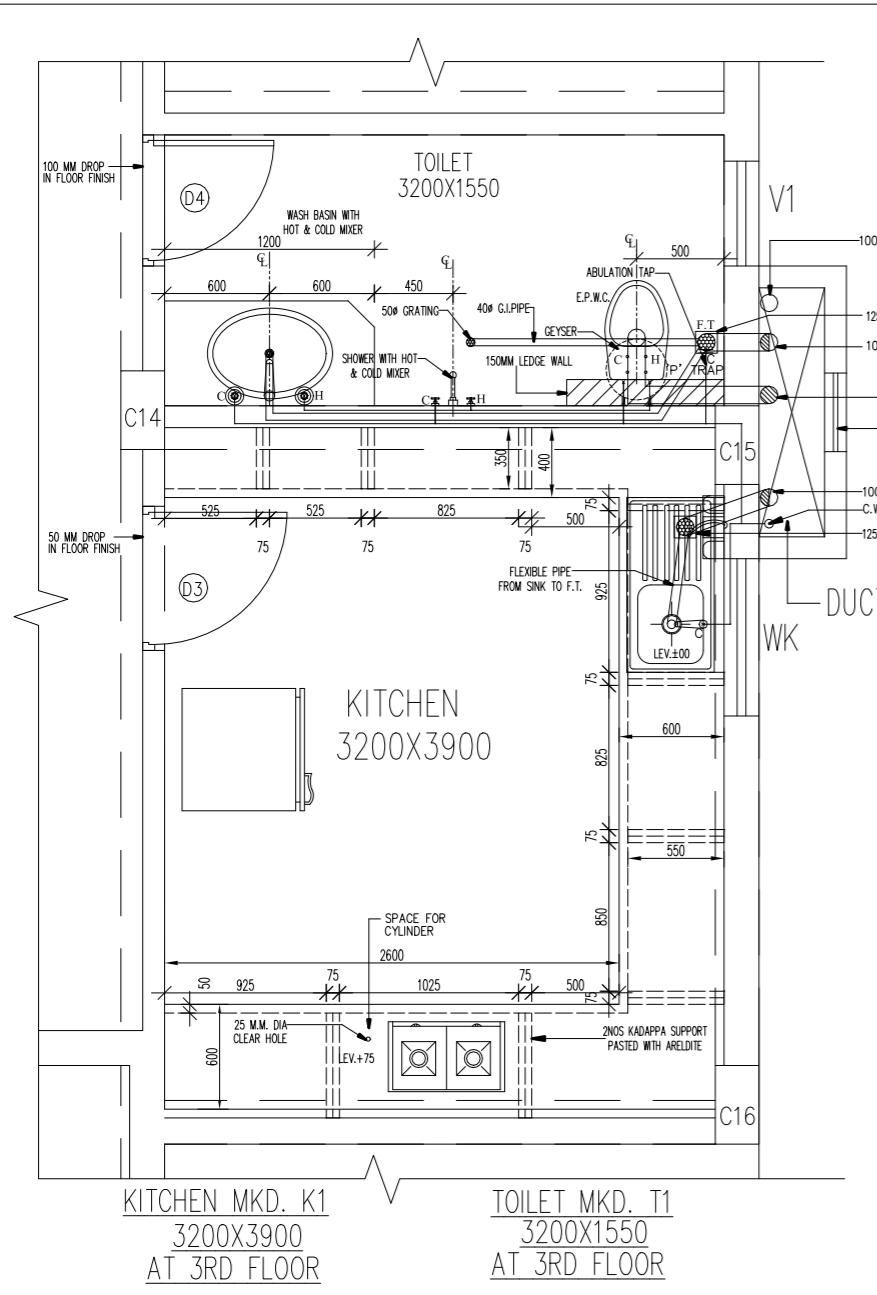

GENERAL NOTES:-

1. WRITTEN MEASUREMENTS SHOULD BE FOLLOWED ALWAYS, DRAWING SHOULD NOT BE SCALED.
2. IN CASE OF ANY DISCREPANCY NOTICED IN THE DRAWINGS, IMMEDIATELY INFORM THE ARCHITECTS, BEFORE PROCEEDING WITH ANY WORK ON THAT PART.
3. REFER ONLY THE LATEST REVISED DRAWINGS; SUPERSEDED DRAWINGS NOT TO BE KEPT IN USE AT SITE.
4. ALL DIMENSIONS ARE FINISHED DIMENSIONS (INCLUDING CLADDING)
5. PIPE FROM CYLINDER CAN BE TAKEN ALTERNATIVELY THROUGH WALL.
6. WASHING MACHINE POSITION IS ALREADY SHOWN IN FLOOR PLAN.

SANITARY PIPE LEGEND

1. 100# SOIL PIPE
2. 100# WASTE PIPE
3. 100# RAIN WATER PIPE
4. 150# RAIN WATER PIPE
5. COLD LINE WATER DROP

SANITARY FIXTURE LEGEND

HT. OF FIX. FROM FLOOR FINISH
E.P.W.C. EUROPEAN WALL MOUNTED 100 mm
W.H.B. WASH HAND BASIN 800 mm
A.B.T. ABLOUTION TAP 450 mm
SHOWER MIXTURE 800 mm
SHOWER ROSE 1950 mm
GEYSER
F.T. FLOOR TRAP


SANITARY CONSULTANT


NO. DATE DEALT PARTICULARS CHECKED
1. REVISION
TITLE
DETAIL OF 3RD FLOOR TOILET KITCHEN DETAIL
PROJECT
PROPOSED G+H STORED BUILDING AT SOUTH DUMDUM


SCALE 1:25 ARCHITECTS

RAJ AGRAWAL & ASSOCIATES.
8B, ROYD STREET,
KOLKATA-16.



DATE DRG.NO	JOB NO. REV.NO.	REV.DATE DEALT CHECKED
30.10.17		SIMPLY SHEULI

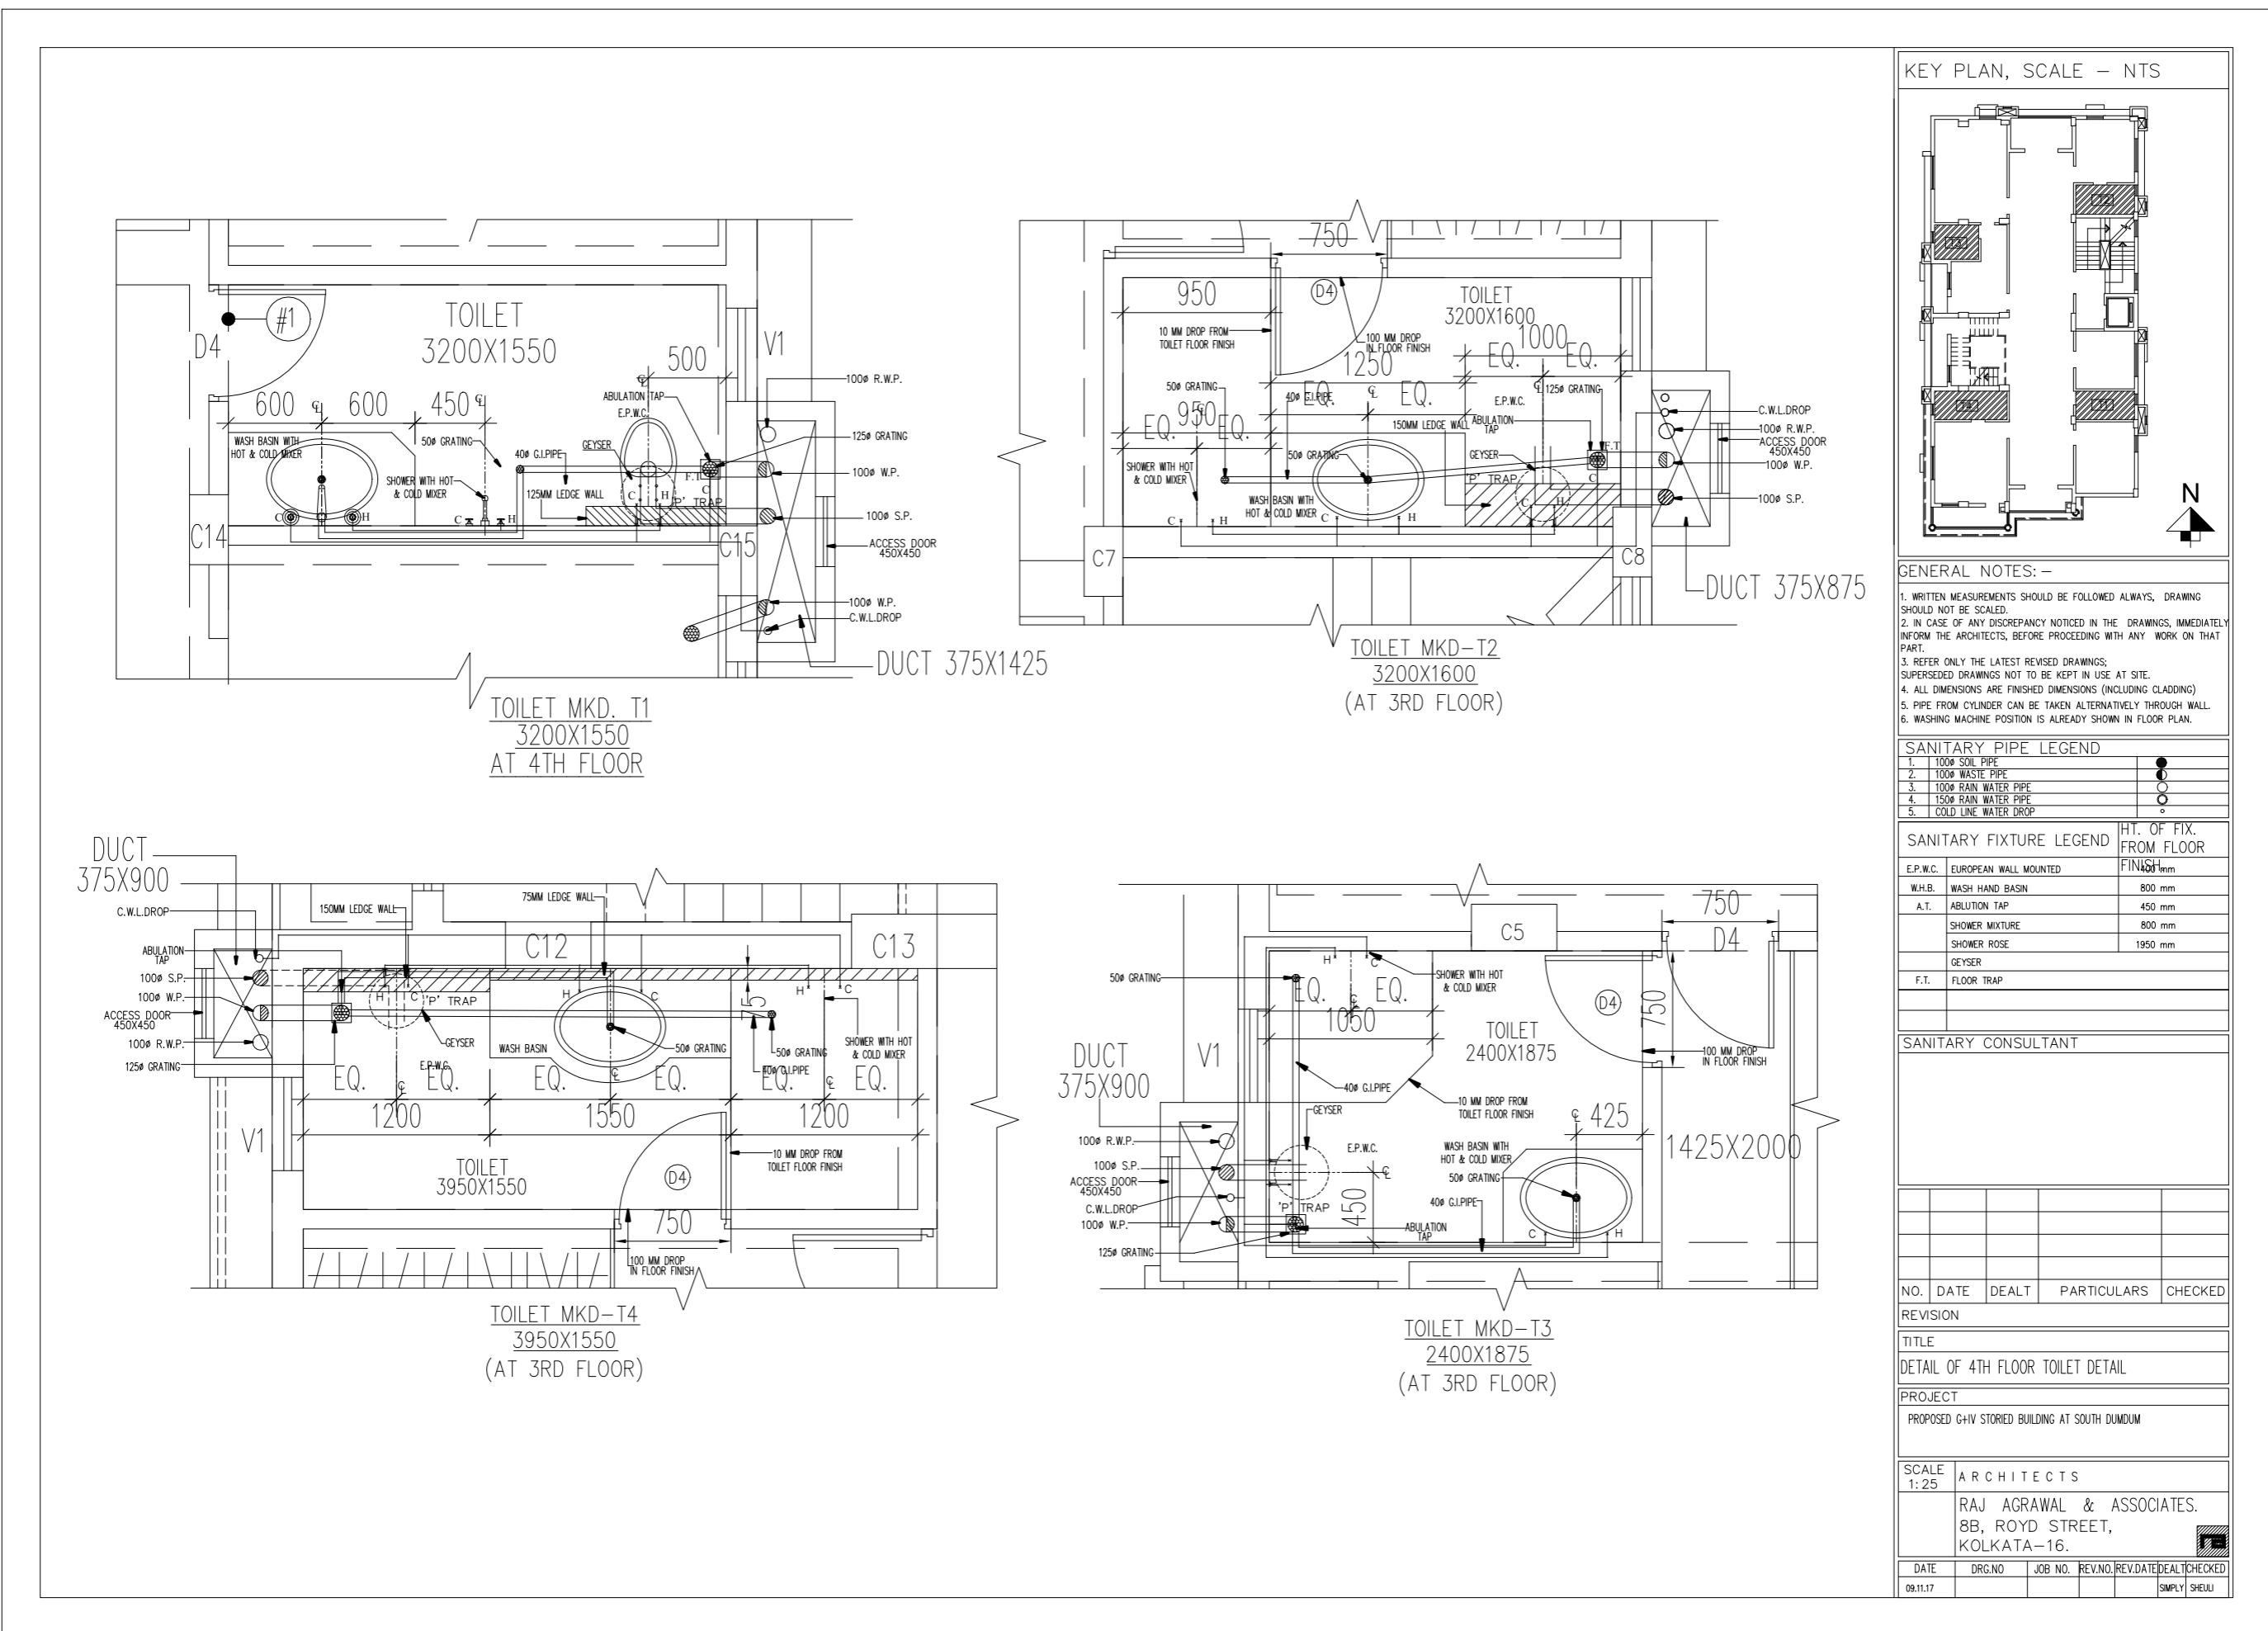

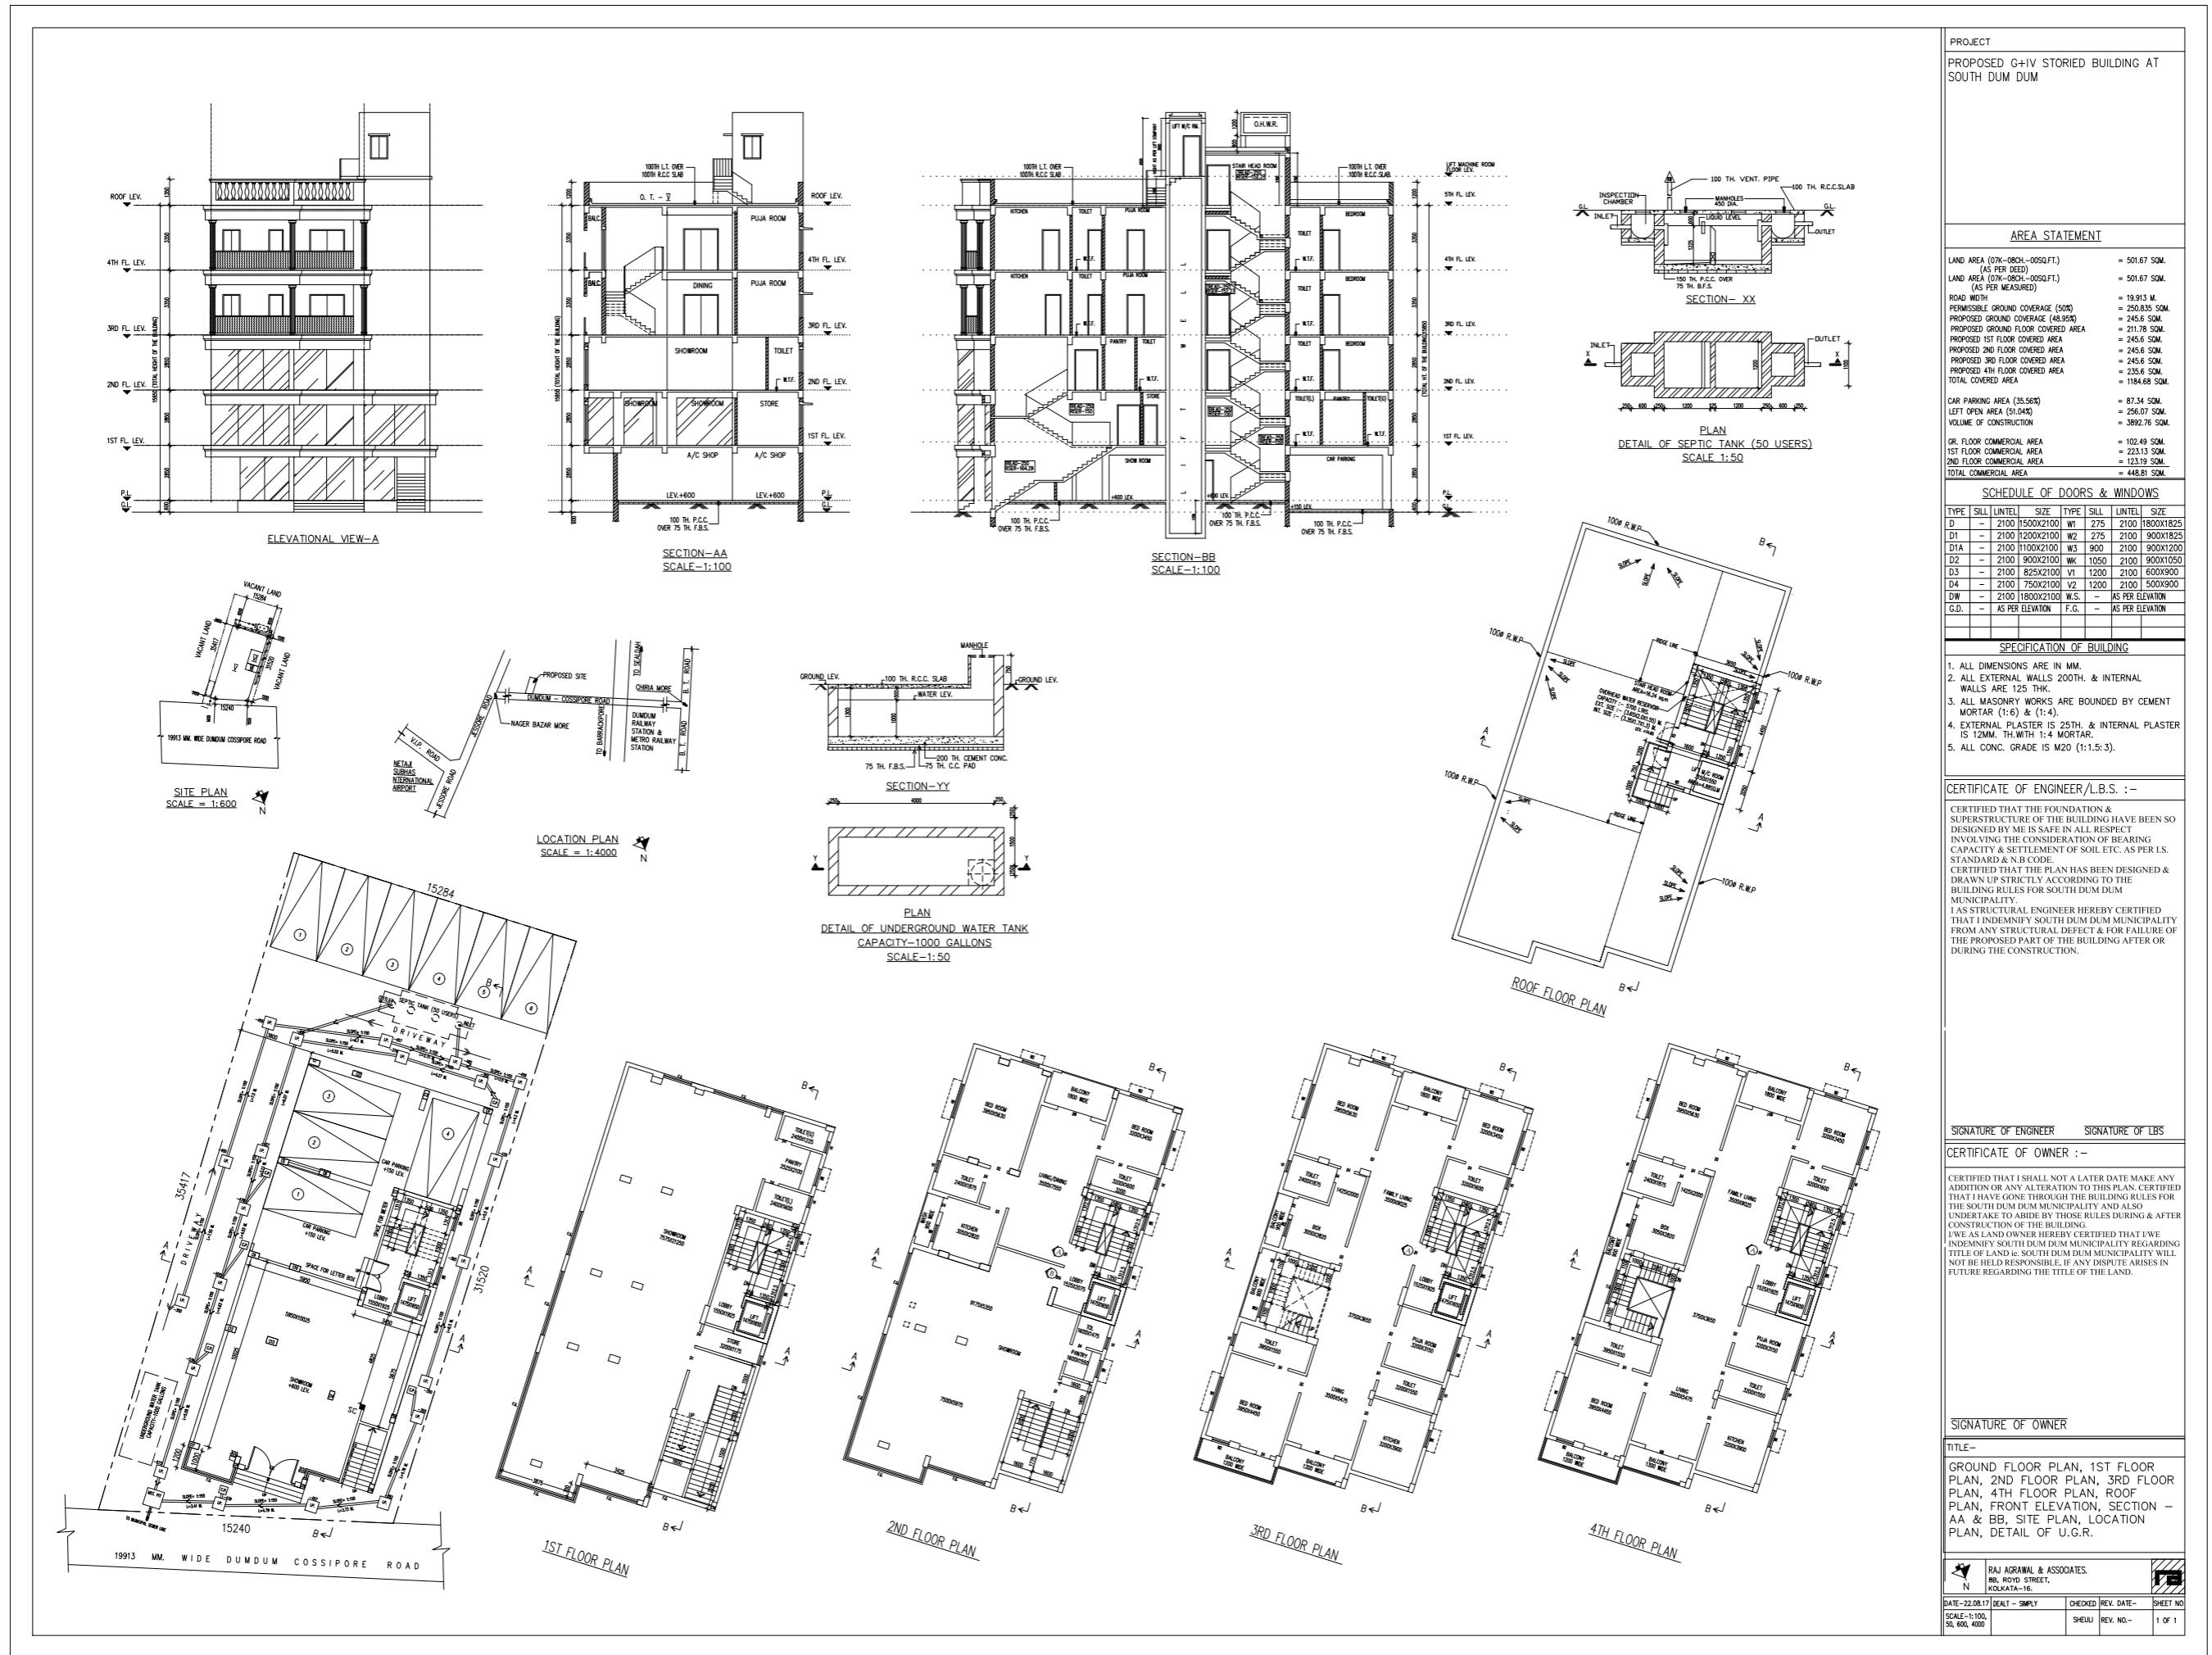

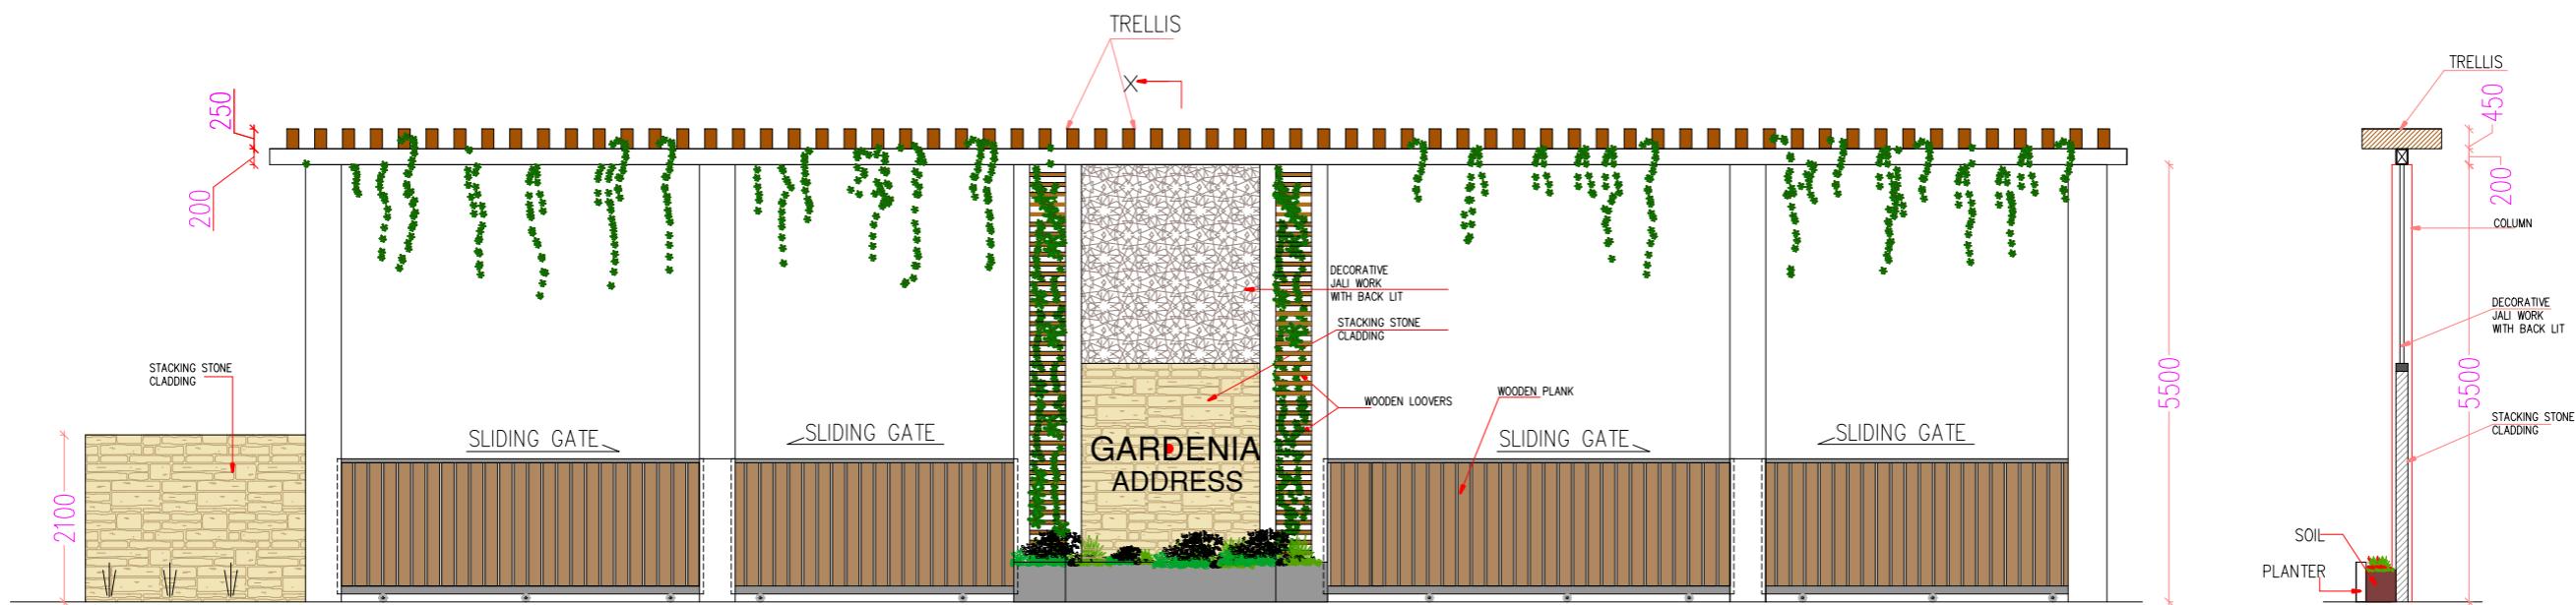

TYPICAL SECTION
OF TRELLIS XX

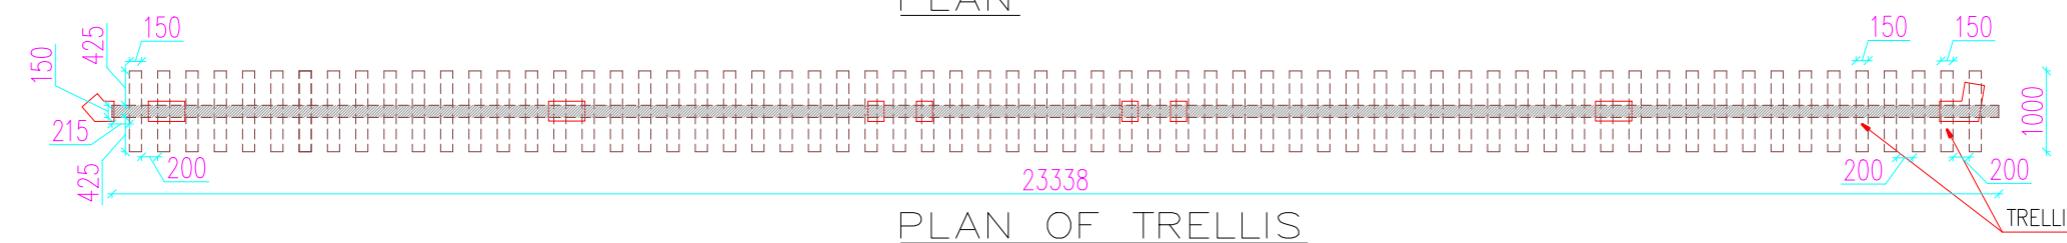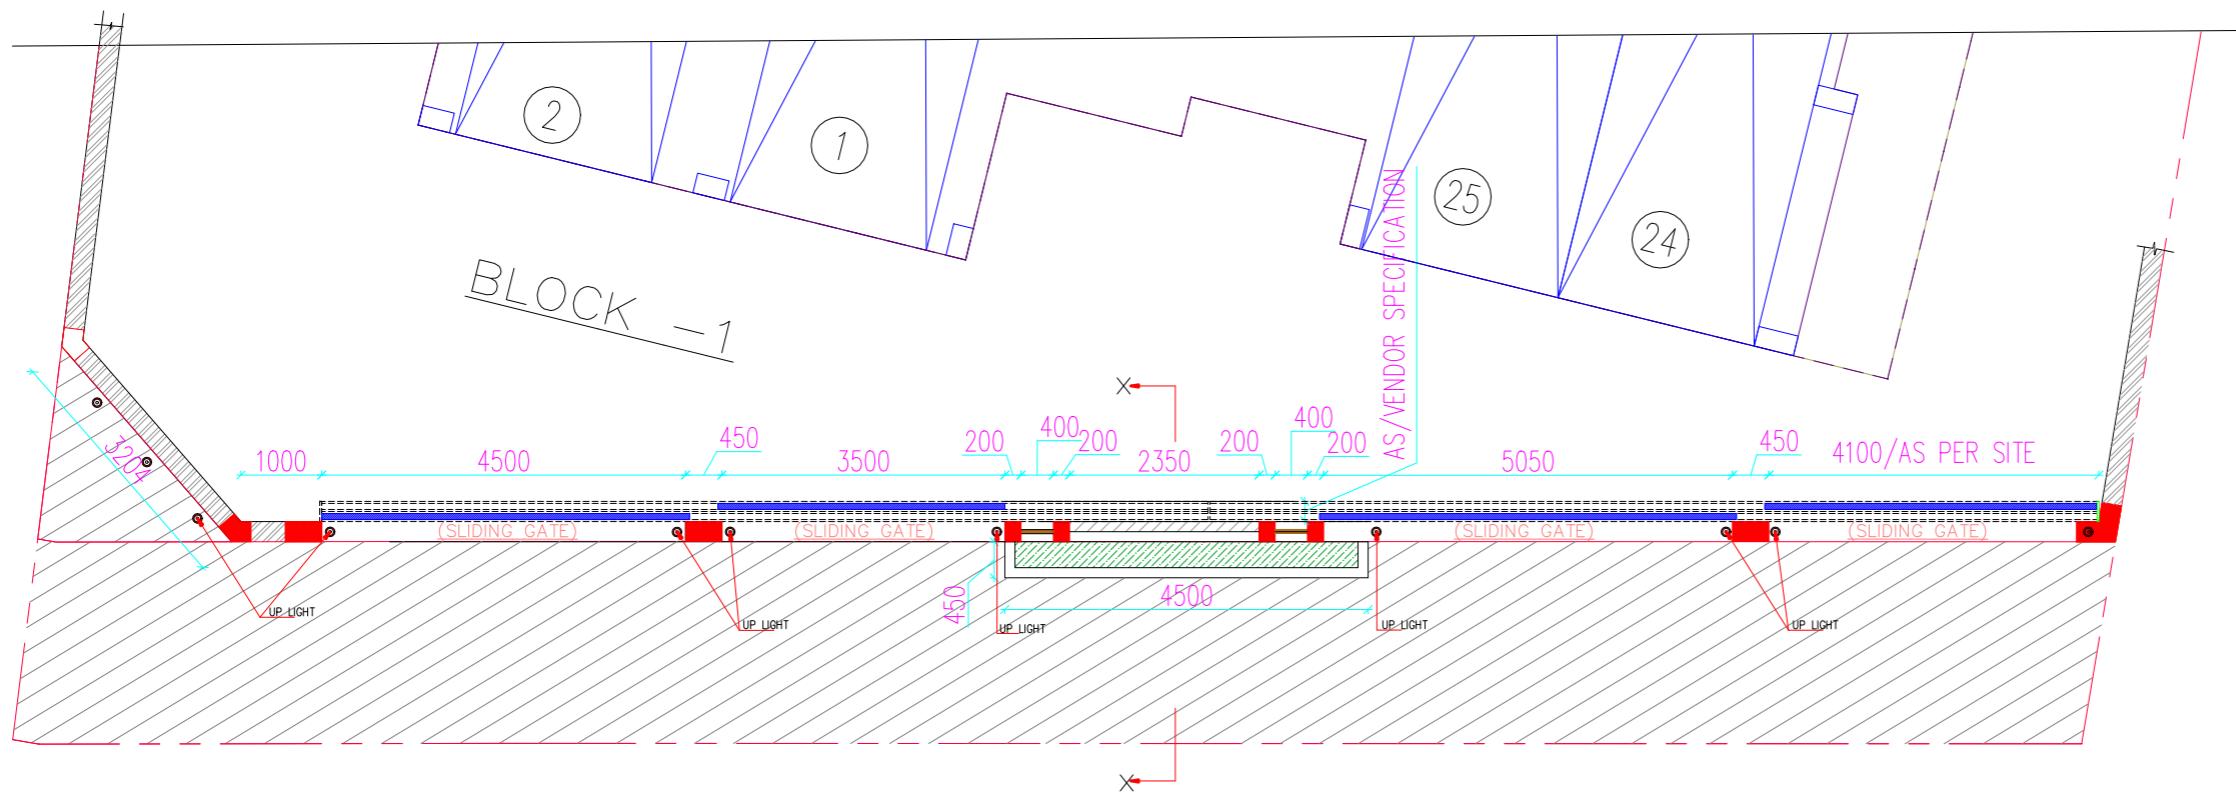

PROJECTS:


PROPOSED MAIN GATE FOR G+IV HOUSING COMPLEX AT RAMCHANDRAPUR.

MAIN GATE DESIGN RAJ AGRAWAL & ASSOCIATES.


DEALT-SHEULI




DATE-17.10.2017

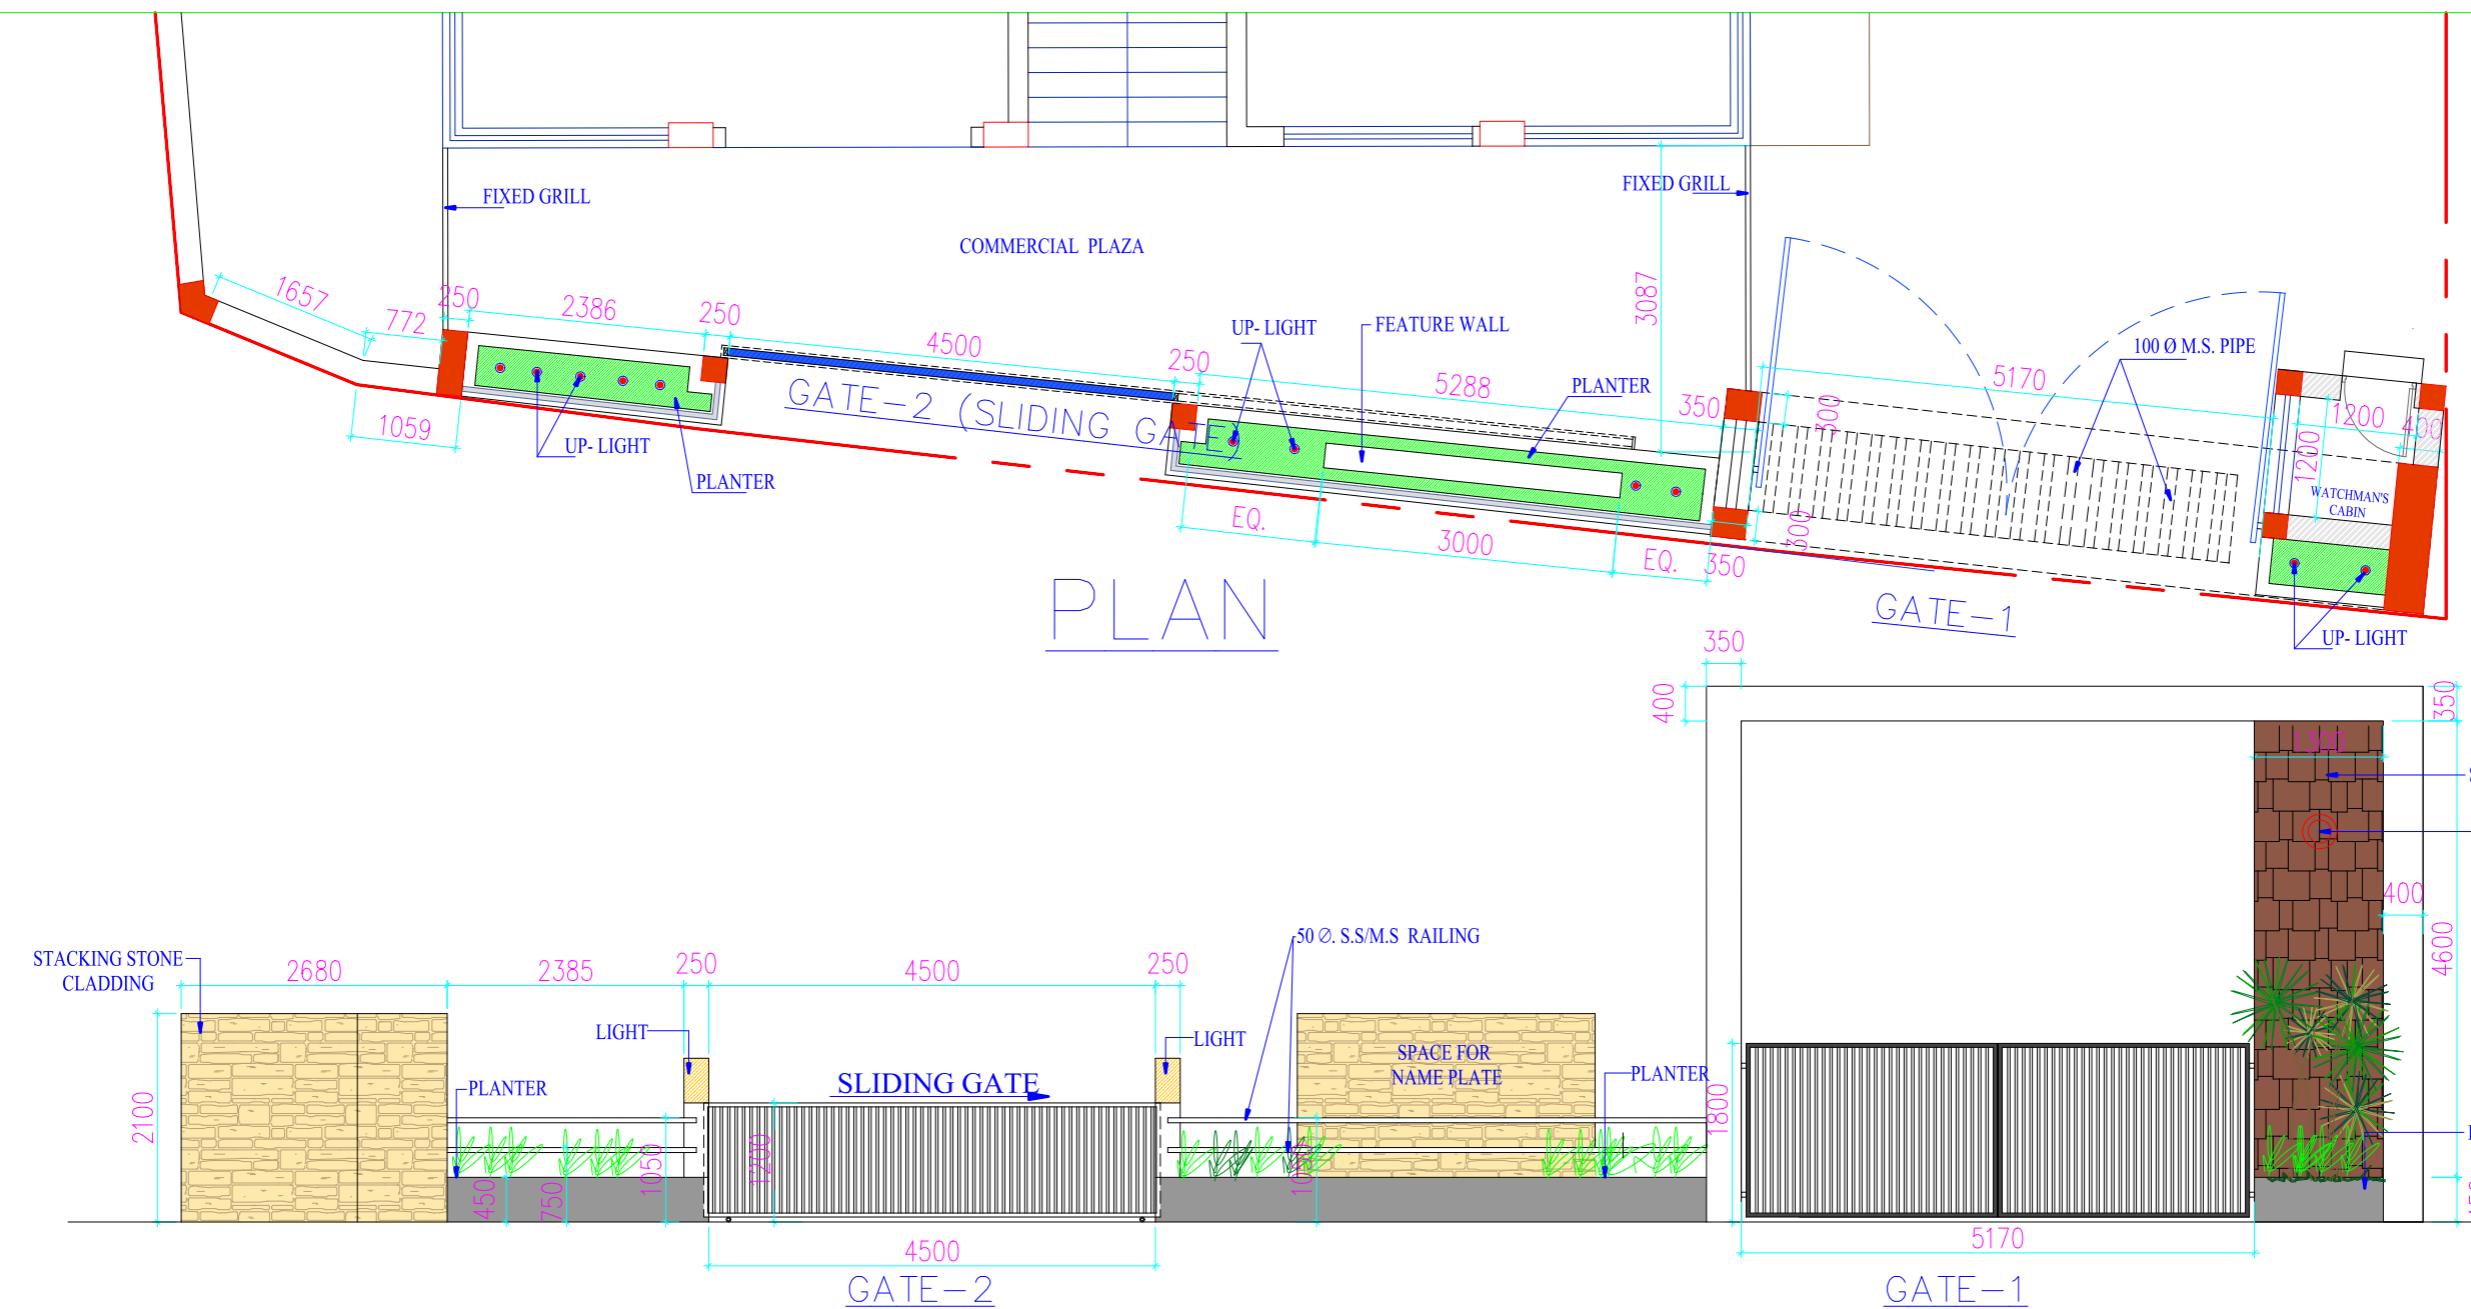


TITLE	
GATE DETAIL (PLAN , ELEVATION)	
PROJECT	
SCALE 1:100	ARCHITECTS
	RAJ AGRAWAL & ASSOCIATES.
	8B, ROYD STREET, KOLKATA - 16.
DATE 24.10.2017	DRG. NO. JOB NO. REV NO. REV DATE DEALT SIMPLY SHEULI

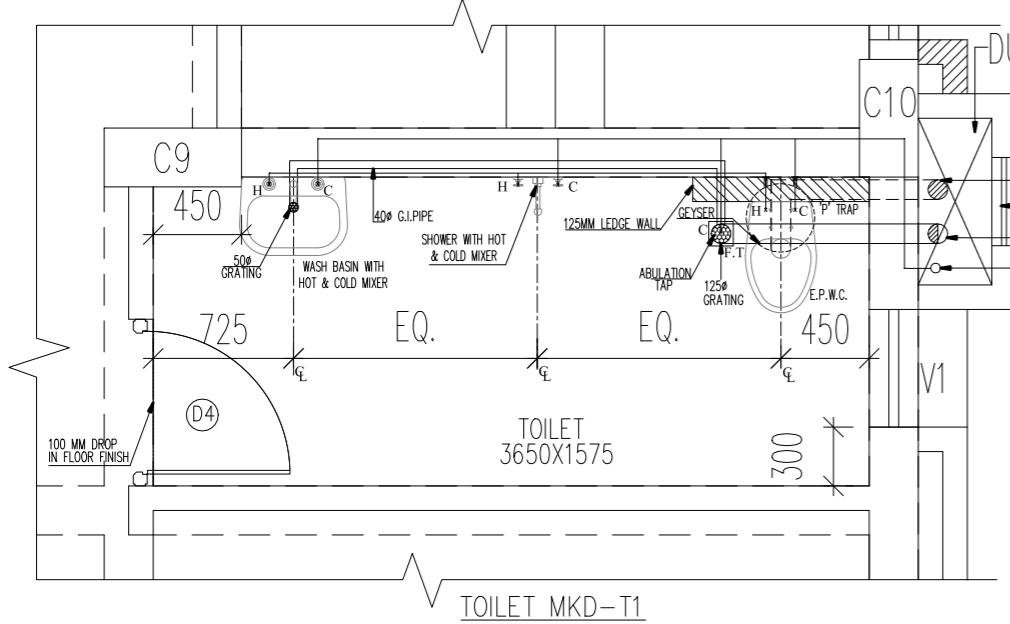


TOILET MKD-T1
3650X1575
(AT 3RD FLOOR)

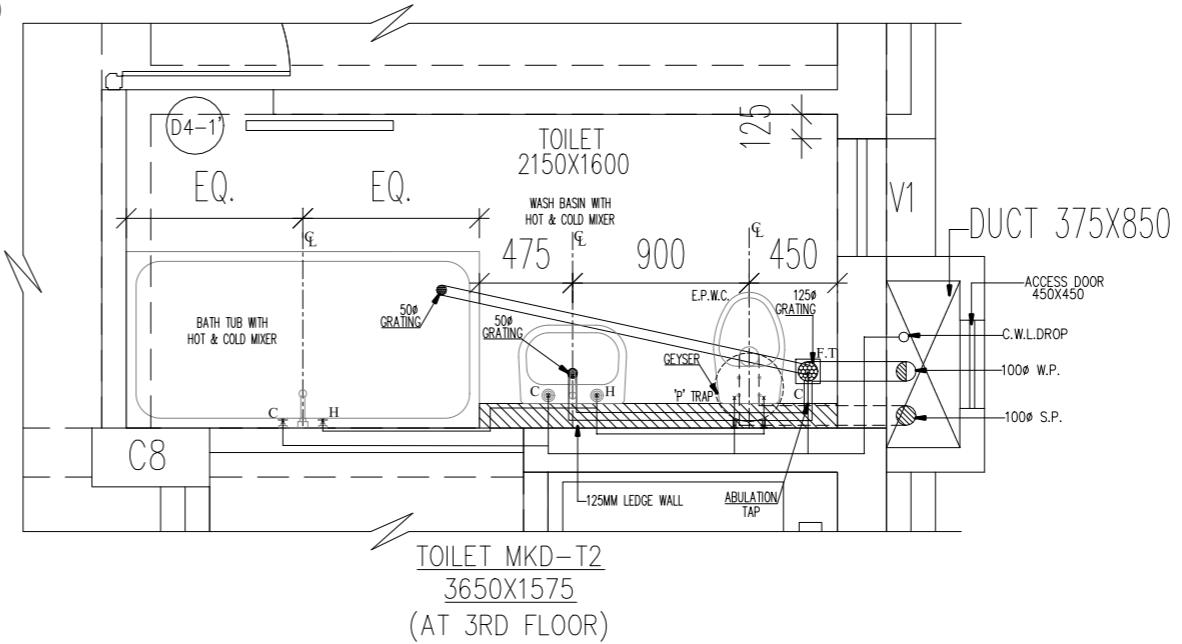

TOILET MKD-T2
3650X1575
(AT 3RD FLOOR)

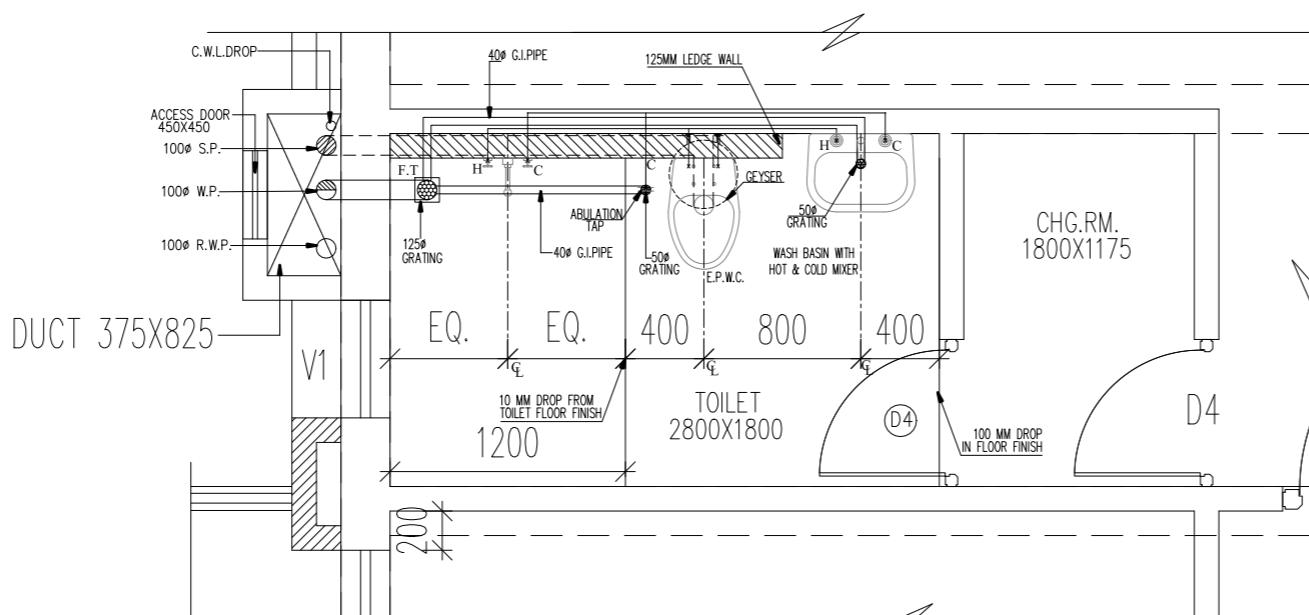

TOILET MKD-T3
3650X1575
(AT 3RD FLOOR)

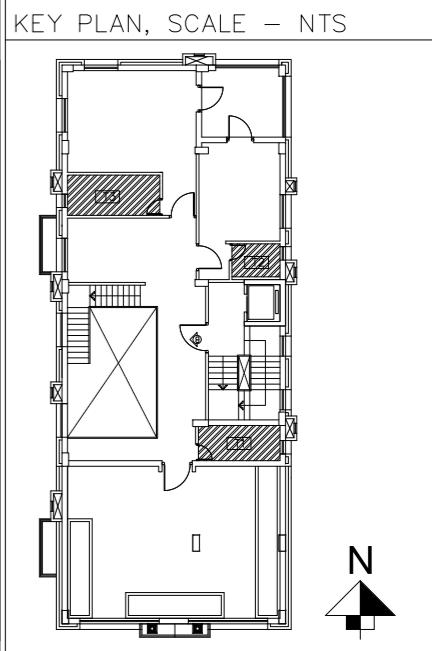

GENERAL NOTES:-

- WRITTEN MEASUREMENTS SHOULD BE FOLLOWED ALWAYS, DRAWING SHOULD NOT BE SCALED.
- IN CASE OF ANY DISCREPANCY NOTICED IN THE DRAWINGS, IMMEDIATELY INFORM THE ARCHITECTS, BEFORE PROCEEDING WITH ANY WORK ON THAT PART.
- REFER ONLY THE LATEST REVISED DRAWINGS;
SUPERSEDED DRAWINGS NOT TO BE KEPT IN USE AT SITE.
- ALL DIMENSIONS ARE FINISHED DIMENSIONS (INCLUDING CLADDING)
- PIPE FROM CYLINDER CAN BE TAKEN ALTERNATIVELY THROUGH WALL.
- WASHING MACHINE POSITION IS ALREADY SHOWN IN FLOOR PLAN.

SANITARY PIPE LEGEND	
1. 100Ø SOIL PIPE	●
2. 100Ø WASTE PIPE	○
3. 100Ø RAIN WATER PIPE	○
4. 150Ø RAIN WATER PIPE	○
5. COLD LINE WATER DROP	○

SANITARY FIXTURE LEGEND		HT. OF FIX. FROM FLOOR
E.P.W.C.	EUROPEAN WALL MOUNTED	450 mm
W.H.B.	WASH HAND BASIN	800 mm
A.T.	ABLUTION TAP	450 mm
A.T.	SHOWER MIXTURE	800 mm
	SHOWER ROSE	1950 mm
F.T.	GEYSER	
	FLOOR TRAP	

SANITARY CONSULTANT


1.	19.02.13	SONALI	WASH AREA DETAIL	SRABANTI
NO.	DATE	DEALT	PARTICULARS	CHECKED

REVISION

TITLE
DETAIL OF 3RD FLOOR TOILET KITCHEN DETAIL


PROJECT
PROPOSED G+IV STORED BUILDING AT SOUTH DUMDUM

SCALE 1:25	ARCHITECTS
	RAJ AGRAWAL & ASSOCIATES, 8B, ROYD STREET, KOLKATA-16.
DATE 31.10.17	DRG.NO JOB NO. REV.NO. REV.DATE DEALT SIMPLY SHEU

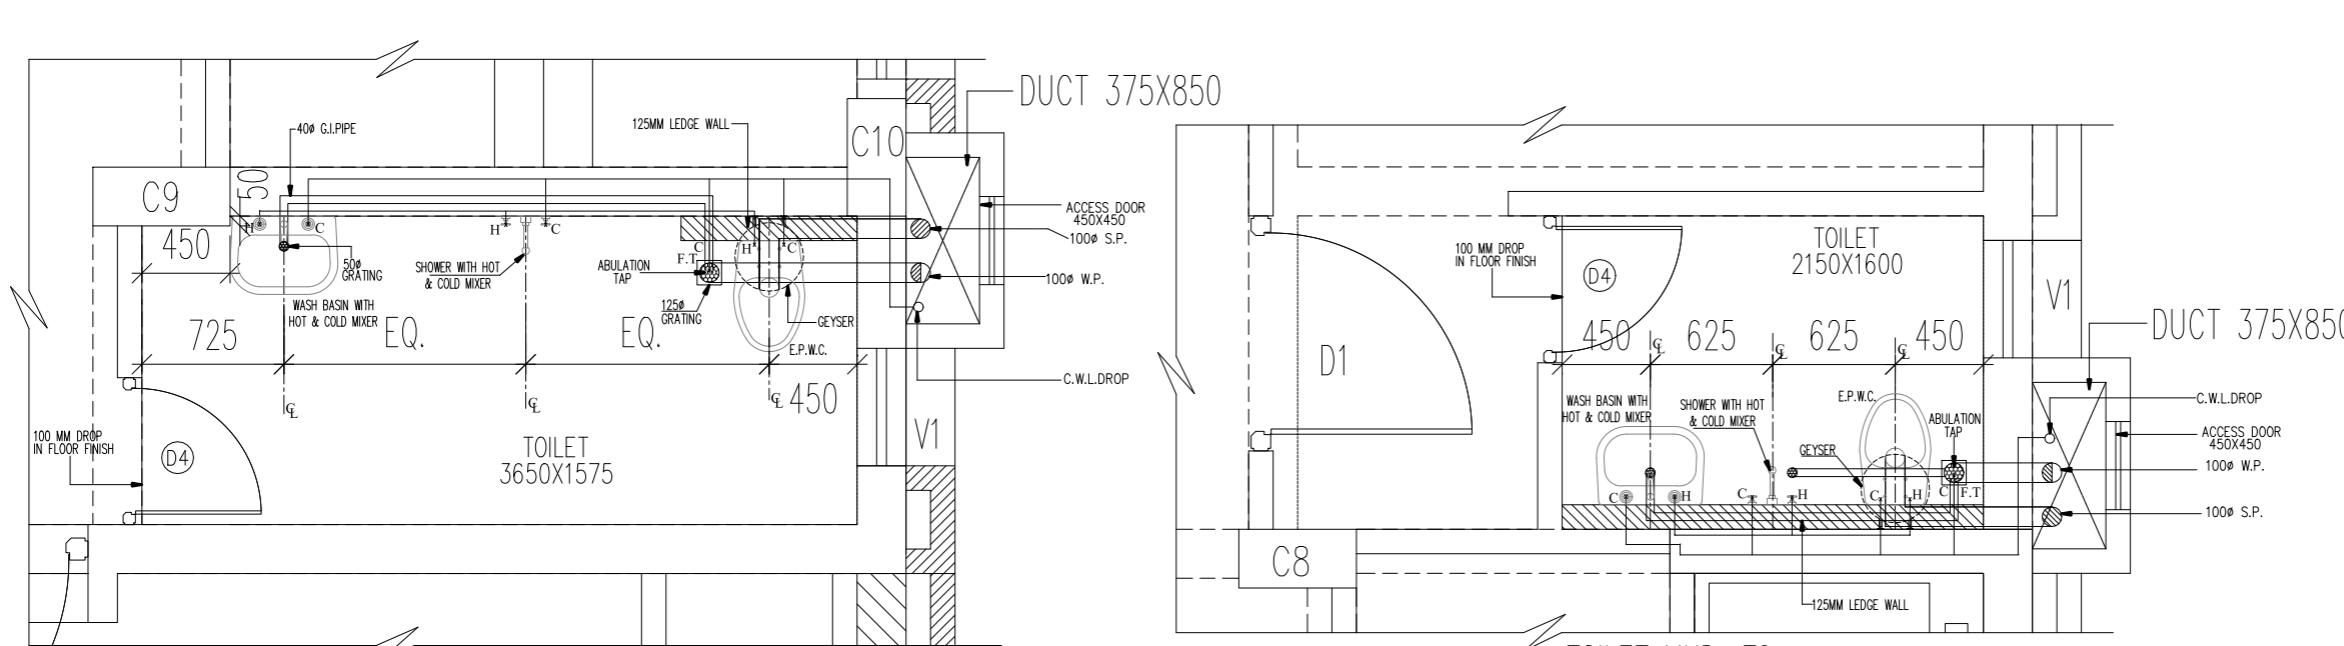


TOILET MKD. T1
3650x1575
AT 4TH FLOOR

TOILET MKD. T2
2150x1600
AT 4TH FLOOR

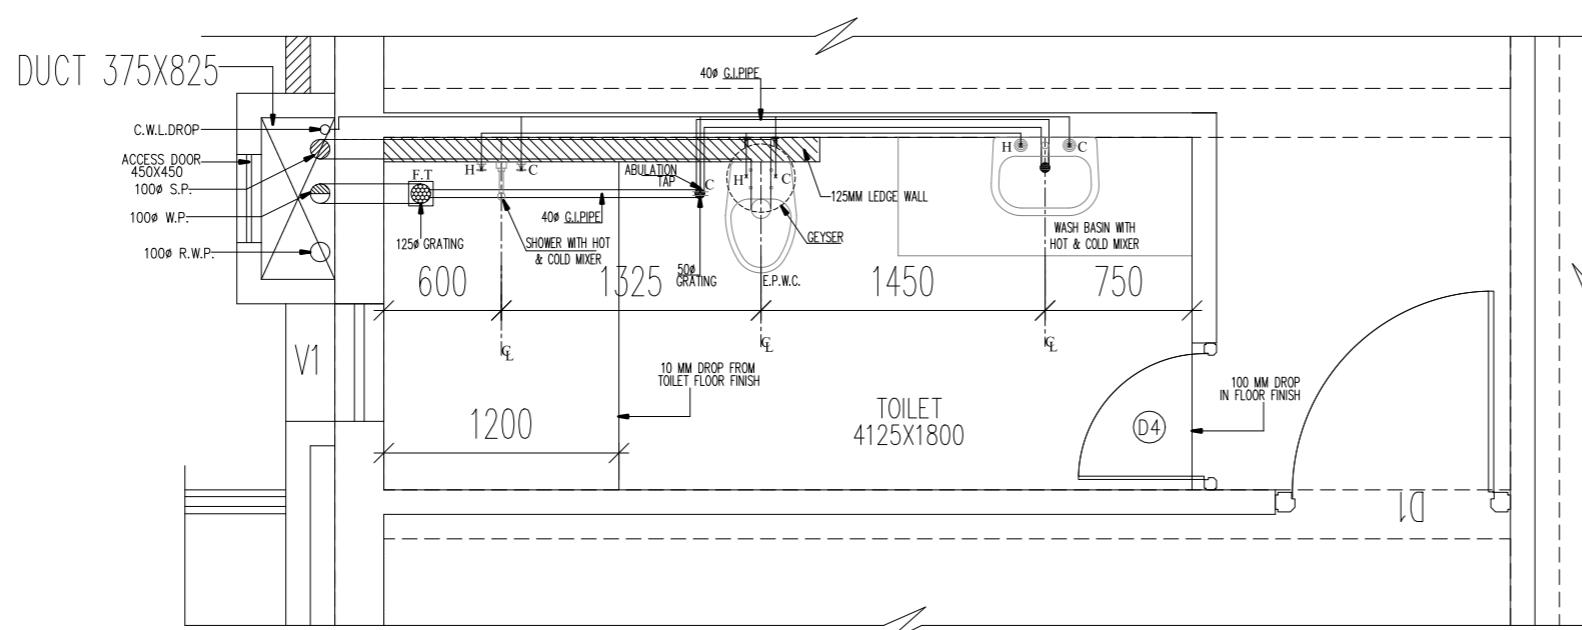

TOILET MKD. T3
4125x1800
AT 4TH FLOOR

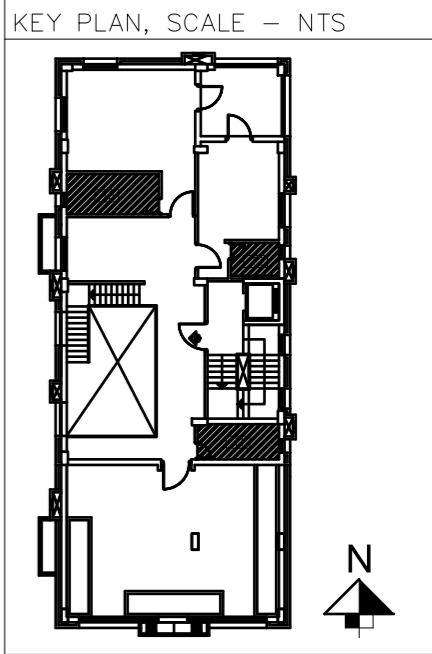

GENERAL NOTES: –

1. WRITTEN MEASUREMENTS SHOULD BE FOLLOWED ALWAYS, DRAWING SHOULD NOT BE SCALED.
2. IN CASE OF ANY DISCREPANCY NOTICED IN THE DRAWINGS, IMMEDIATELY INFORM THE ARCHITECTS, BEFORE PROCEEDING WITH ANY WORK ON THAT PART.
3. REFER ONLY THE LATEST REVISED DRAWINGS;
SUPERSEDED DRAWINGS NOT TO BE KEPT IN USE AT SITE.
4. ALL DIMENSIONS ARE FINISHED DIMENSIONS (INCLUDING CLADDING)
5. PIPE FROM CYLINDER CAN BE TAKEN ALTERNATIVELY THROUGH WALL.
6. WASHING MACHINE POSITION IS ALREADY SHOWN IN FLOOR PLAN.

SANITARY PIPE LEGEND	
1. 100Φ SOIL PIPE	●
2. 100Φ WASTE PIPE	○
3. 100Φ RAIN WATER PIPE	○
4. 150Φ RAIN WATER PIPE	○
5. COLD LINE WATER DROP	○

SANITARY FIXTURE LEGEND	
E.P.W.C.	EUROPEAN WALL MOUNTED
W.H.B.	WASH HAND BASIN
A.T.	ABLUTION TAP
SHOWER MIXTURE	450 mm
SHOWER ROSE	800 mm
GEYSER	
F.T.	FLOOR TRAP

SANITARY CONSULTANT


HIMADRI CHOWDHURI			
1. 19.02.13	SONALI	WASH AREA DETAIL	SRABANTI
NO.	DATE	DEALT	PARTICULARS


REVISION

TITLE
DETAIL OF 4TH FLOOR TOILET KITCHEN DETAIL


PROJECT
PROPOSED G+IV STORED BUILDING AT SOUTH DUMDUM

SCALE 1:25	ARCHITECTS
	RAJ AGRAWAL & ASSOCIATES. 8B, ROYD STREET, KOLKATA-16.
DATE 09.11.17	DRG.NO JOB NO. REV.NO. REV.DATE DEALT SIMPLY SHEU

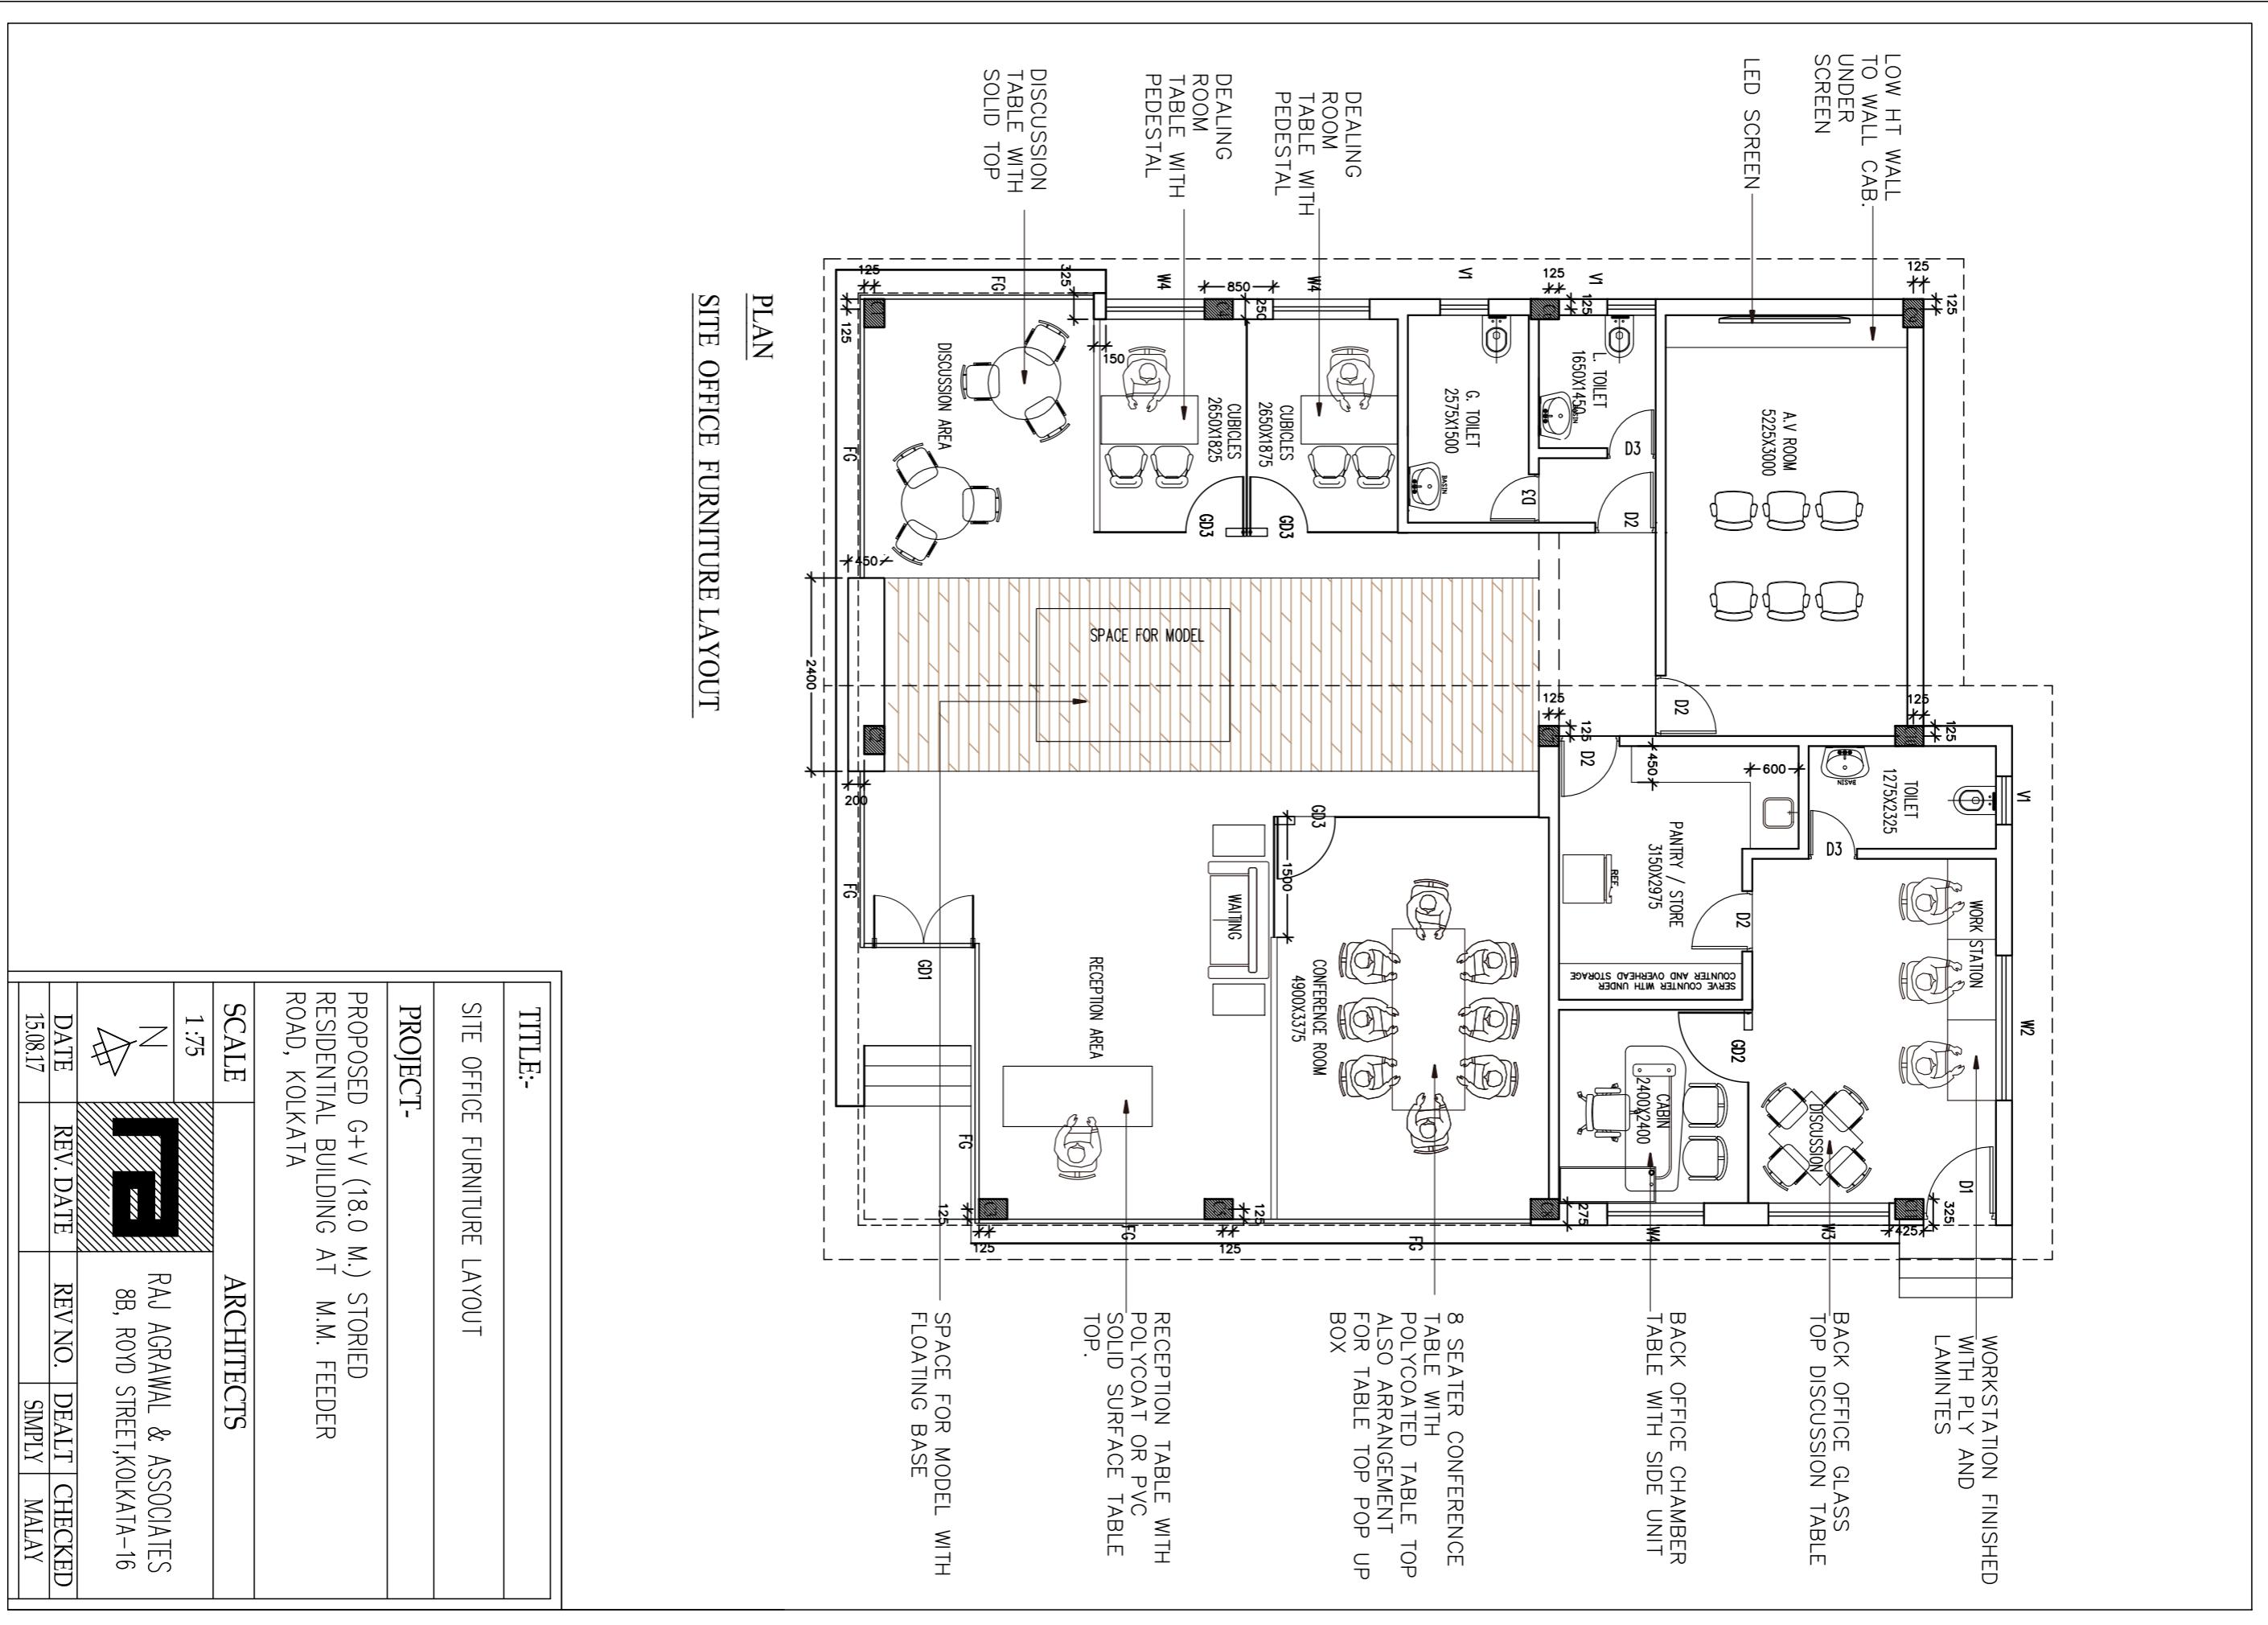

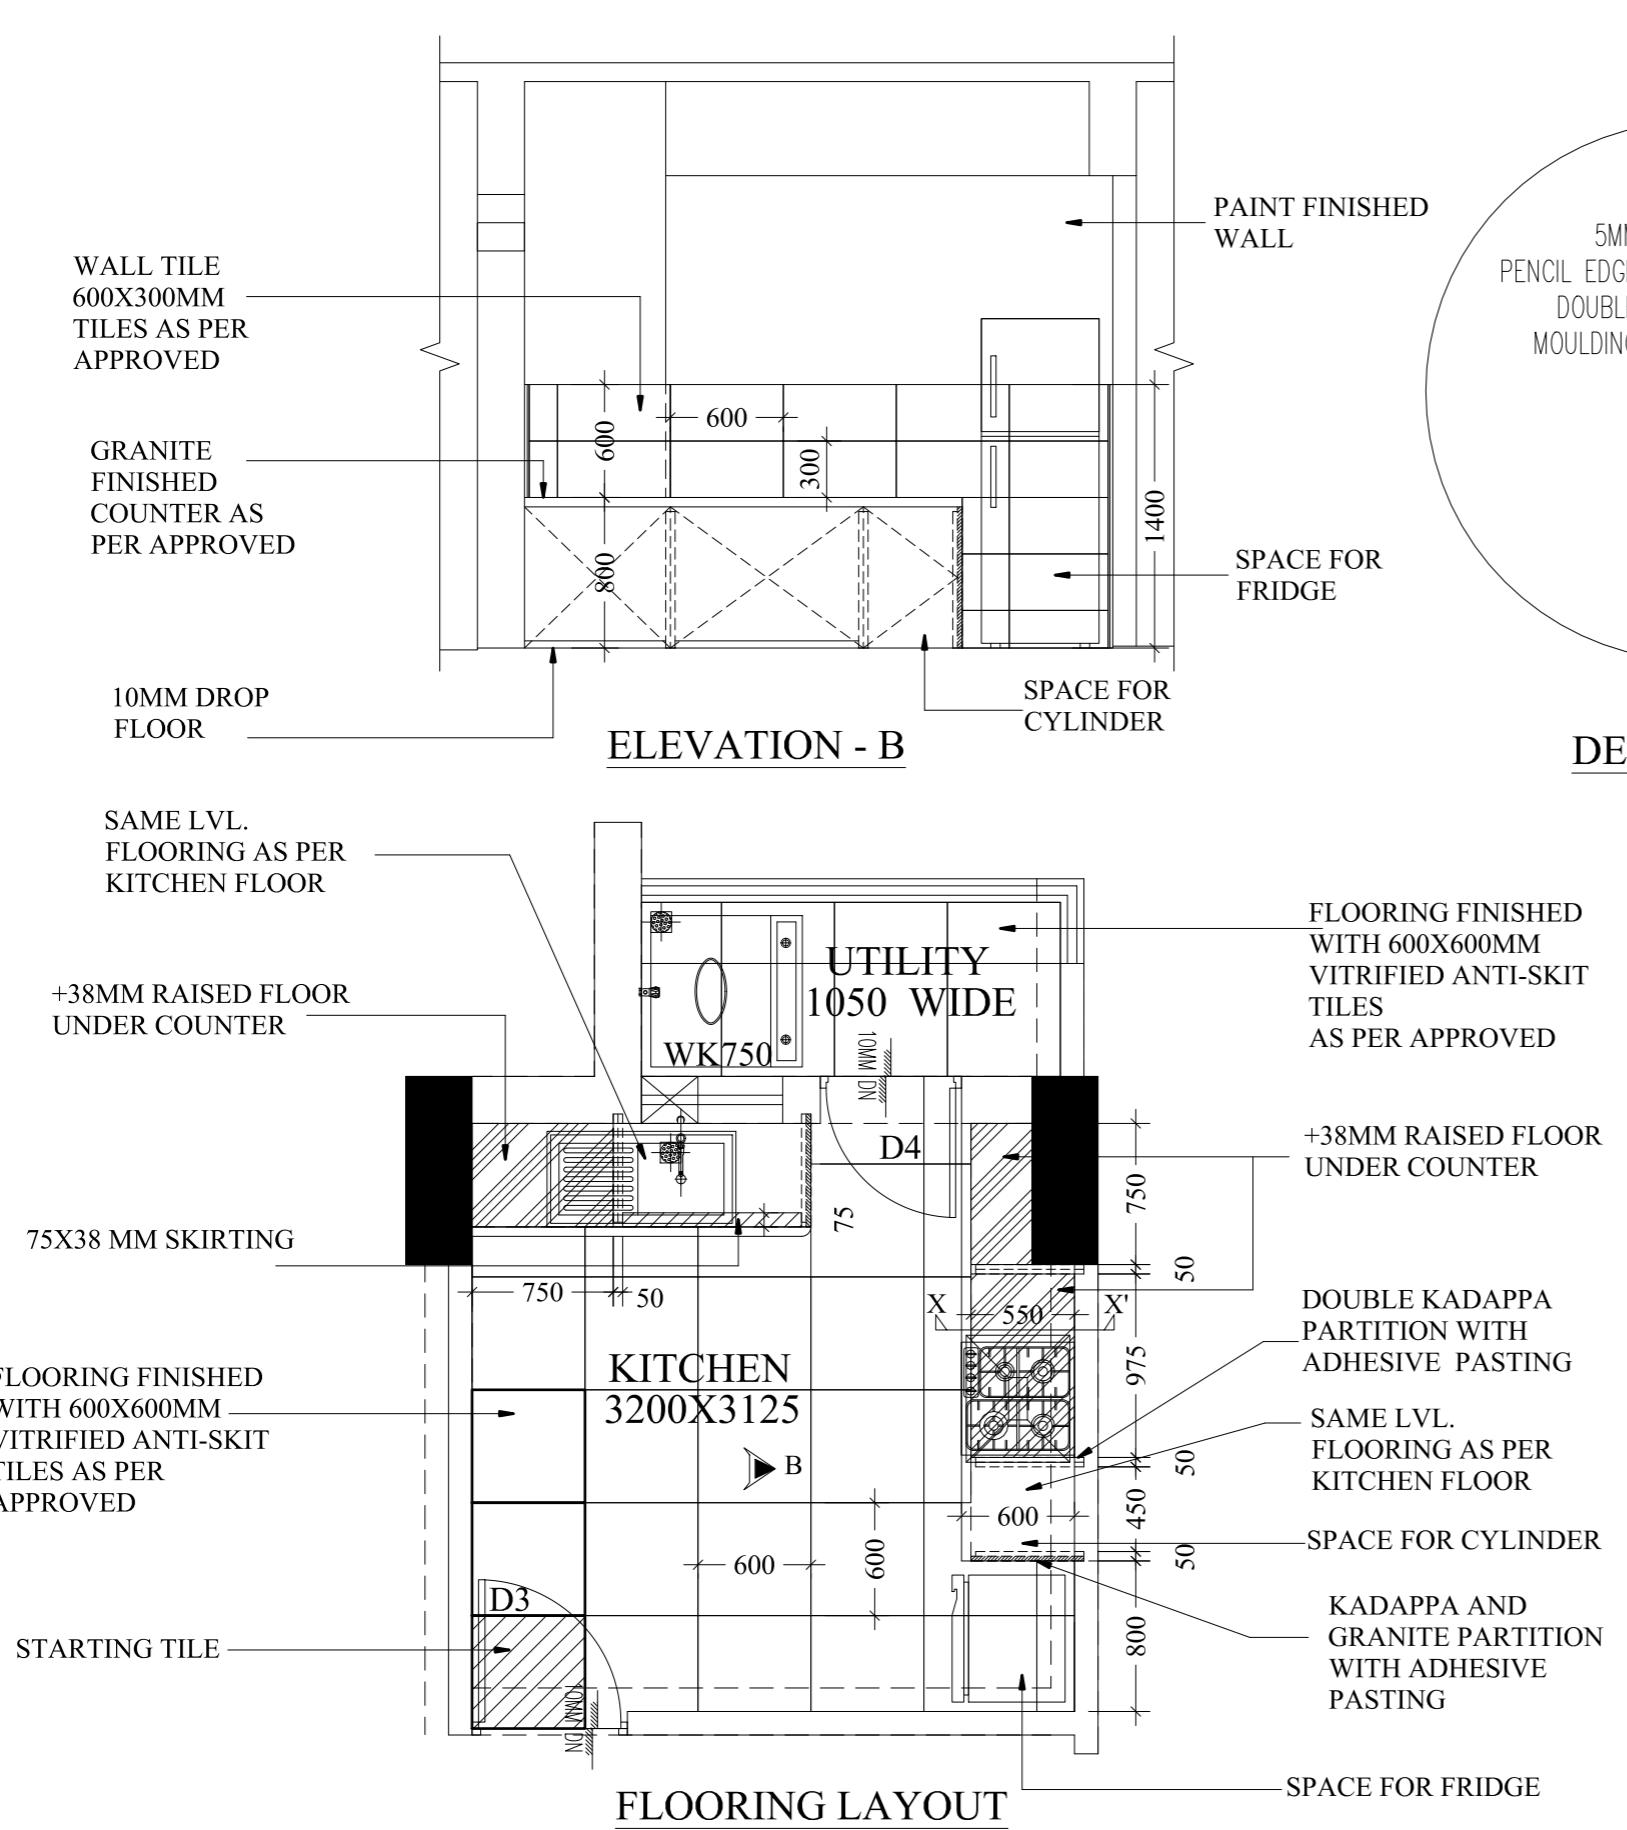









DETAIL AT "X"

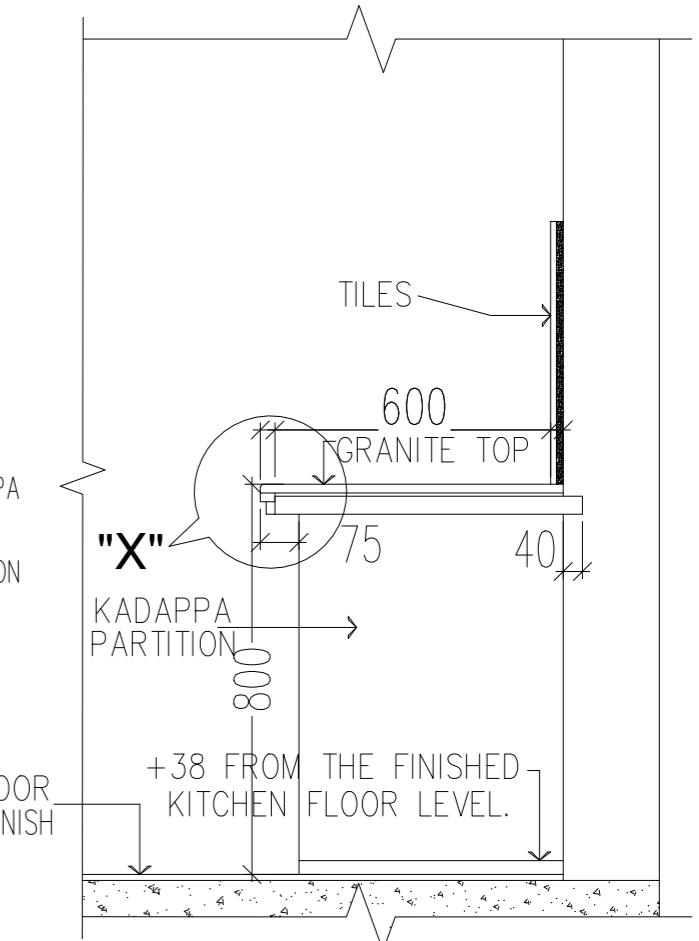



SECTION-XX'

FOR APPROVAL

TITLE		(BLOCK - 1 & 2)		
5TH FLOOR FLAT-C KITCHEN DADO DETAIL				
PROJECT				
LAXMI - AQUASCAPE				
SCALE 1:50	ARCHITECTS			
	RAJ AGRAWAL & ASSOCIATES. 8B, ROYD STREET, KOLKATA - 16.			
DATE	REV. NO.	REV.DATE	DEALT	CHKD.
17.07.2017			SIMPLY	MALAY

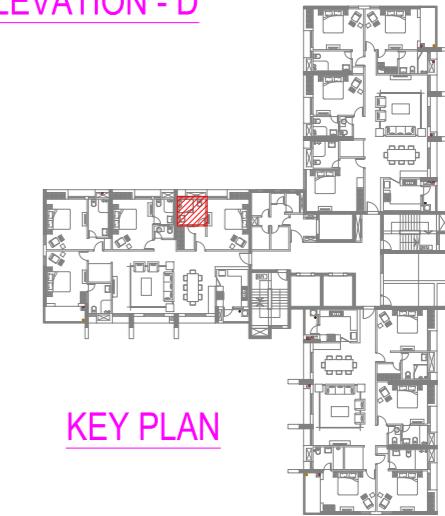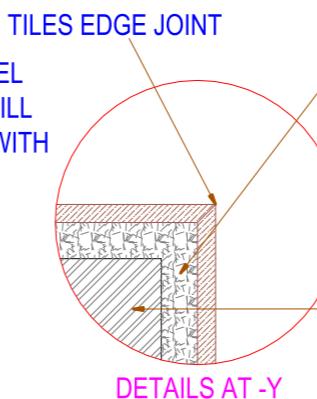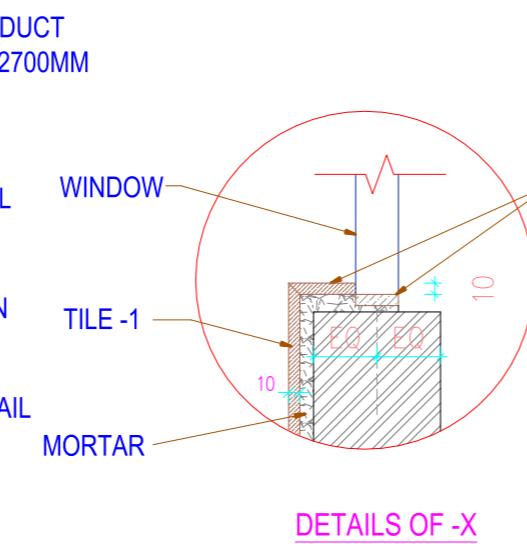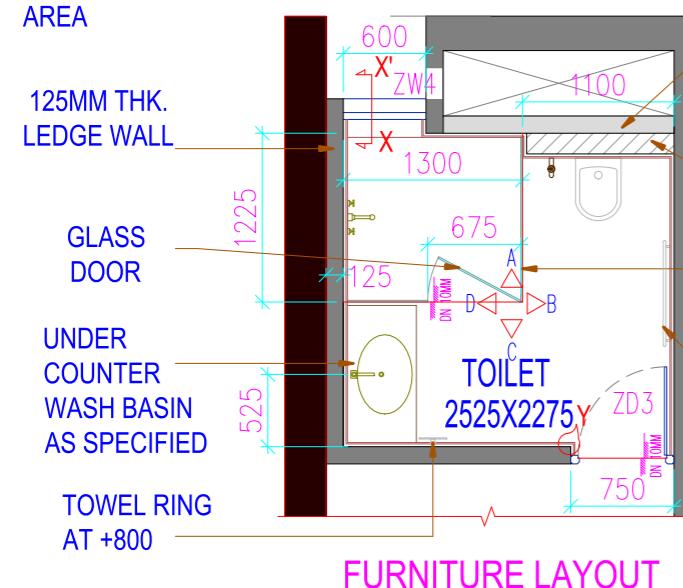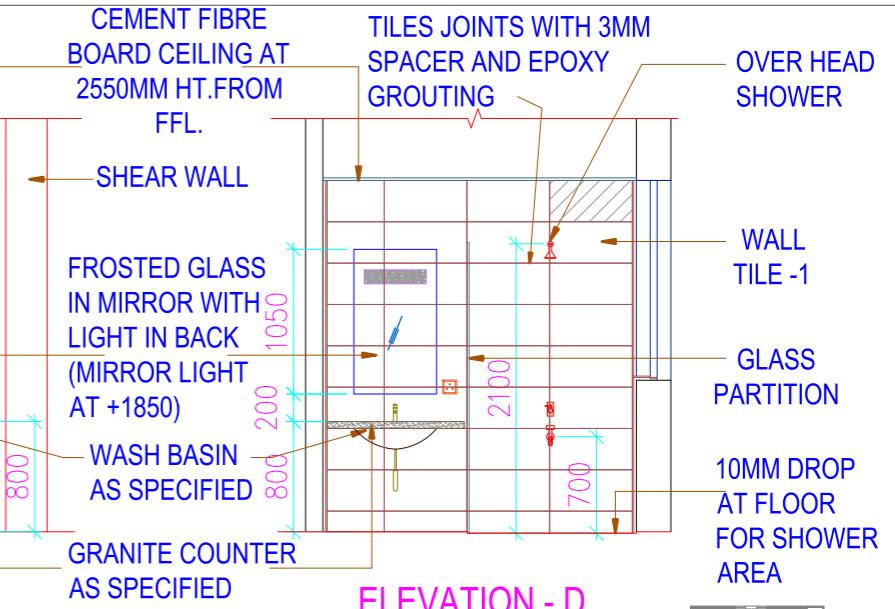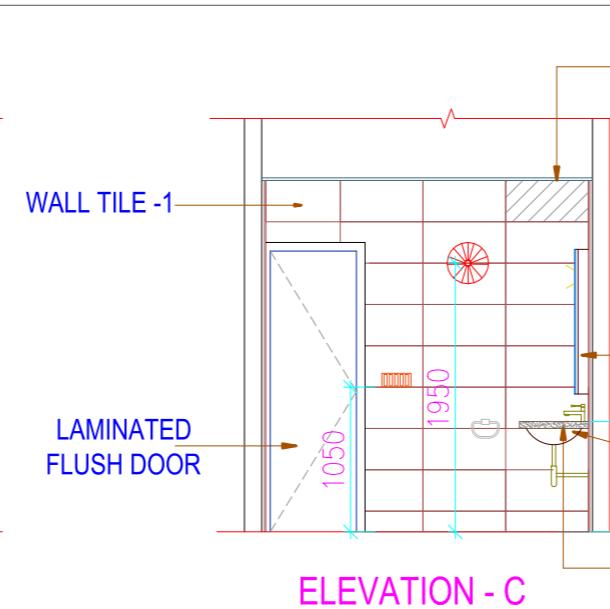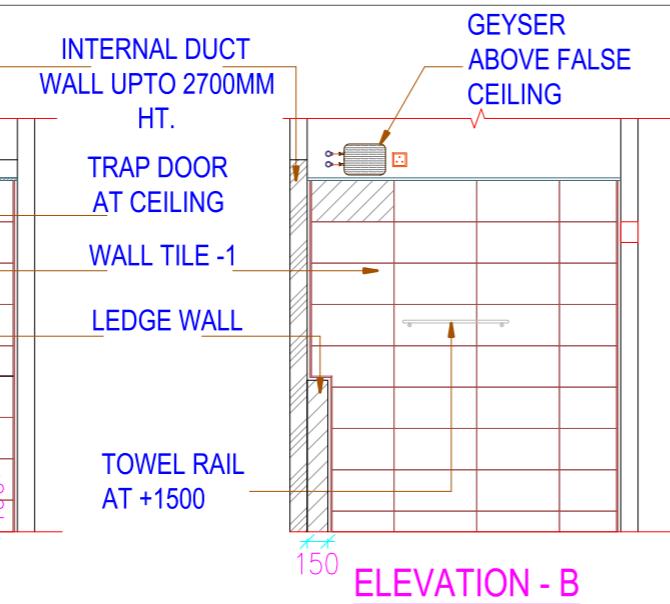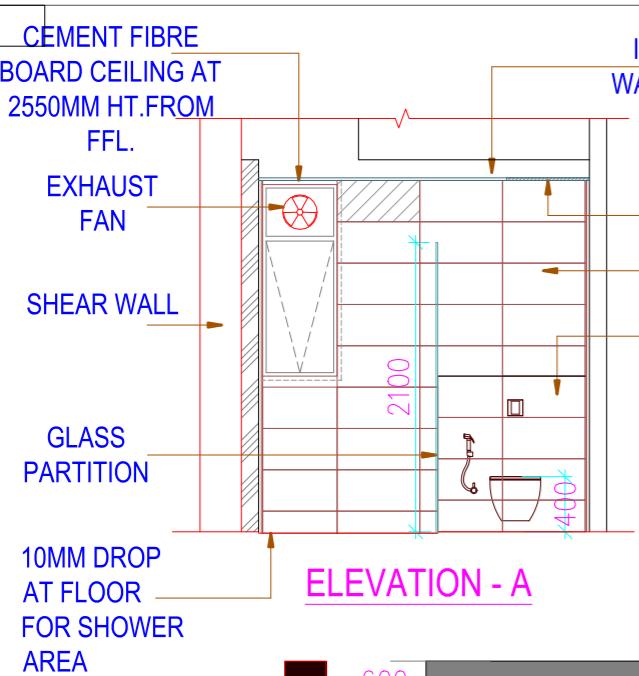

WALL TILE-1: TURKISH BEIGE (300X600)
FLOOR TILE BLACK GRANITE-HONED FINISH (600X600)
TITLE TYPICAL FLOOR FLAT-A MASTER TOILET DADO DETAILS LAYOUT
PROJECT
(SWARNAMANI-ZARINA)
SCALE 1: 50
ARCHITECTS RAJ AGRAWAL & ASSOCIATES.
N 8B, ROYD STREET, KOLKATA-16.
DATE DRG.NO. JOB NO. REV.NO. REV.DATE DEALT CHECKED 24.10.17 SIMPLY MALAY

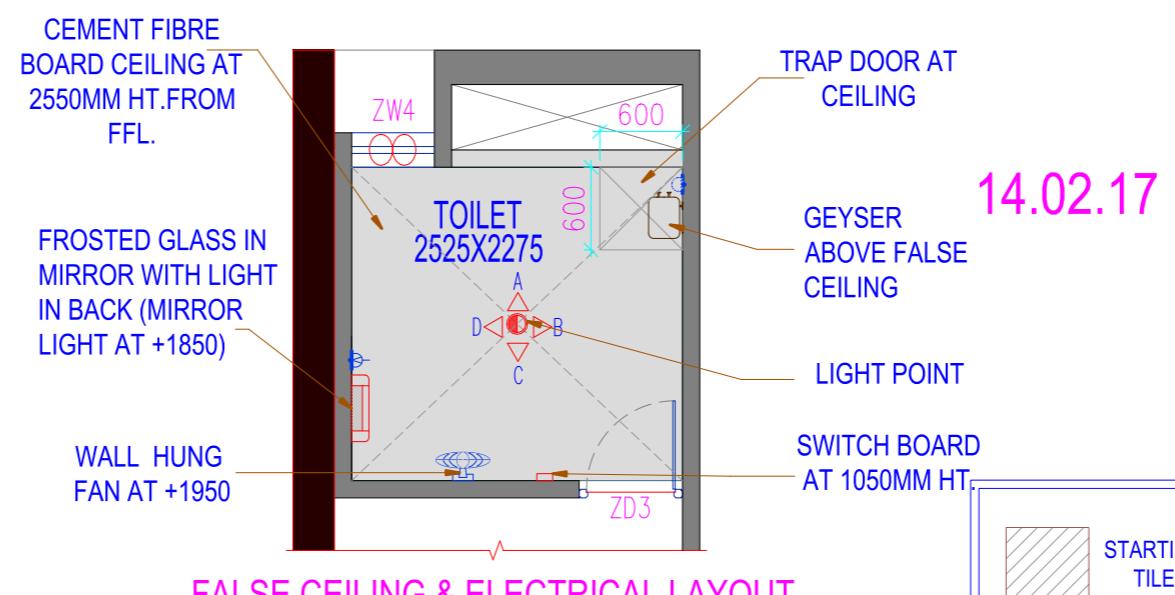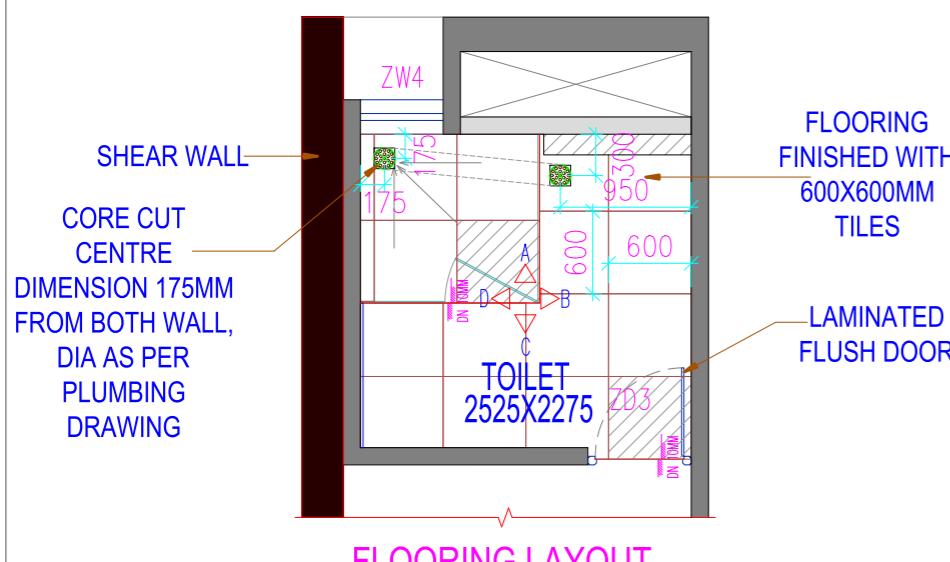

14.02.17